


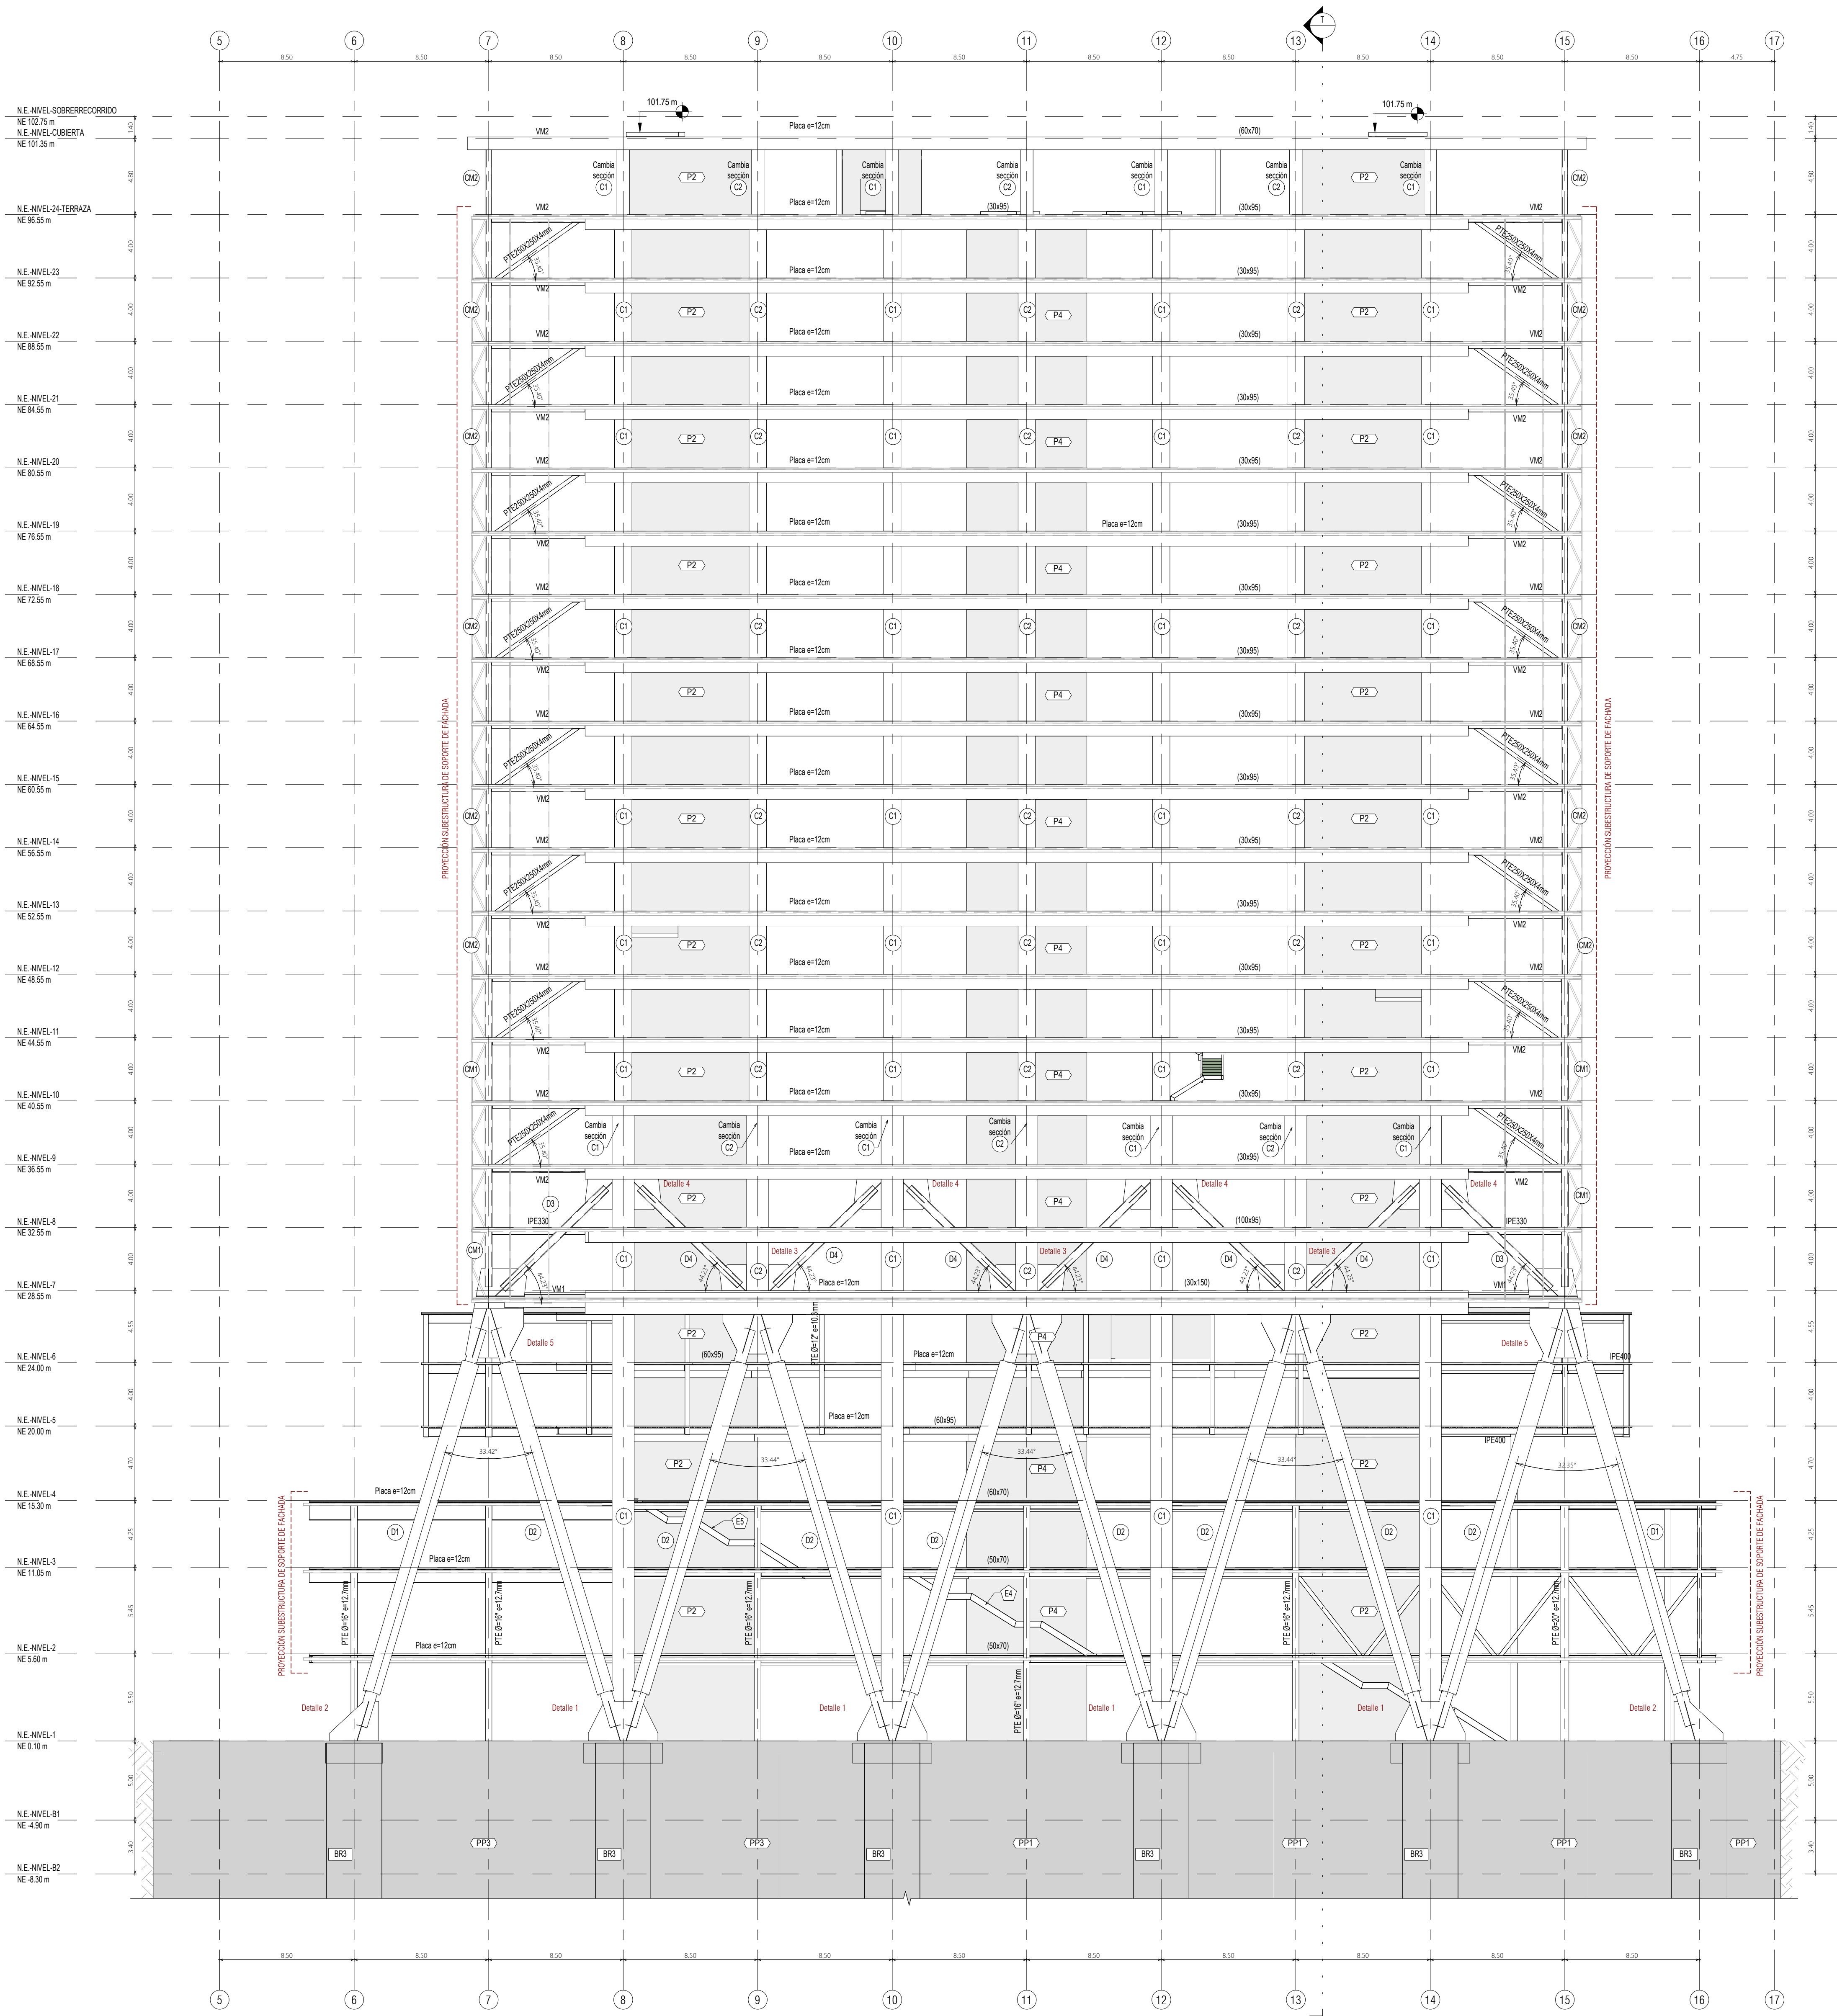

ALZADO SUR
escala 1 : 200

CTIB

Campus de Ciencia, Tecnología e Innovación de Bogotá - Región

corferias

Generadores de Oportunidades y Progreso

Cámara de Comercio de Bogotá

BOGOTÁ

Secretaría Distrital de Desarrollo Económico

ARQUITECTO COORDINADOR

ELEQUIPO MAZZANTI + Gensler

DISEÑO ESTRUCTURAL

CNI

INGENIEROS

Disenador:

ING. NICOLÁS PARRA GARCÍA
MAT. 25202-62063 QND

INTERVENTORÍA

GUTIERREZ DÍAZ S.A.S.

SUPERVISIÓN Y GESTIÓN DE PROYECTOS DE CONSTRUCCIÓN

Director de Interventoría:

Ing. Jorge Iván García Mancilla
Mat. 632021 148063 QND

Versión	Emisión	Descripción
AA	15-06-2023	Ingeniería básica
AB	04-08-2023	Anteproyecto
AC	01-11-2023	Anteproyecto V2 50%
AD	15-12-2023	Anteproyecto V2 100%
DD	13-03-2024	Curaduría V2
EE	10-05-2024	Proyecto final 100%
EF	31-05-2024	Respuestas Obs. 100%
FF	21-06-2024	Entrega final
01	26-07-2024	ENTREGA FINAL

PROYECTO:

CAMPUS DE CIENCIA, TECNOLOGÍA E INNOVACIÓN DE BOGOTÁ
MAT. No. 500-0025470

FASE

ENTREGA FINAL

PROPÓSITO DE EMISIÓN

Curaduría

Revisión

Entrega Cliente

Coordinación

Construcción

ENTREGA FINAL

APTO PARA CONSTRUCCIÓN

KEY PLAN

1A

Fecha:

26-07-2024

Escala:

1 : 200

FACHADA SUR

CTIB_CNI_EST_201_ELE_XXX_01