
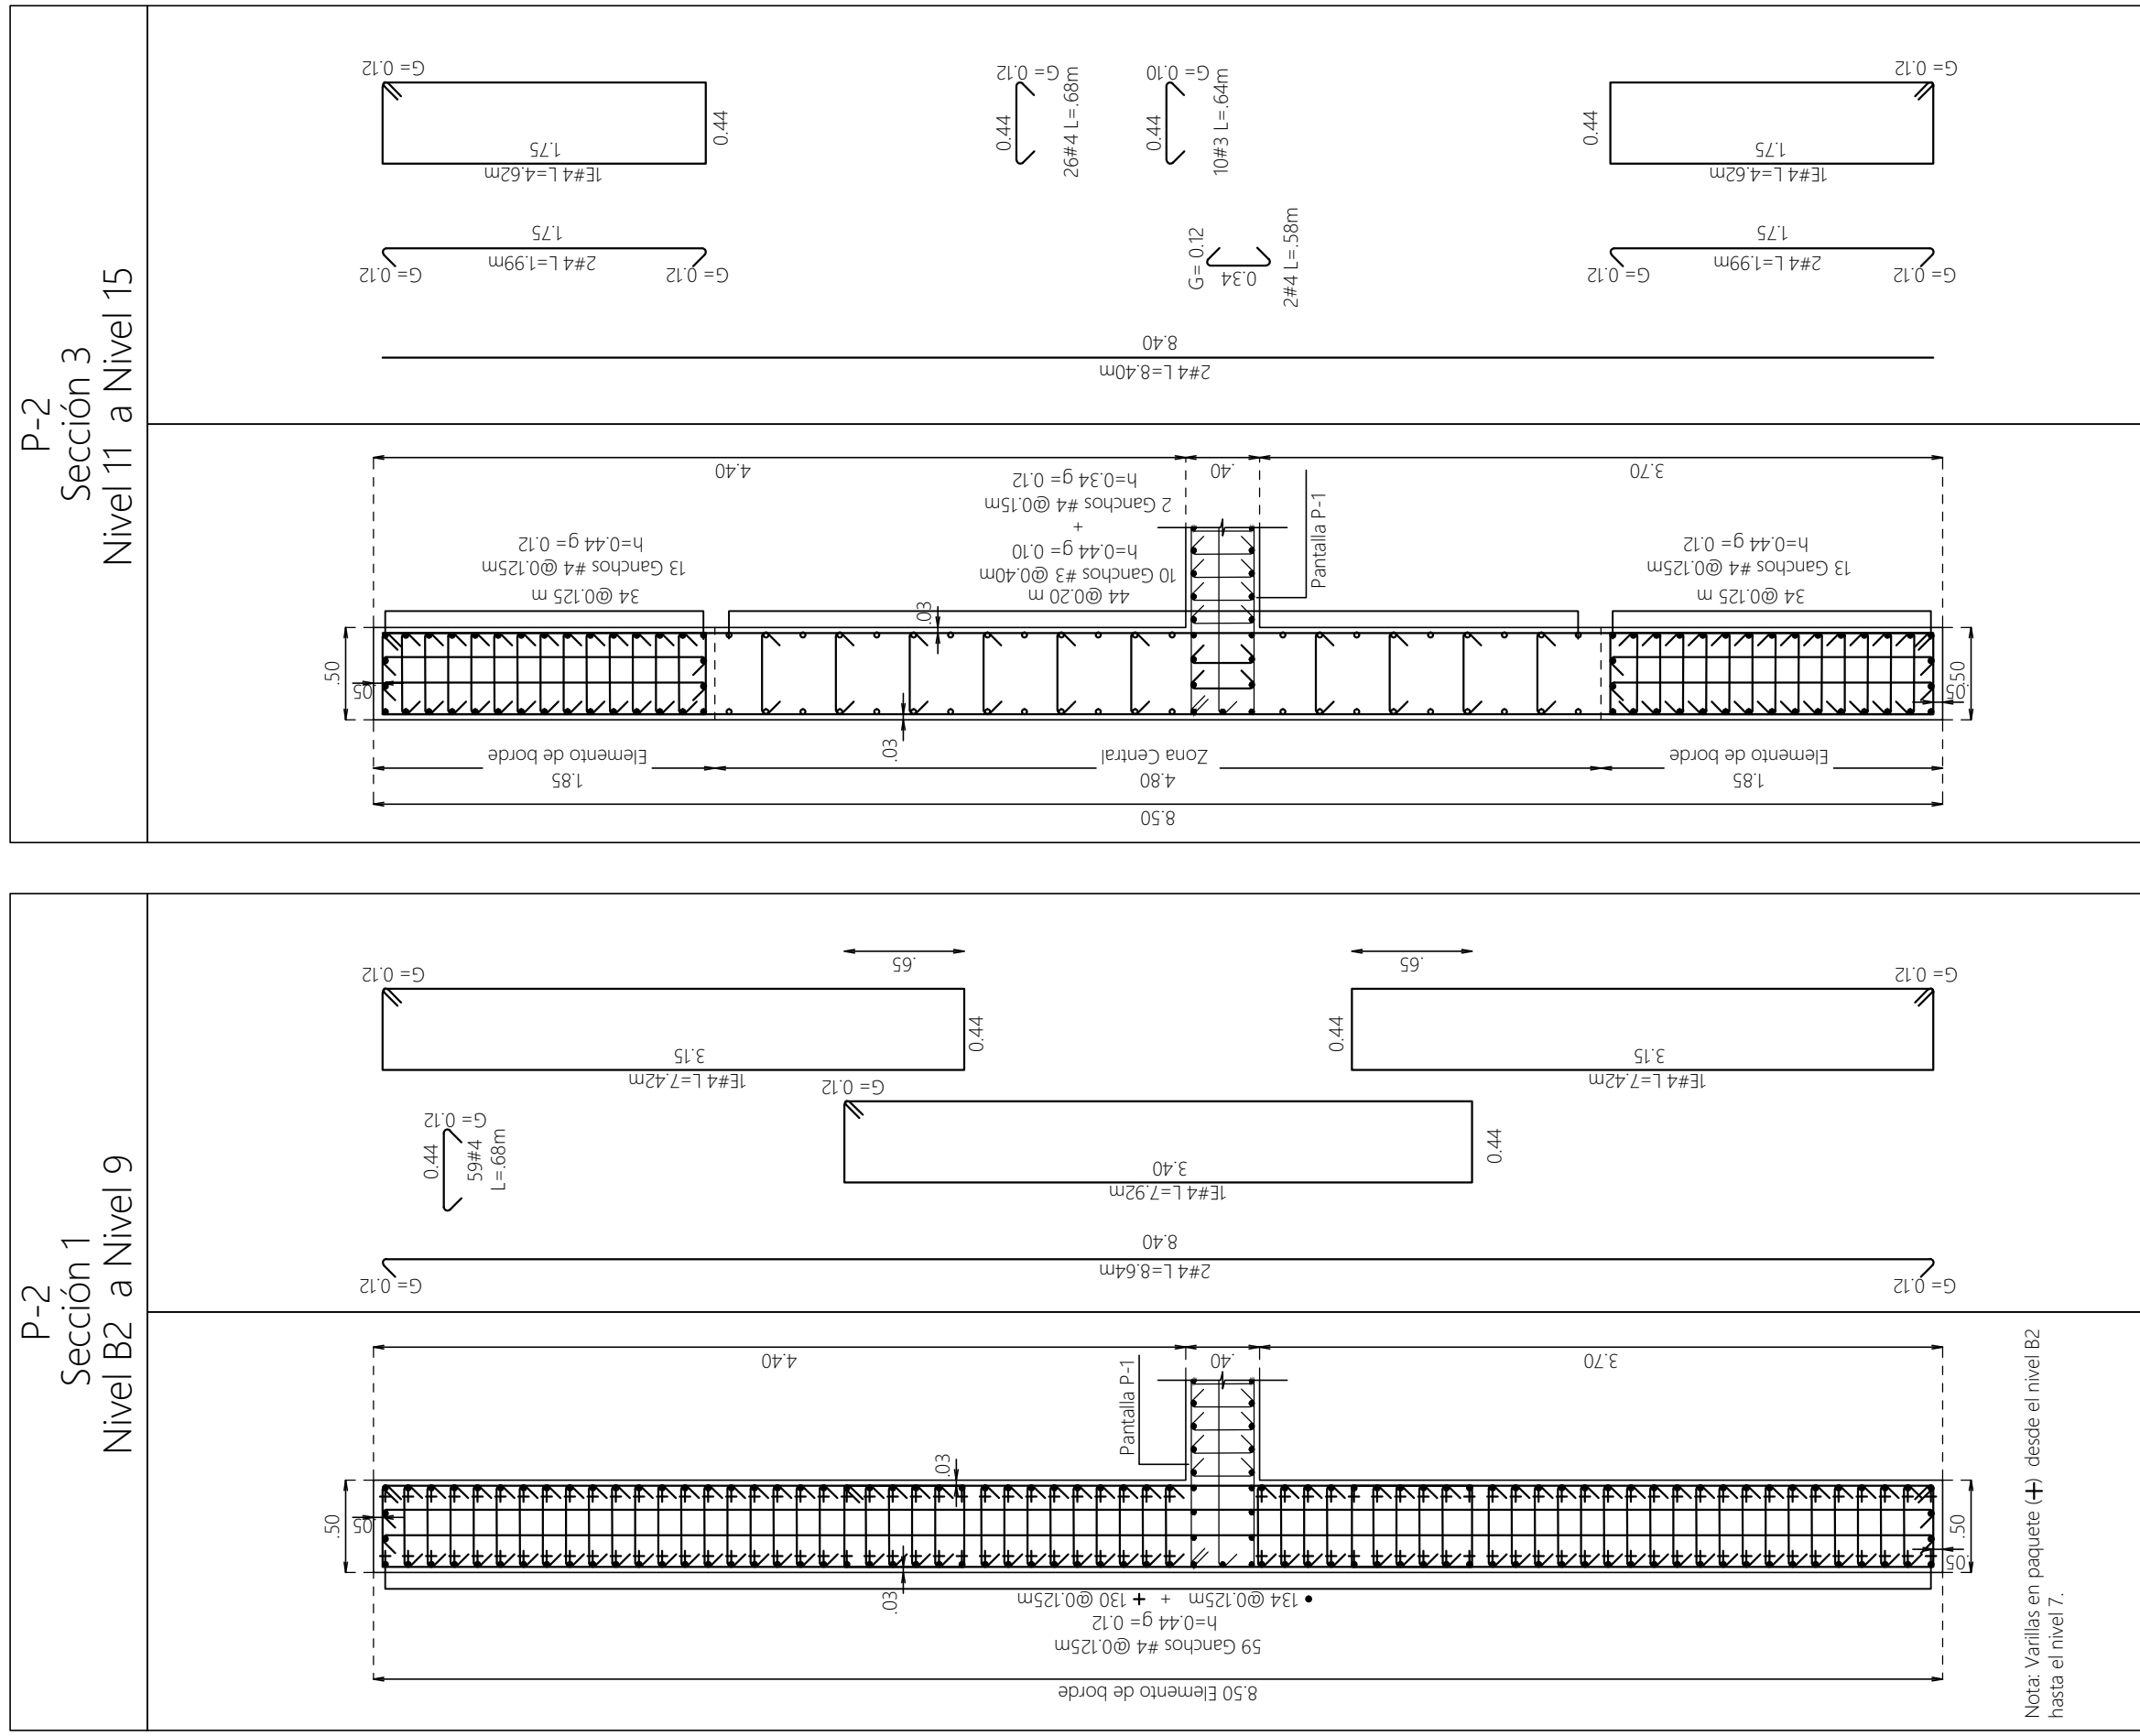
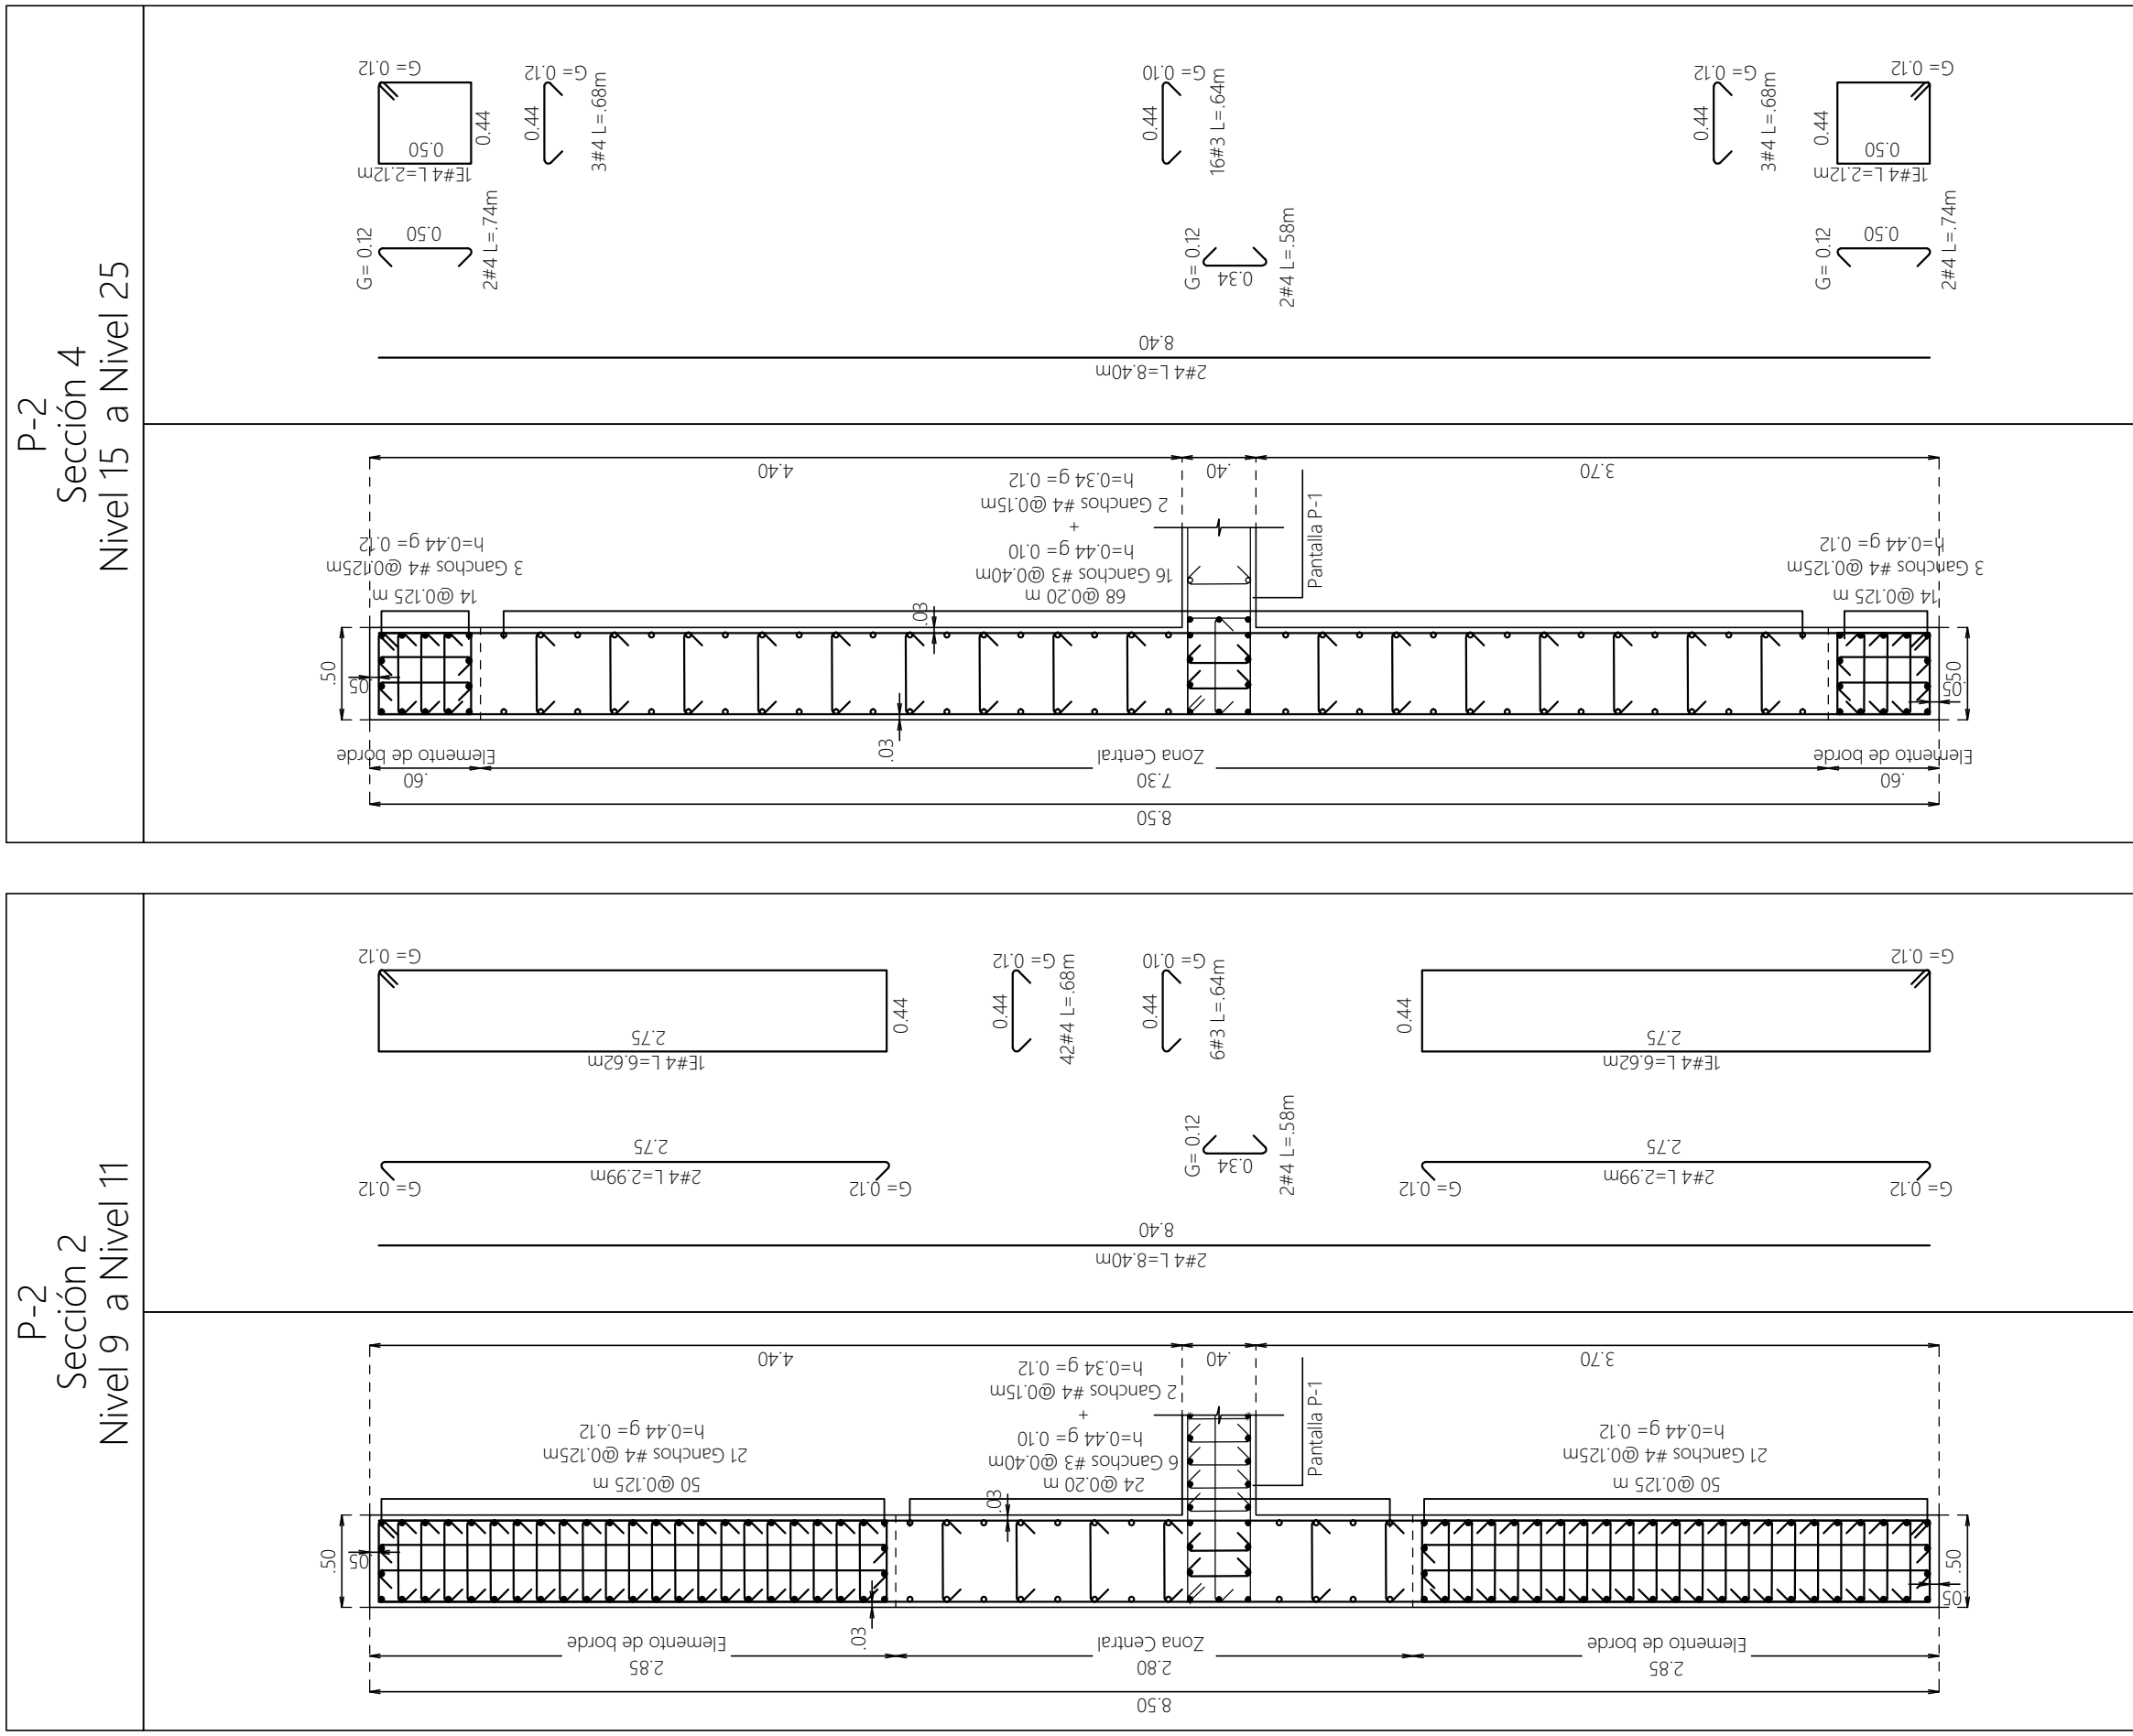
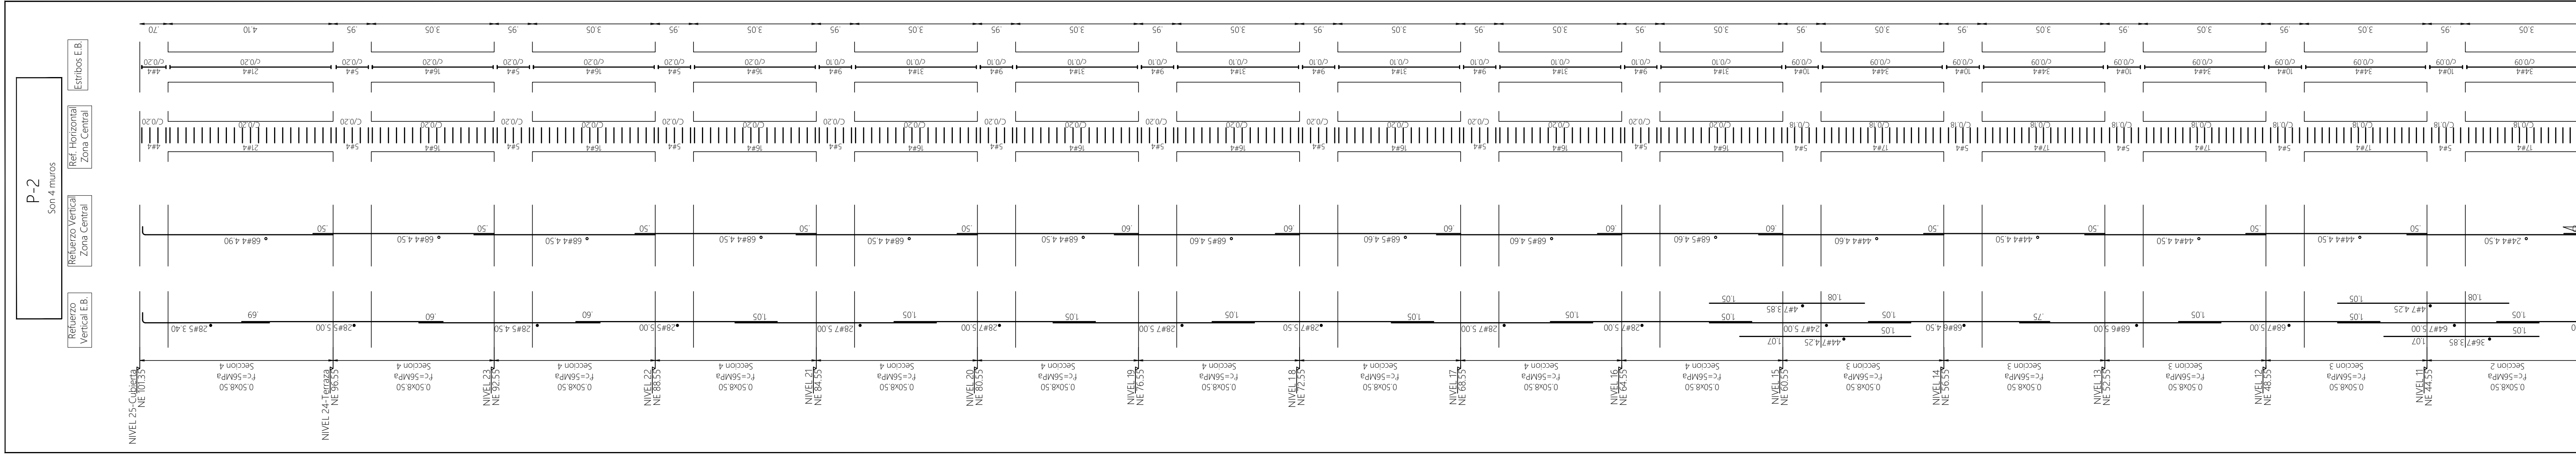


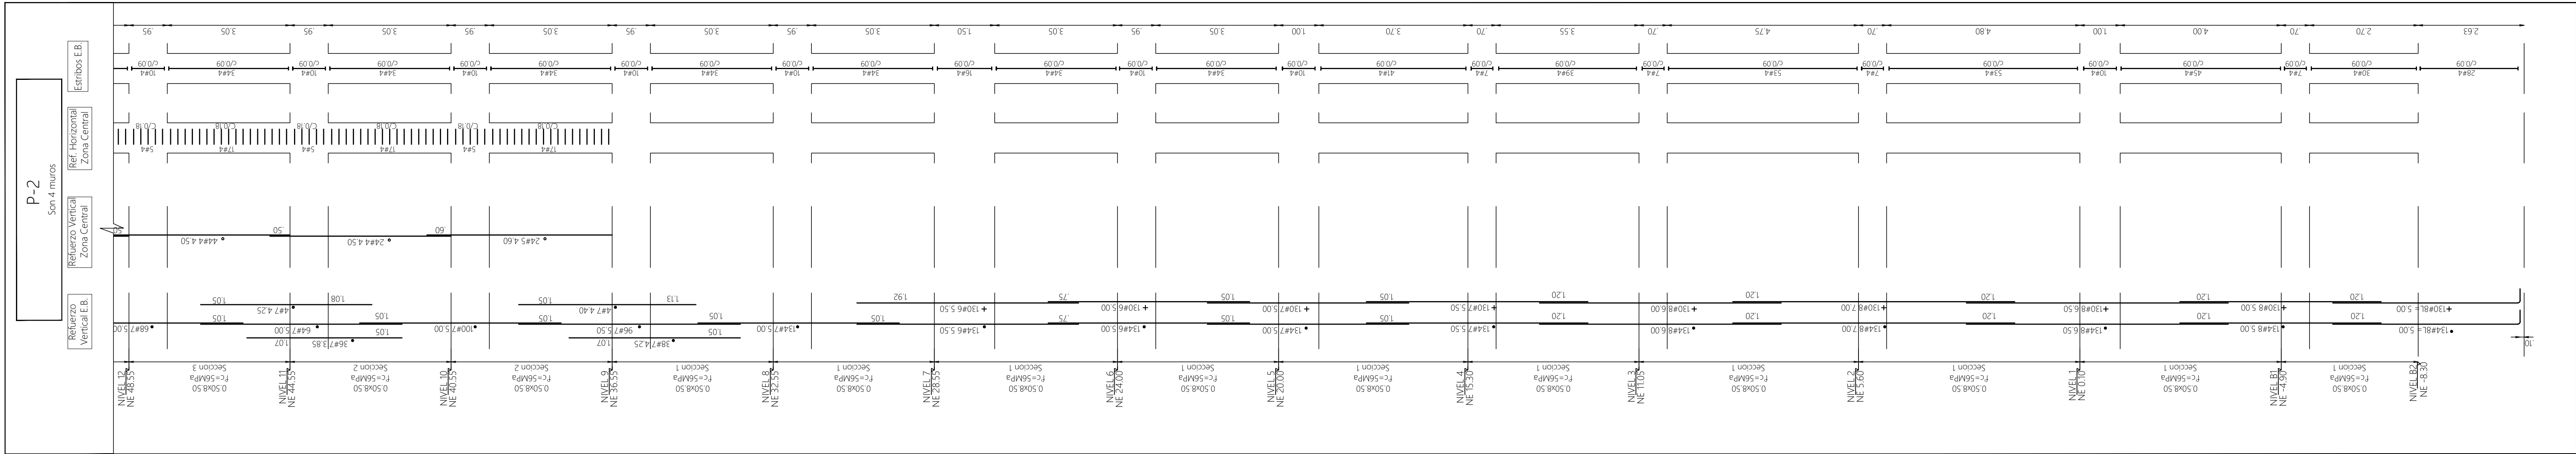

DESPIECE DE PANTALLA P-2
escala 1:75

CTIB

Campus de Ciencia, Tecnología e Innovación de Bogotá - Región

corferias

Generadores de Oportunidades y Progreso

Cámara de Comercio de Bogotá

BOGOTÁ

Secretaría Distrital de Desarrollo Económico

ARQUITECTO COORDINADOR

EL EQUIPO MAZZANTI + Gensler

DISEÑO ESTRUCTURAL

CNI

CONSTRUCCIÓN

ING. NICOLÁS PARRA GARCÍA

MAT. 23021 62063 QND

INTERVENTORIA

GUTIERREZ DÍAZ S.A.S.

Superintendencia de Construcción

Director de Interventoría:

Ing. Jorge Iván García Mancilla

MAT. 632021 148063 QND

Versión	Emisión	Descripción
AA	15-06-2023	Ingeniería básica
AB	04-08-2023	Anteproyecto
AC	01-11-2023	Anteproyecto V2 50%
AD	15-12-2023	Anteproyecto V2 100%
DE	13-03-2024	Entrega curaduría
EE	10-05-2024	Proyecto Final 100%
EF	31-05-2024	Respuesta Obs 100%
FF	21-06-2024	Entrega Final
01	28-07-2024	ENTREGA FINAL

PROYECTO:

CAMPUS DE CIENCIA TECNOLOGÍA E INNOVACIÓN DE BOGOTÁ

MAT. No. 502-00252470

FASE

ENTREGA FINAL

PROPÓSITO DE EMISIÓN

Curaduría

Revisión

Entrega Cliente

Coordinación

Construcción

NOTIFICACION

Nivel 24

Nivel 23

Nivel 22

Nivel 21

Nivel 20

Nivel 19

Nivel 18

Nivel 17

Nivel 16

Nivel 15

Nivel 14

Nivel 13

Nivel 12

Nivel 11

Nivel 10

Nivel 9

Nivel 8

Nivel 7

Nivel 6

Nivel 5

Nivel 4

Nivel 3

Nivel 2

Nivel 1

Nivel 01

Nivel 02

KEY PLAN

1C

1B

1A

Fecha:

26-07-2024

Escala:

As Indicated

DESPIECES DE PANTALLAS

CTIB_CNI_EST_401_DSP_XXX_01

PROYECTO DETALLADO

APTO PARA CONSTRUCCIÓN (APC)

NOTA: Ver detalle remate refuerzo horizontal zona central muros pantalla plano N°E-0000