

ARQUITECTO COORDINADOR

EL EQUIPO
MAZZANTI + Gensler

DISÑO ESTRUCTURAL



W. B. B. B.

DISEÑADOR ING. NICOLÁS PARRA GARCÍA
MAT. 232021 148063 QND

INTERVENTORIA



GUTIERREZ DÍAZ S.A.S.
SUPERVISOR Y LABORATORIO DE INVESTIGACIÓN

Director de Interventoría: Ing. Jorge Iván García Mancilla
Mat. 632021 148063 QND


Versión	Emisión	Descripción
AA	15-06-2023	Ingeniería básica
AB	04-08-2023	Anteproyecto
AC	01-11-2023	Anteproyecto V2 50%
AD	15-12-2023	Anteproyecto V2 100%
DD	13-03-2024	Entrega curaduría
DE	10-05-2024	Proyecto Final 100%
EF	31-05-2024	Respuesta Obs 100%
FF	21-06-2024	Entrega Final
01	28-07-2024	ENTREGA FINAL

PROYECTO:
CAMPUS DE CIENCIA TECNOLOGÍA E
INNOVACIÓN DE BOGOTÁ
MAT. No. 500-202324010

FASE
ENTREGA FINAL

PROPÓSITO DE EMISIÓN			
Curaduría	☐	Coordinación	☐
Revisión	☐	Construcción	☐
Entrega Cliente	☒		

ZONIFICACIÓN	
Nivel 24	
Nivel 23	
Nivel 22	
Nivel 21	
Nivel 20	
Nivel 19	
Nivel 18	
Nivel 17	
Nivel 16	
Nivel 15	
Nivel 14	
Nivel 13	
Nivel 12	
Nivel 11	
Nivel 10	
Nivel 9	
Nivel 8	
Nivel 7	
Nivel 6	
Nivel 5	
Nivel 4	
Nivel 3	
Nivel 2	
Nivel 1	
Nivel 01	
Nivel 02	

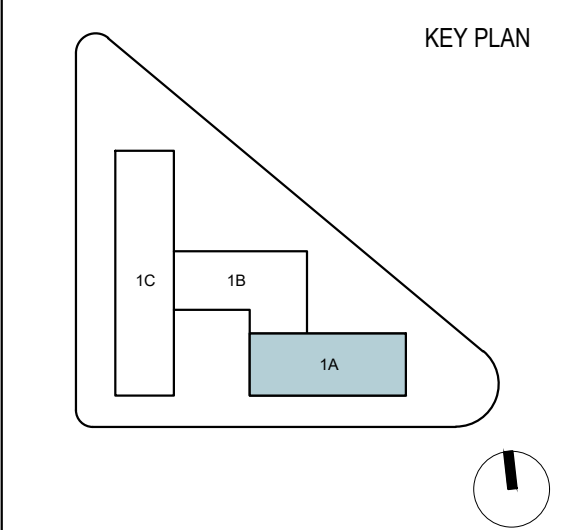


Fecha: 28-07-2024

Escala: As Indicated

DESPIECES DE
PANTALLAS

CTIB_CNI_EST_404_DSP_XXX_01

DESPIECE DE PANTALLA P-5
escala 1:75

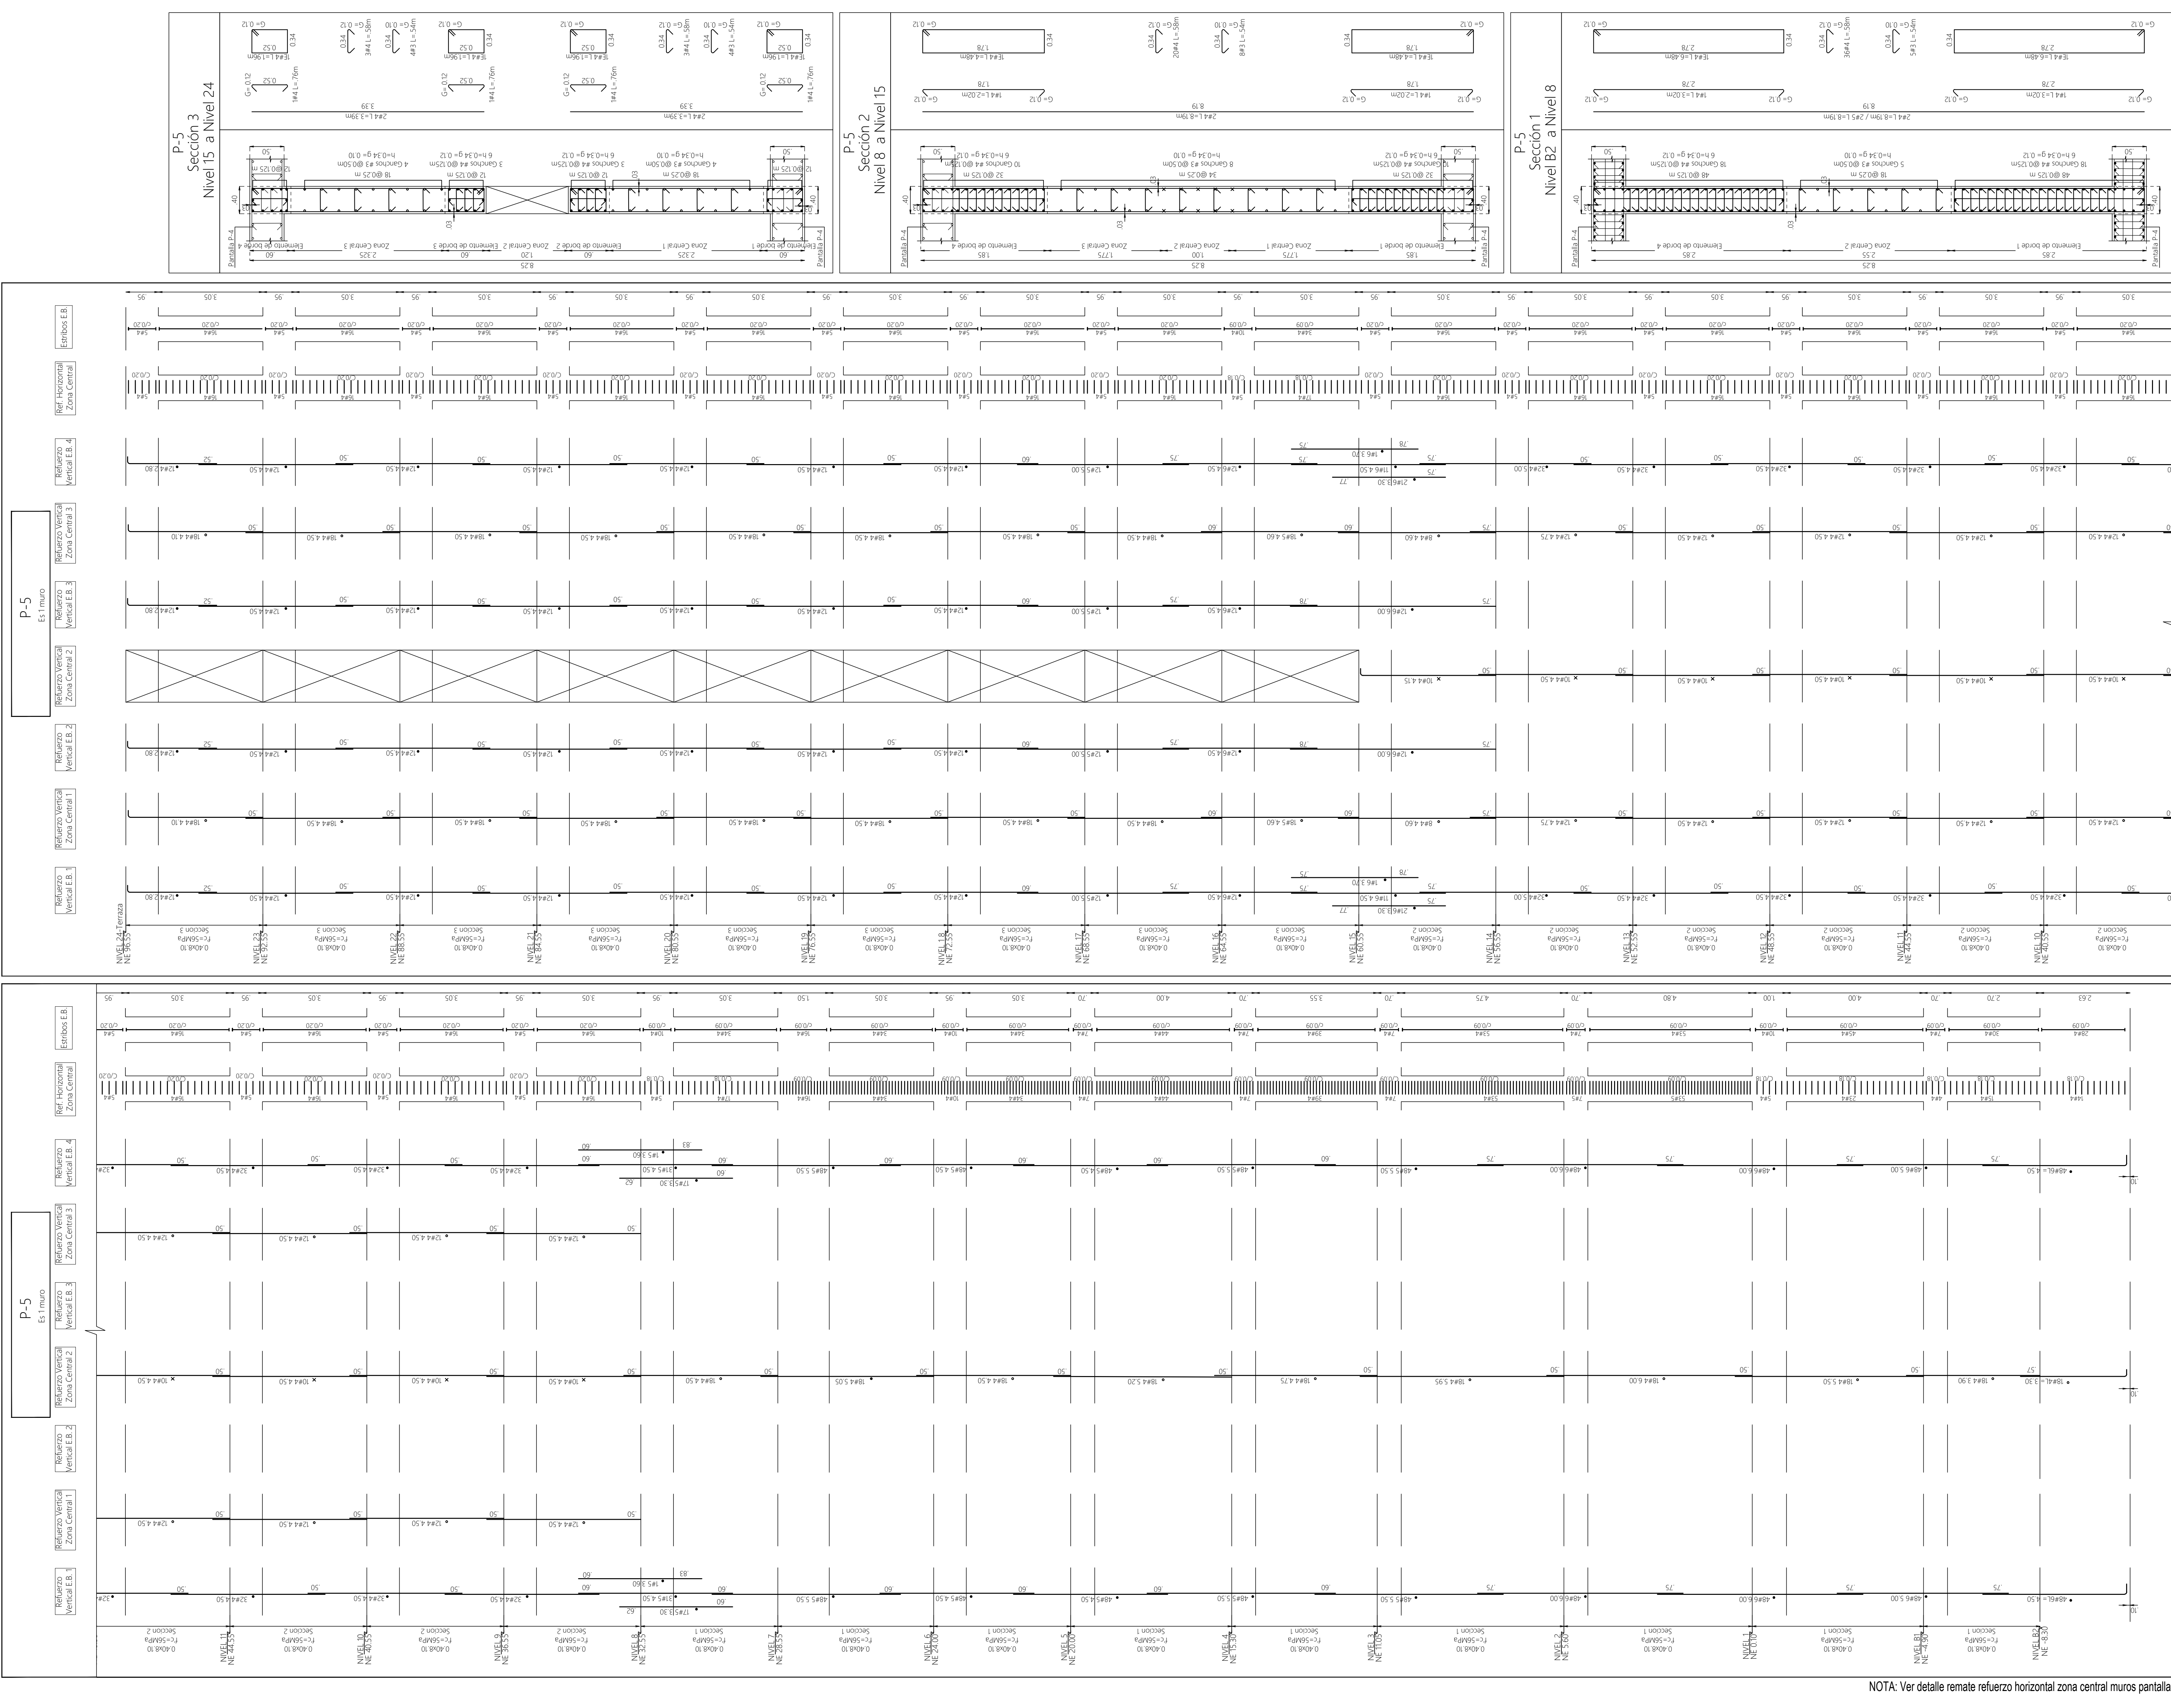

NOTA: Ver detalle remate refuerzo horizontal zona central muros pantalla plano N°E-0000