
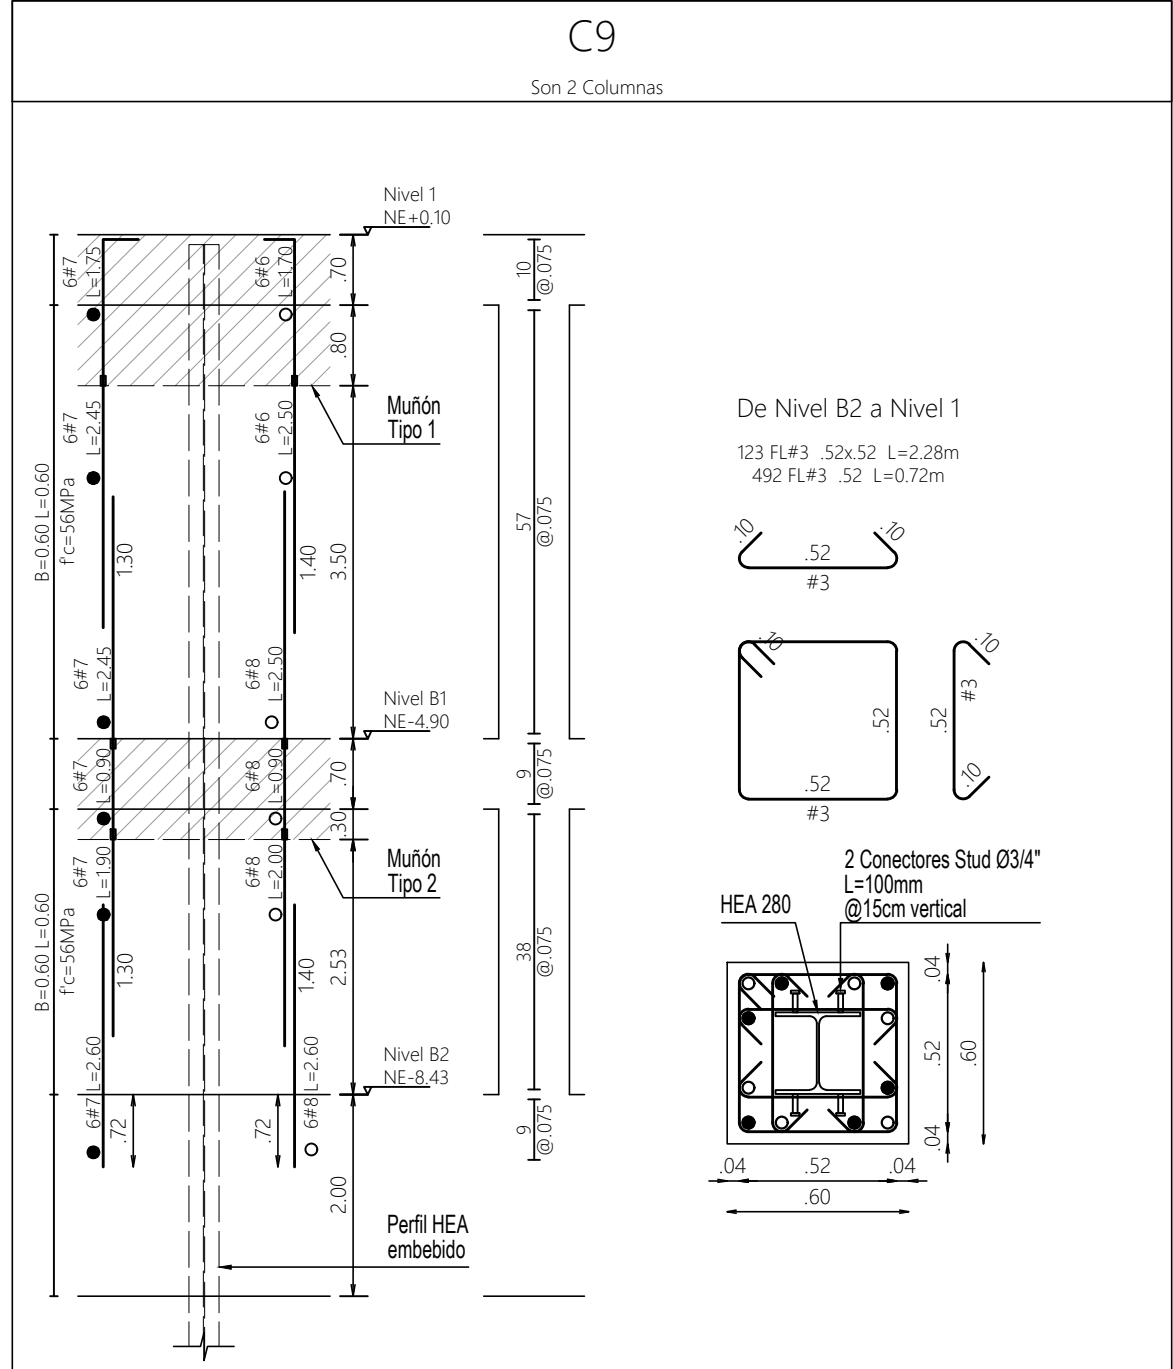
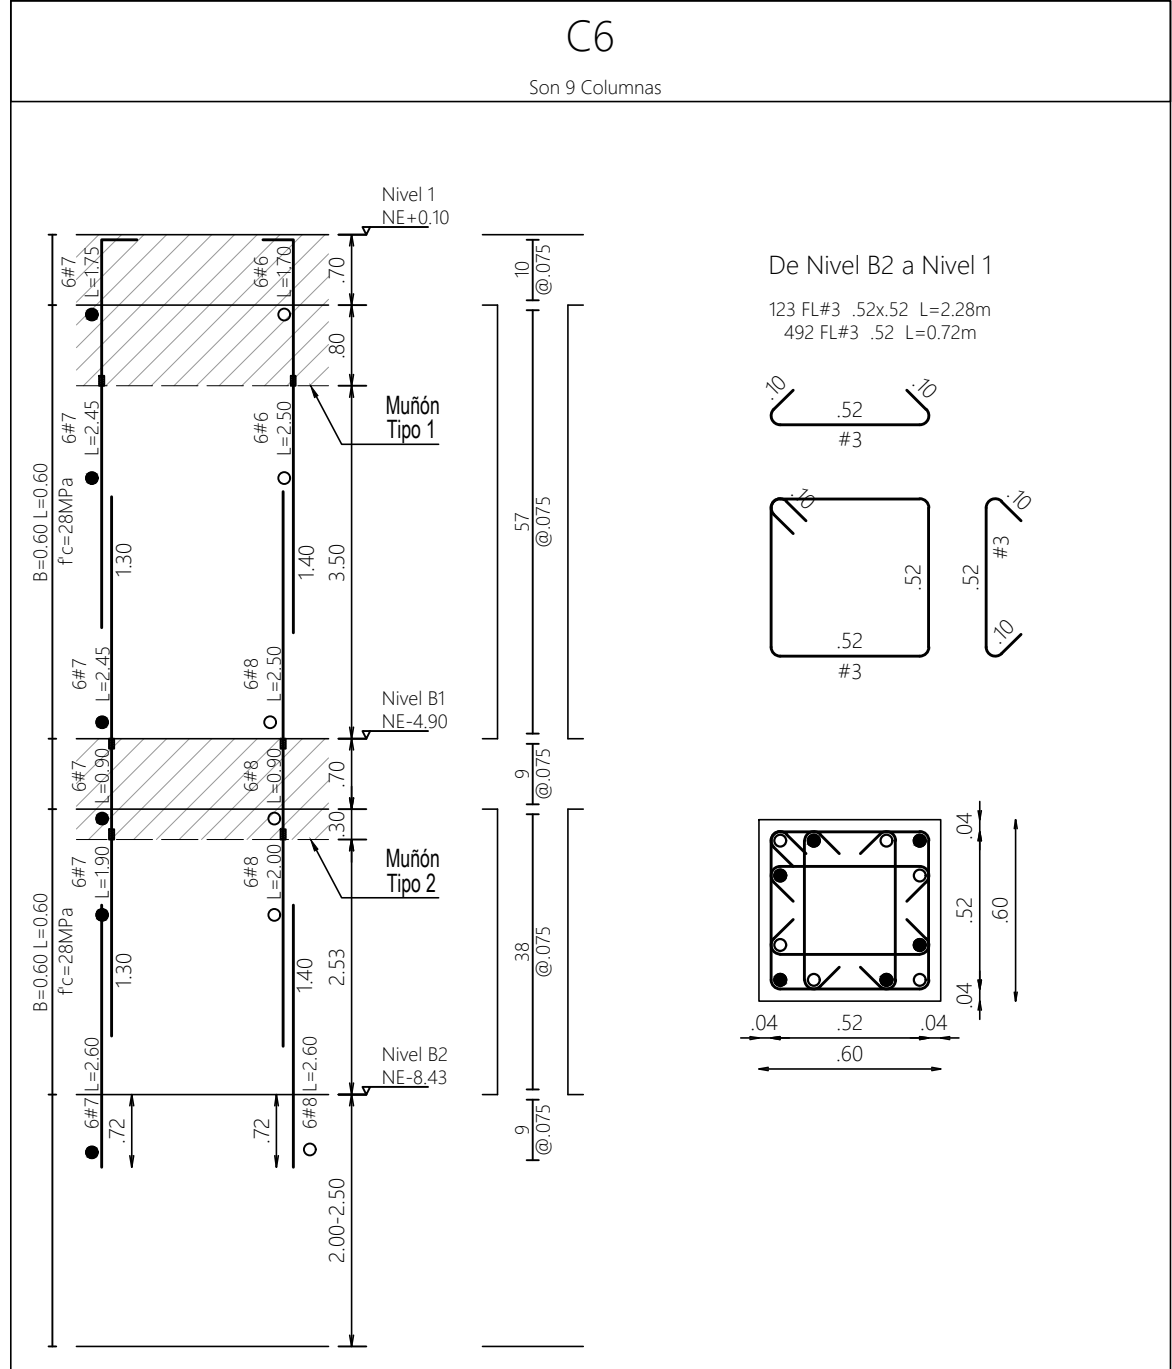
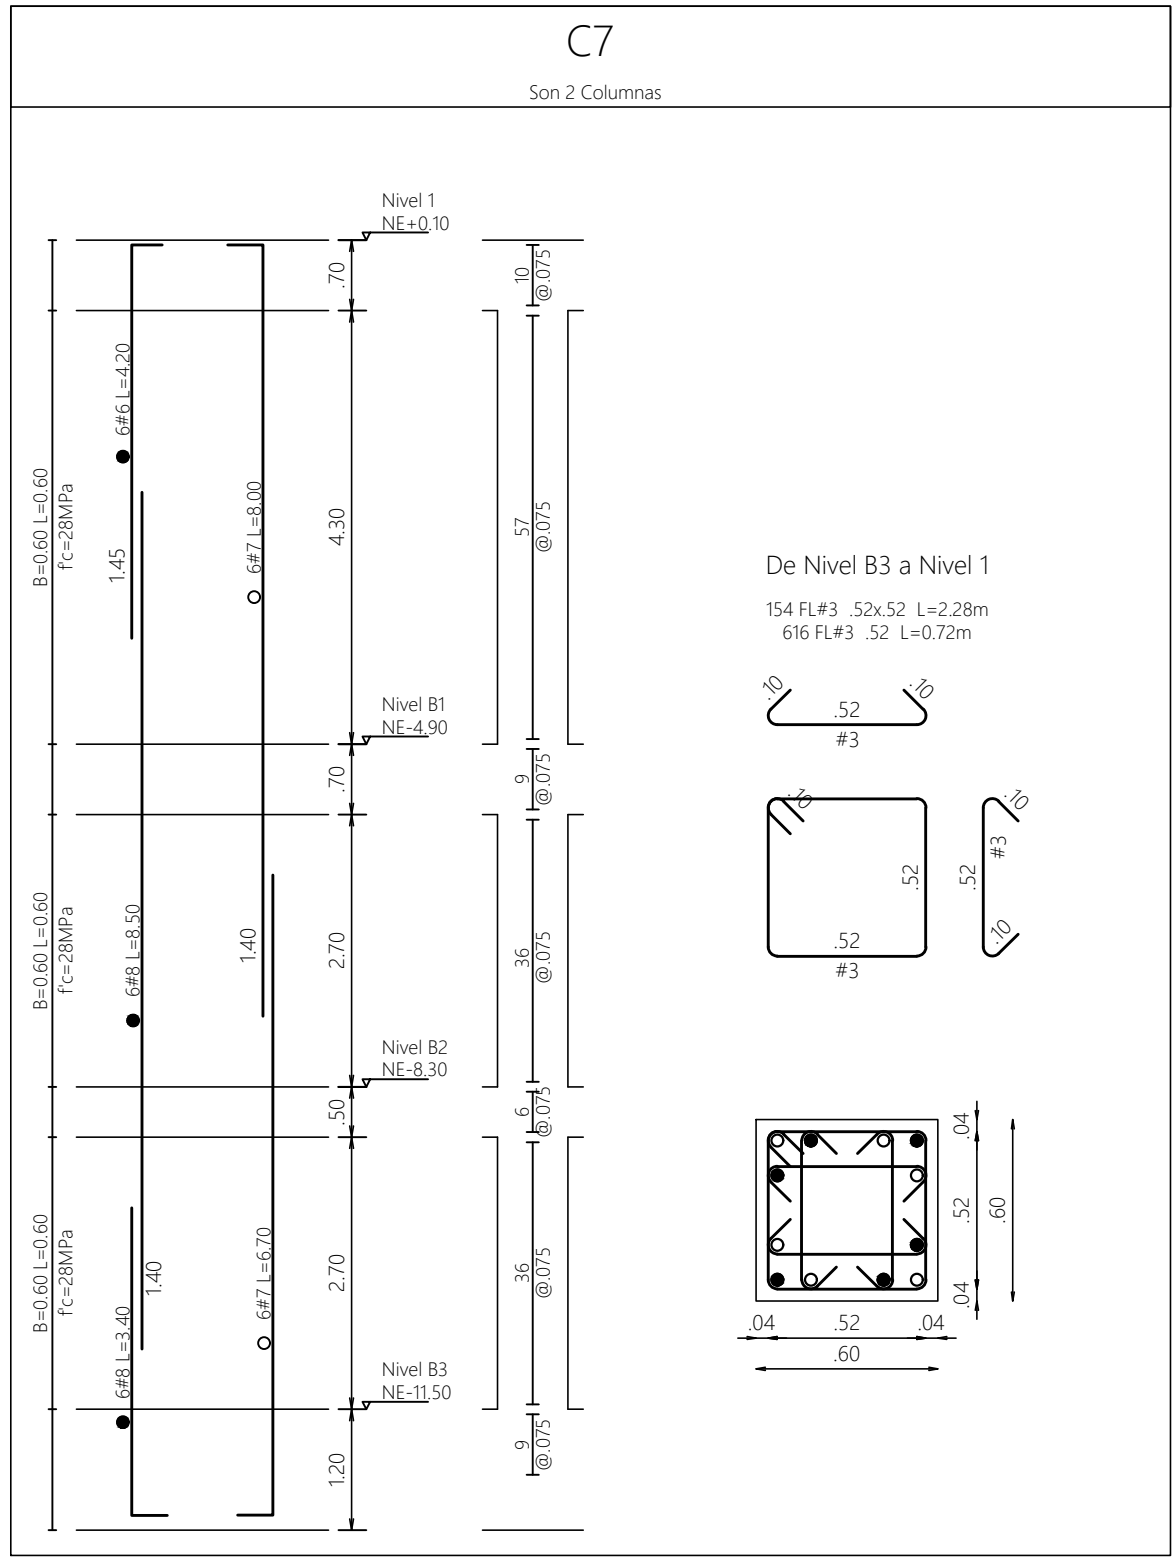
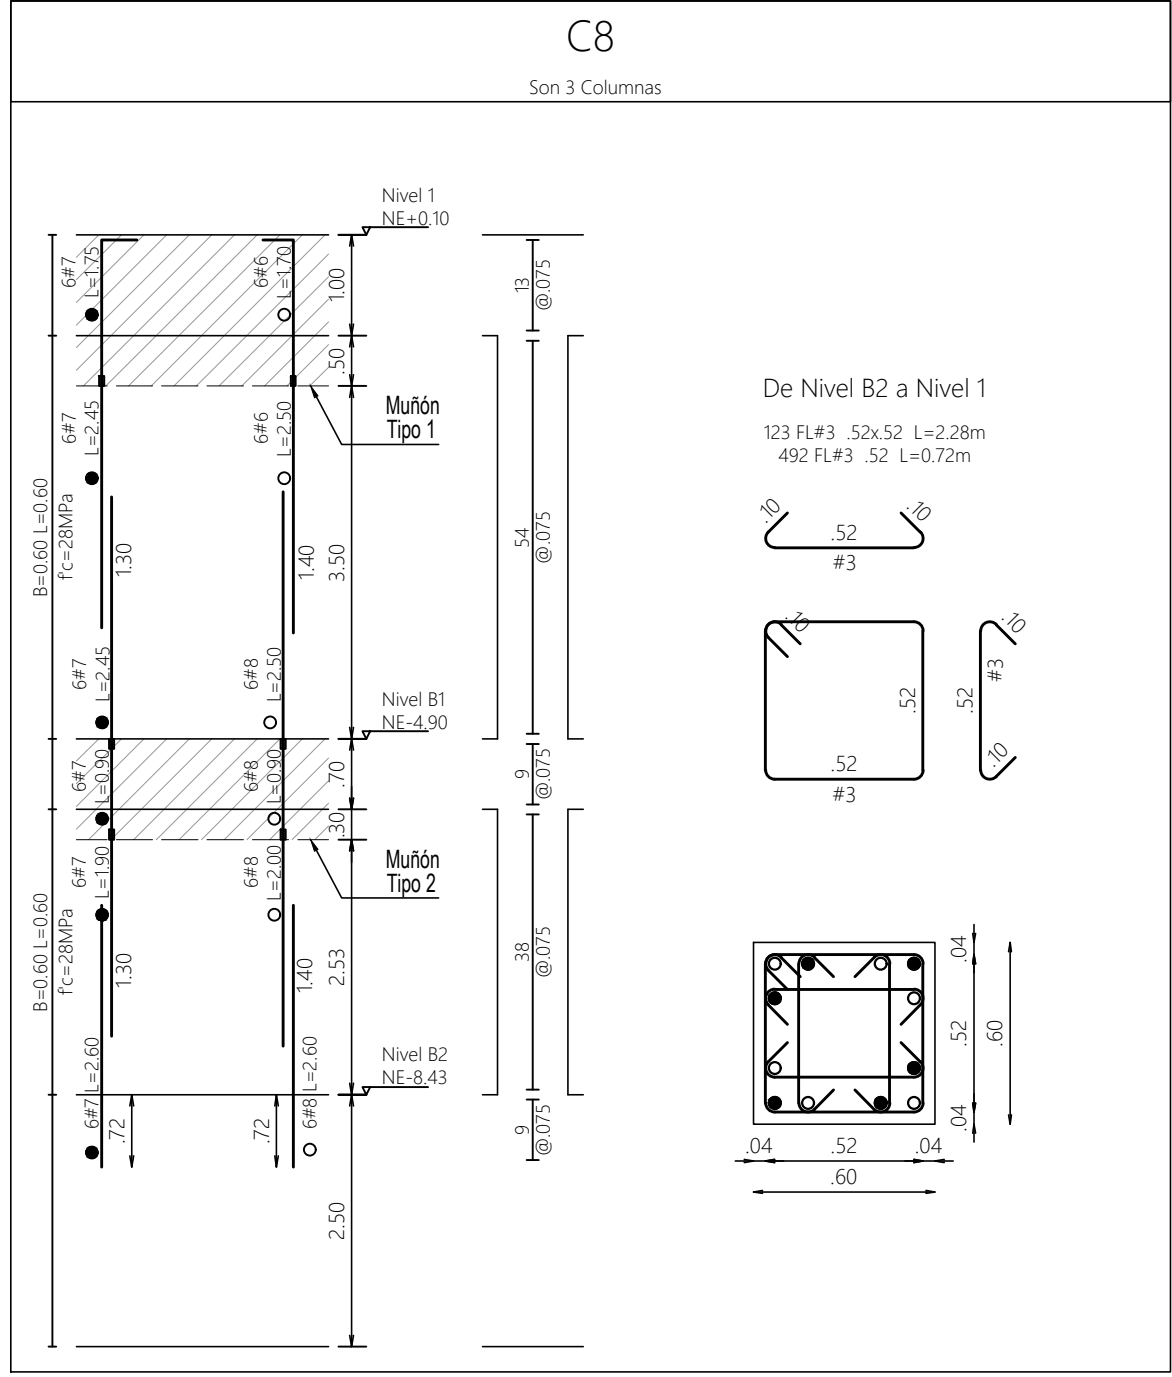
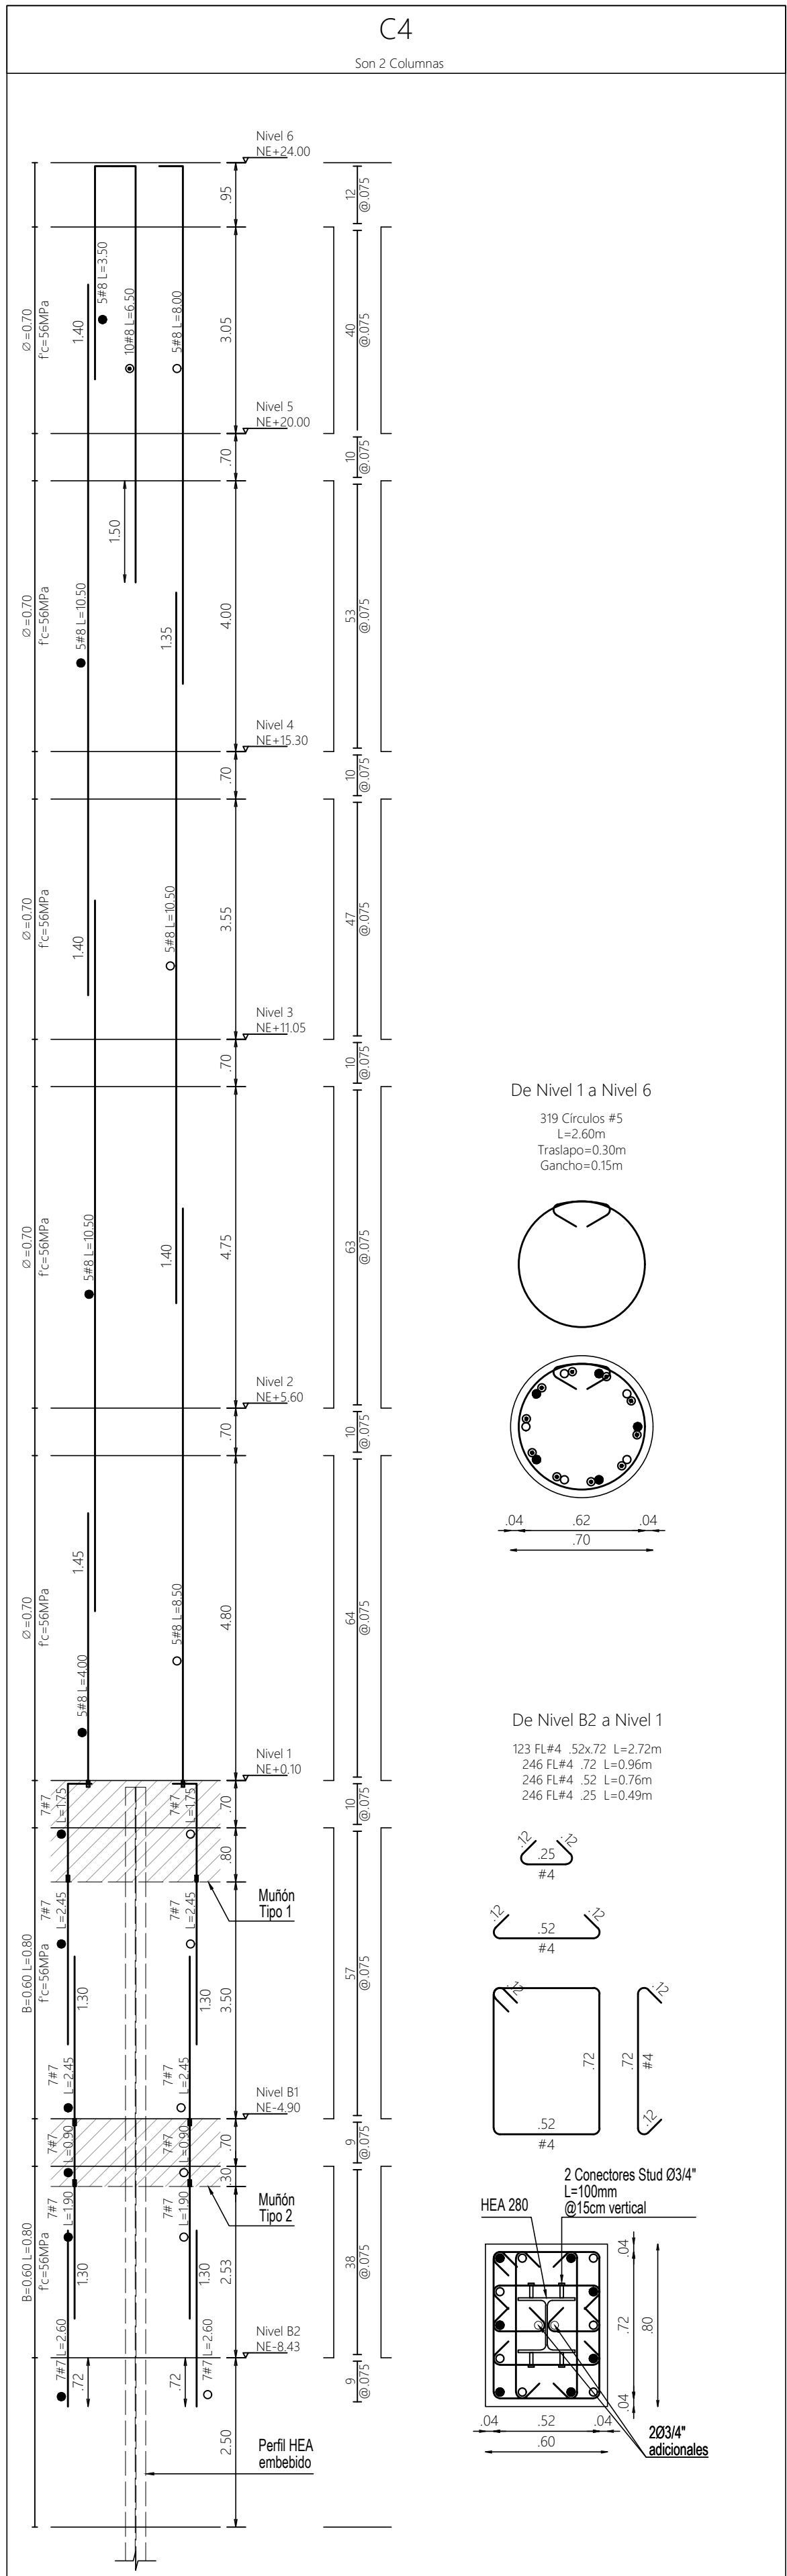
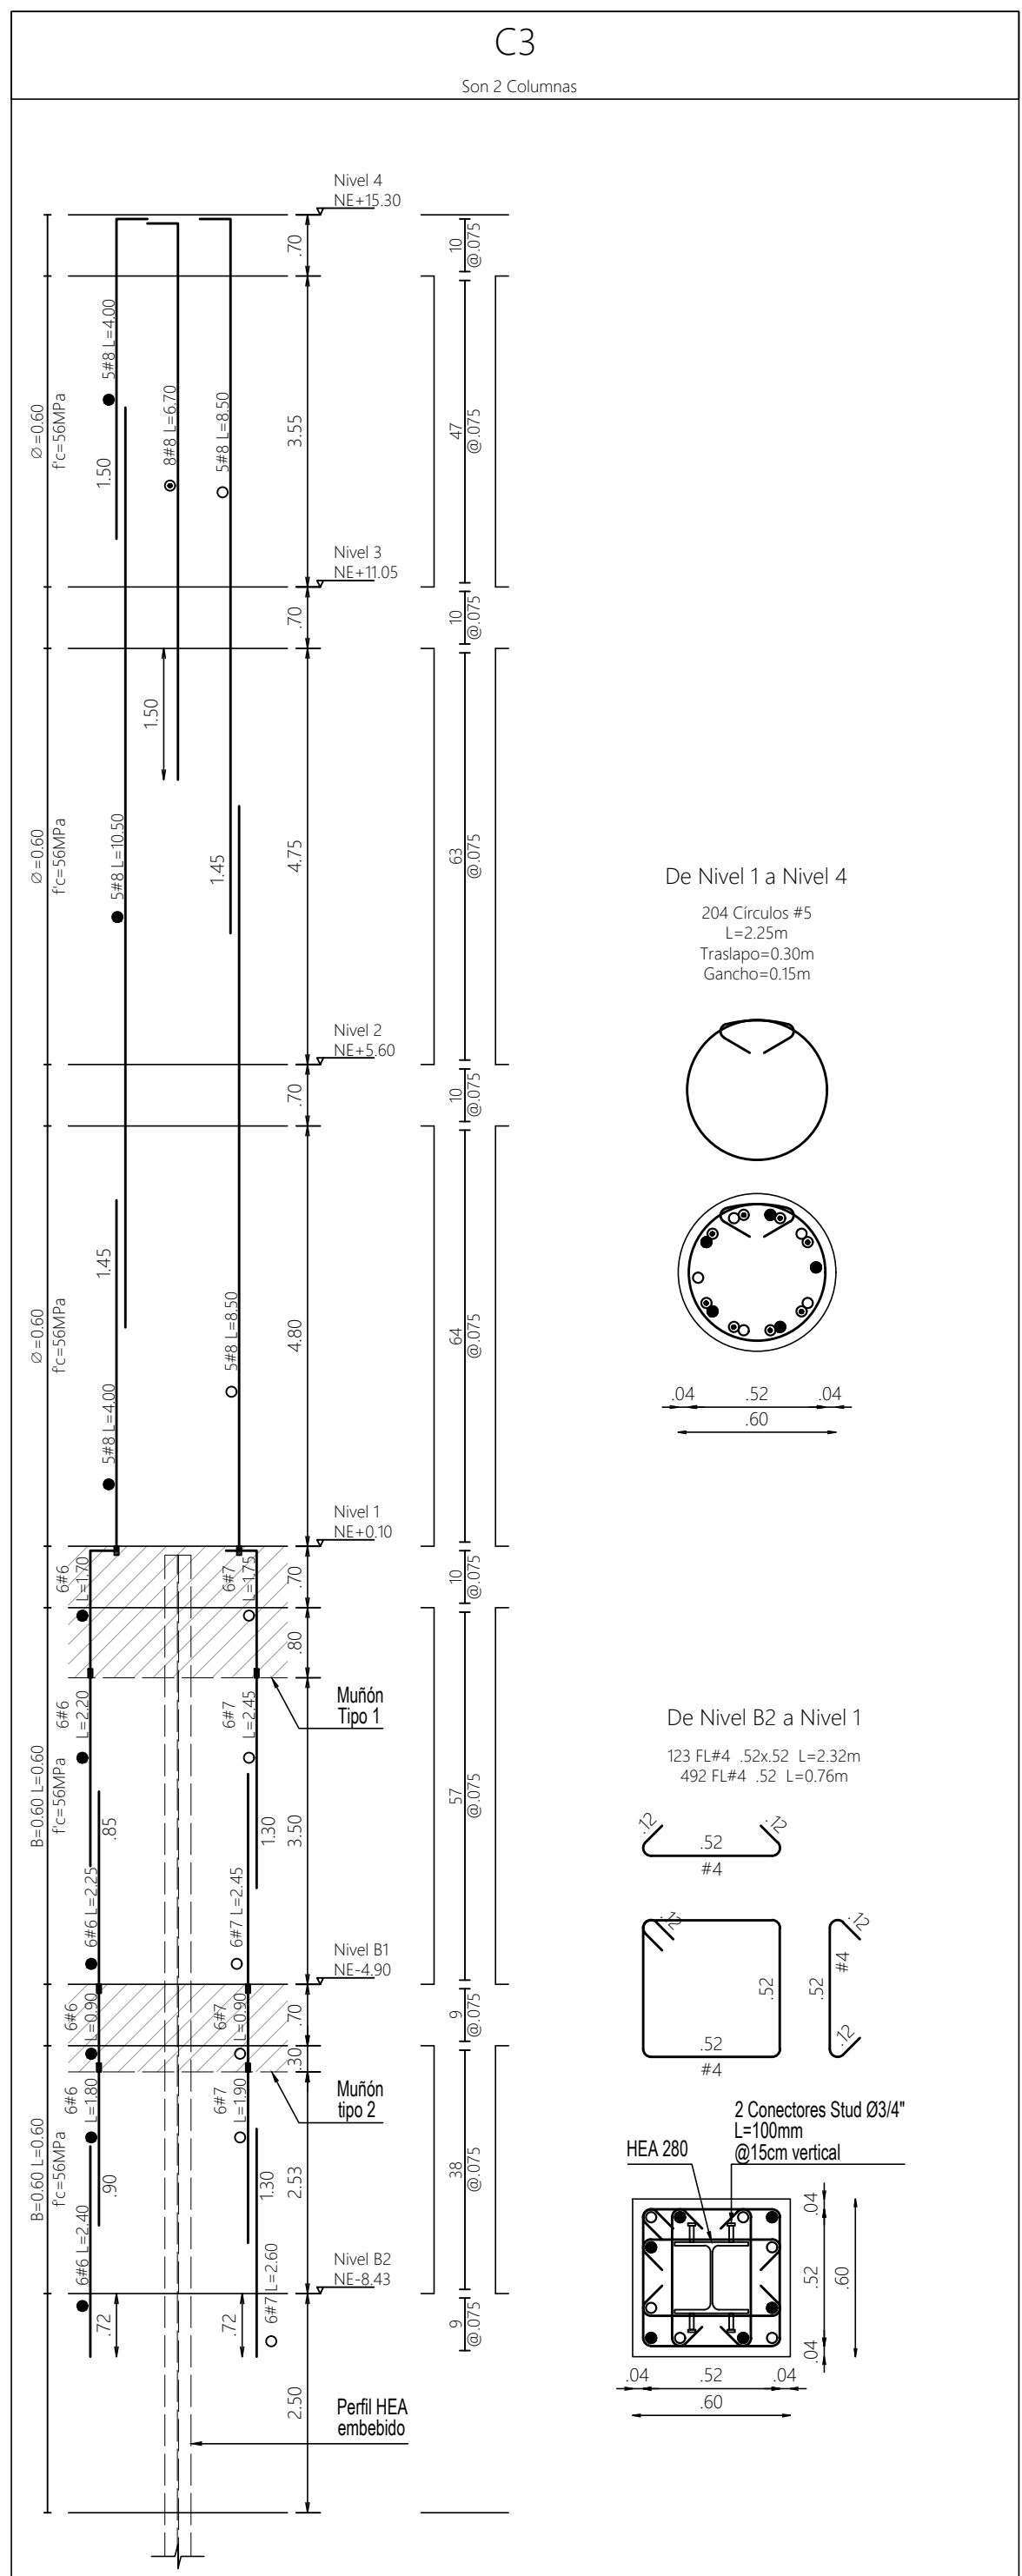


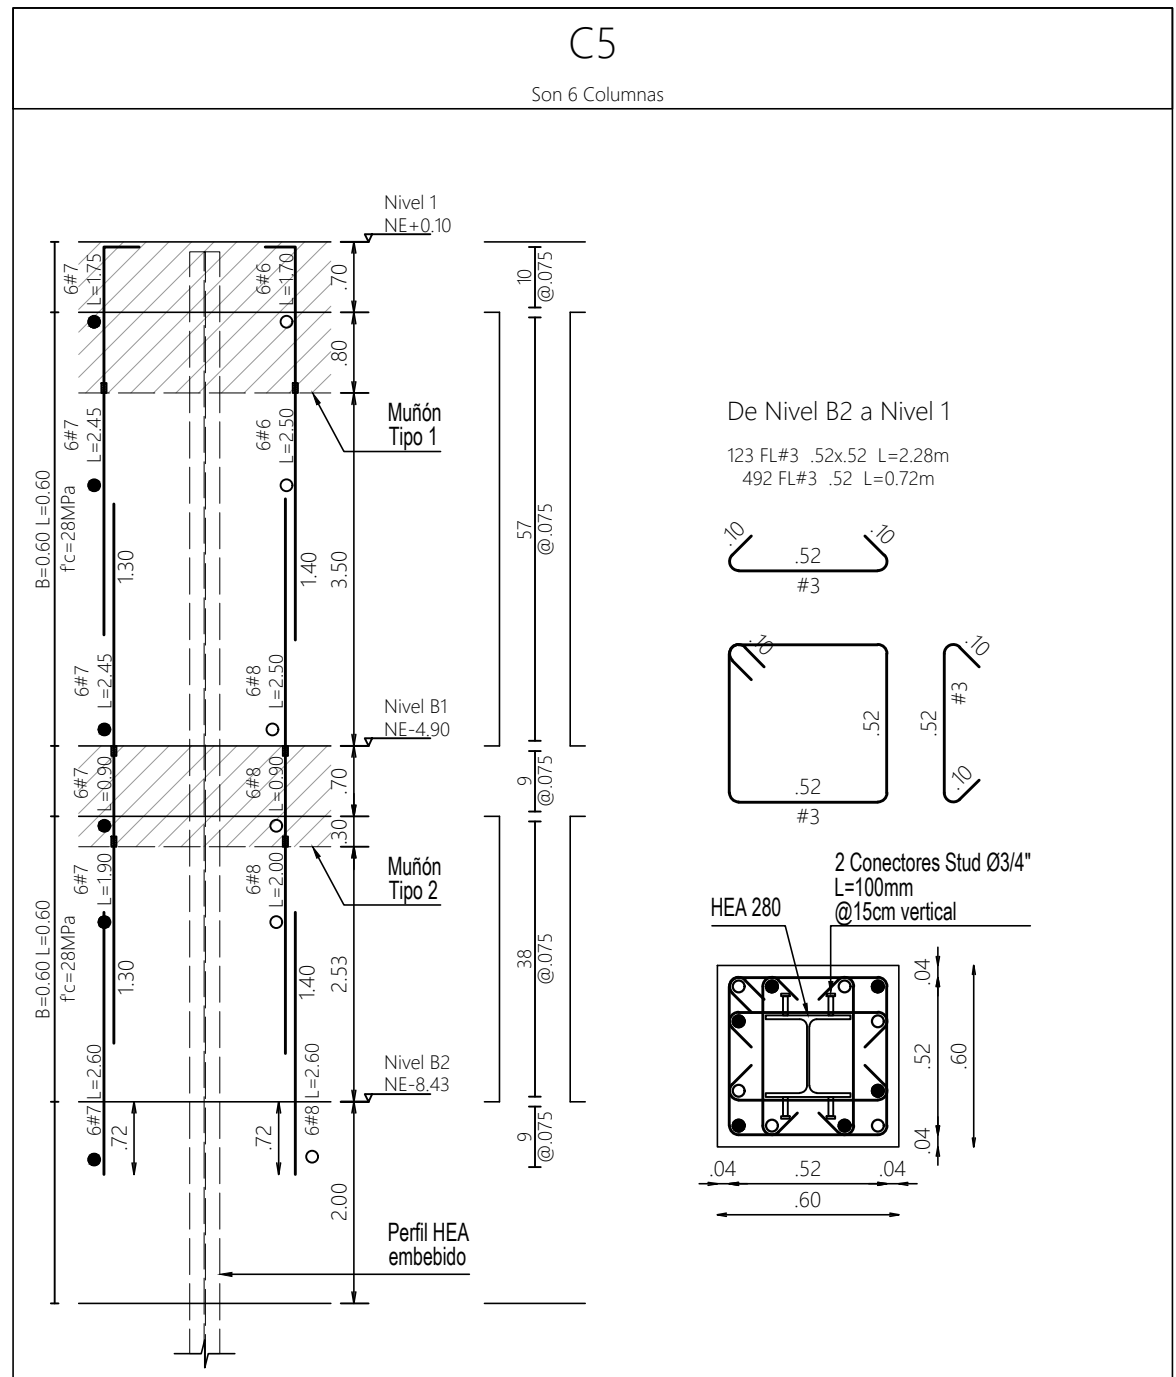

DESPIECES DE COLUMNAS

escala 1:75

Notas:

- Ver esquema de armado base columnas en plano E000
- Ver detalle de muñones en plano CTIB_CNI_EST_604_PCO_XXX



Indica muñón de columna fundido en Primera Etapa. Prever empalmes mecánicos



Empalme mecánico tipo 2

CTIB

Campus de Ciencia, Tecnología e Innovación de Bogotá - Región



ARQUITECTO COORDINADOR

ELEQUIPO MAZZANTI + Gensler

DISÑO ESTRUCTURAL



ING. NICOLÁS PARRA GARCÍA

DISEÑADOR

INTERVENTORIA



Director de Interventoría: Ing. Jorge Iván García Mancilla
Mat. 632021 148063 QND

Versión	Emisión	Descripción
AA	15-06-2023	Ingeniería básica
AB	04-08-2023	Anteproyecto
AC	01-11-2023	Anteproyecto V2 50%
AD	15-12-2023	Anteproyecto V2 100%
DD	13-03-2024	Entrega curaduría
EE	10-05-2024	Proyecto Final 100%
EF	31-05-2024	Respuesta Obs 100%
FF	21-06-2024	Entrega Final
01	28-07-2024	ENTREGA FINAL


PROYECTO:
CAMPUS DE CIENCIA TECNOLOGÍA E INNOVACIÓN DE BOGOTÁ
MAT. No. 502-0025470

FASE
ENTREGA FINAL

PROPÓSITO DE EMISIÓN
Curaduría ☐ Coordinación ☐
Revisión ☐ Construcción ☒
Entrega Cliente ☒

ZONIFICACION

Nivel 24
Nivel 23
Nivel 22
Nivel 21
Nivel 20
Nivel 19
Nivel 18
Nivel 17
Nivel 16
Nivel 15
Nivel 14
Nivel 13
Nivel 12
Nivel 11
Nivel 10
Nivel 9
Nivel 8
Nivel 7
Nivel 6
Nivel 5
Nivel 4
Nivel 3
Nivel 2
Nivel 1
Nivel B1
Nivel B2

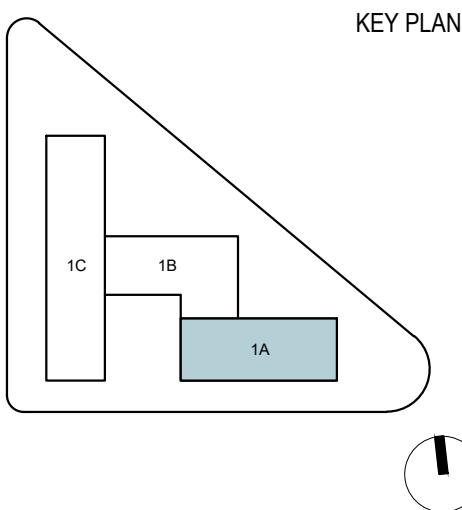

Fecha: 26-07-2024

Escala: As Indicated

DESPIECES DE COLUMNAS

CTIB_CNI_EST_406_DSP_XXX_01