


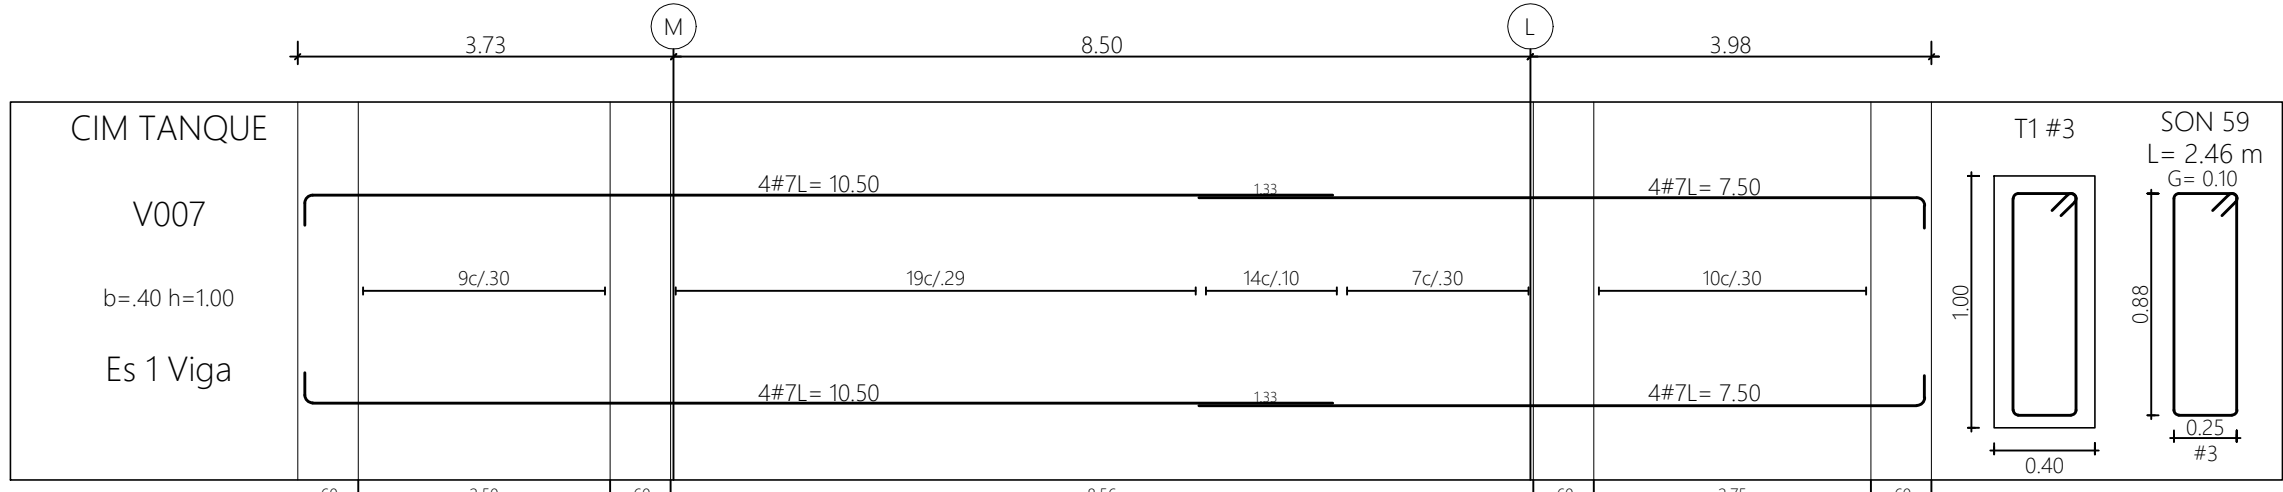
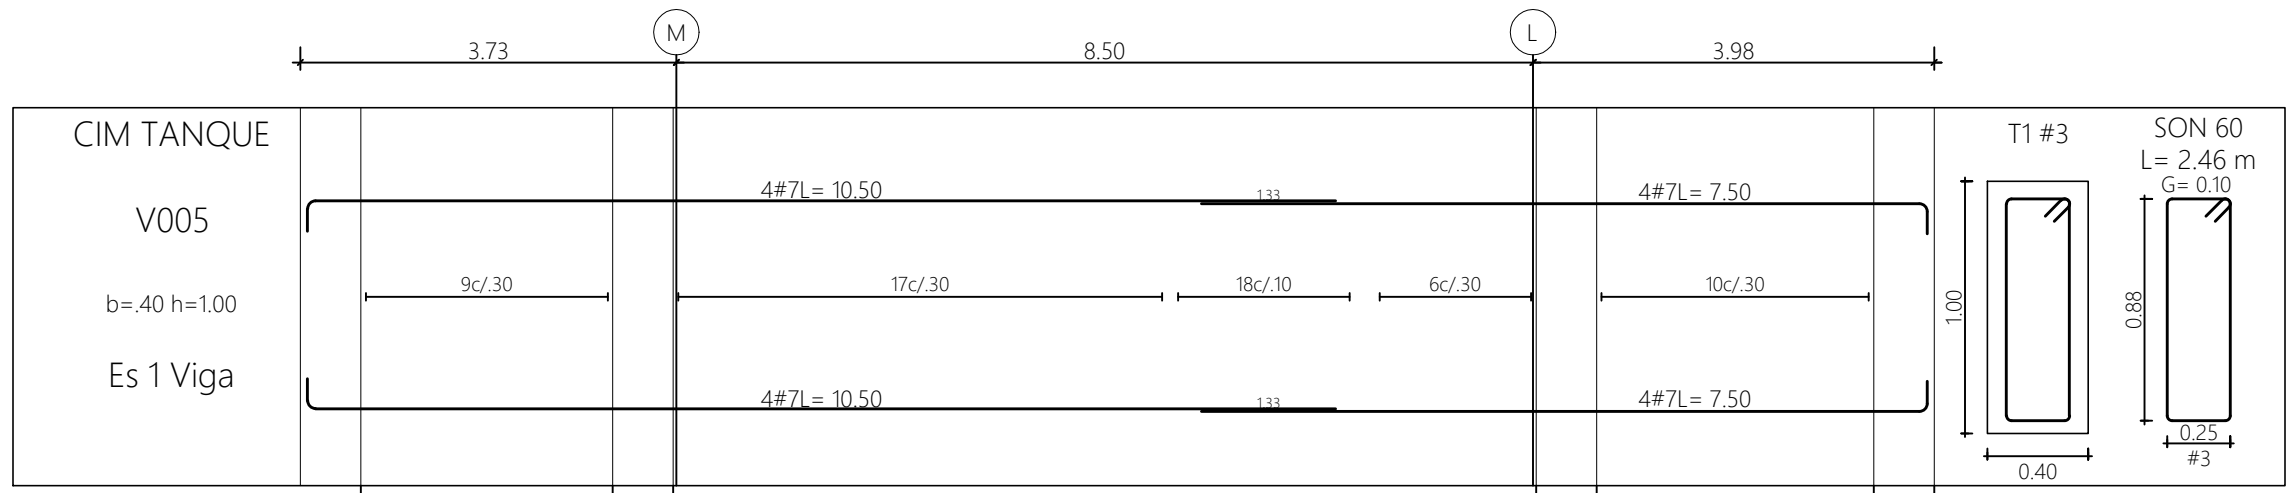
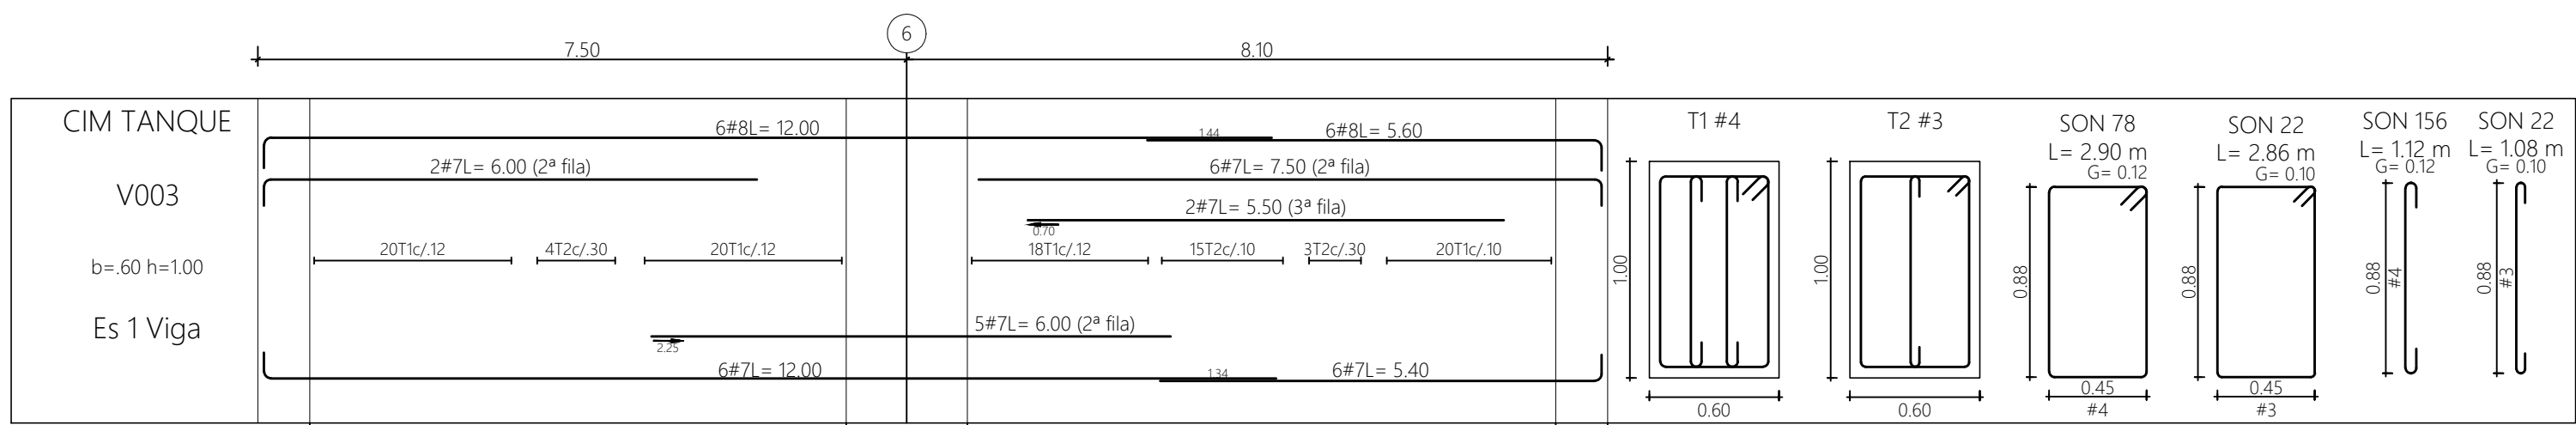
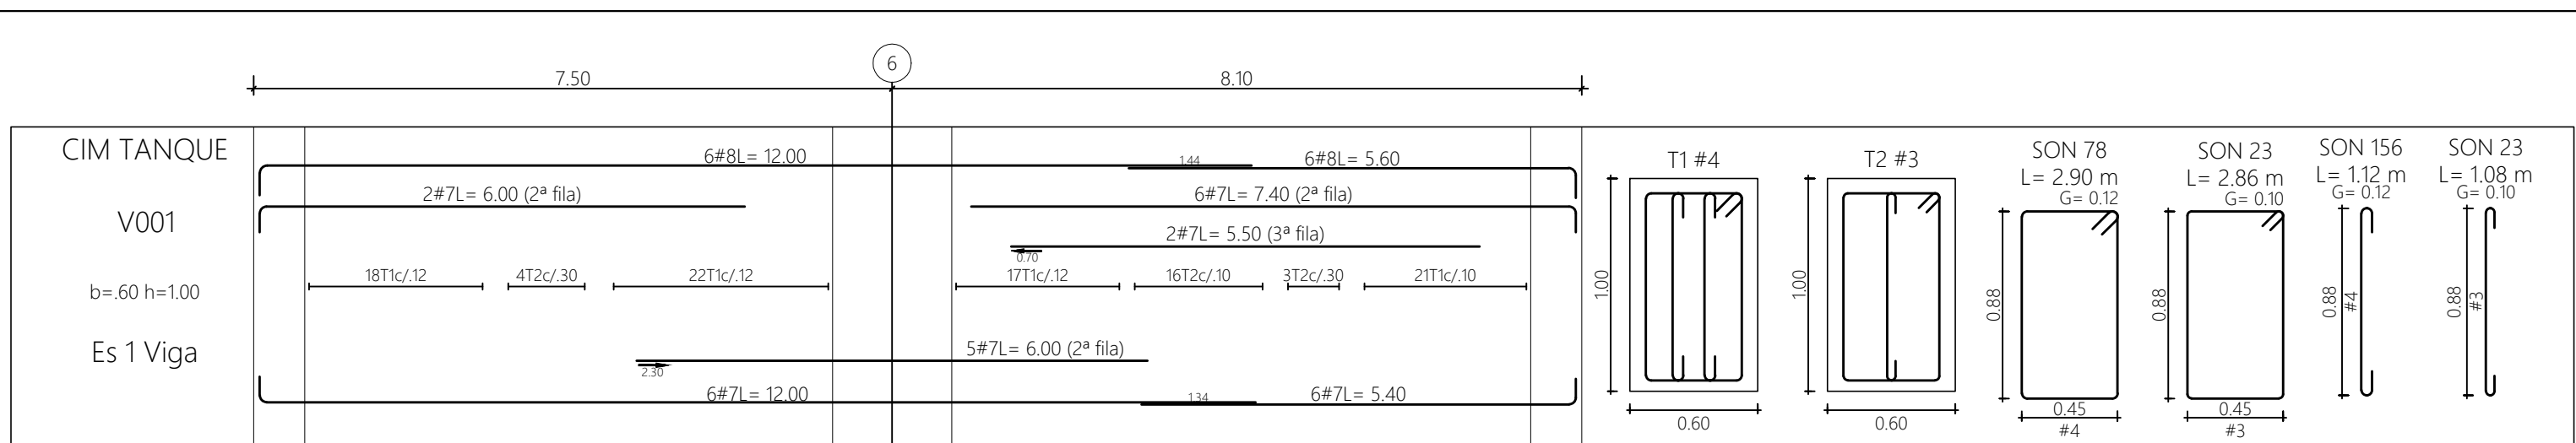


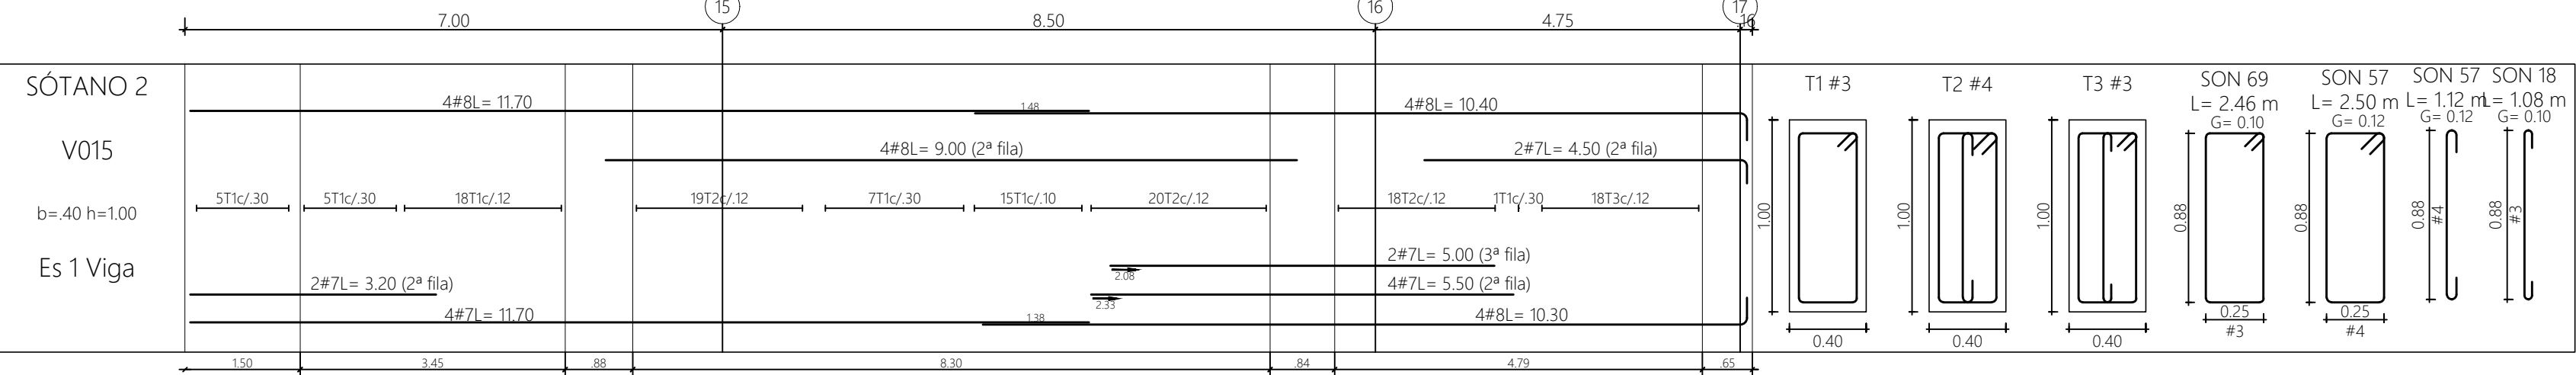

DESPIECE DE VIGAS CIMENTACIÓN TANQUE
escala 1:75

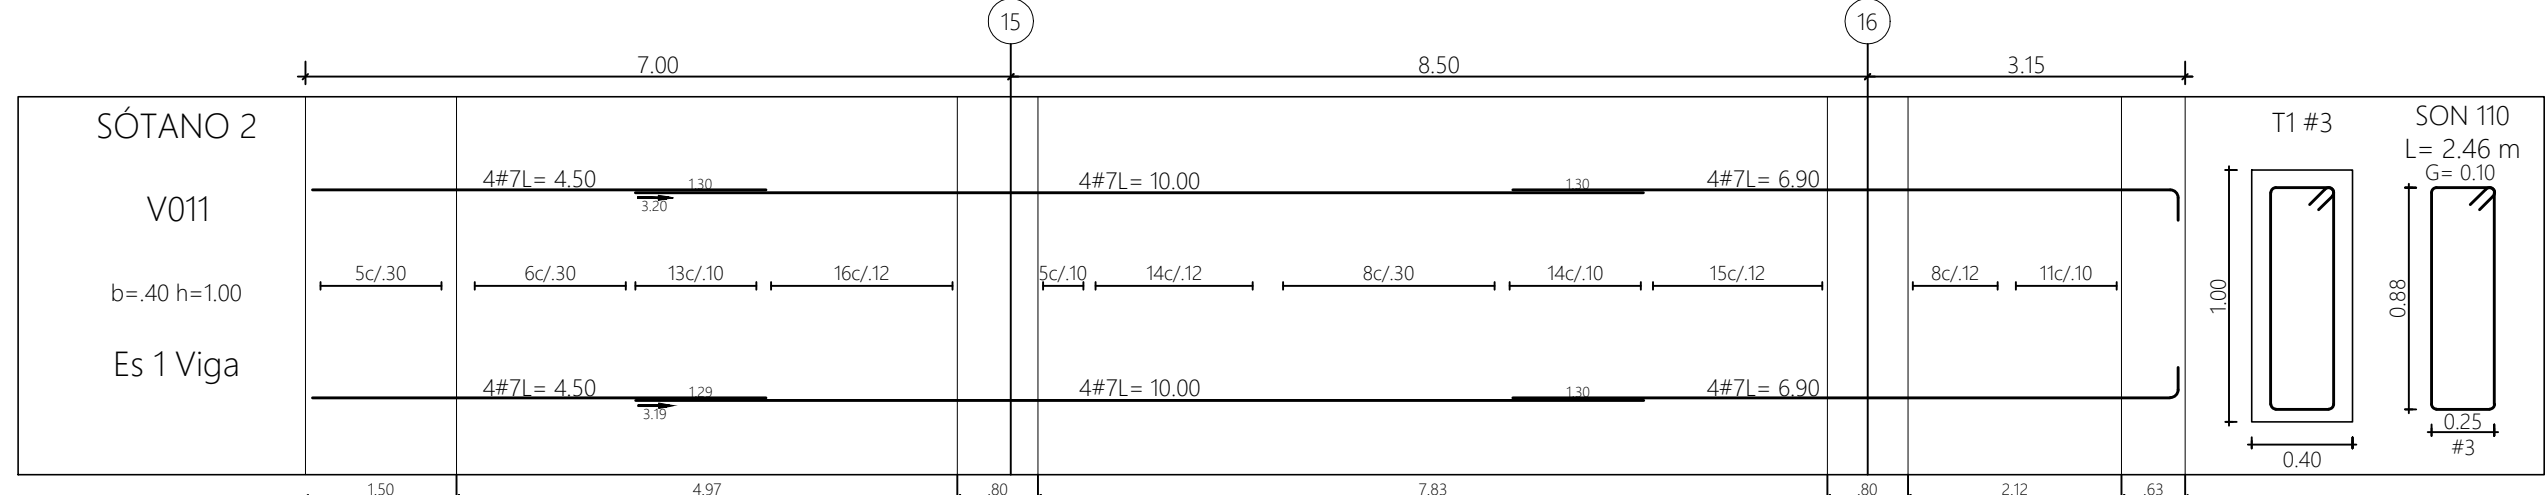

DESPIECE DE VIGAS SOTANO 2
escala 1:75

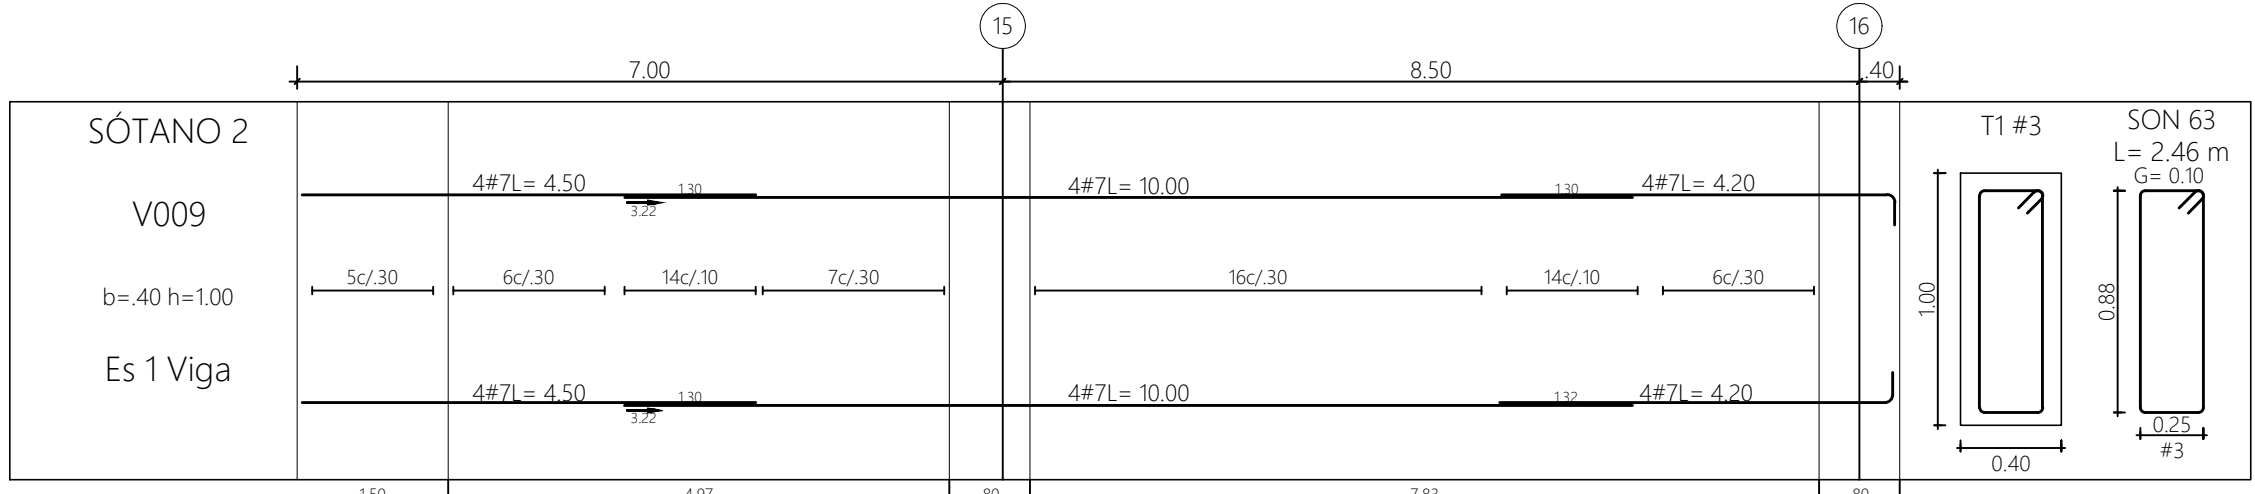