


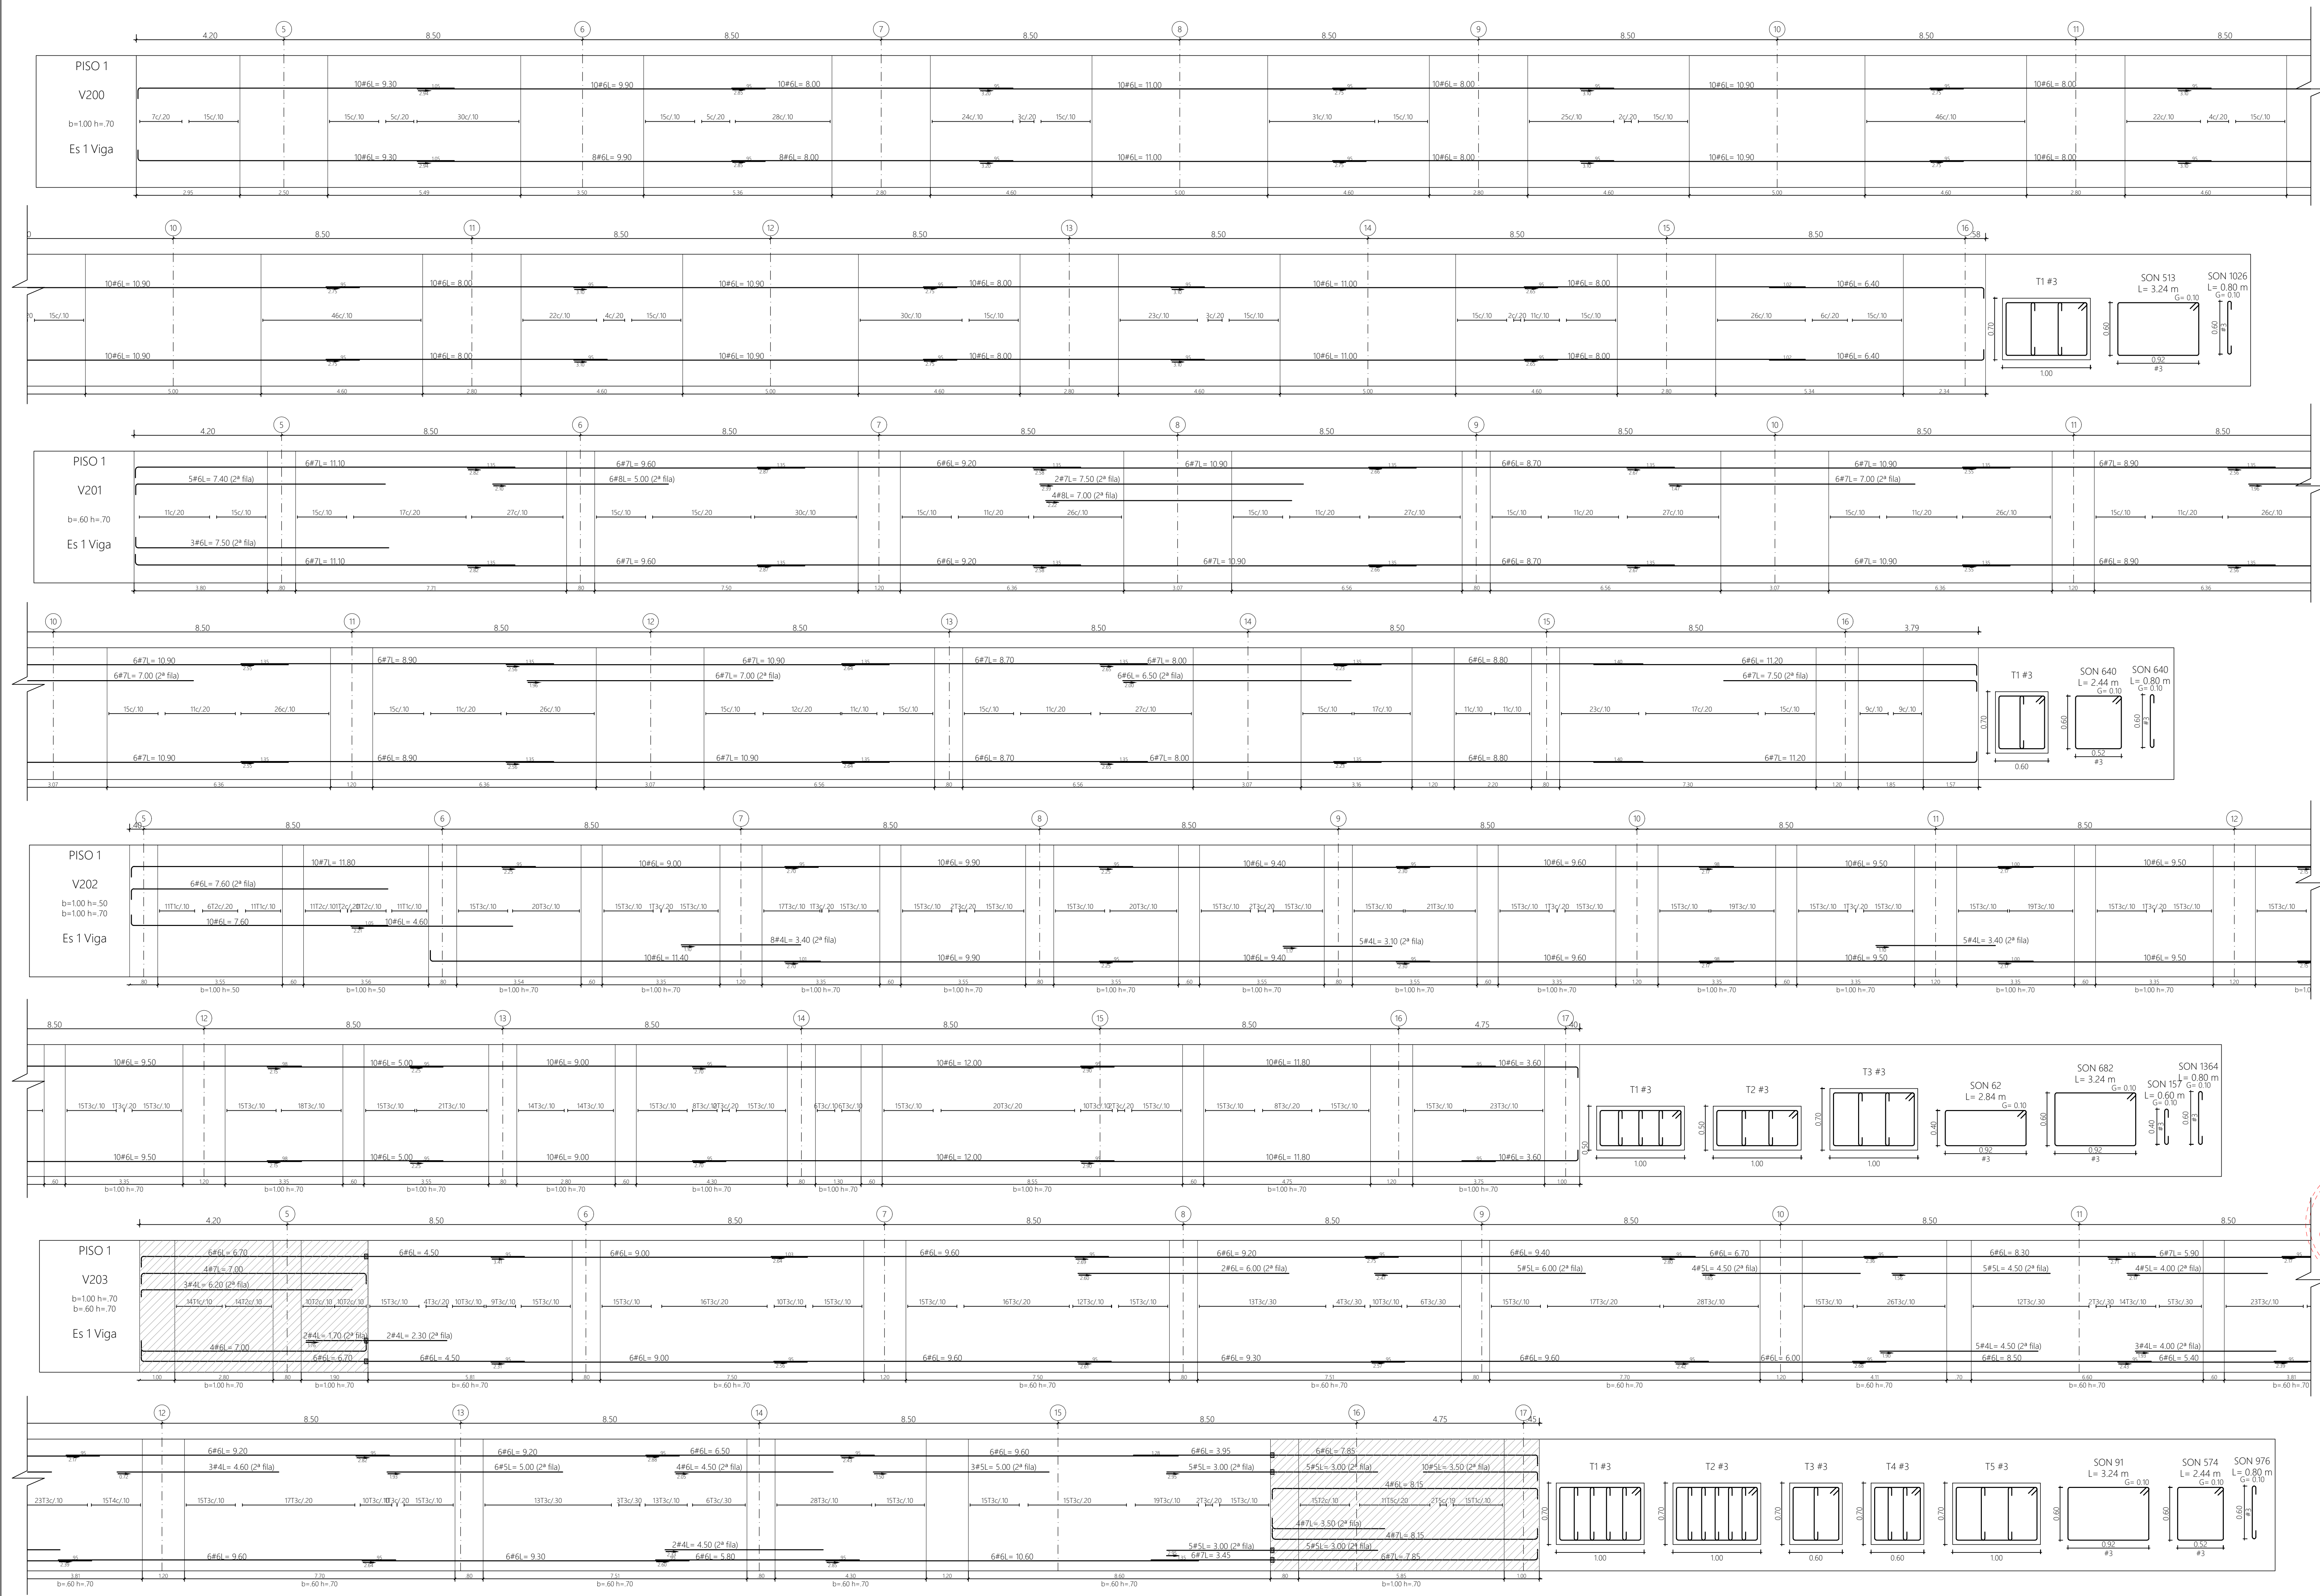

Indica seccion de viga fundida en Primera Etapa, prever conectores
Empalme mecánico tipo 2

DESPIECE DE VIGASDE PISO 1
Escala 1:75
NOTA: Ver esquema de armado base de vigas y viguetas en planos E000

Campus de Ciencia, Tecnología e Innovación de Bogotá - Región

Generadores de Oportunidades y Progreso

BOGOTÁ

ARQUITECTO COORDINADOR

ELEQUIPO MAZZANTI + Gensler

DISÑO ESTRUCTURAL

ING. NICOLÁS PARRA GARCÍA
MAT. 23202 62063 QND

INTERVENTORIA

Director de Interventoria: Ing. Jorge Iván García Mancilla
MAT. 632021 148063 QND

Versión	Emisión	Descripción
AA	15-06-2023	Ingeniería básica
AB	04-08-2023	Anteproyecto
AC	01-11-2023	Anteproyecto V2 50%
AD	15-12-2023	Anteproyecto V2 100%
DD	13-03-2024	Entrega curaduría
EE	10-05-2024	Proyecto Final 100%
EF	31-05-2024	Respuesta Obs 100%
FF	21-06-2024	Entrega Final
01	28-07-2024	ENTREGA FINAL

PROYECTO:
CAMPUS DE CIENCIA TECNOLOGÍA E INNOVACIÓN DE BOGOTÁ
MAT. No. 502-0025470

FASE
ENTREGA FINAL

PROPÓSITO DE EMISIÓN

Curaduría	Revisión	Entrega Cliente	Coordinación	Construcción
☐	☐	☐	☐	☐

SONIFICACION

Nivel	Descripción
Nivel 24	
Nivel 23	
Nivel 22	
Nivel 21	
Nivel 20	
Nivel 19	
Nivel 18	
Nivel 17	
Nivel 16	
Nivel 15	
Nivel 14	
Nivel 13	
Nivel 12	
Nivel 11	
Nivel 10	
Nivel 9	
Nivel 8	
Nivel 7	
Nivel 6	
Nivel 5	
Nivel 4	
Nivel 3	
Nivel 2	
Nivel 1	
Nivel B1	
Nivel B2	

KEY PLAN

Fecha: 28-07-2024

Escala: As Indicated

DESPIECES DE VIGAS DE PISO 1

CTIB_CNI_est_415_DSP_XXX_01