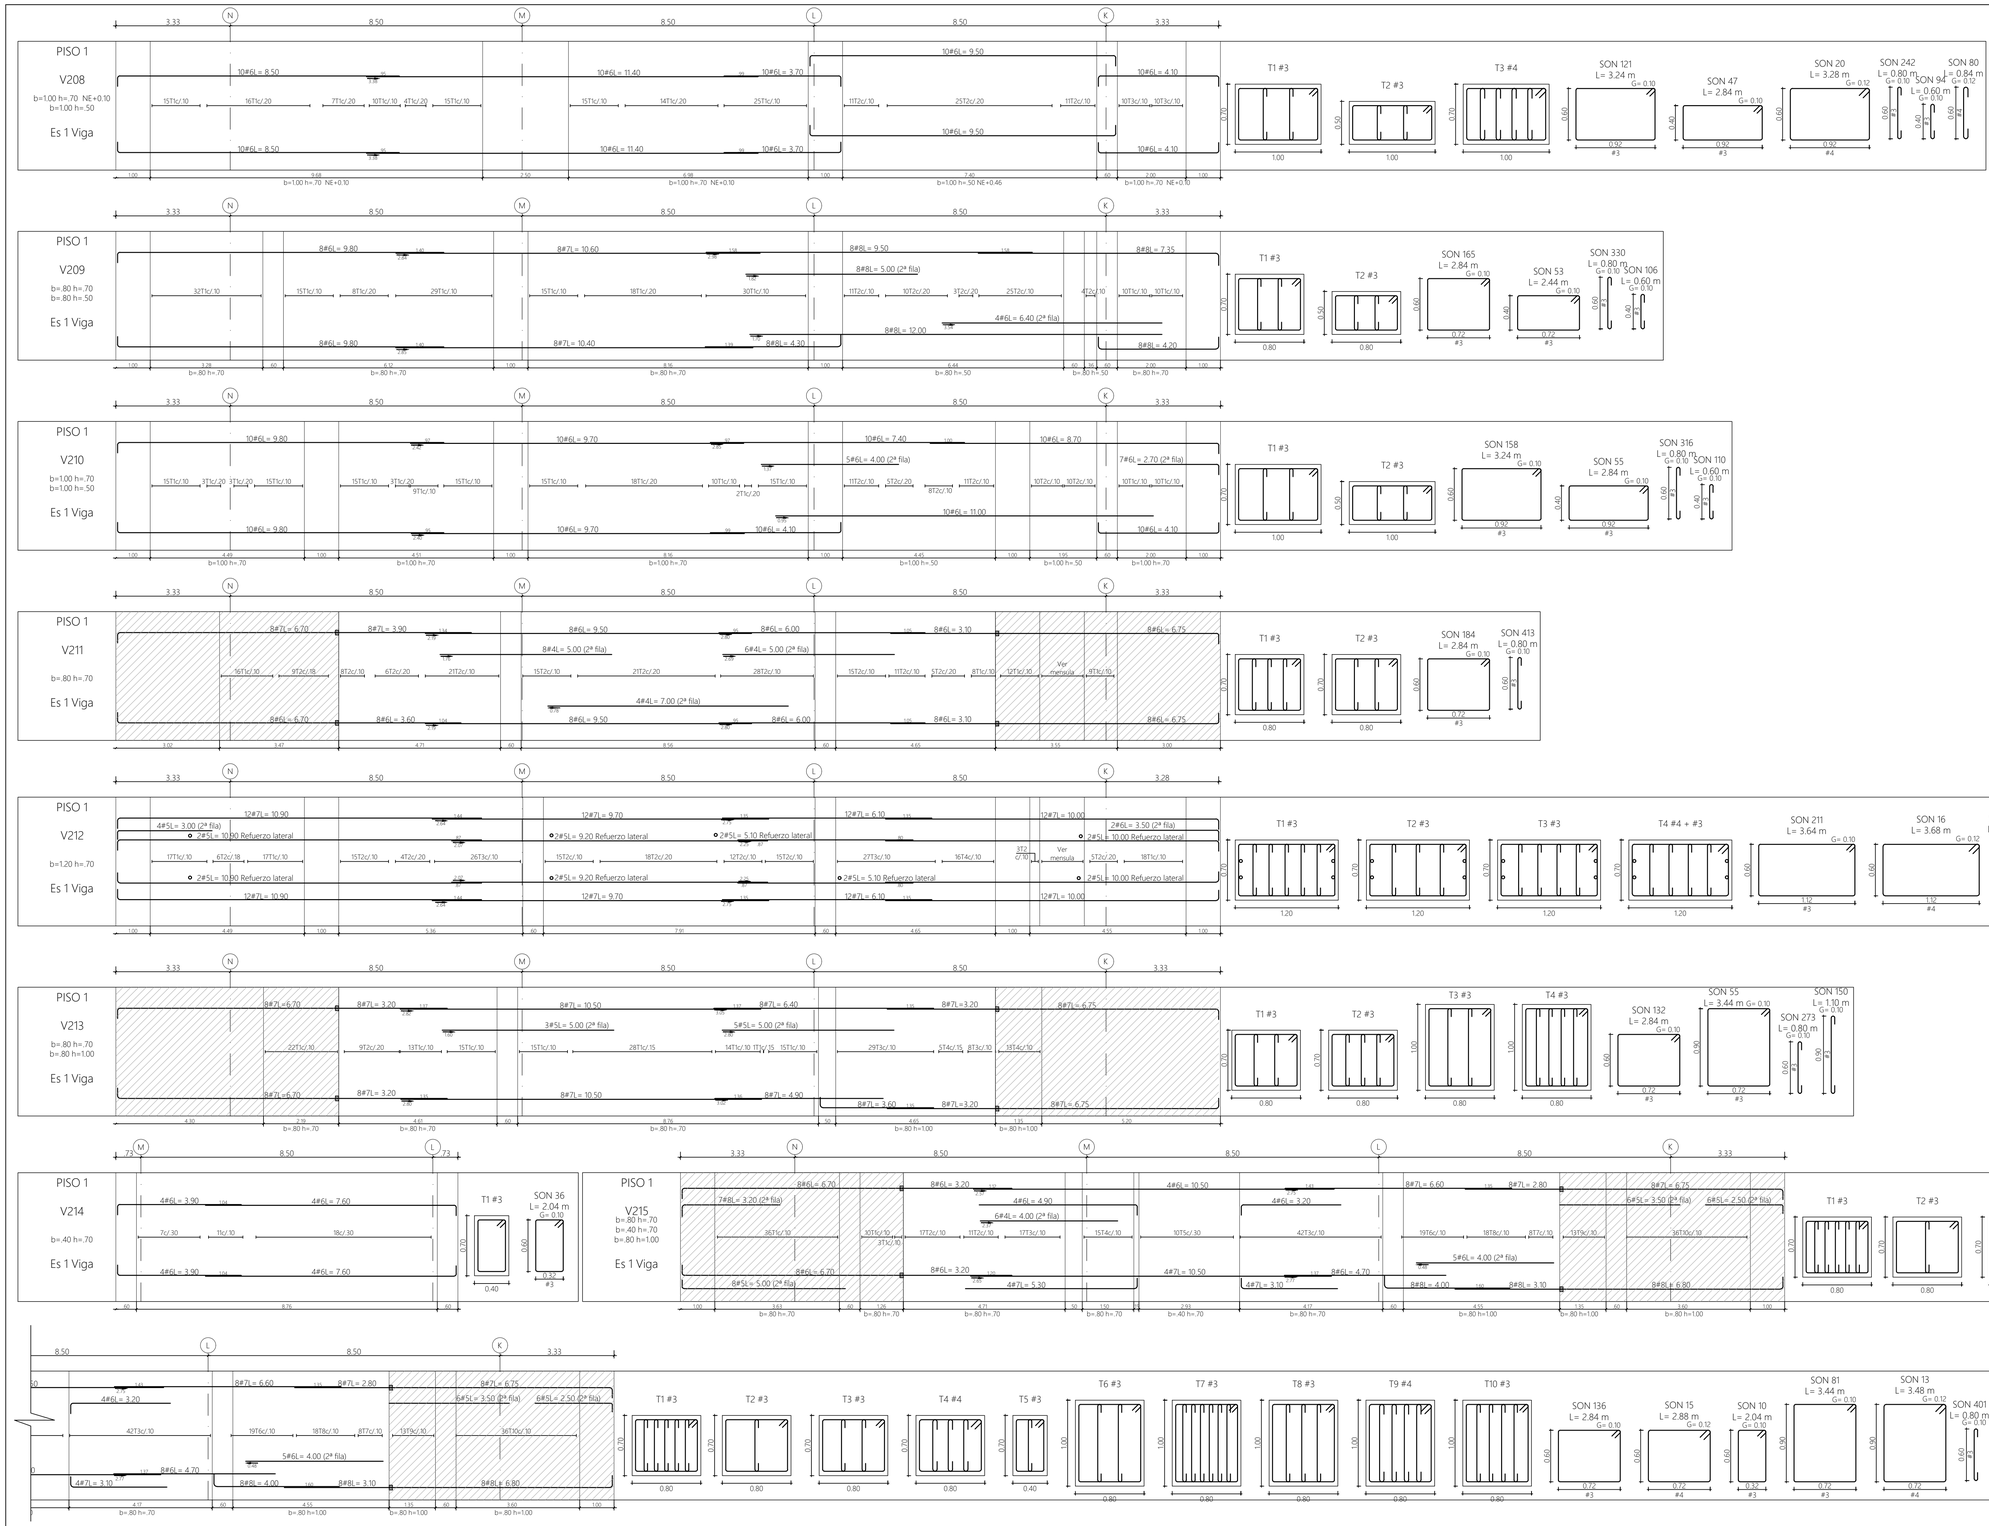


Indica seccion de viga fundida en Primera Etapa, prever conectores

Empalme mecánico tipo 2

Ver detalle de mensulas en plano CTIB_CNI_EST_515_DET_XXX

## DESPIECE DE VIGASDE PISO 1

Escala 1:75

CTIB

Campus de Ciencia, Tecnología e Innovación de Bogotá - Región

corferias — Generadores de Oportunidades y Progreso

Cámara de Comercio de Bogotá

BOGOTÁ Secretaría Distrital de Desarrollo Económico

**ARQUITECTO COORDINADOR**

EL EQUIPO MAZZANTI + Gensler

**DISEÑO ESTRUCTURAL**

CNI INGENIEROS

| DISEÑADOR | ING. NICOLÁS PARRA GARCÍA<br>MAT. 25202 62063 CND |
|---|---|

**INTERVENTORÍA**

GUTIÉRREZ DÍAZ S.A.S.
SUPERVISIÓN Y GESTIÓN DE PROYECTOS DE CONSTRUCCIÓN

| Director de Interventoria: | Ing. Jorge Iván Garcia Mancilla<br>Mat. 6320211 48063 QND |
|---|---|

| Versión | Emisión | Descripción |
|---|---|---|
| | | |
| AA | 15-06-2023 | Ingeniería básica |
| AB | 04-08-2023 | Anteproyecto |
| AC | 01-11-2023 | Anteproyecto V2 50% |
| AD | 15-12-2023 | Anteproyecto V2 100% |
| DD | 13-03-2024 | Entrega curaduría |
| EE | 10-05-2024 | Proyecto Final 100% |
| EF | 31-05-2024 | Respuesta Obs 100% |
| FF | 21-06-2024 | Entrega Final |
| 01 | 26-07-2024 | ENTREGA FINAL |

**PROYECTO:**

CAMPUS DE CIENCIA TECNOLOGÍA E INNOVACIÓN DE BOGOTA

MAT.: No. SDC-00052470

**FASE**

ENTREGA FINAL

**PROPÓSITO DE EMISIÓN**

| | | | |
|---|---|---|---|
| Curaduría | ☐ | Coordinación | ☐ |
| Revisión | ☐ | Construcción | ■ |
| Entrega Ciente | ■ | | |

**ZONIFICACIÓN**

| |
|---|
| Nivel 24 |
| Nivel 23 |
| Nivel 22 |
| Nivel 21 |
| Nivel 20 |
| Nivel 19 |
| Nivel 18 |
| Nivel 17 |
| Nivel 16 |
| Nivel 15 |
| Nivel 14 |
| Nivel 13 |
| Nivel 12 |
| Nivel 11 |
| Nivel 10 |
| Nivel 9 |
| Nivel 8 |
| Nivel 7 |
| Nivel 6 |
| Nivel 5 |
| Nivel 4 |
| Nivel 3 |
| Nivel 2 |
| Nivel 1 |
| Nivel S1 |
| Nivel S2 |

PROYECTO DETALLADO

APTO PARA CONSTRUCCIÓN (APC)

KEY PLAN

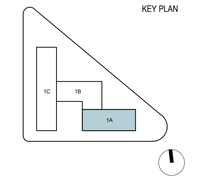


| Fecha: | 26-07-2024 |
|---|---|
| Escala: | As Indicated |

DESPIECES DE VIGAS DE PISO 1

CTIB_CNI_EST_416_DSP_XXX_01