


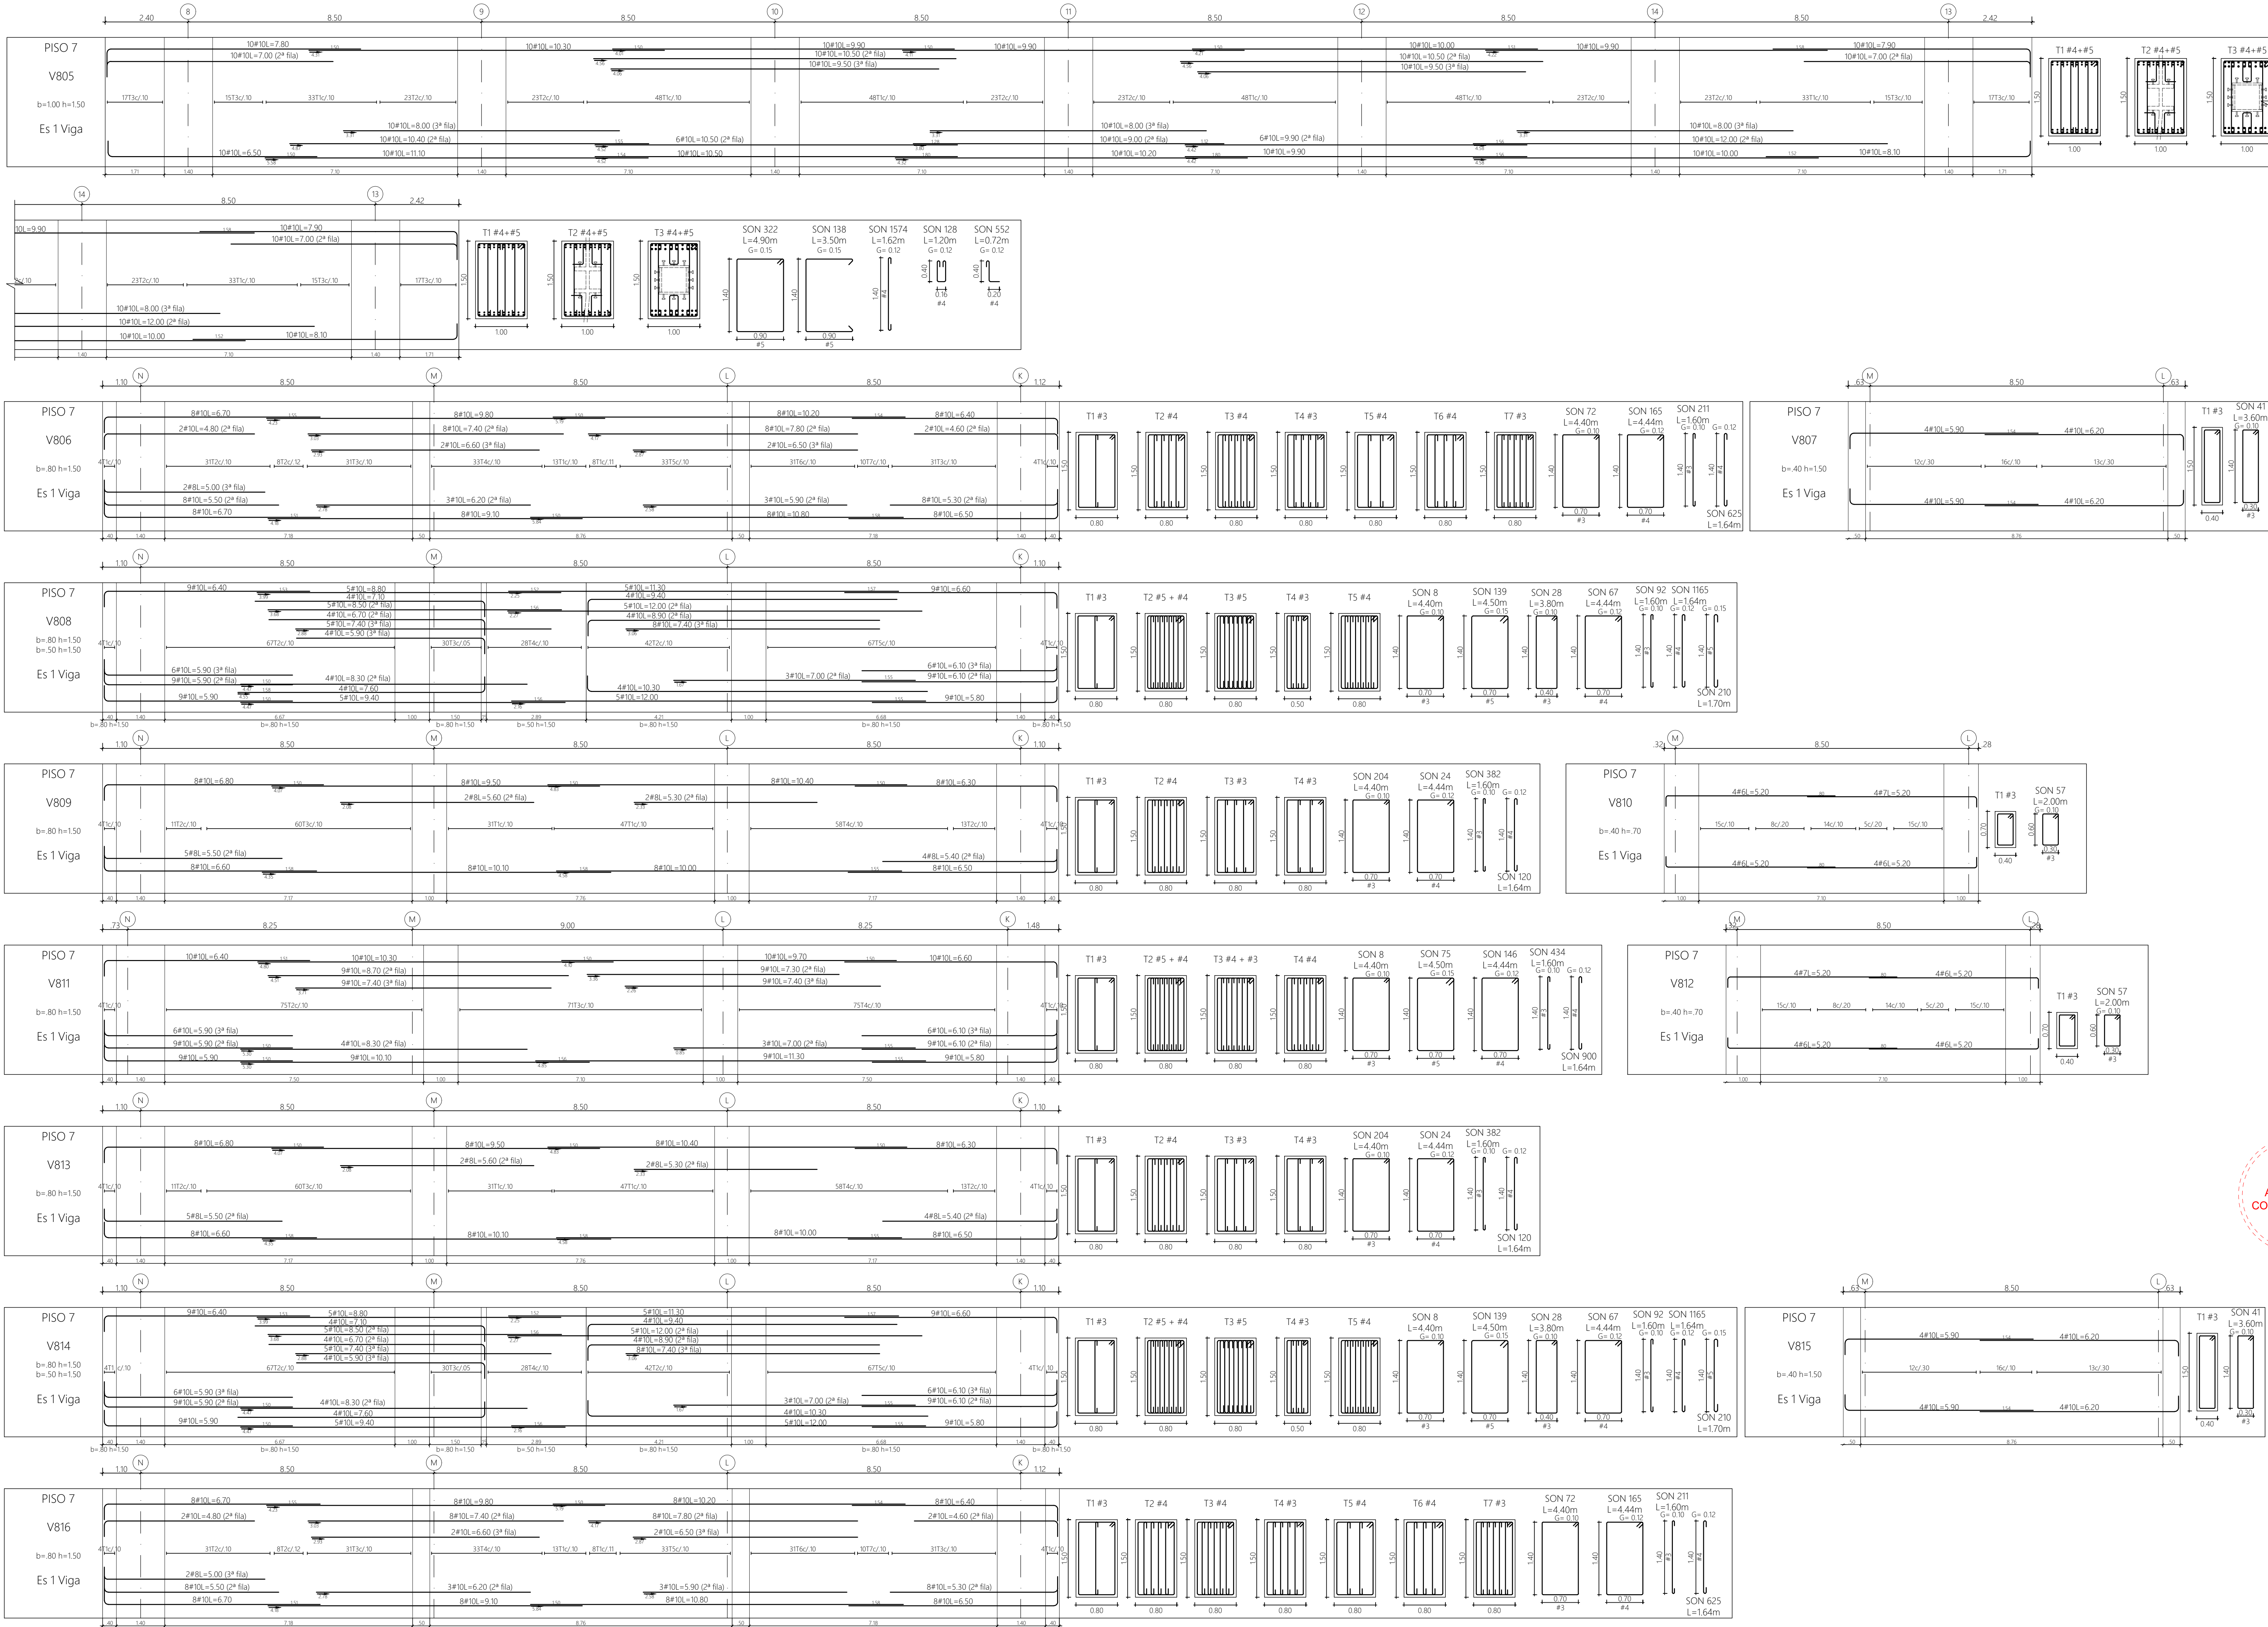

DESPIECES DE VIGAS DE PISO 7
escala 1:75

CTIB

Campus de Ciencia, Tecnología e Innovación de Bogotá - Región

corferias

Generadores de Oportunidades y Progreso

Cámara de Comercio de Bogotá

Secretaría Distrital de Desarrollo Económico

BOGOTÁ

Secretaría Distrital de Desarrollo Económico

ARQUITECTO COORDINADOR

EL EQUIPO MAZZANTI + Gensler

DISÑO ESTRUCTURAL

CNI

CONSTRUCCIÓN

ING. NICOLÁS PARRA GARCÍA

MAT. 232021 62063 CND

DISEÑADOR

ING. NICOLÁS PARRA GARCÍA

MAT. 232021 62063 CND

INTERVENTORIA

GUTIERREZ DÍAZ S.A.S.

Supervisión y Asesoría Técnica de Construcción

Director de Interventoría:

Ing. Jorge Iván García Mancilla

MAT. 632021 148063 QND

Versión

Emisión

Descripción

AA

15-06-2023

Ingeniería básica

AB

04-08-2023

Anteproyecto

AC

01-11-2023

Anteproyecto V2 50%

AD

15-12-2023

Anteproyecto V2 100%

DD

13-03-2024

Entrega curaduría

EE

10-05-2024

Proyecto Final 100%

EF

31-05-2024

Respuesta Obs 100%

FF

21-06-2024

Entrega Final

01

28-07-2024

ENTREGA FINAL

PROYECTO:

CAMPUS DE CIENCIA TECNOLOGÍA E INNOVACIÓN DE BOGOTÁ

MAT. No. 502-0025470

FASE

ENTREGA FINAL

PROPÓSITO DE EMISIÓN

Curaduría

Revisión

Entrega Cliente

Coordinación

Construcción

ZONIFICACIÓN

Nivel 24

Nivel 23

Nivel 22

Nivel 21

Nivel 20

Nivel 19

Nivel 18

Nivel 17

Nivel 16

Nivel 15

Nivel 14

Nivel 13

Nivel 12

Nivel 11

Nivel 10

Nivel 9

Nivel 8

Nivel 7

Nivel 6

Nivel 5

Nivel 4

Nivel 3

Nivel 2

Nivel 1

Nivel 0

Nivel B1

Nivel B2

KEY PLAN

1C

1B

1A

Fecha:

28-07-2024

Escala:

As Indicated

DESPIECES DE VIGAS DE PISO 7

CTIB_CNI_EST_428_DSP_XXX_01

PROYECTO DETALLADO
APTO PARA CONSTRUCCIÓN (APC)