



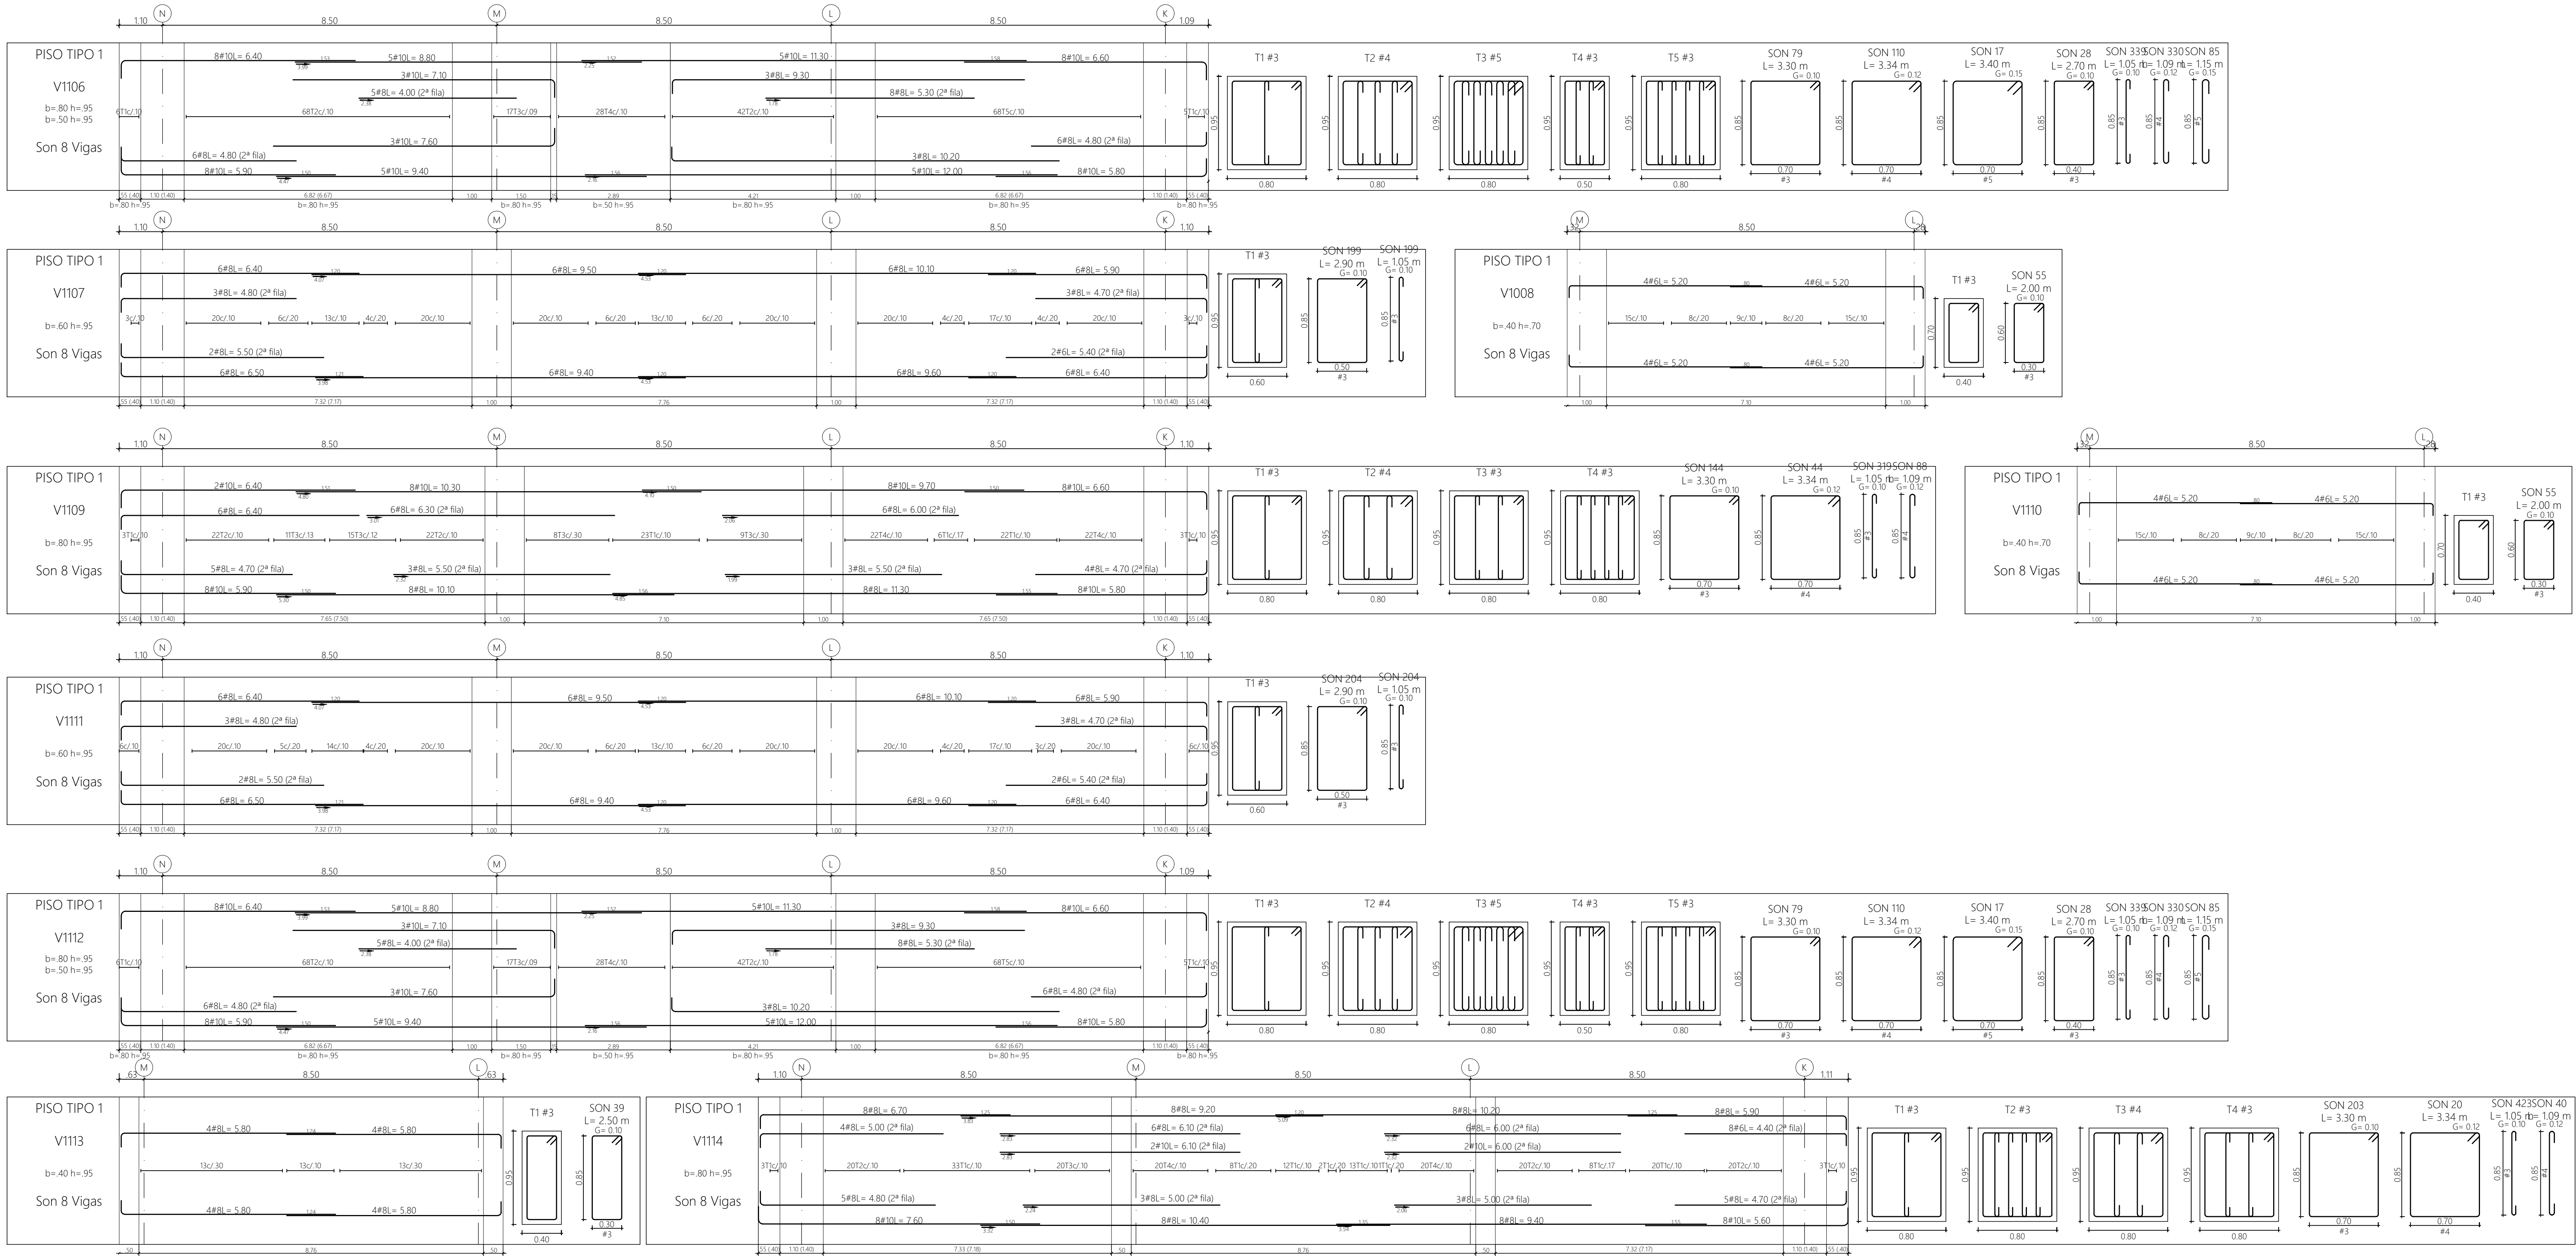

DESPIECES DE VIGAS DE PISO TIPO 1 (NIVEL 10 A 17)
escala 1:75

NOTAS IMPORTANTES:
1. Los valores entre parentesis aplican para el nivel 10.
2. El primer estubo debe quedar a 5cm de la cara de la columna o el muro.

ZONIFICACION	
Nivel 24	
Nivel 23	
Nivel 22	
Nivel 21	
Nivel 20	
Nivel 19	
Nivel 18	
Nivel 17	
Nivel 16	
Nivel 15	
Nivel 14	
Nivel 13	
Nivel 12	
Nivel 11	
Nivel 10	
Nivel 9	
Nivel 8	
Nivel 7	
Nivel 6	
Nivel 5	
Nivel 4	
Nivel 3	
Nivel 2	
Nivel 1	
Nivel B1	
Nivel B2	

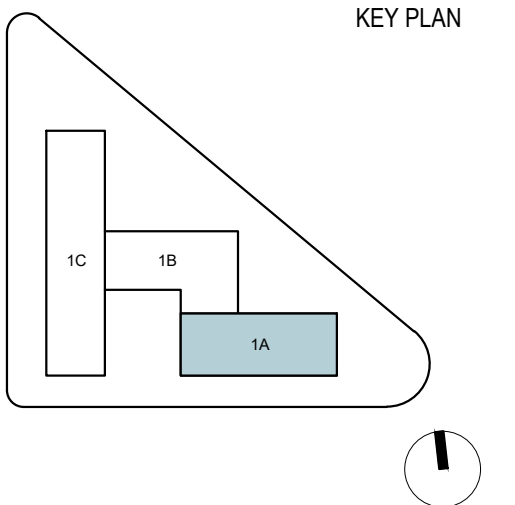

Fecha: 26-07-2024

Escala: As Indicated

DESPIECES DE VIGAS PISO TIPO 1
(NIVEL 10 A 17)
CTIB_CNI_EST_434_DSP_XXX_01