




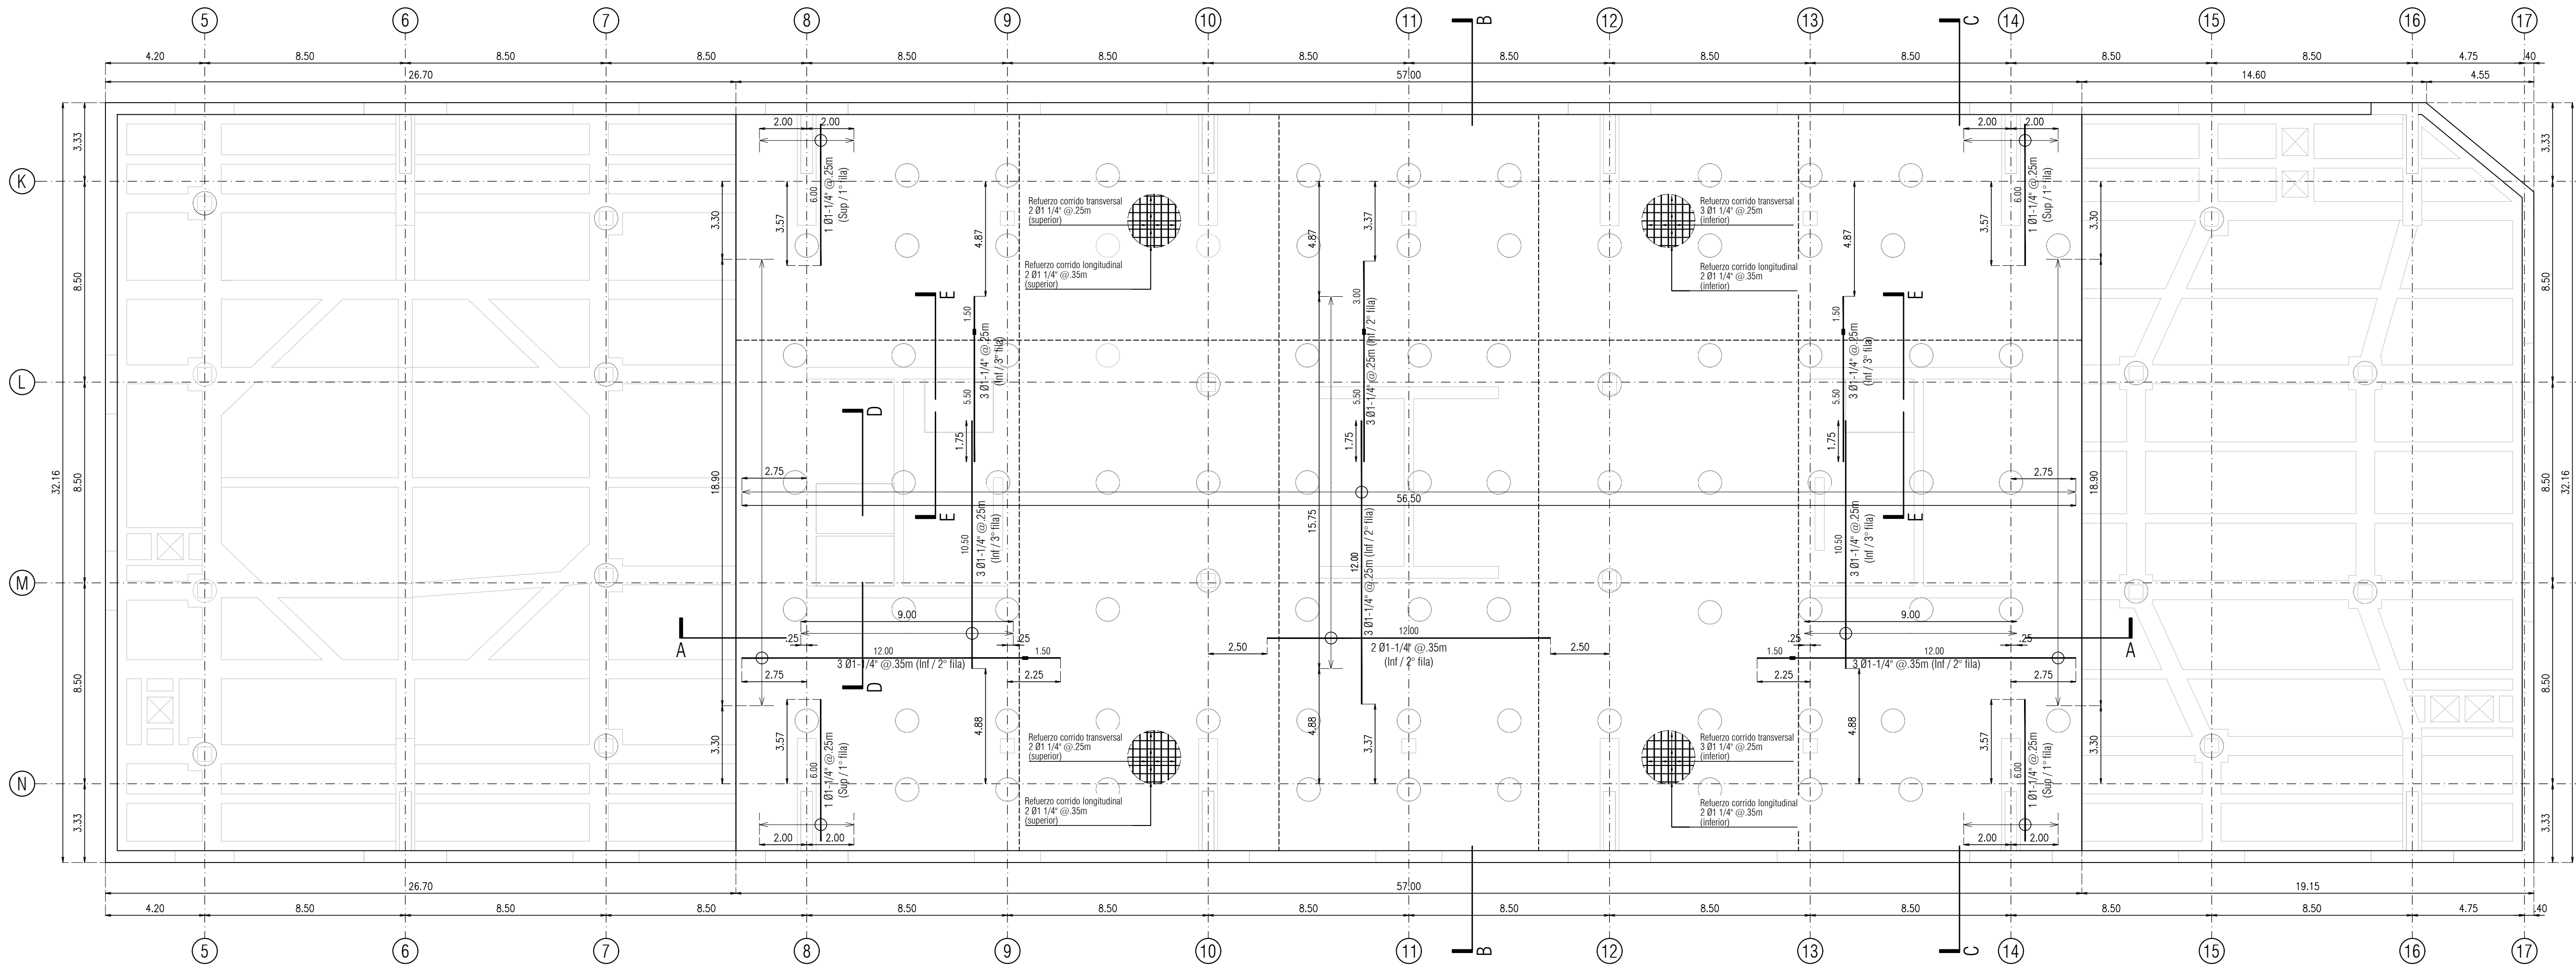


REFUERZO ADICIONAL
escala 1:150

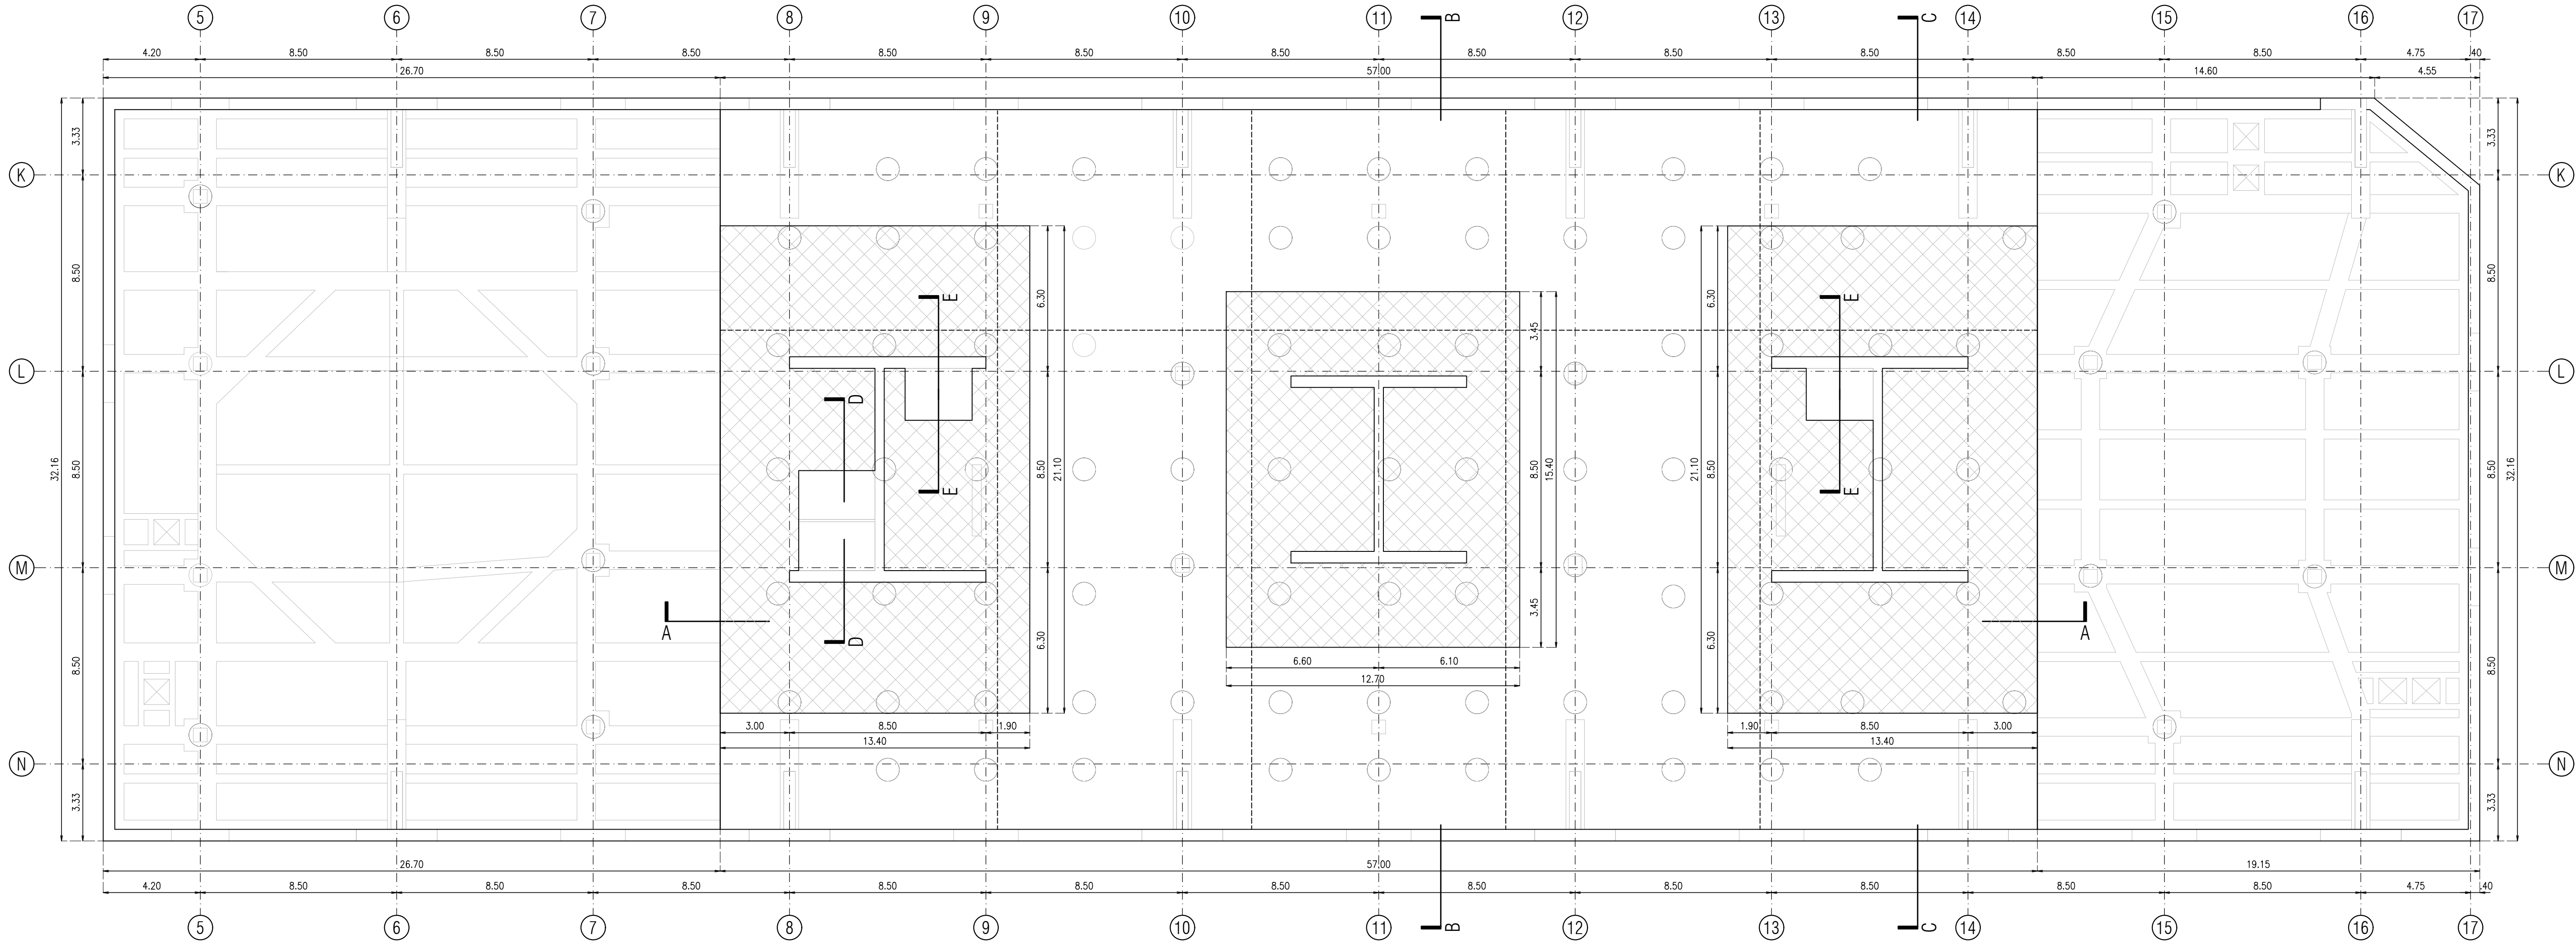

REFUERZO A CORTANTE
escala 1:150

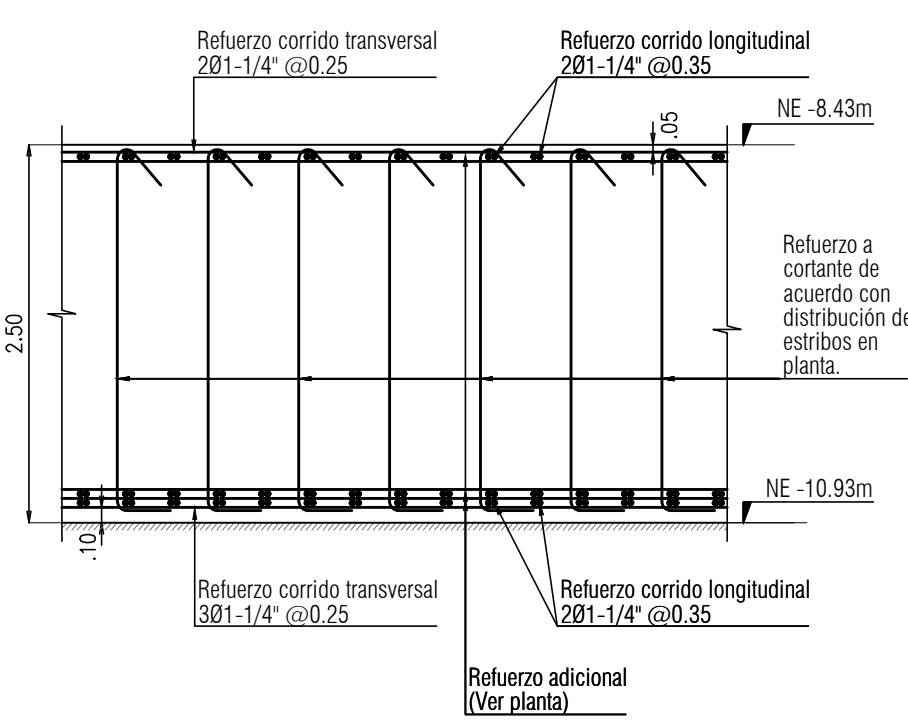

CORTE TÍPICO LOSA h=2.50m
escala 1:50

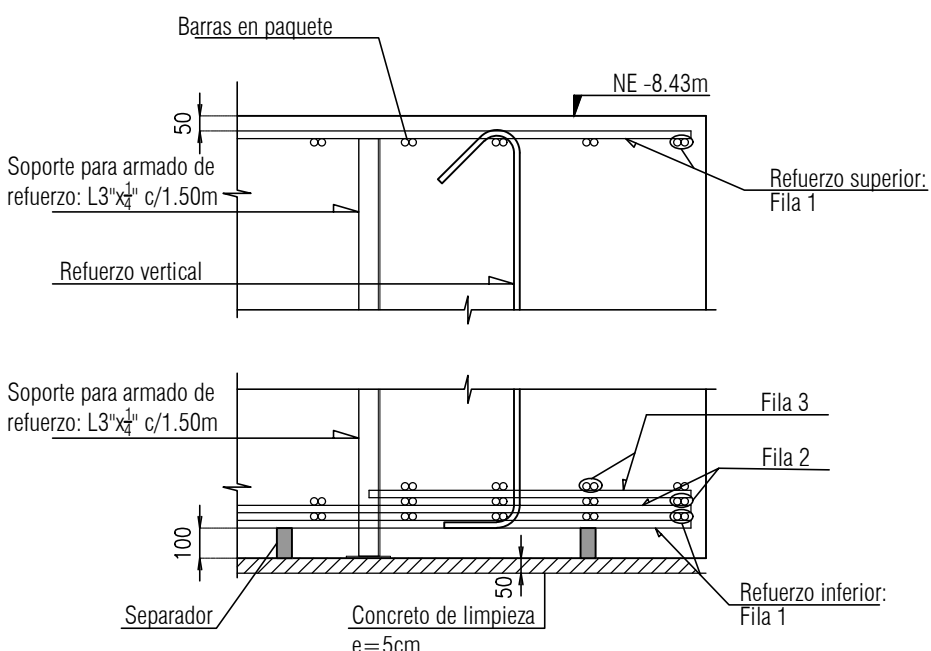

DETALLE TÍPICO ARMADO REFUERZO
escala 1:25

- Notas y Convenciones:
- Ver cortes losa de subpresión en plano EST-501.
 - Los empalmes mecánicos deben cumplir con C.12.14.3.2 de NSR-10.
 - No se requiere separación libre entre filas de refuerzo.
 - Los ángulos de soporte del refuerzo son recomendados. El constructor es responsable correcta colocación del refuerzo y de su estabilidad durante la fundida.
- Zonas de placa achurada, requiere estribos 2Ø1" @ 50m en dirección longitudinal y 2Ø1" @ 35m en dirección transversal.
- Zonas de placa sin achurada, requiere estribos 1Ø1" @ 75m en dirección longitudinal y 1Ø1" @ 70m en dirección transversal.
- ⊕ Franja de refuerzo adicional
- Empalme mecánico tipo 2