




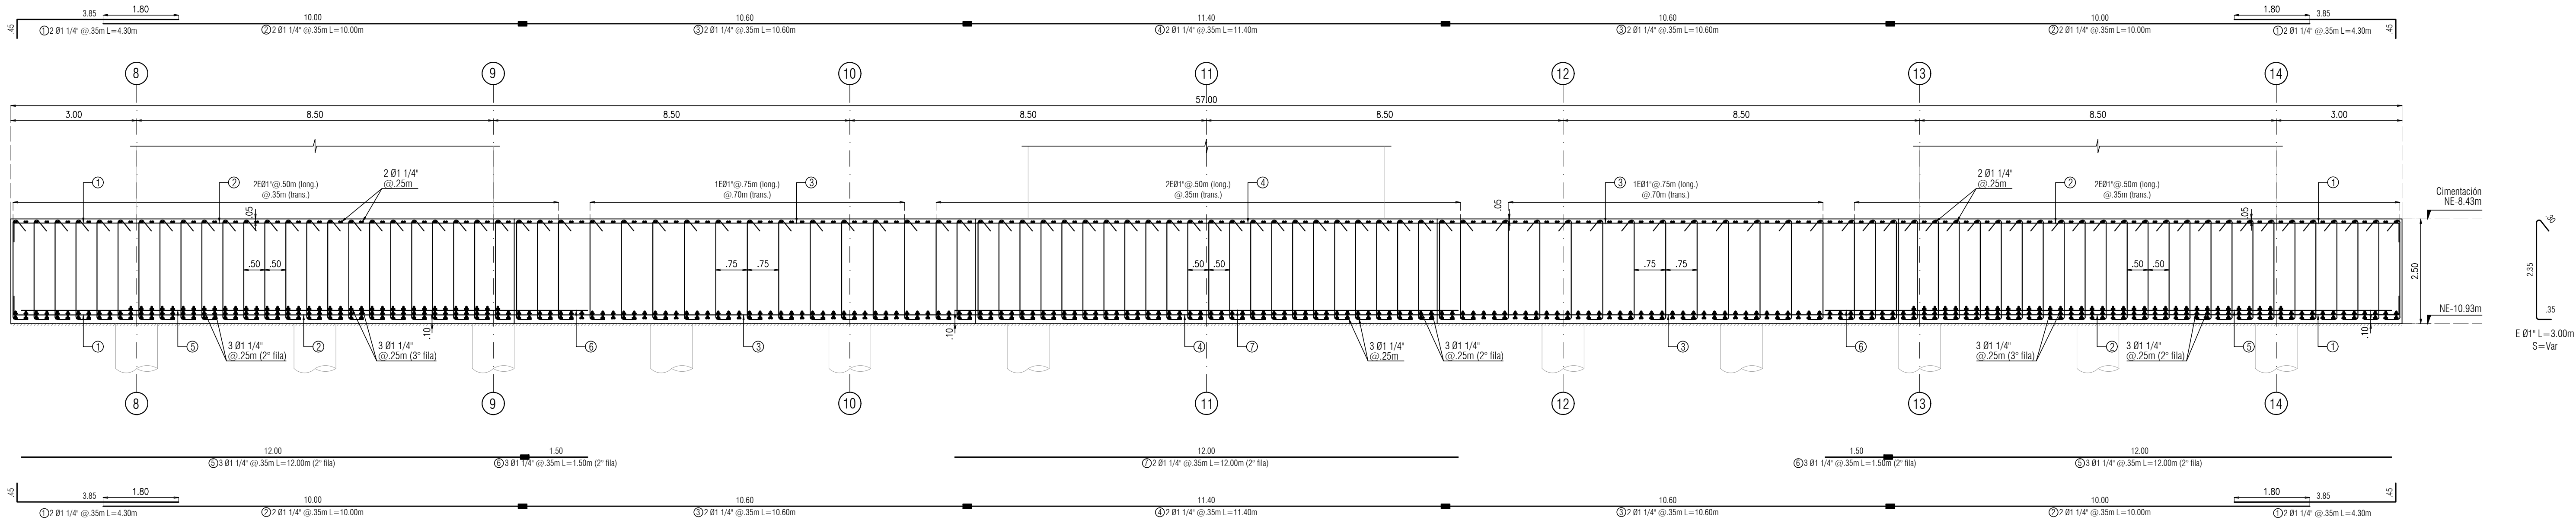


CORTE A-A
escala 1:75

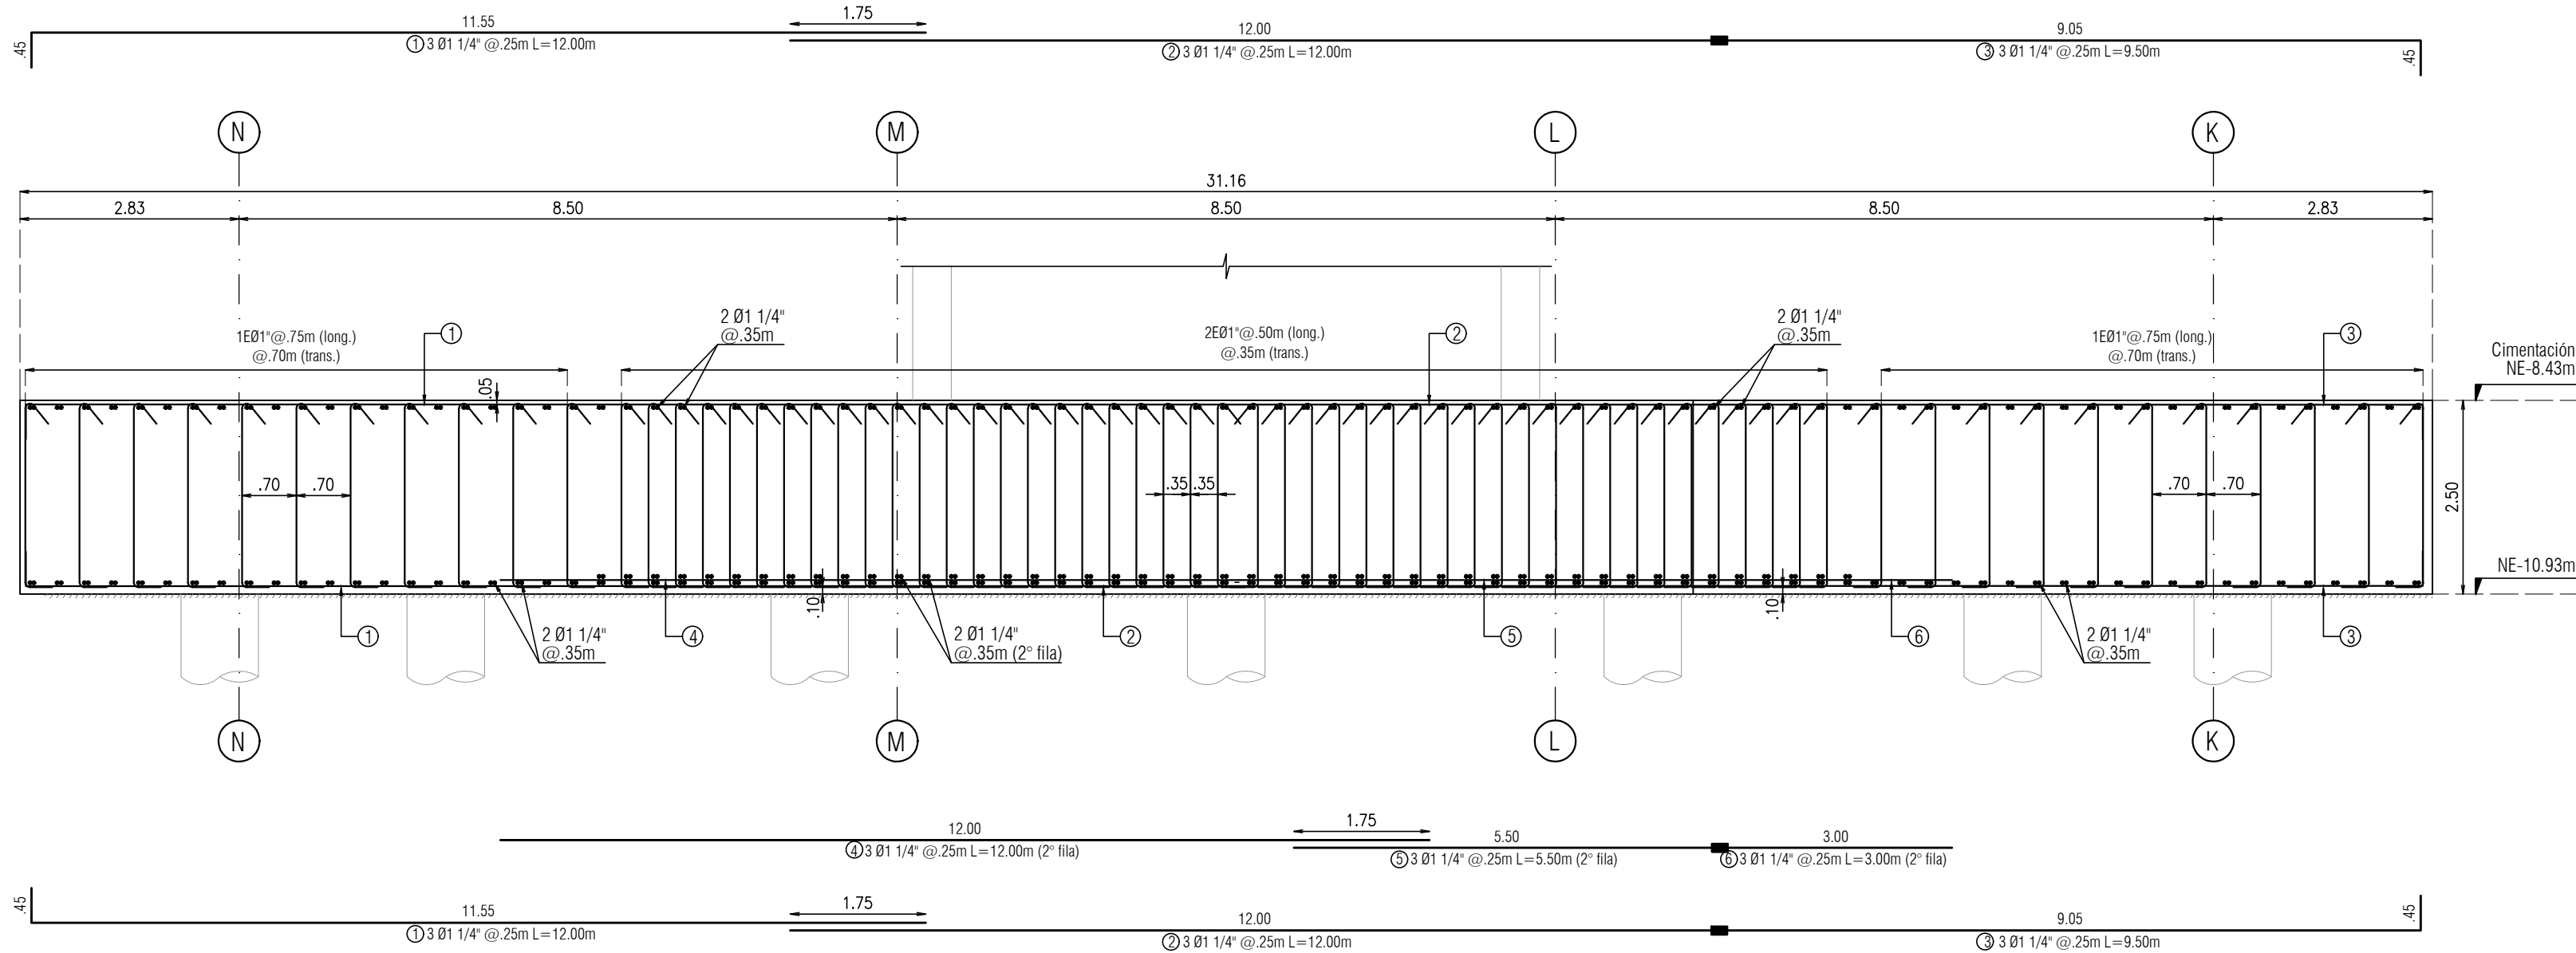


CORTE B-B
escala 1:75

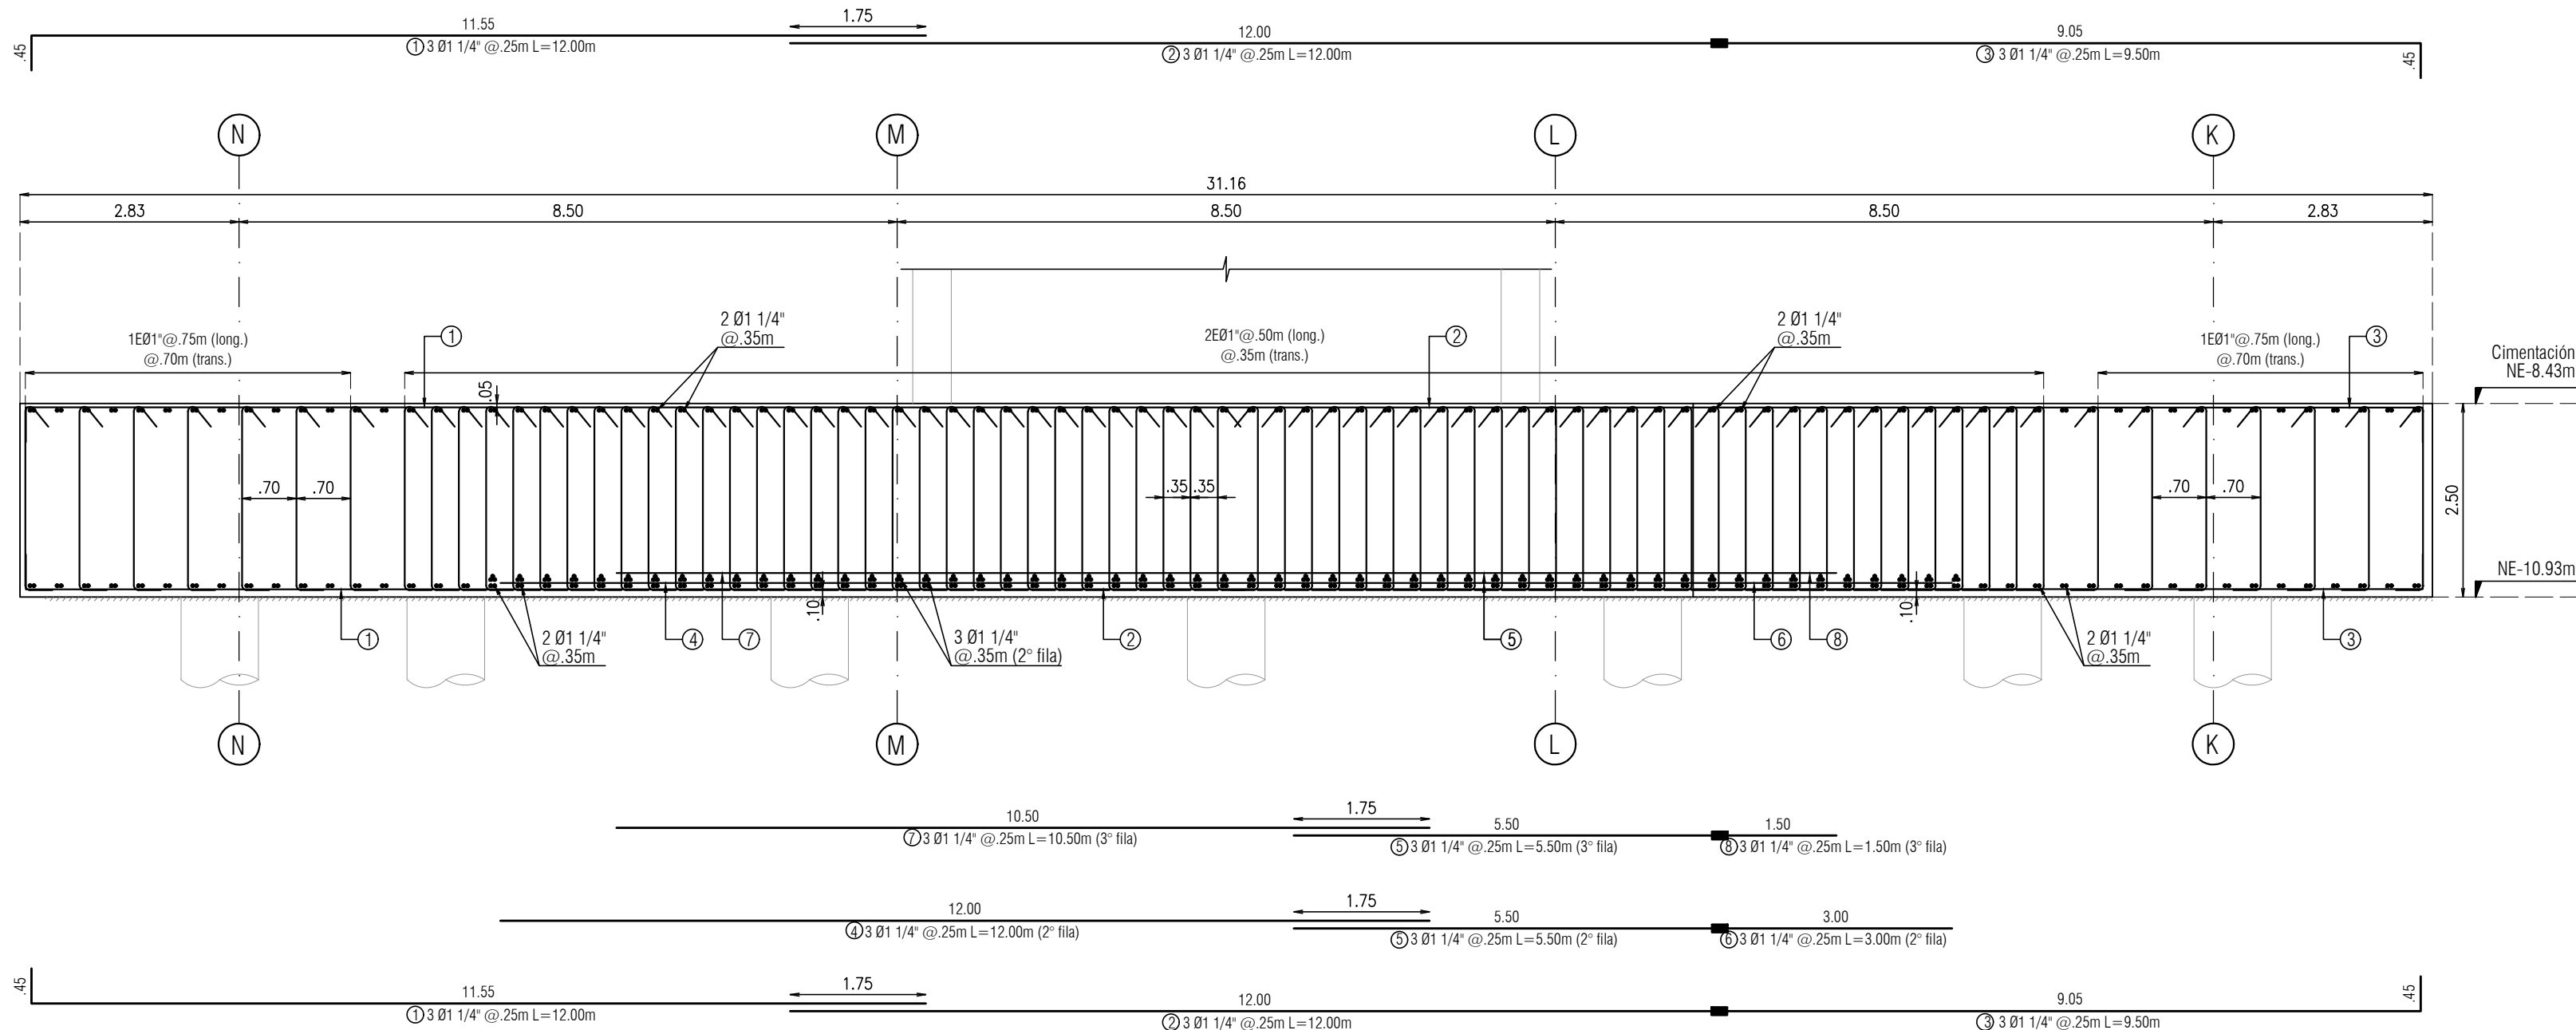


CORTE C-C
escala 1:75

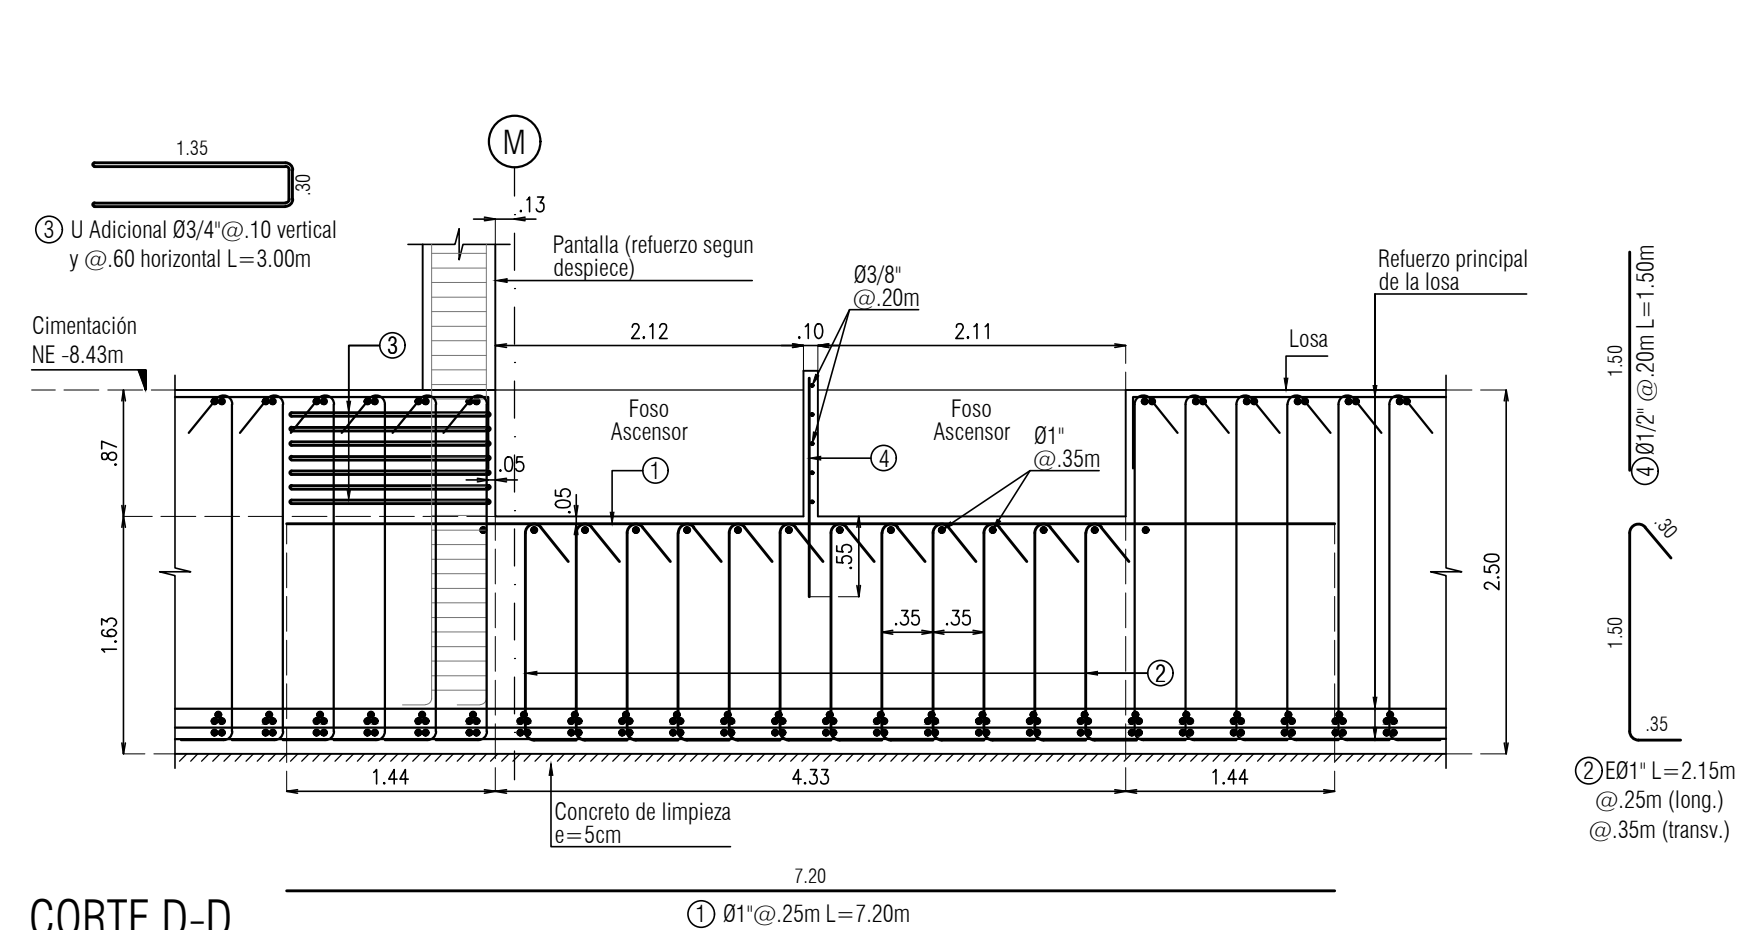


CORTE D-D
escala 1:50

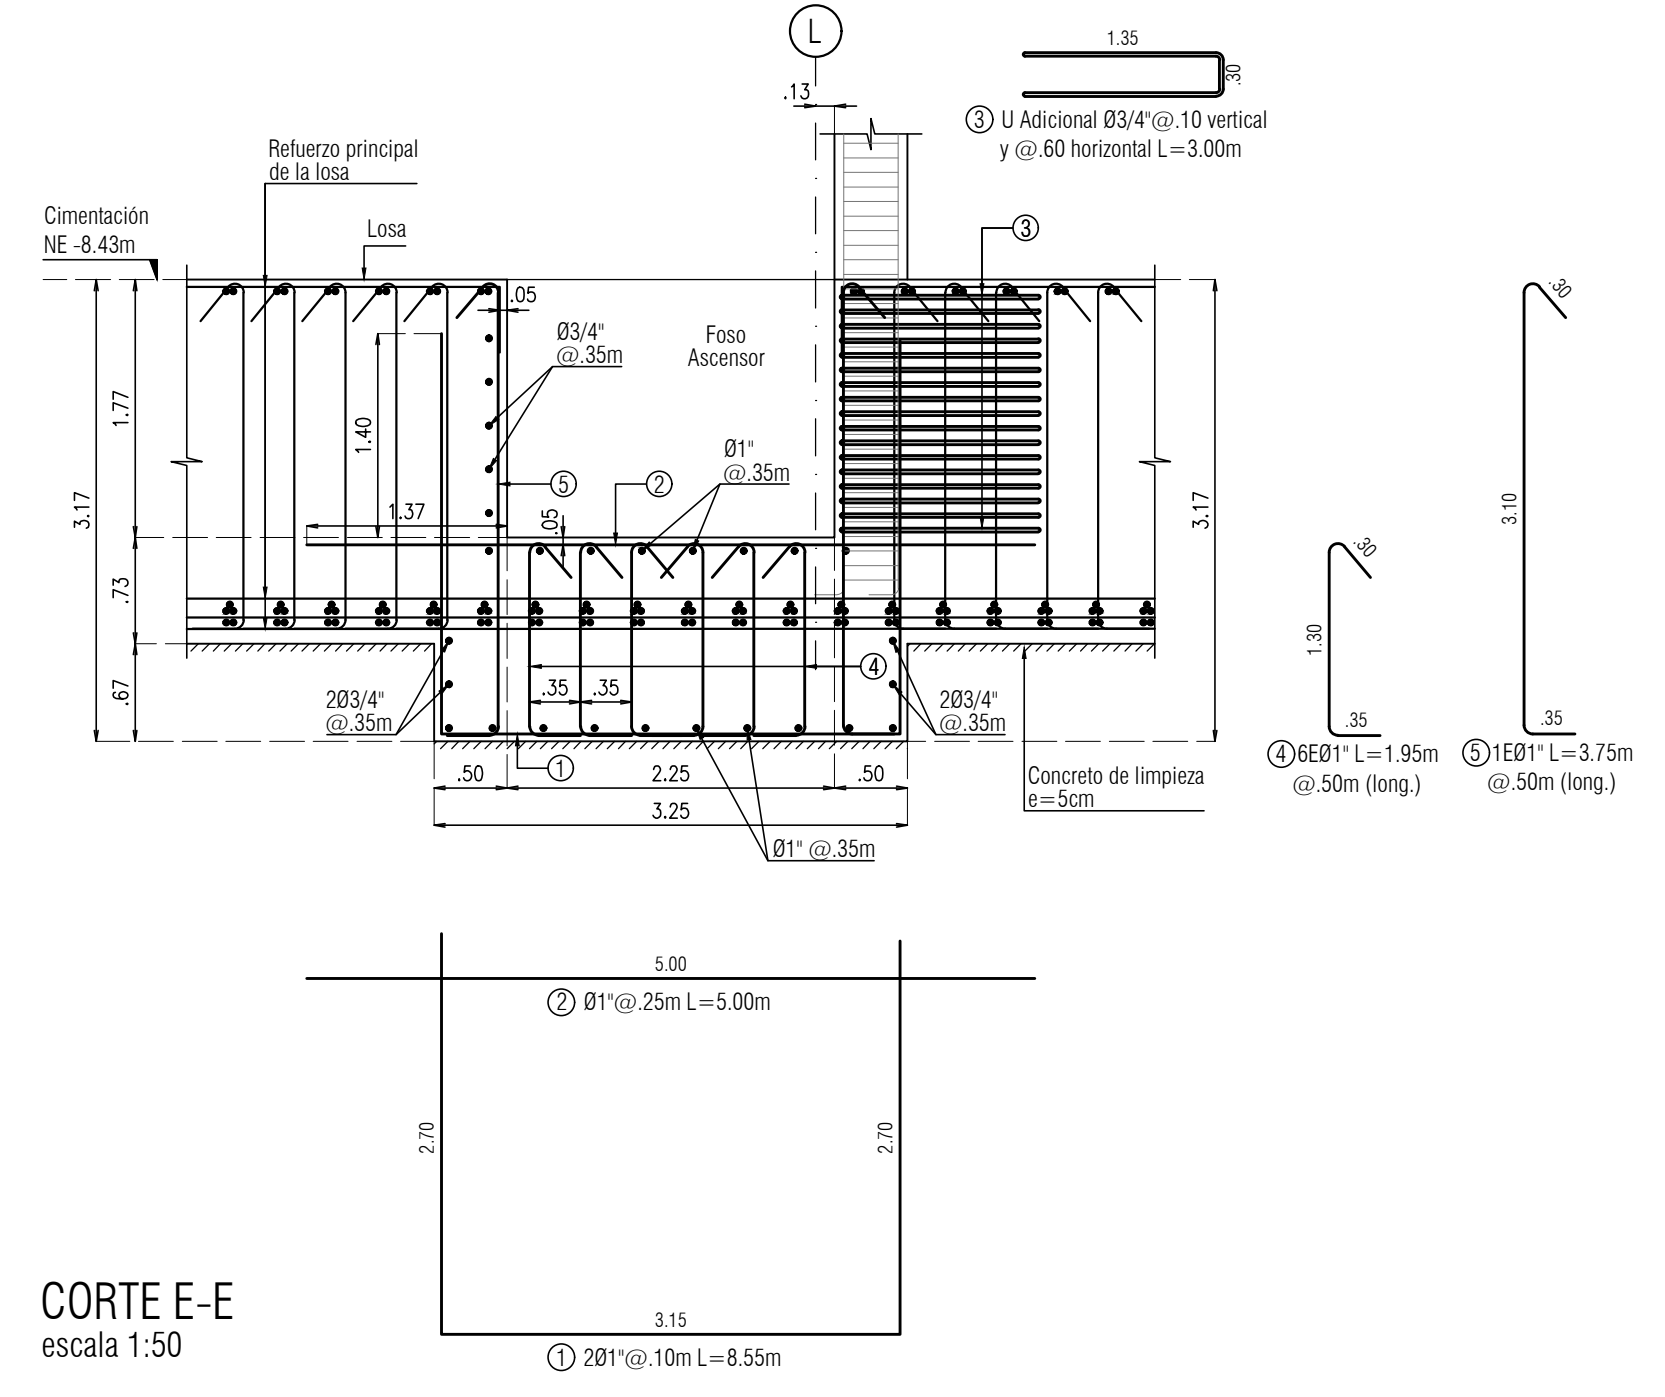

CORTE E-E
escala 1:50

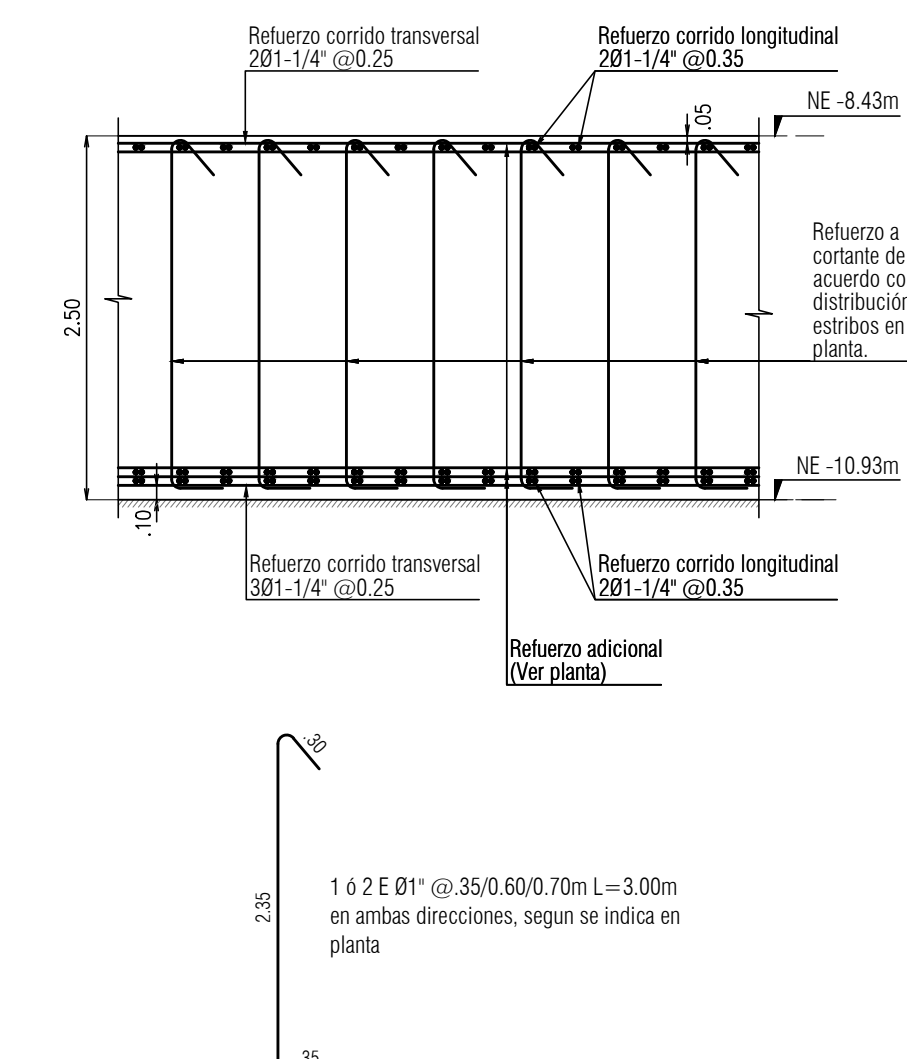

CORTE TÍPICO LOSA h=2.50m
escala 1:50

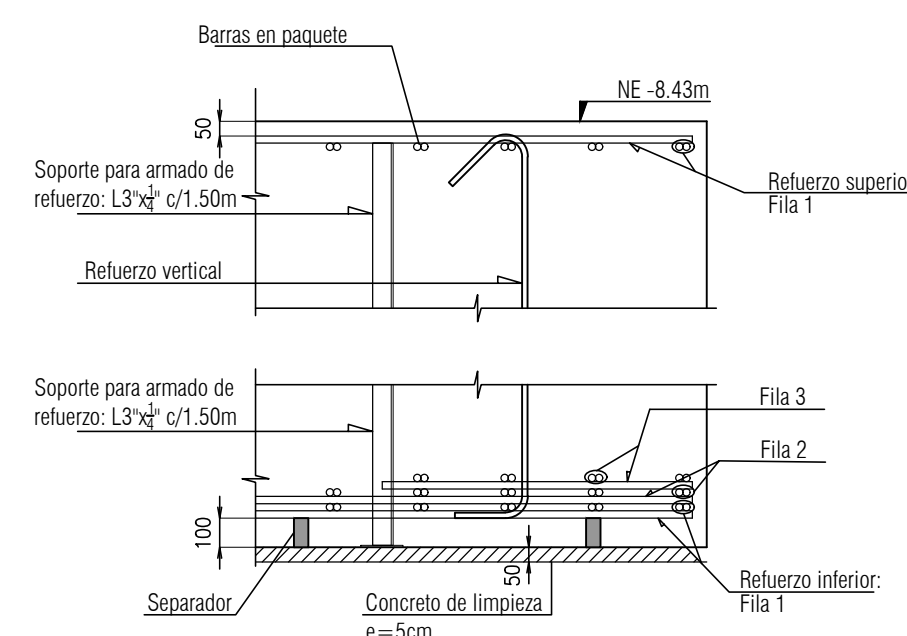

DETALLE TÍPICO ARMADO REFUERZO
escala 1:25

Notas y Convenciones:
- Ver cortes losa de subpresión en plano EST-501.
- Los empalmes mecánicos deben cumplir con C.12.14.3.2 de NSR-10.
- No se requiere separación libre entre filas de refuerzo.
- Los ángulos de soporte del refuerzo son recomendados. El constructor es responsable de la correcta colocación del refuerzo y de su estabilidad durante la fundida.

■ Empalme mecánico tipo 2
— Junta constructiva propuesta

CTIB
Campus de Ciencia, Tecnología e
Innovación de Bogotá - Región

ARQUITECTO COORDINADOR
ELEQUIPO MAZZANTI + Gensler

DISEÑO ESTRUCTURAL

DISEÑADOR
ING. NICOLÁS PARRA GARCÍA
MAT. 630521148033 QND

INTERVENTORIA

Director de Interventoría:
Ing. Jorge Iván García Mancilla
Mat. 630521148033 QND

Versión	Emisión	Descripción
AA	15-06-2023	Ingeniería básica
AB	04-08-2023	Anteproyecto
AC	01-11-2023	Anteproyecto V2 50%
AD	15-12-2023	Anteproyecto V2 100%
DD	13-03-2024	Entrega curaduría
EE	10-05-2024	Proyecto Final 100%
EF	31-05-2024	Respuesta Obs 100%
FF	21-06-2024	Entrega Final
01	26-07-2024	ENTREGA FINAL

PROYECTO:
CAMPUS DE CIENCIA TECNOLOGÍA E
INNOVACIÓN DE BOGOTÁ
MAT. No. 900-00252470

FASE
ENTREGA FINAL

PROPOSITO DE EMISION
Curaduría ☐ Coordinación ☐
Revisión ☐ Construcción ☒
Entrega Cliente ☒

ZONIFICACIÓN

Nivel	Altura
Nivel 04	10.00
Nivel 03	9.00
Nivel 02	8.00
Nivel 01	7.00
Nivel 00	6.00
Nivel -01	5.00
Nivel -02	4.00
Nivel -03	3.00
Nivel -04	2.00
Nivel -05	1.00
Nivel -06	0.00
Nivel -07	-1.00
Nivel -08	-2.00
Nivel -09	-3.00
Nivel -402	-396.00
Nivel -403	-39