




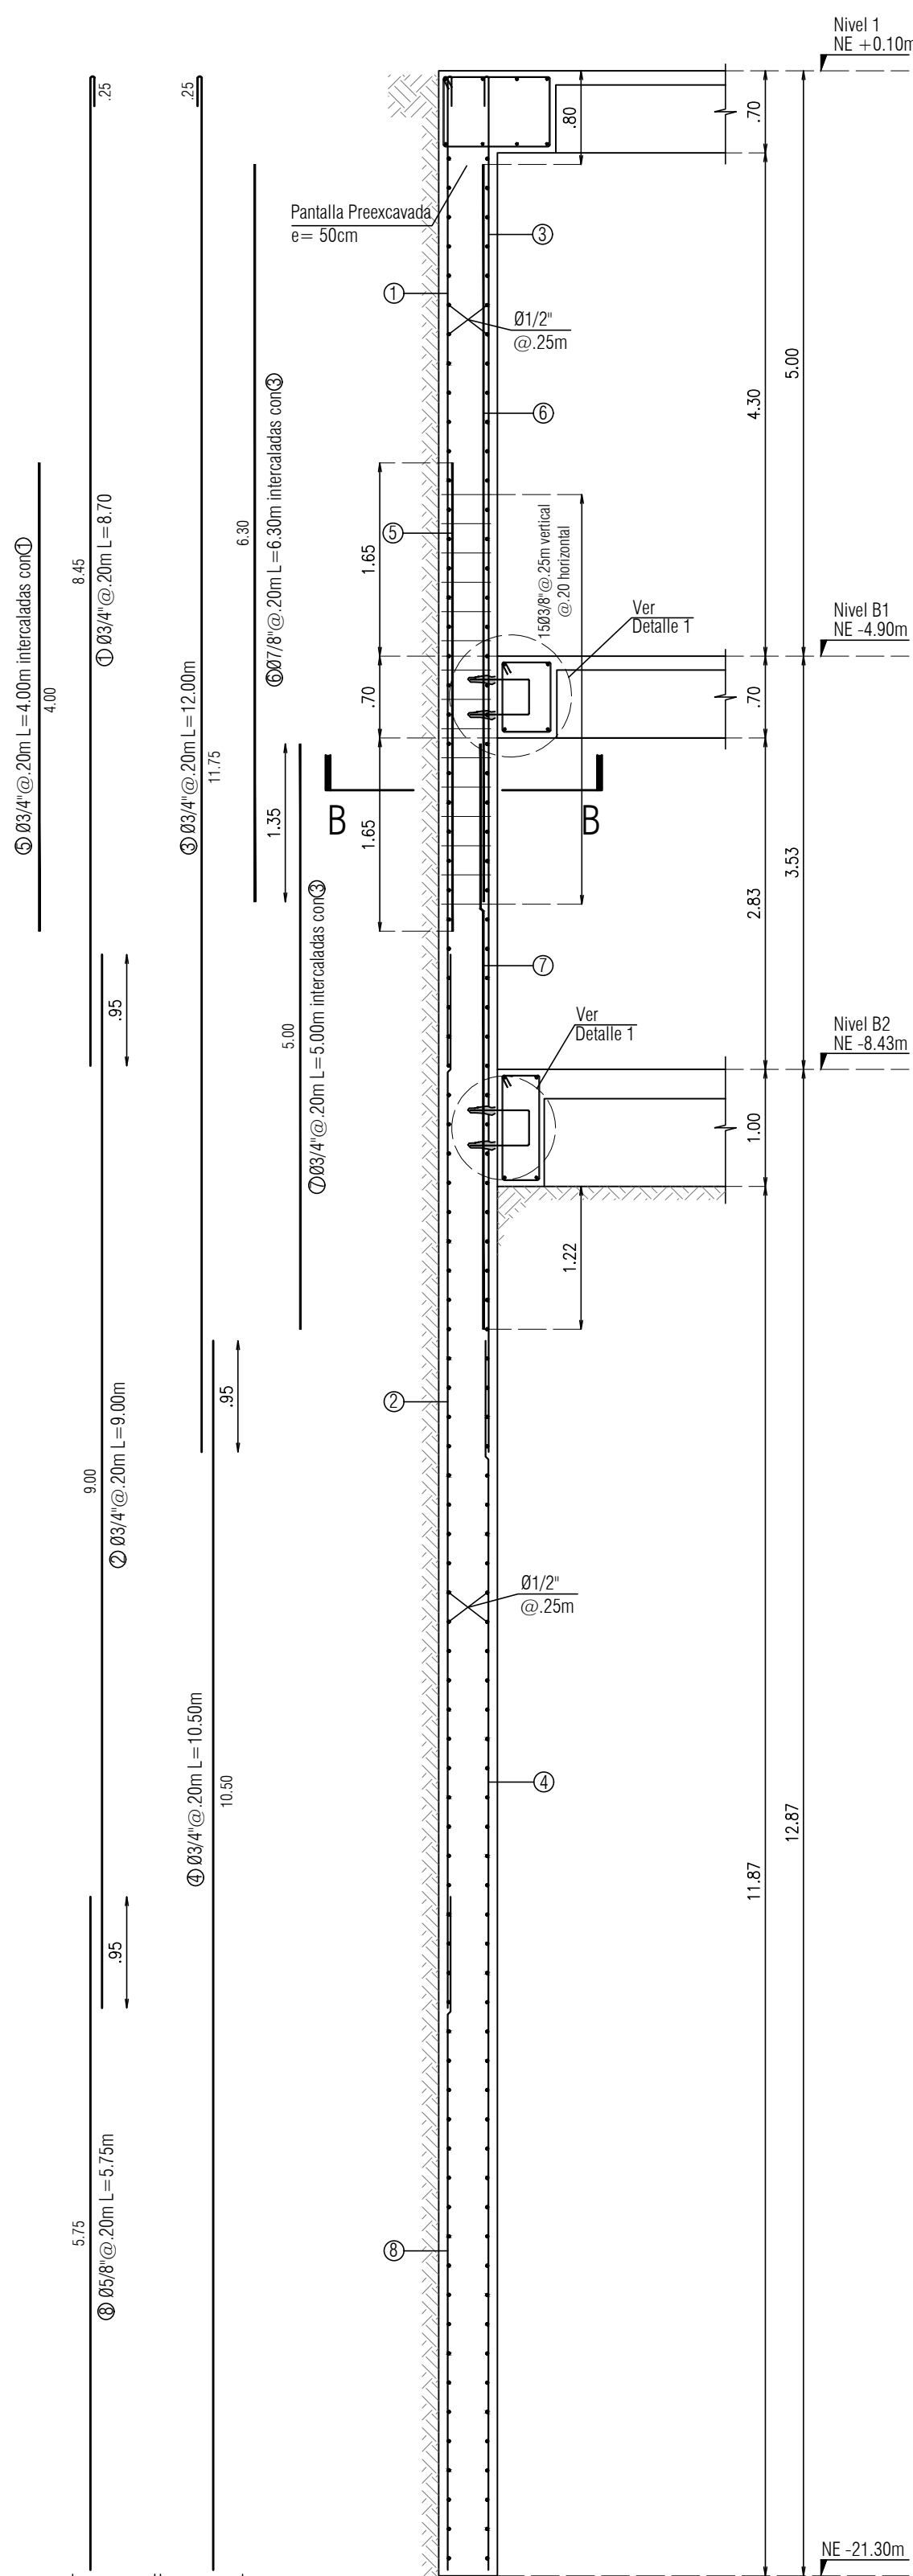


PANTALLA PREEXCAVADA PP3
escala 1:50

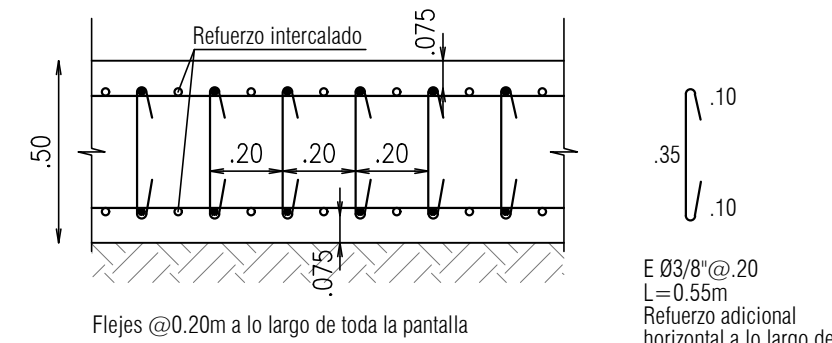


CORTE B-B
REFUERZO HORIZONTAL
PANTALLA PREEXCAVADA PP2 Y PP3
escala 1:20

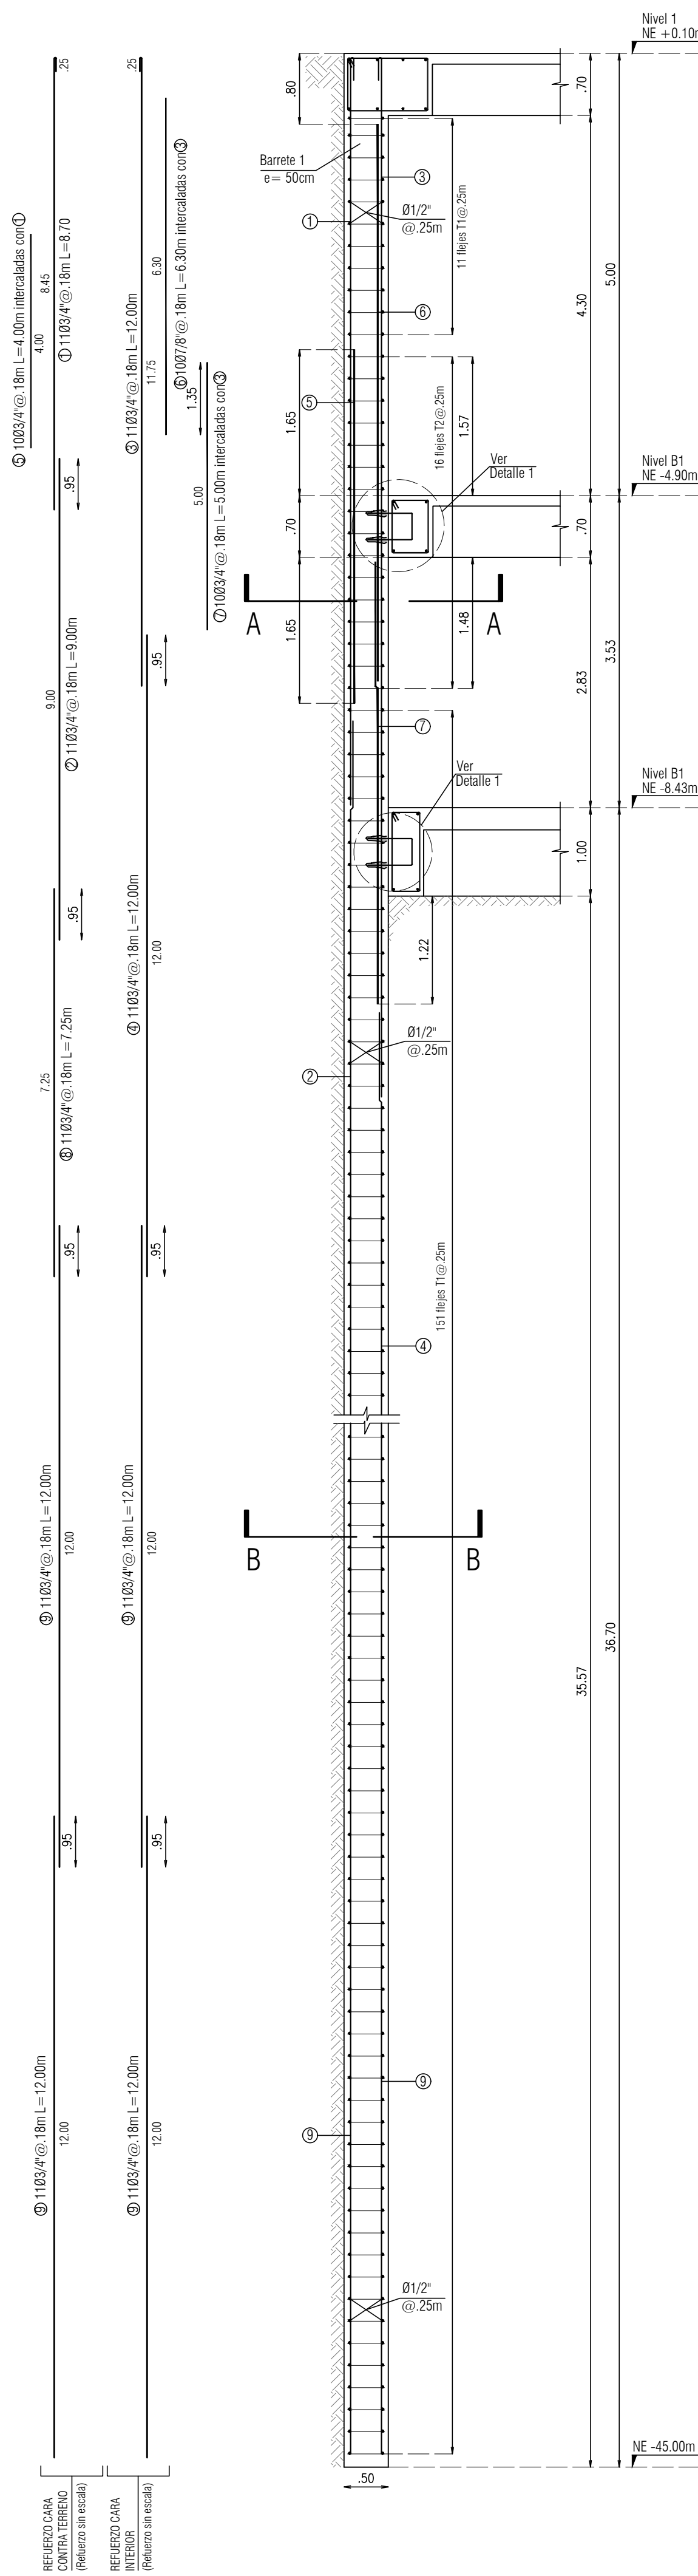


BARRETE BR1
escala 1:50

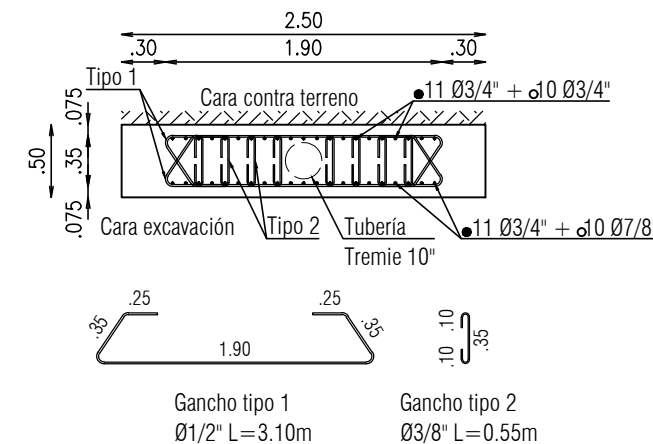


CORTE A-A - BR1
DISTRIBUCION FLEJES - T2
escala 1:50

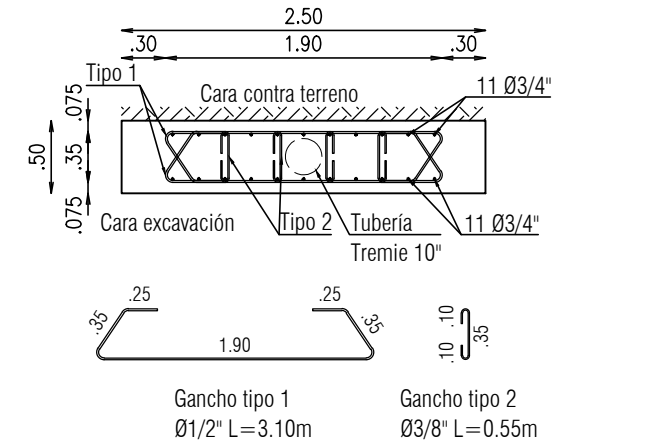


CORTE B-B - BR1
DISTRIBUCION FLEJES - T1
escala 1:50

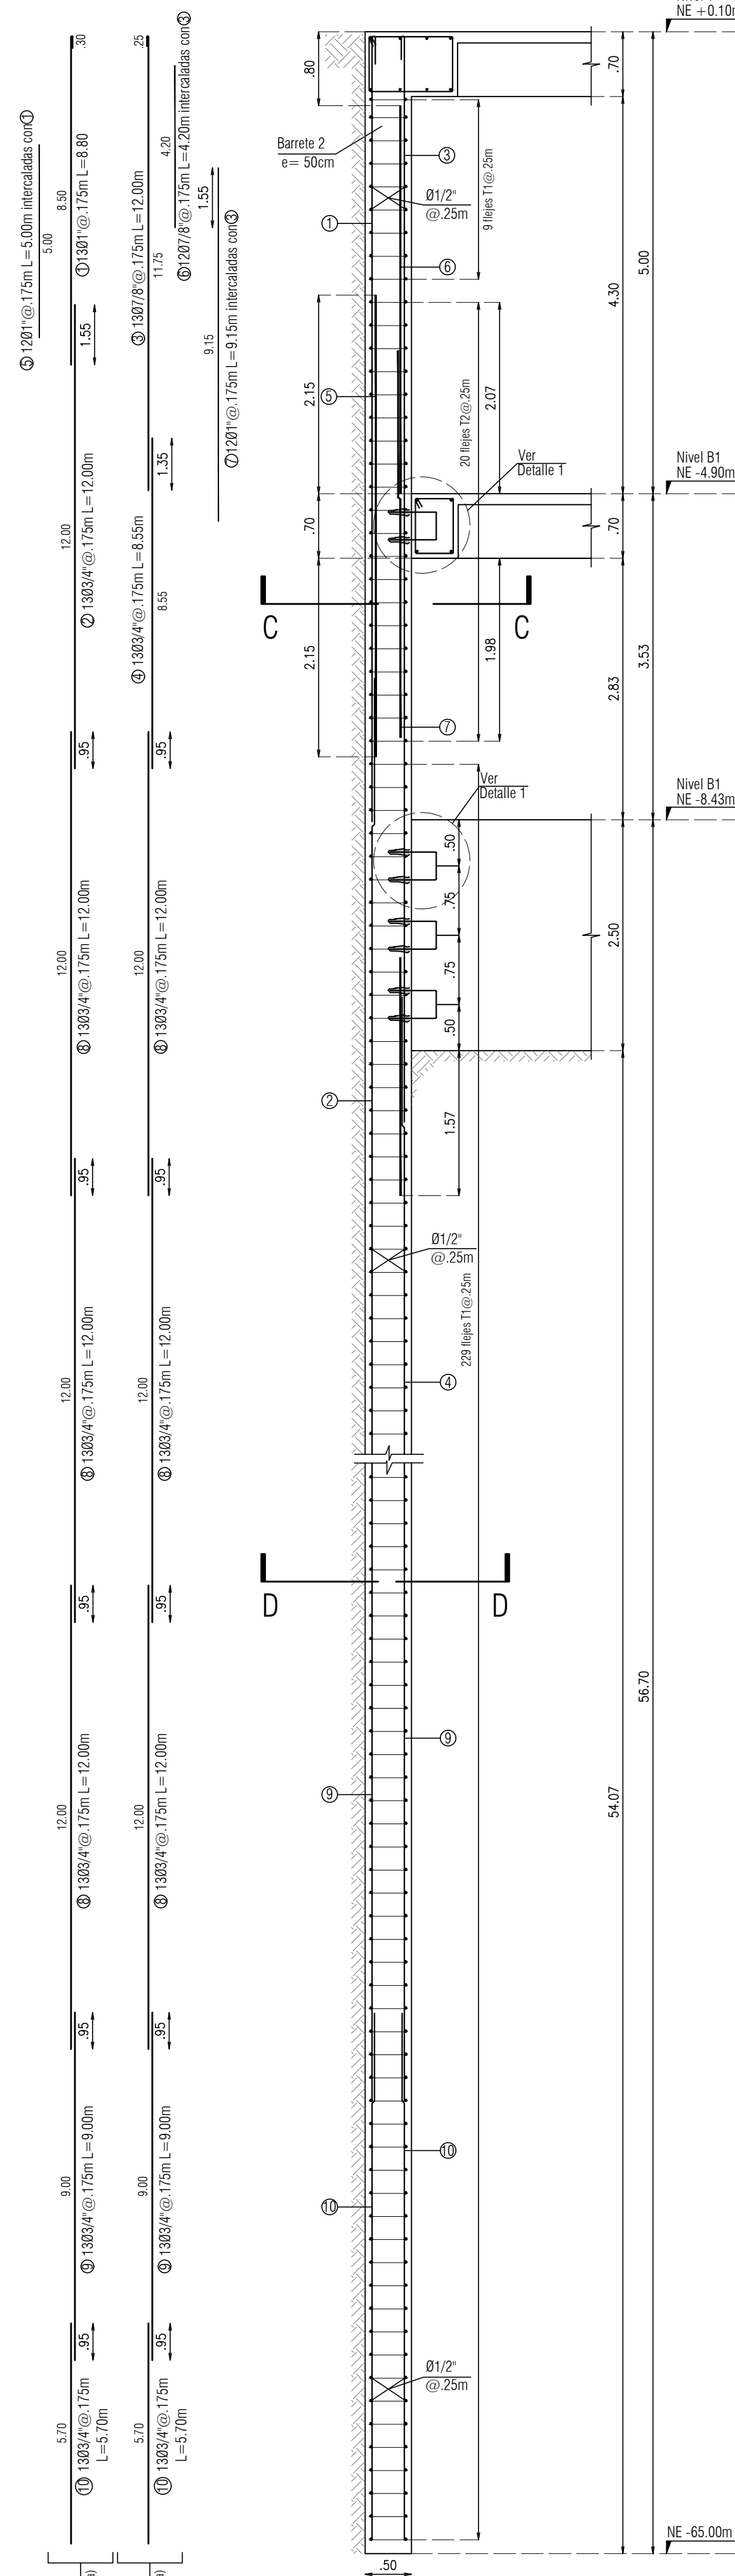


BARRETE BR2
escala 1:50

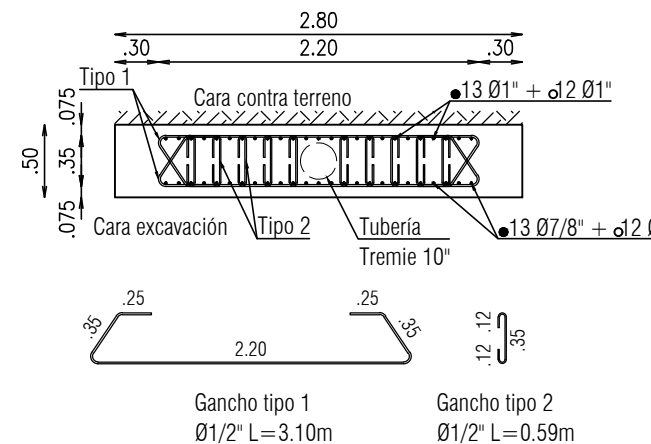


CORTE C-C - BR2
DISTRIBUCION FLEJES - T2
escala 1:50

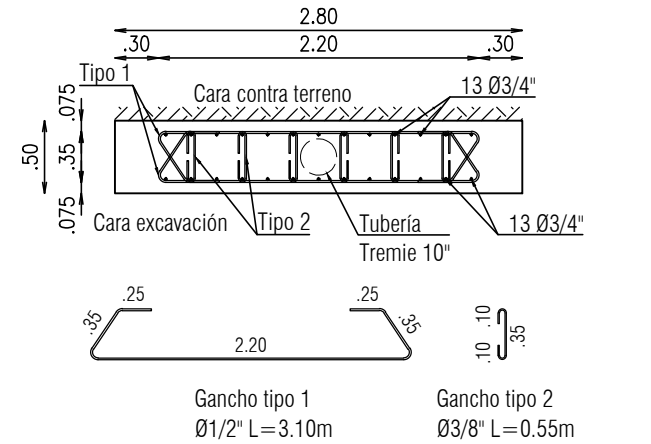


CORTE D-D - BR2
DISTRIBUCION FLEJES - T1
escala 1:50

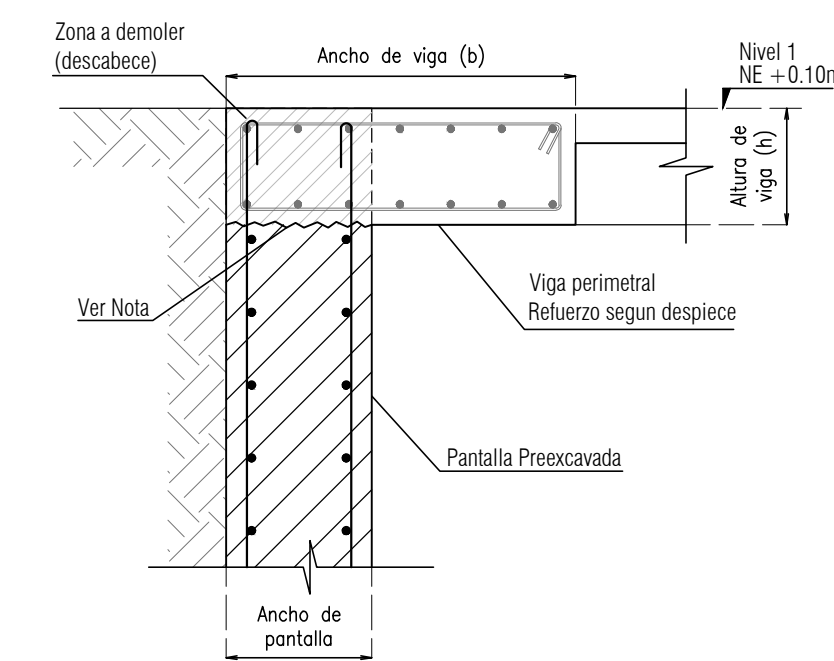

DETALLE VIGA PERIMETRAL SOBRE
PANTALLA PREEXCAVADA
escala 1:25

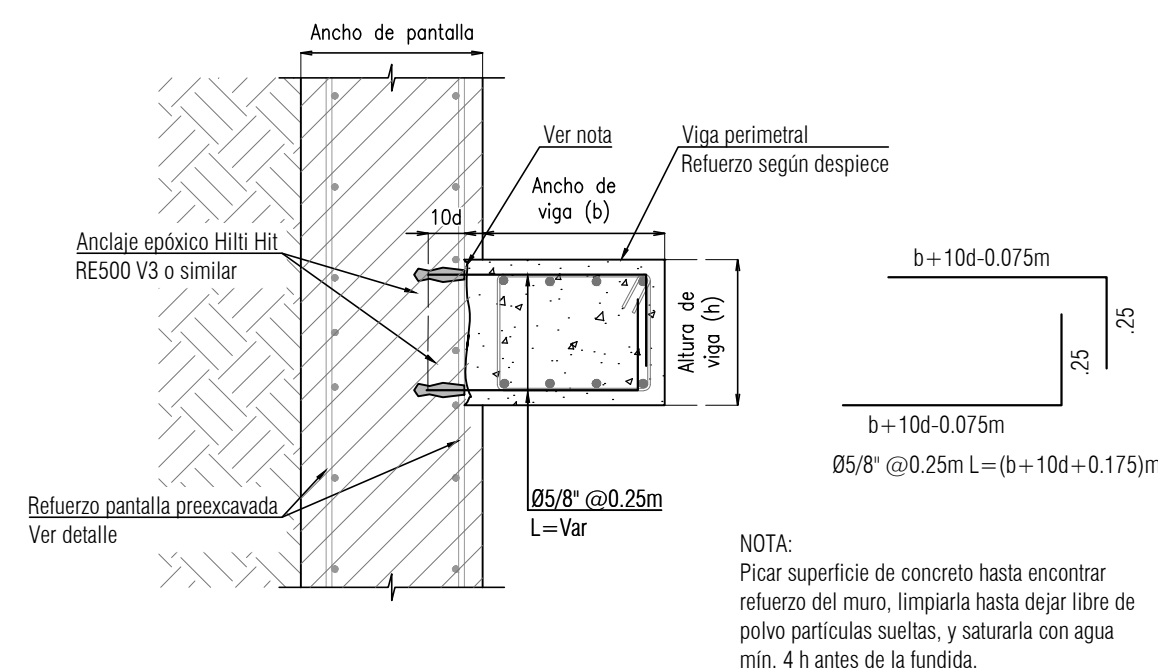

DETALLE 1
ANCLAJE VIGA PERIMETRAL A PANTALLA
PREEXCAVADA Y PILOTES TANGENTES
escala 1:20

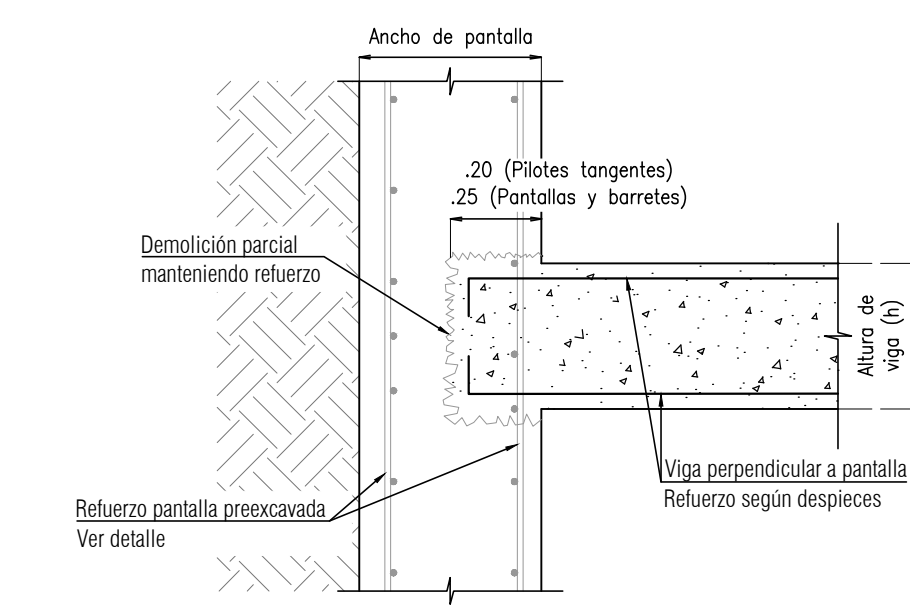

DETALLE 2
ANCLAJE DE VIGAS PERPENDICULARES A
PANTALLA PREEXCAVADA Y PILOTES TANGENTES
escala 1:20

NOTA:
Escarificar superficie de concreto hasta encontrar refuerzo del muro, limpiarla hasta dejar libre de polvo y/o partículas sueltas. Se recomienda el uso de agua como puente de adherencia entre concretos de diferentes edades. La superficie del concreto existente deberá humedecerse por cuatro horas continuas antes de vaciar el nuevo concreto.

ARQUITECTO COORDINADOR

ELEQUIPO MAZZANTI + Gensler

DISEÑO ESTRUCTURAL



ING. NICOLÁS PARRA GARCÍA
MAT. 25202-62063 CND

DISEÑADOR

INTERVENTORIA



GUTIÉRREZ DÍAZ S.A.S.
Ingeniería, arquitectura, planeación y construcción

Dirección de Interventoría: Ing. Jorge Iván García Mancilla
Mat. 630521-148083 CND


Versión	Emisión	Descripción
AA	15-06-2023	Ingeniería básica
AB	04-08-2023	Anteproyecto
AC	01-11-2023	Anteproyecto V2 50%
AD	15-12-2023	Anteproyecto V2 100%
DD	13-03-2024	Entrega curaduría
EE	10-05-2024	Proyecto Final 100%
EF	31-05-2024	Respuesta Obs 100%
FF	21-06-2024	Entrega Final
01	26-07-2024	ENTREGA FINAL

PROYECTO:
CAMPUS DE CIENCIA TECNOLOGÍA E
INNOVACIÓN DE BOGOTÁ
MAT. No. 900-00254070

FASE
ENTREGA FINAL

PROPOSITO DE EMISION	
Curaduría	☐
Revisión	☐
Entrega Cliente	☒
Coordinación	☐
Construcción	☒

ZONIFICACIÓN
Nivel 24
Nivel 23
Nivel 22
Nivel 21
Nivel 20
Nivel 19
Nivel 18
Nivel 17
Nivel 16
Nivel 15
Nivel 14
Nivel 13
Nivel 12
Nivel 11
Nivel 10
Nivel 9
Nivel 8
Nivel 7
Nivel 6
Nivel 5
Nivel 4
Nivel 3
Nivel 2
Nivel 1
Nivel 01
Nivel 02

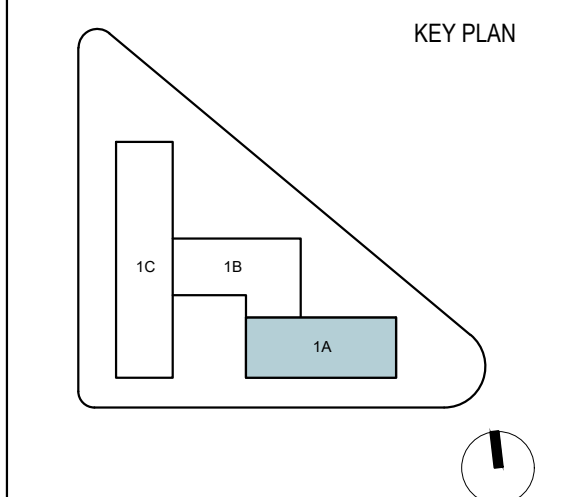

Fecha: 26-07-2024

Escala: As Indicated

DETALLES DE
CIMENTACION

CTIB_CNI_EST_503_DET_XXX_01