




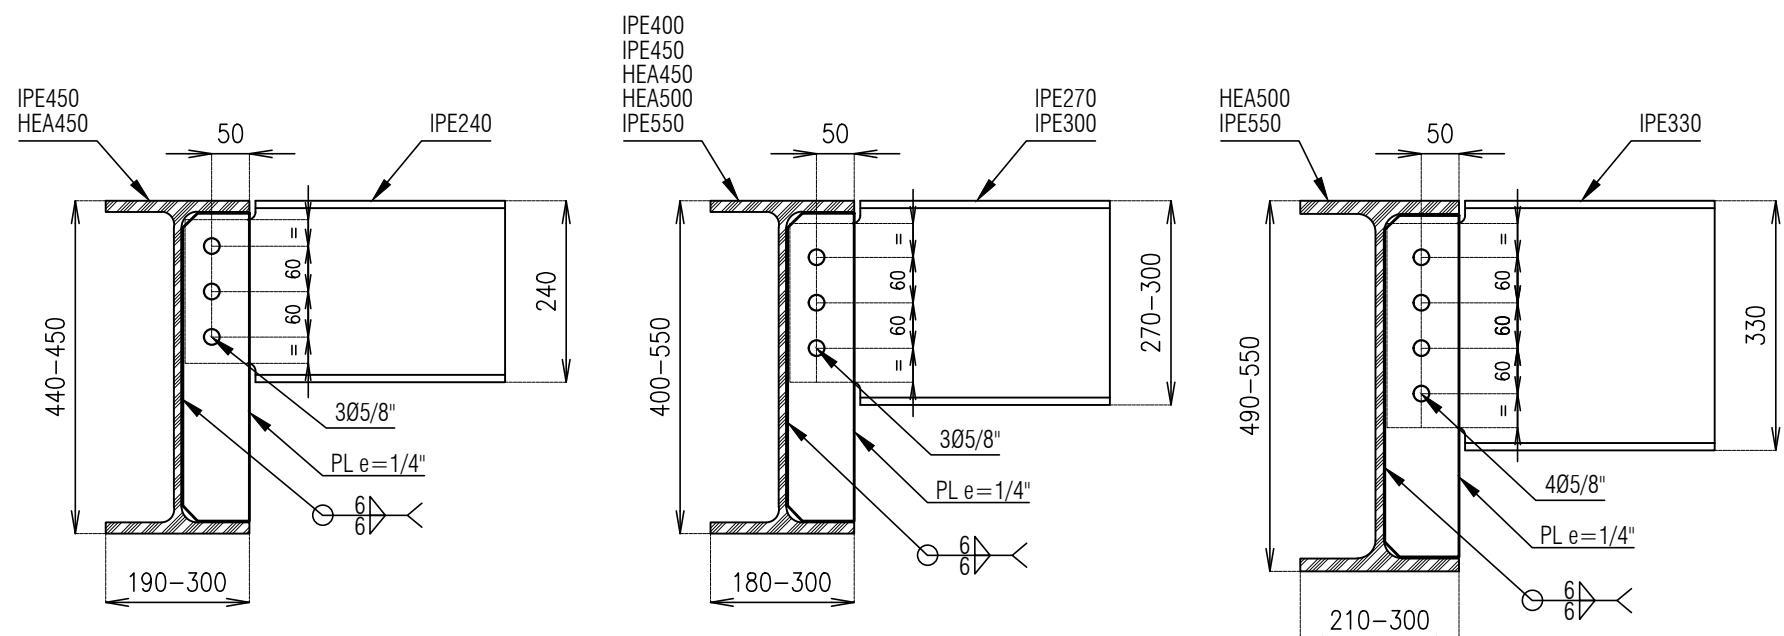


Conexiones típicas de Viguetas
escala 1:10

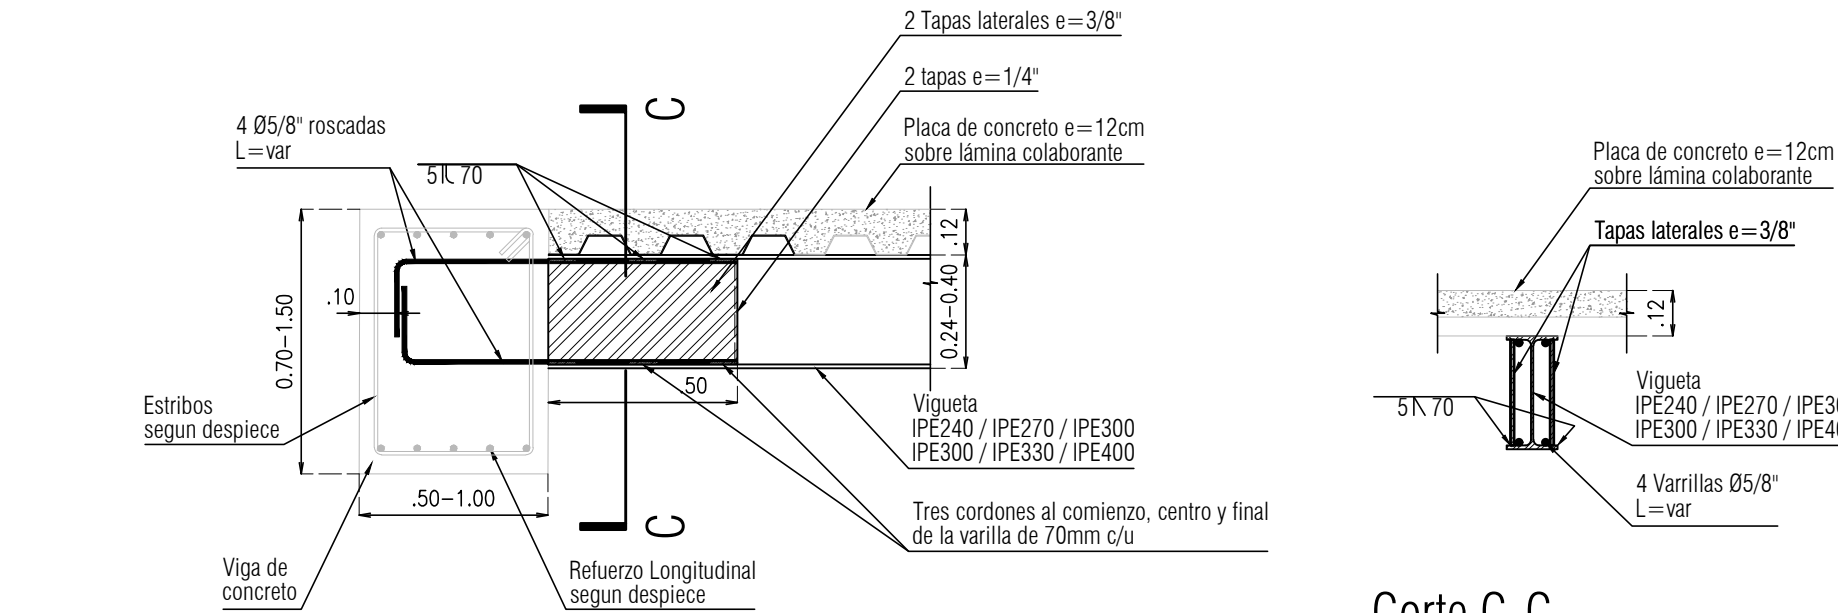


Corte C-C

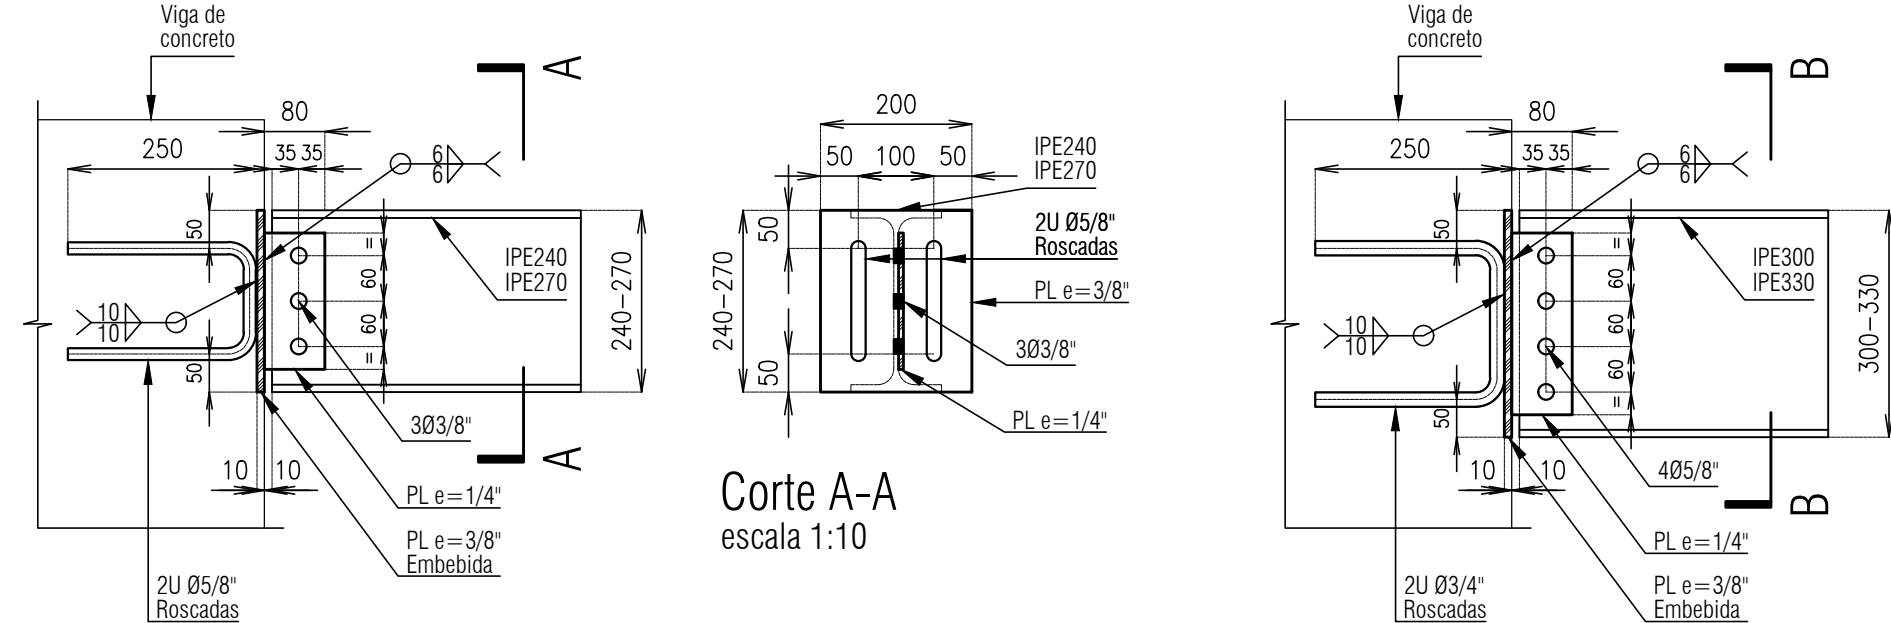


Corte A-A
escala 1:10

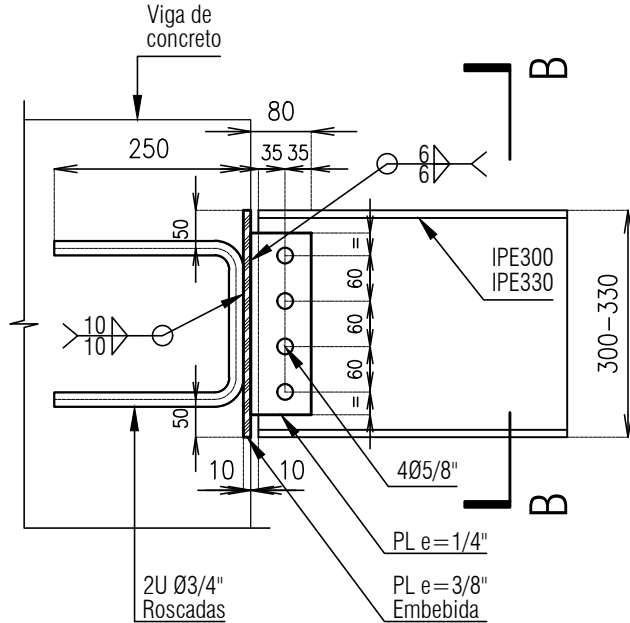

Corte B-B
escala 1:10

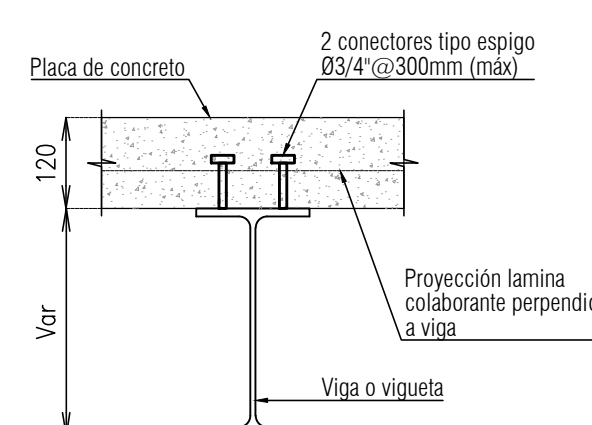


Detalle conectores de cortante
escala 1:10

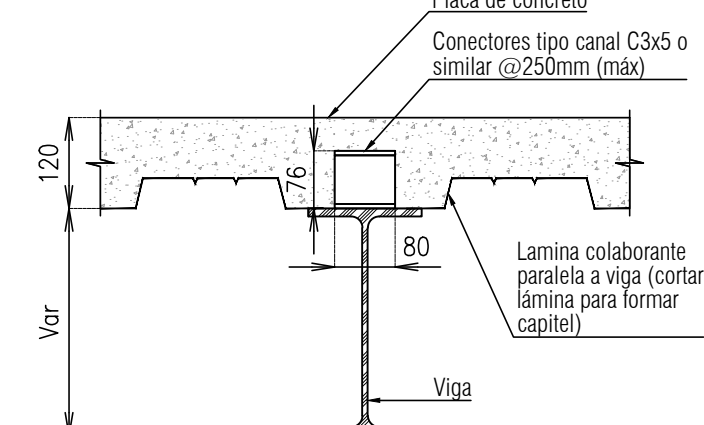

NOTAS IMPORTANTES:


- Ver especificaciones de materiales en plano CTIB_CNI_EST_000_GEN_XXX
- Los presentes planos son de diseño. El fabricante de la estructura metálica debe elaborar los respectivos planos de taller, los cuales deben ser revisados y aprobados por la interventoría y la supervisión técnica de la obra.
- Las vigas y las viguetas requieren apuntalamiento durante la fundida y endurecimiento de la losa de concreto.
- Implementar en obra tapas de lamina colaborante como testero durante fundida de concreto.
- En los detalles se indican cantidad y diámetro de pernos de conexión.

Detalles tipicos de conexión de viguetas a estructura de concreto
escala 1:20

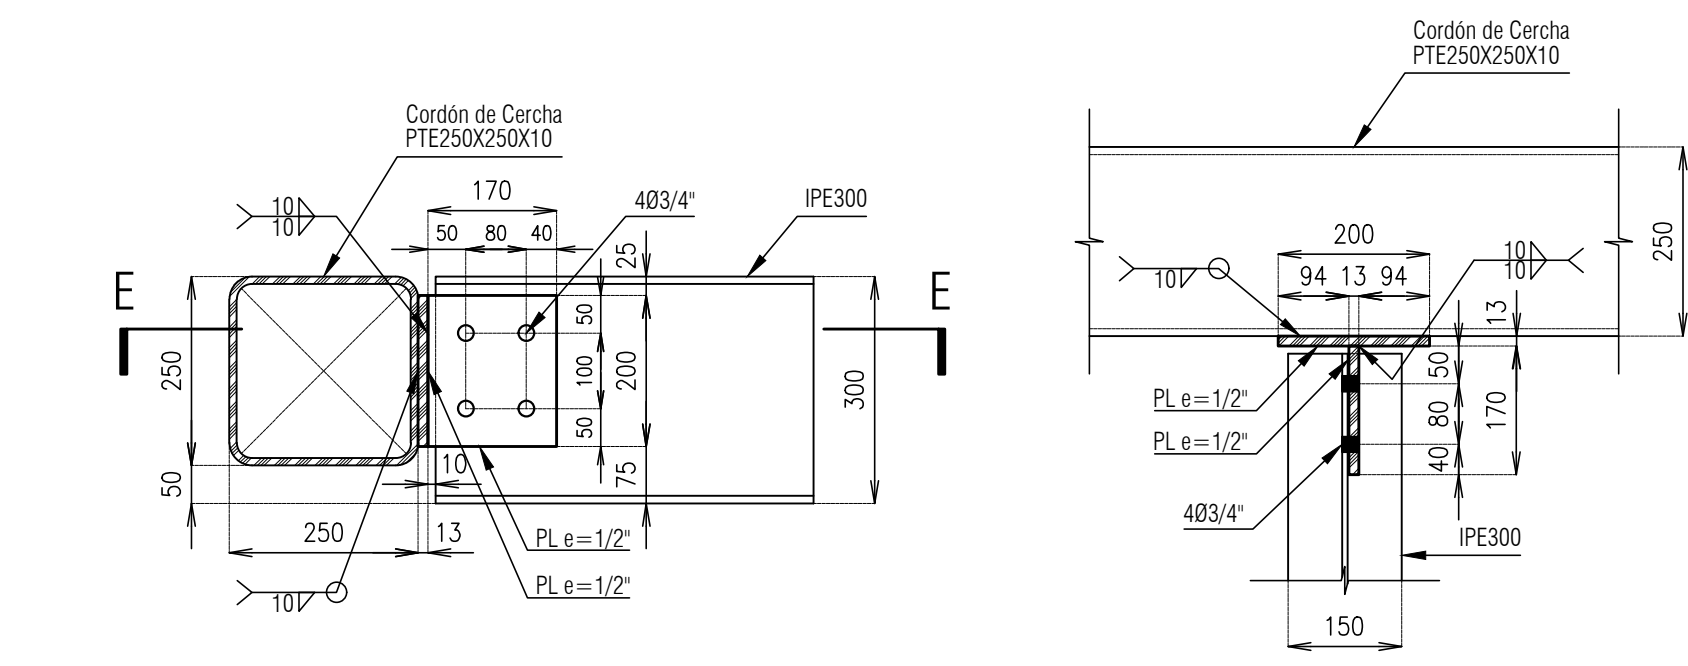


Conexión IPE300 a Cercha de Fachada
Niveles 8 a 23
escala 1:10

Sección E-E
escala 1:10

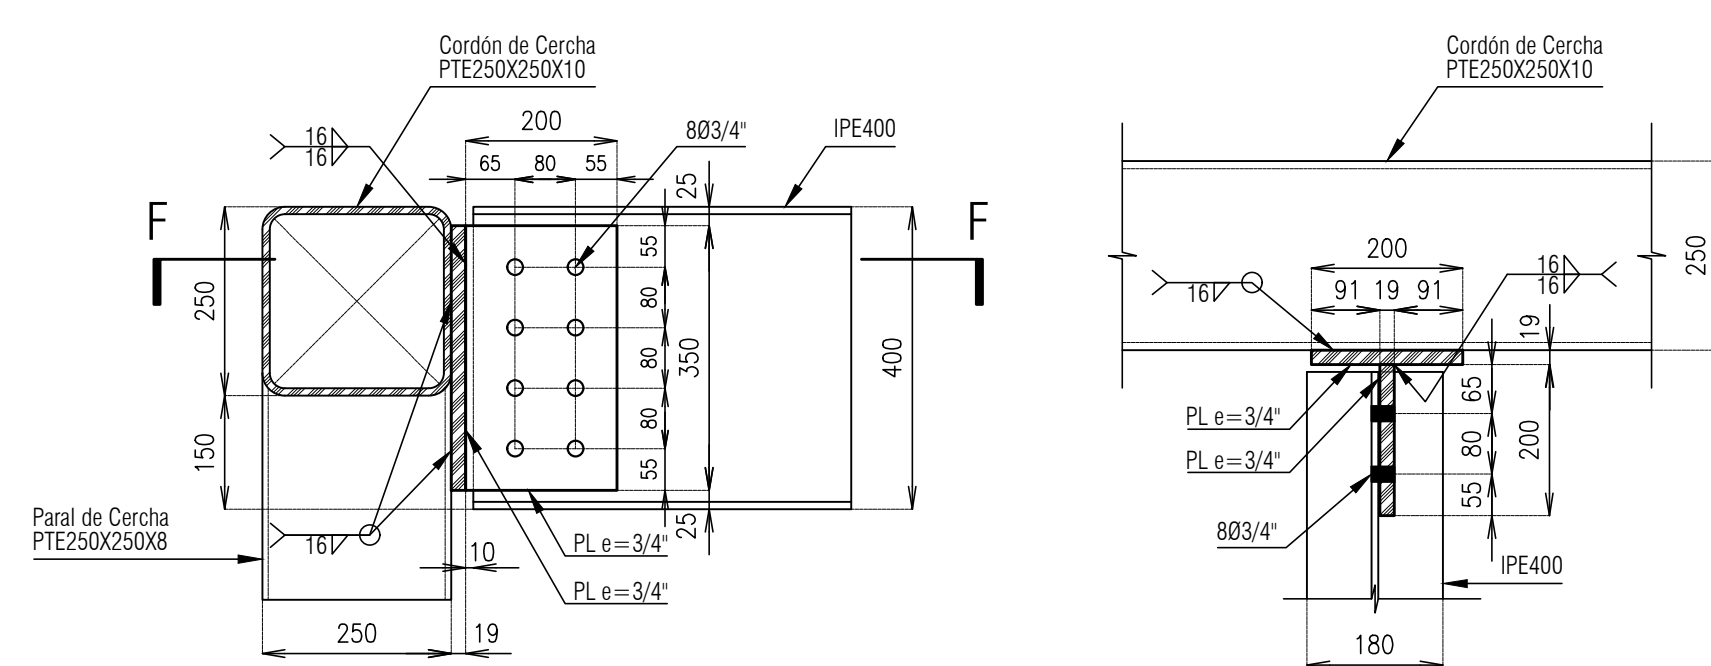


Conexión IPE400 a Cercha de Fachada
Niveles 8 a 23
escala 1:10


Sección F-F
escala 1:10

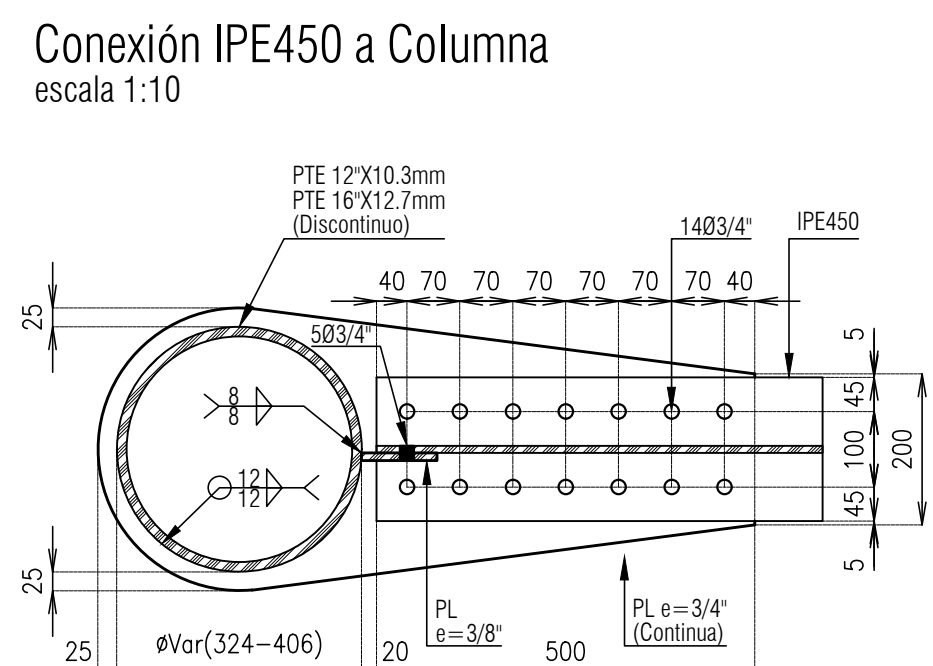


Corte I-I
escala 1:10

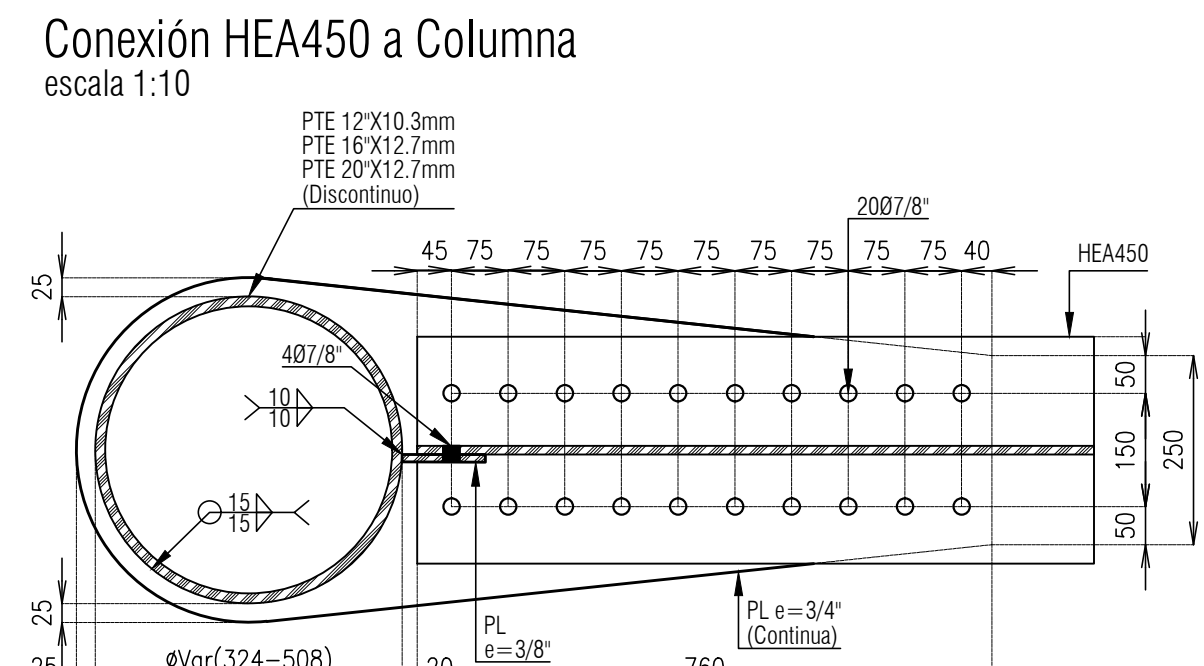


Corte J-J
escala 1:10

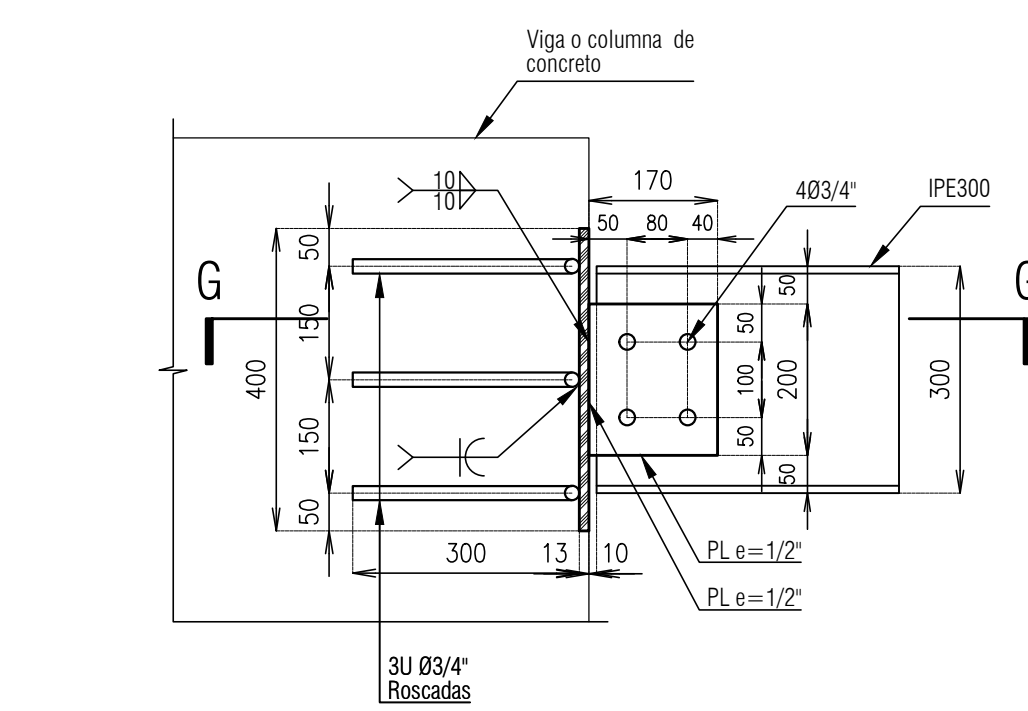


Conexión IPE300 a Concreto (Niveles 8 a 23)
escala 1:10

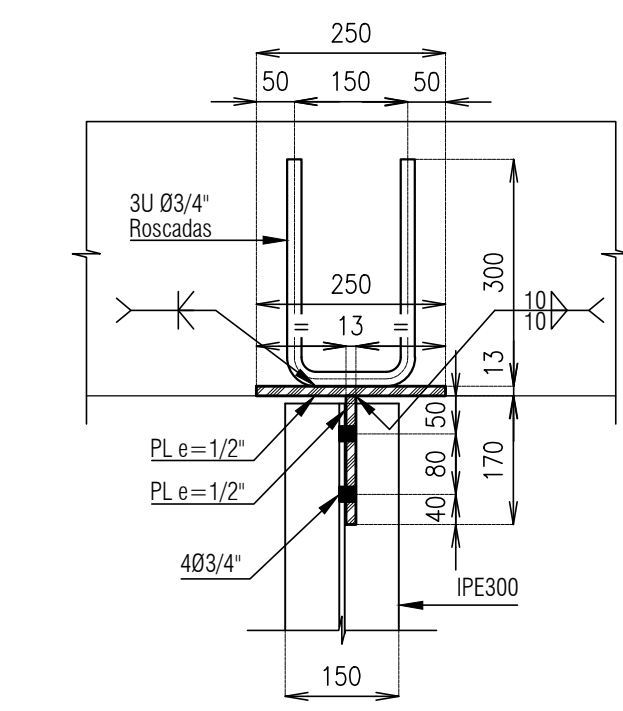


Sección G-G
escala 1:10

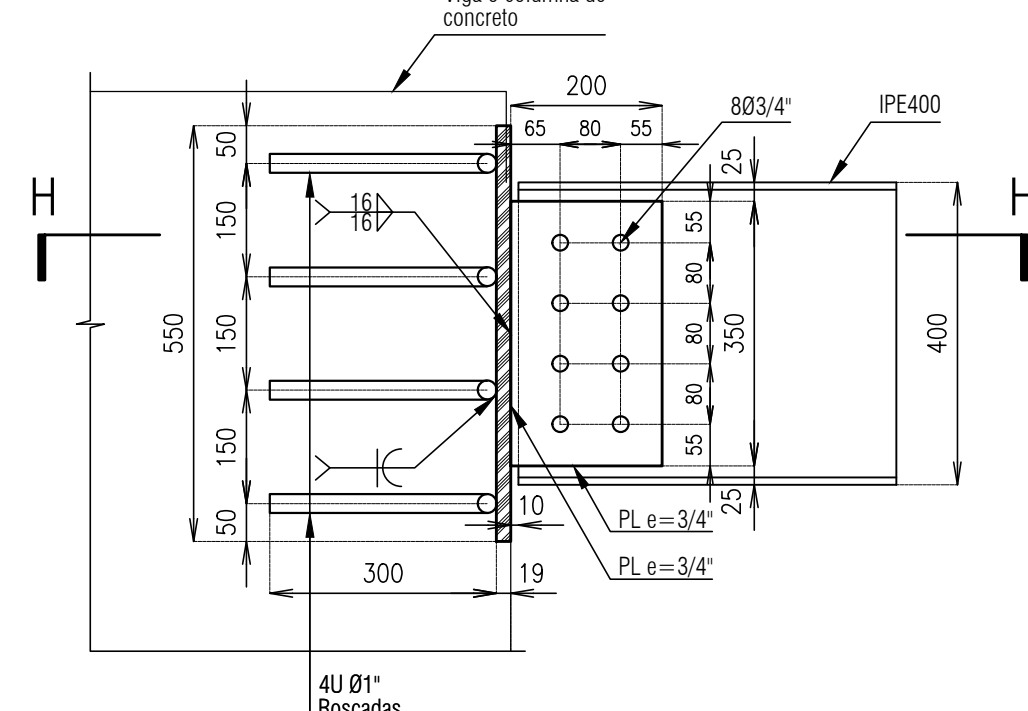


Conexión IPE400 a Concreto (Terraza)
escala 1:10

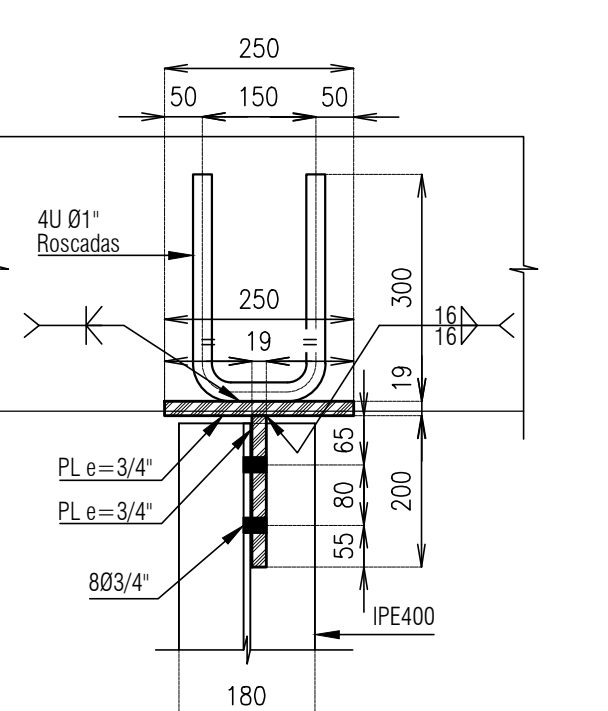


Sección H-H
escala 1:10

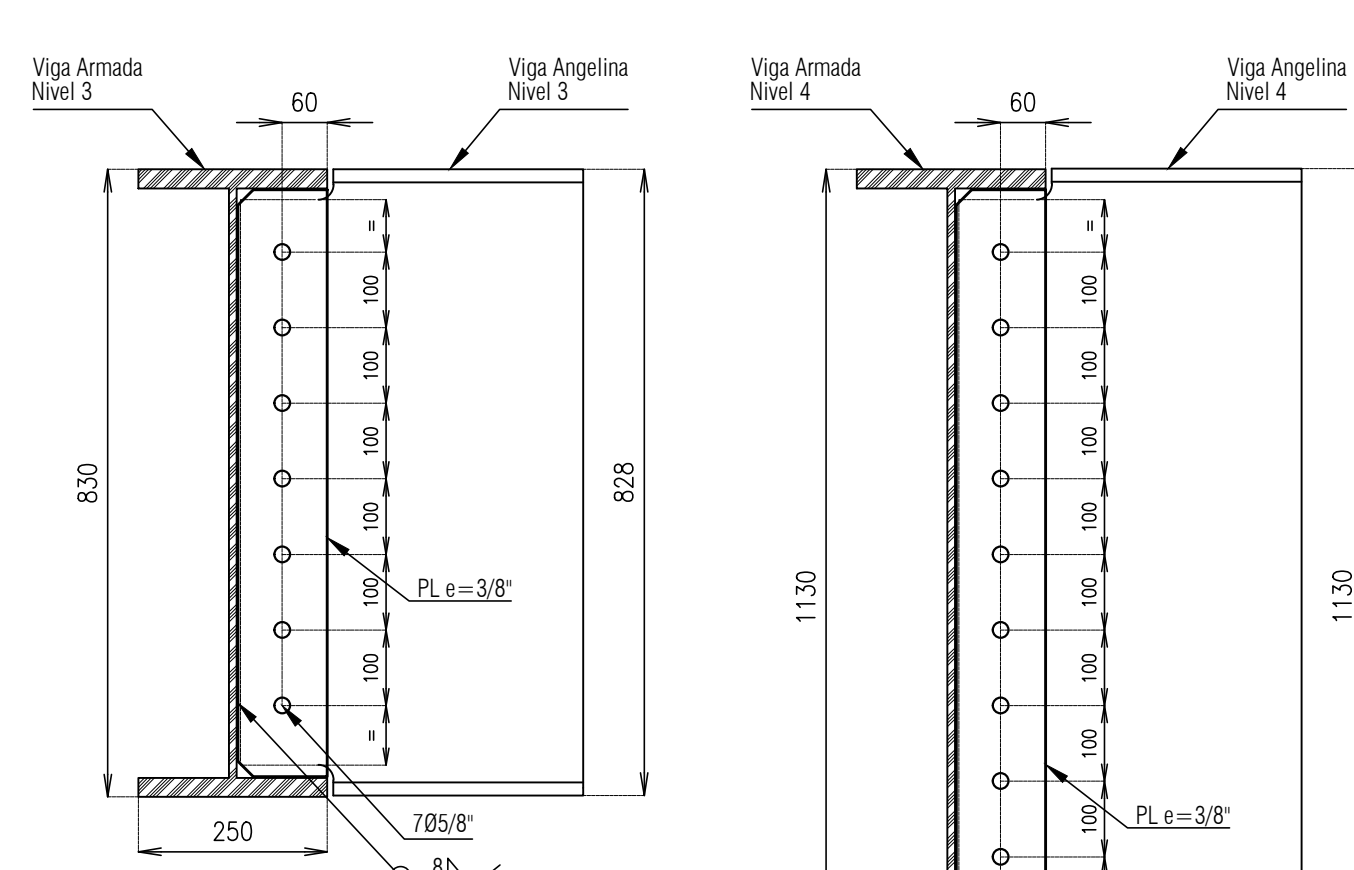

Conexiones de Vigas Angelinas a
Vigas Armadas
escala 1:10

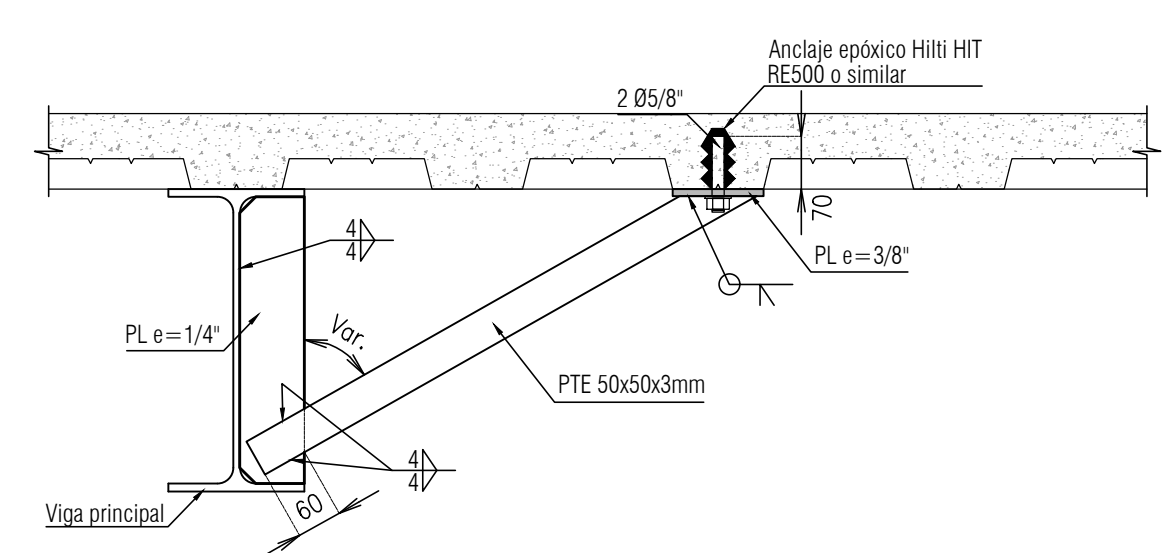

Detalles típicos de arriostamiento de vigas
escala 1:10

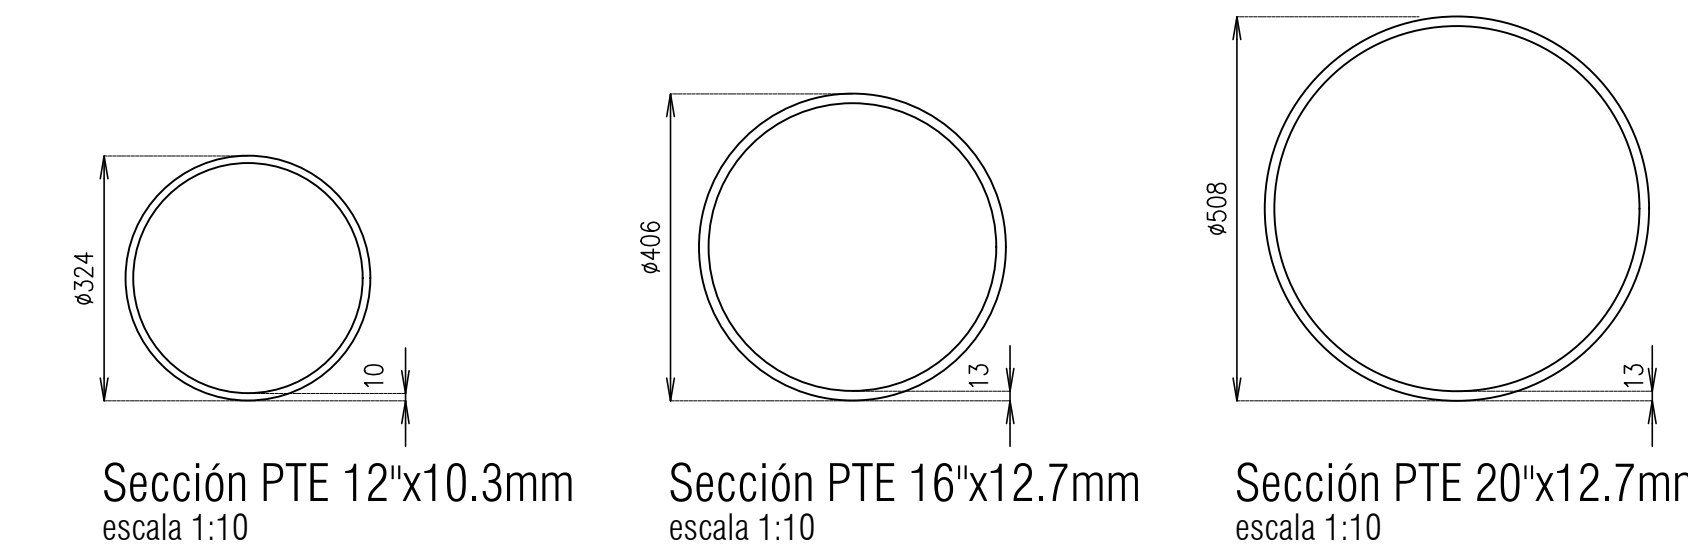

Sección IPE240
escala 1:10

Sección IPE270
escala 1:10

Sección IPE300
escala 1:10

Sección IPE330
escala 1:10

Sección IPE400
escala 1:10

Sección IPE450
escala 1:10

Sección IPE550
escala 1:10

Sección HEA450
escala 1:10

Sección HEA500
escala 1:10

Sección HEA600
escala 1:10


Viga Angelina
Nivel 3
escala 1:20

Viga Angelina
Nivel 4
escala 1:20

Viga Armada
Nivel 3
escala 1:20

Viga Armada
Nivel 4
escala 1:20

Detalle Viga Angelina Nivel 3
escala 1:50

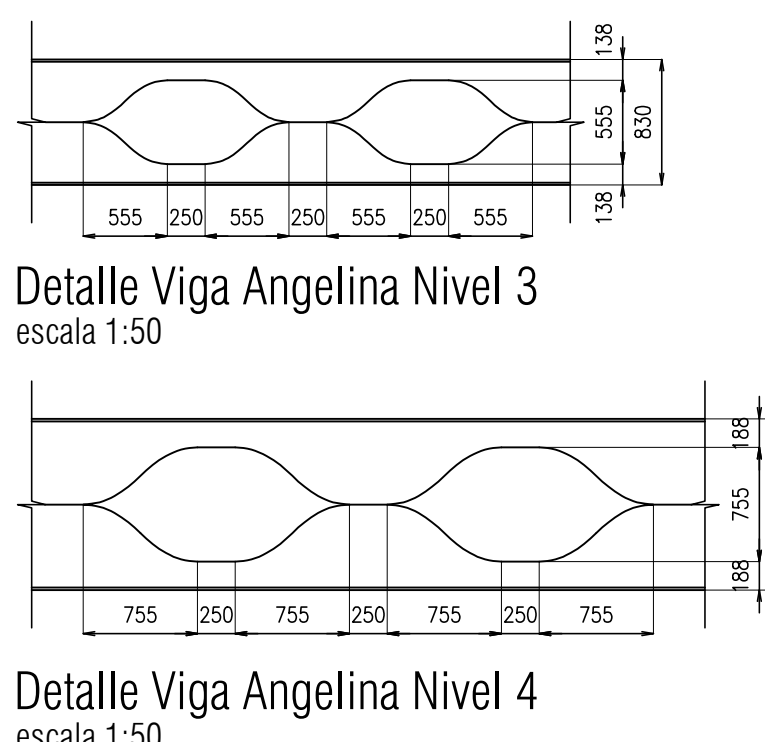

Detalle Viga Angelina Nivel 4
escala 1:50

ARQUITECTO COORDINADOR

**EL EQUIPO
MAZZANTI + Gensler**

DISÑO ESTRUCTURAL



DISEÑADOR

ING. NICOLÁS PARRA GARCÍA
MAT. 23202 62063 CND

INTERVENTORIA



Director de Interventoría:

Ing. Jorge Iván García Mancilla
Mat. 632021 148063 QND

Versión	Emisión	Descripción
AA	15-06-2023	Ingeniería básica
AB	04-08-2023	Anteproyecto
AC	01-11-2023	Anteproyecto V2 50%
AD	15-12-2023	Anteproyecto V2 100%
DD	13-03-2024	Entrega curaduría
EE	10-05-2024	Proyecto Final 100%
EF	31-05-2024	Respuesta Obs 100%
FF	21-06-2024	Entrega Final
01	28-07-2024	ENTREGA FINAL

PROYECTO:

CAMPUS DE CIENCIA TECNOLOGÍA E
INNOVACIÓN DE BOGOTÁ

FASE

ENTREGA FINAL


PROPÓSITO DE EMISIÓN

Curaduría	☐	Coordinación	☐
Revisión	☐	Construcción	☐
Entrega Cliente	☒		

ZONIFICACIÓN

Nivel 24	
Nivel 23	
Nivel 22	
Nivel 21	
Nivel 20	
Nivel 19	
Nivel 18	
Nivel 17	
Nivel 16	
Nivel 15	
Nivel 14	
Nivel 13	
Nivel 12	
Nivel 11	
Nivel 10	
Nivel 9	
Nivel 8	
Nivel 7	
Nivel 6	
Nivel 5	
Nivel 4	
Nivel 3	
Nivel 2	
Nivel 1	
Nivel 01	
Nivel 02	

KEY PLAN

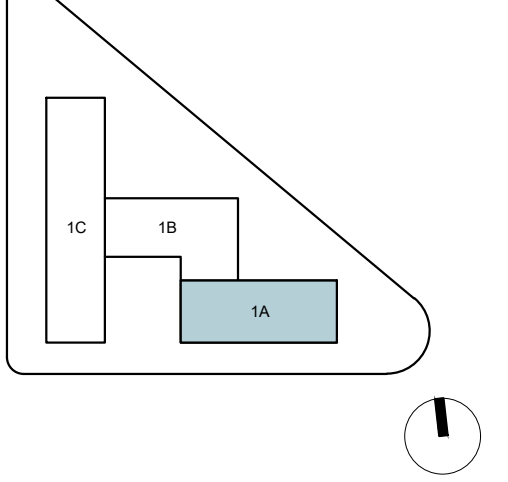

Fecha:

26-07-2024

Escala:

As Indicated

DETALLES DE CONEXIONES

CTIB_CNI_EST_510_DET_XXX_01