




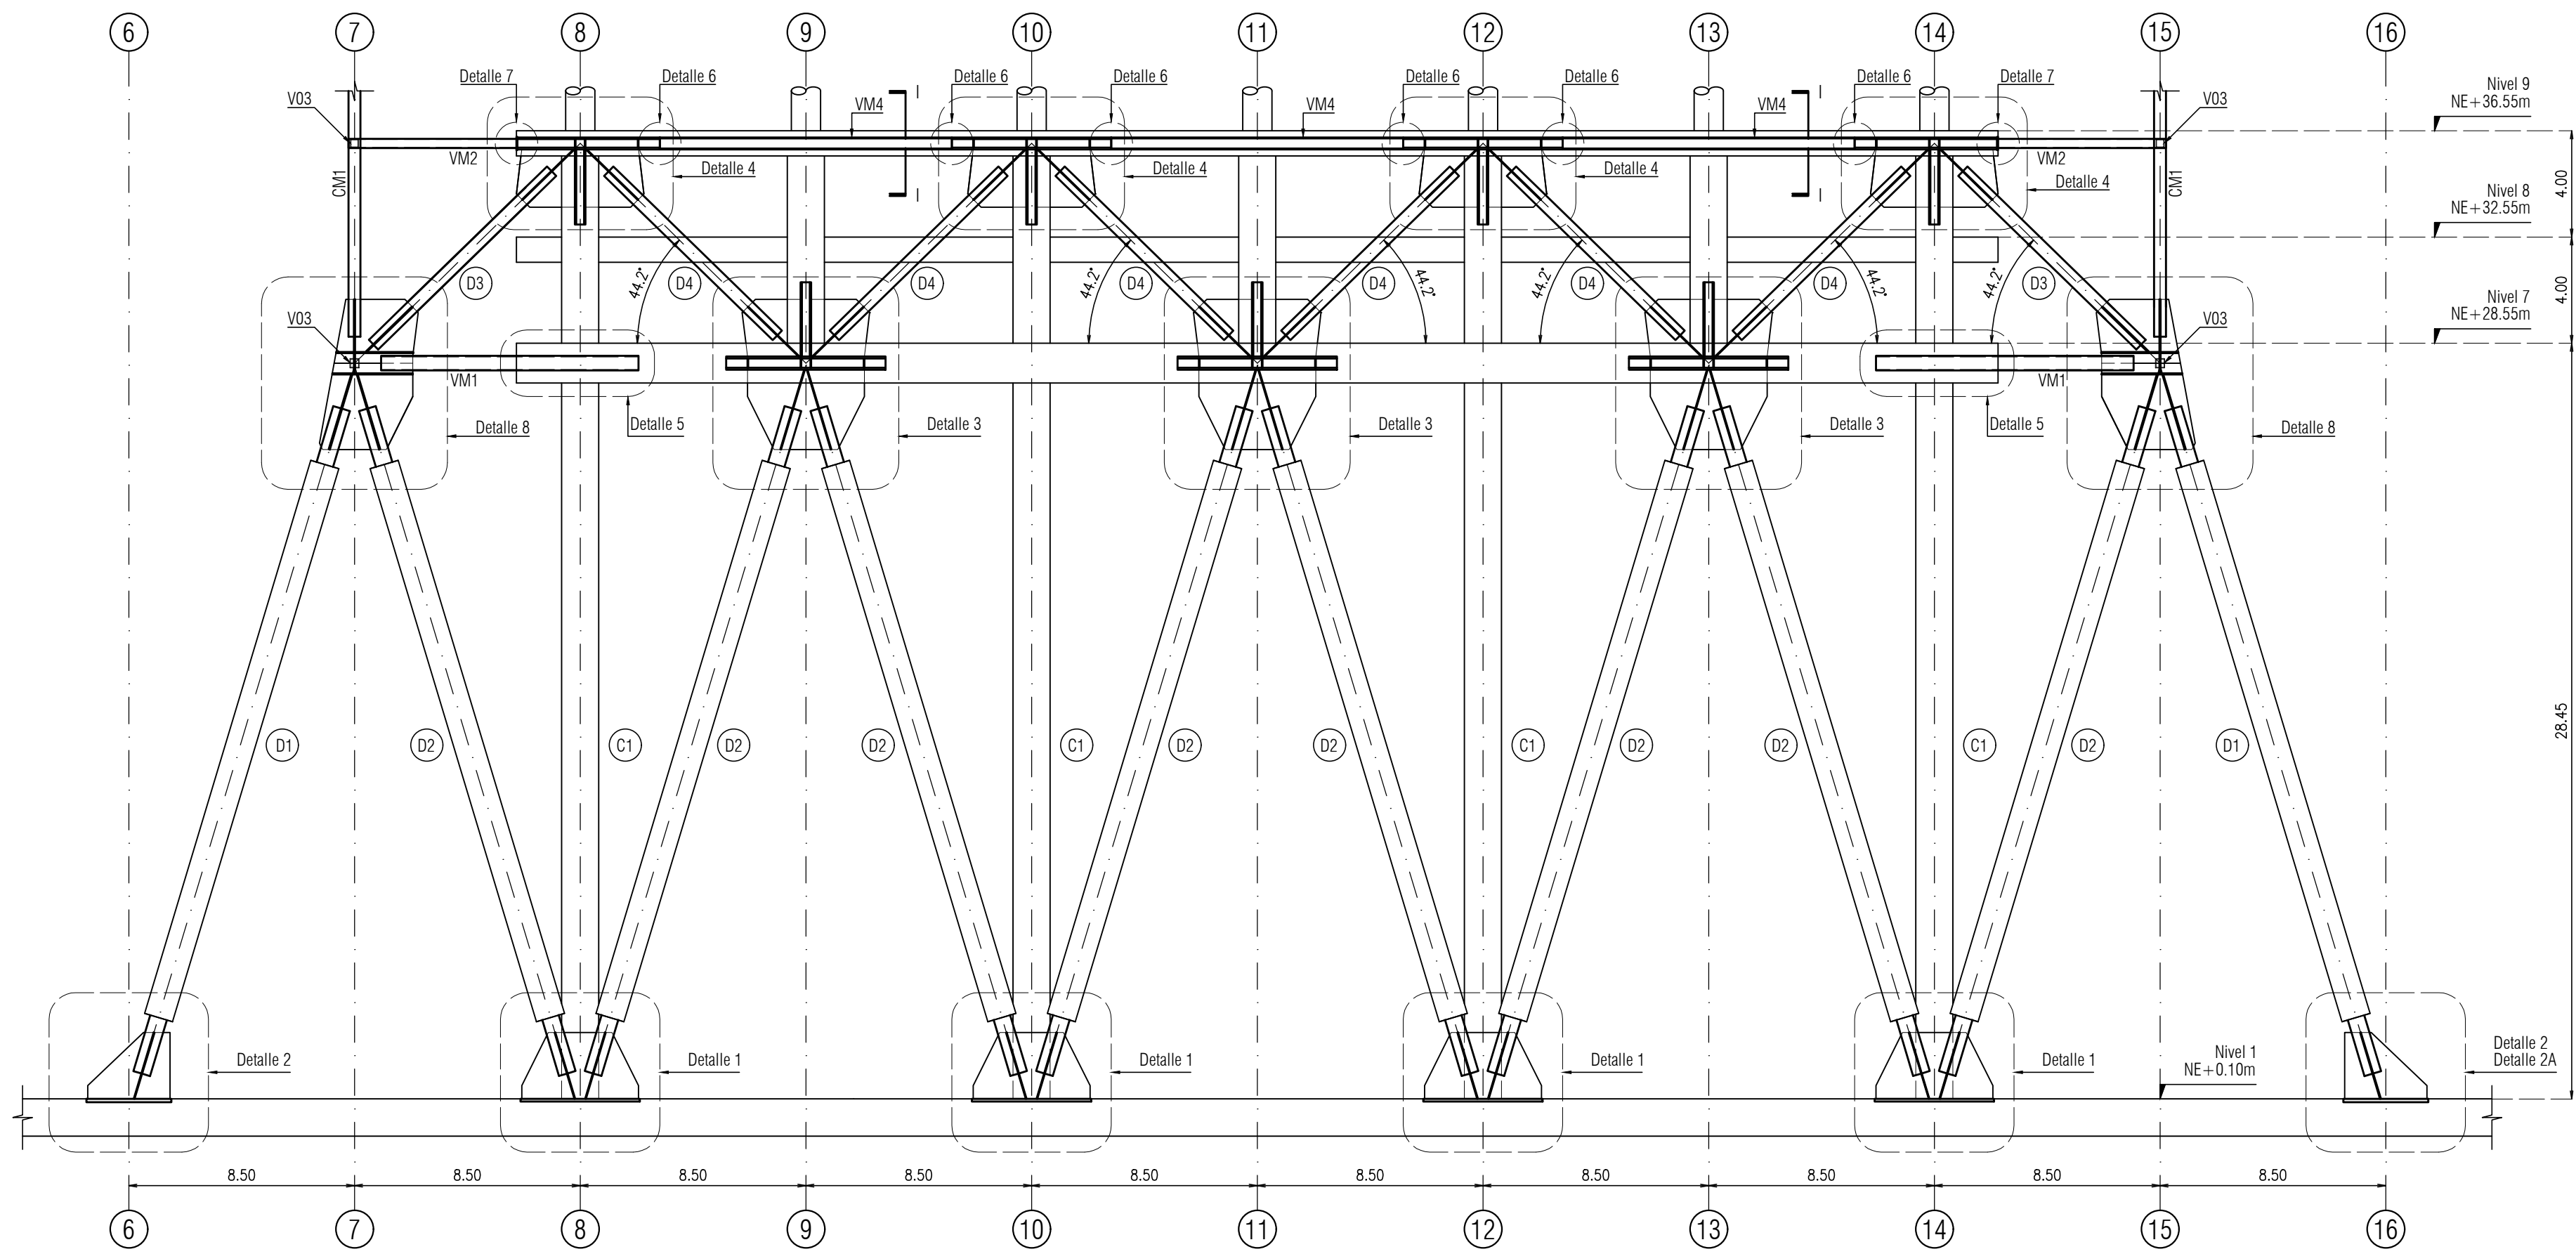


ALZADO DIAGONALES NIVEL 1 A 9
escala 1:100

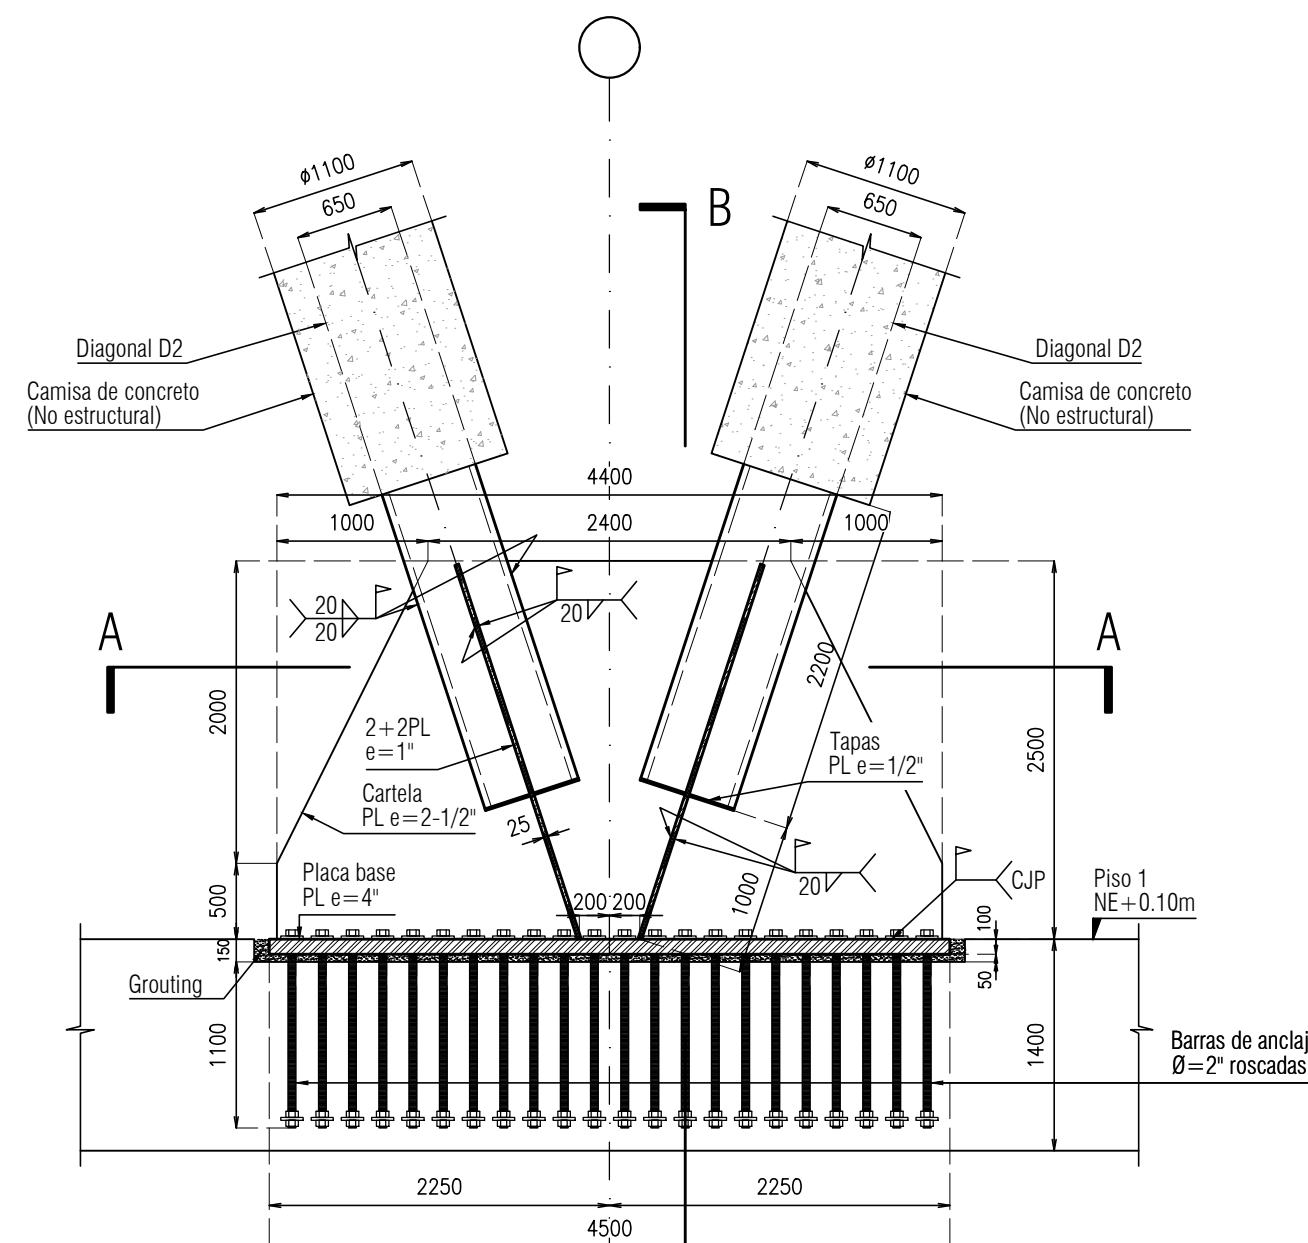


Detalle 1
escala 1:50

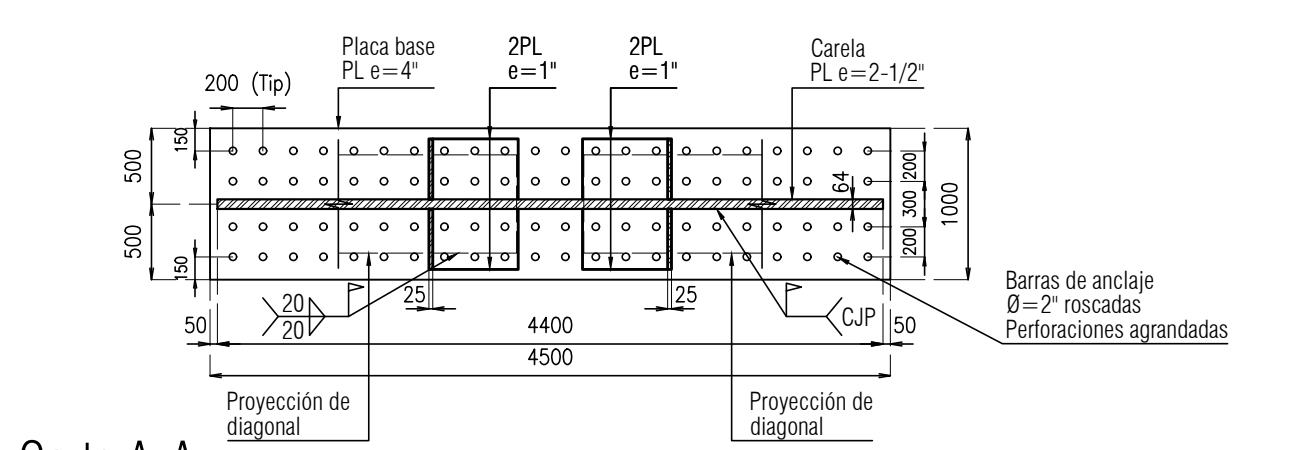


Corte A-A
escala 1:50

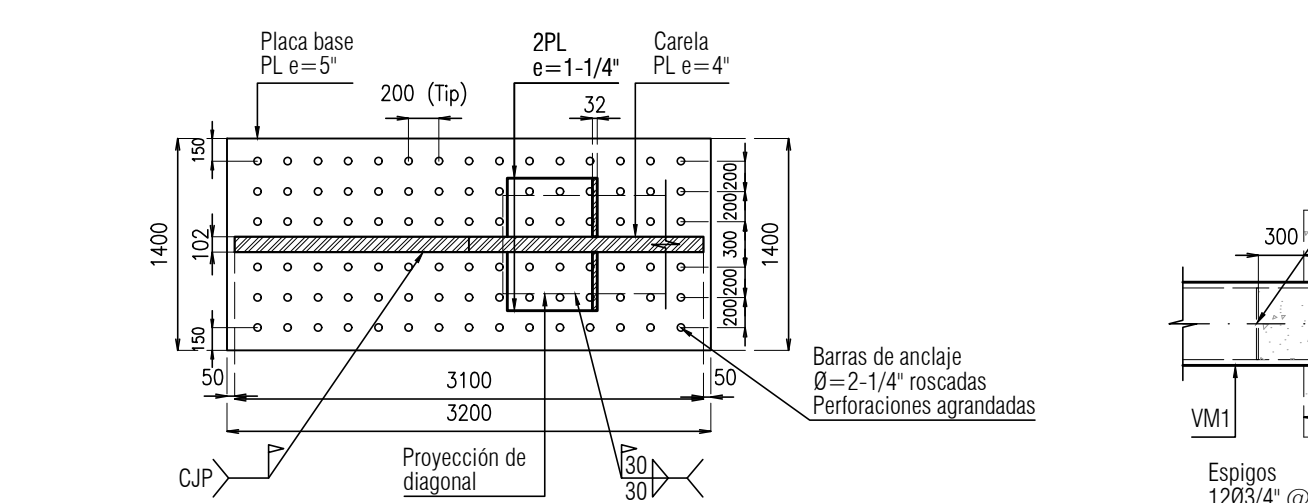


Corte C-C
escala 1:50

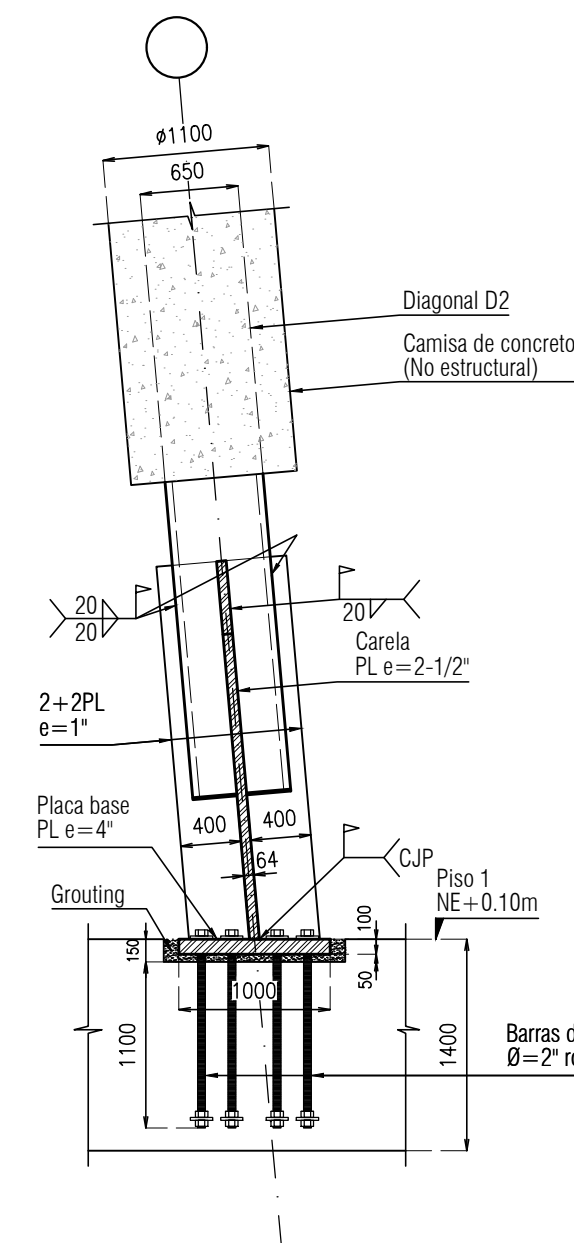


Corte B-B
escala 1:50

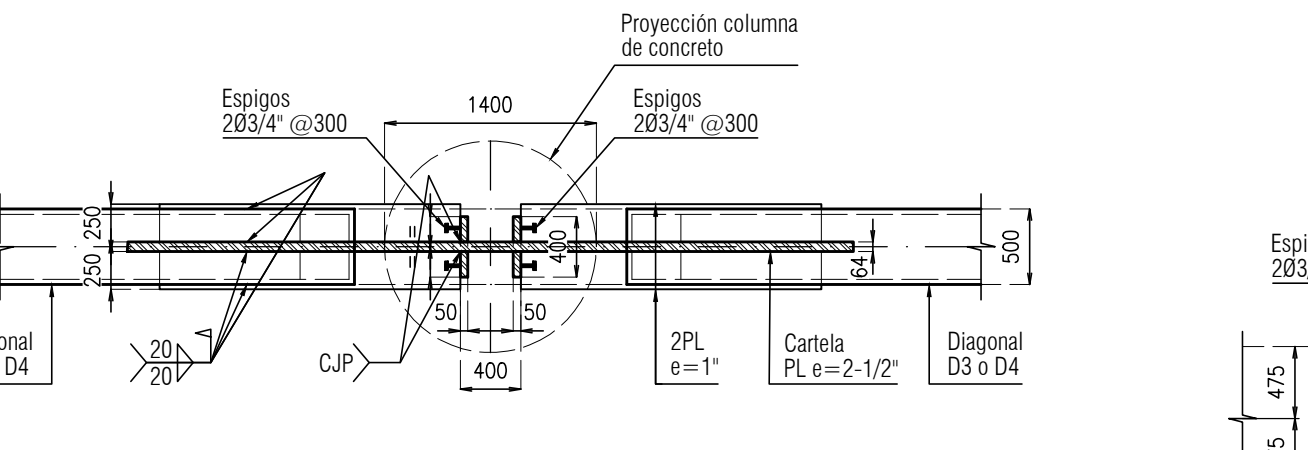


Corte F-F
escala 1:50

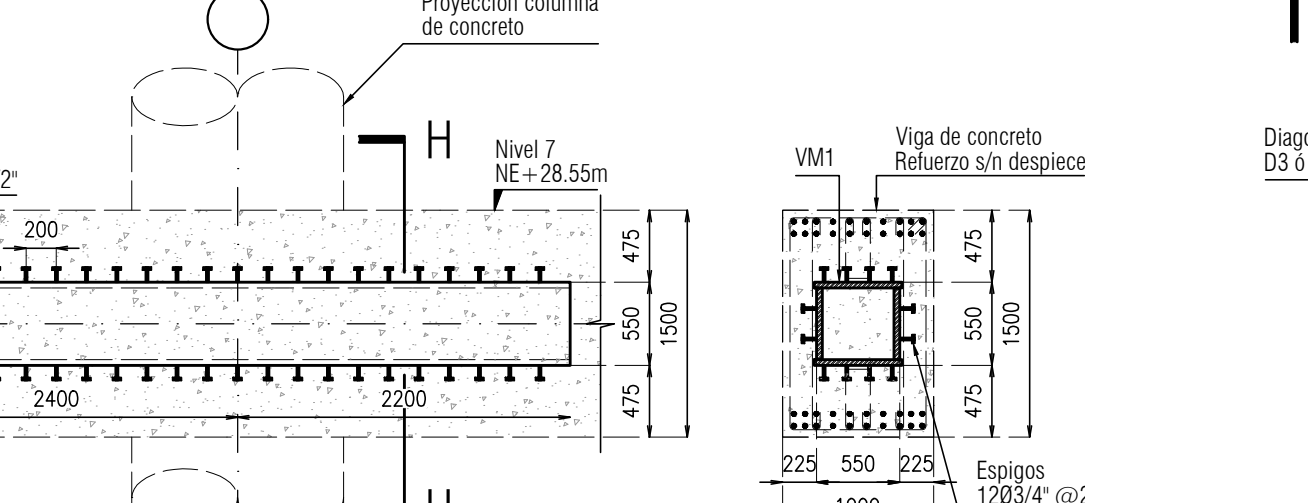


Detalle 5
escala 1:50

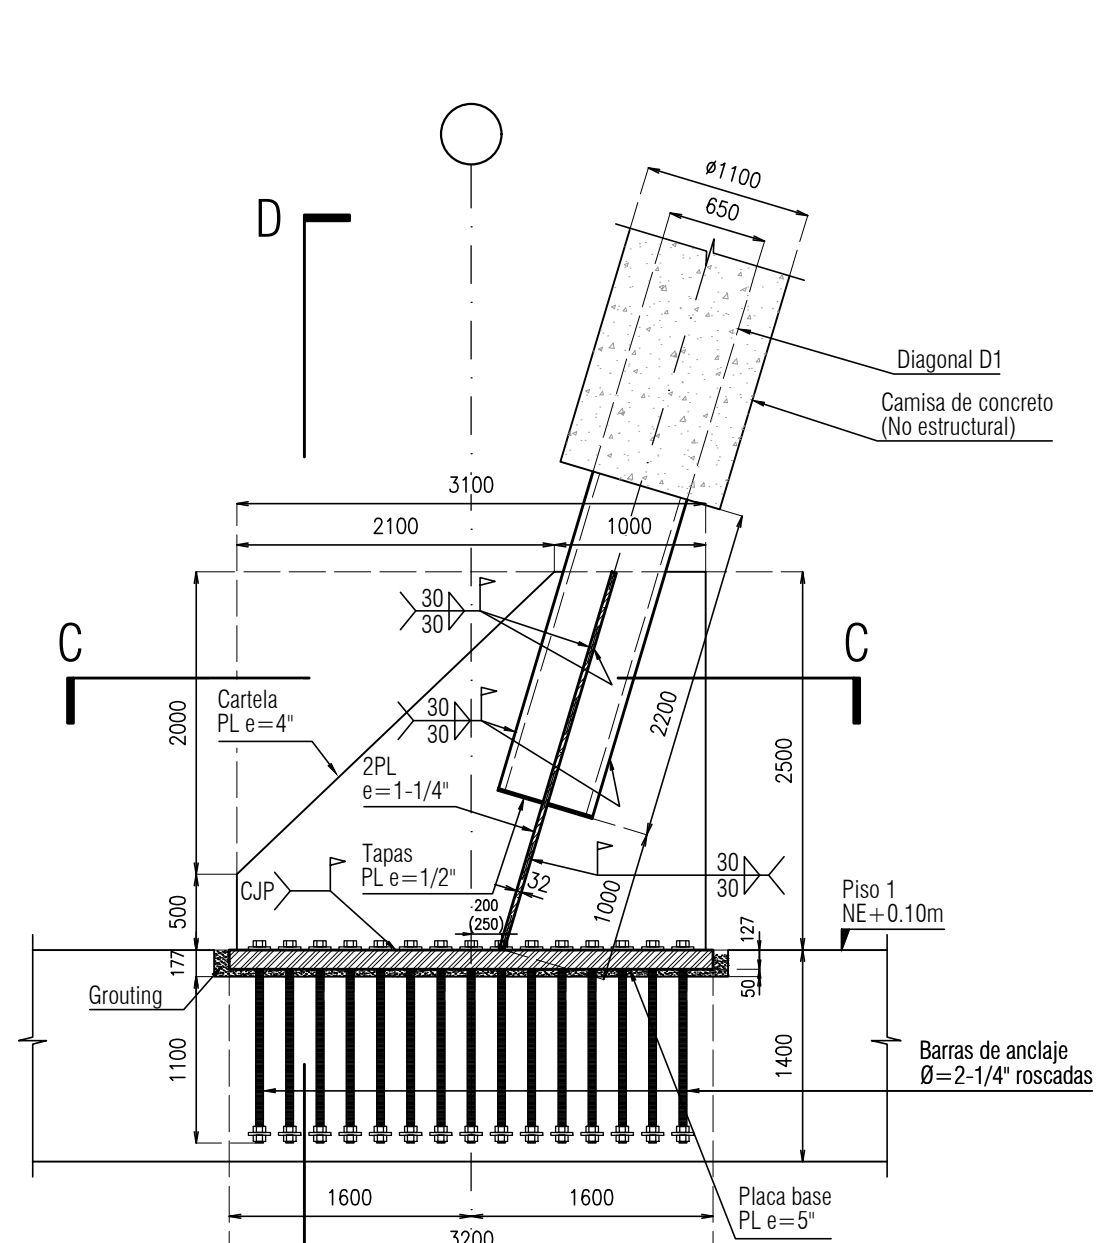


Detalle 2
escala 1:50

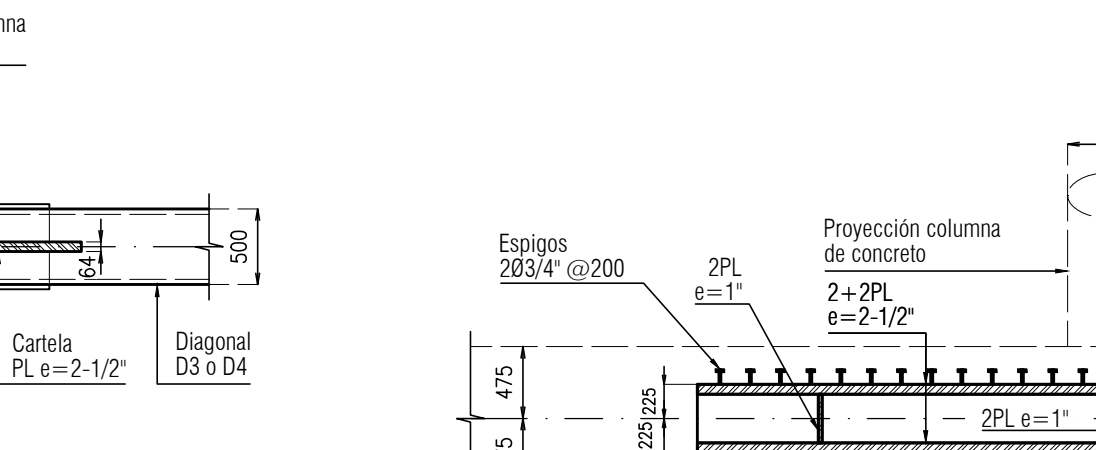


Corte D-D
escala 1:50

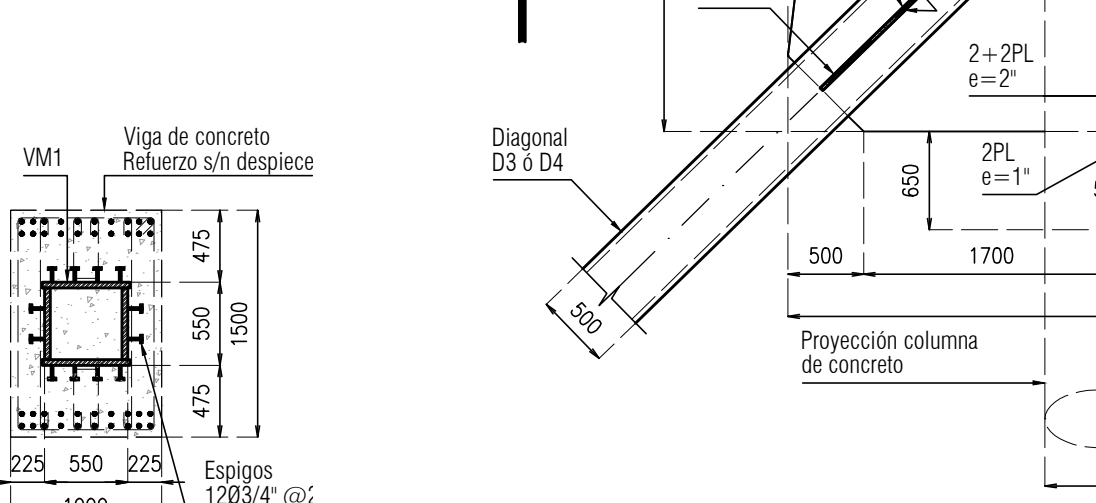


Detalle 4
escala 1:50

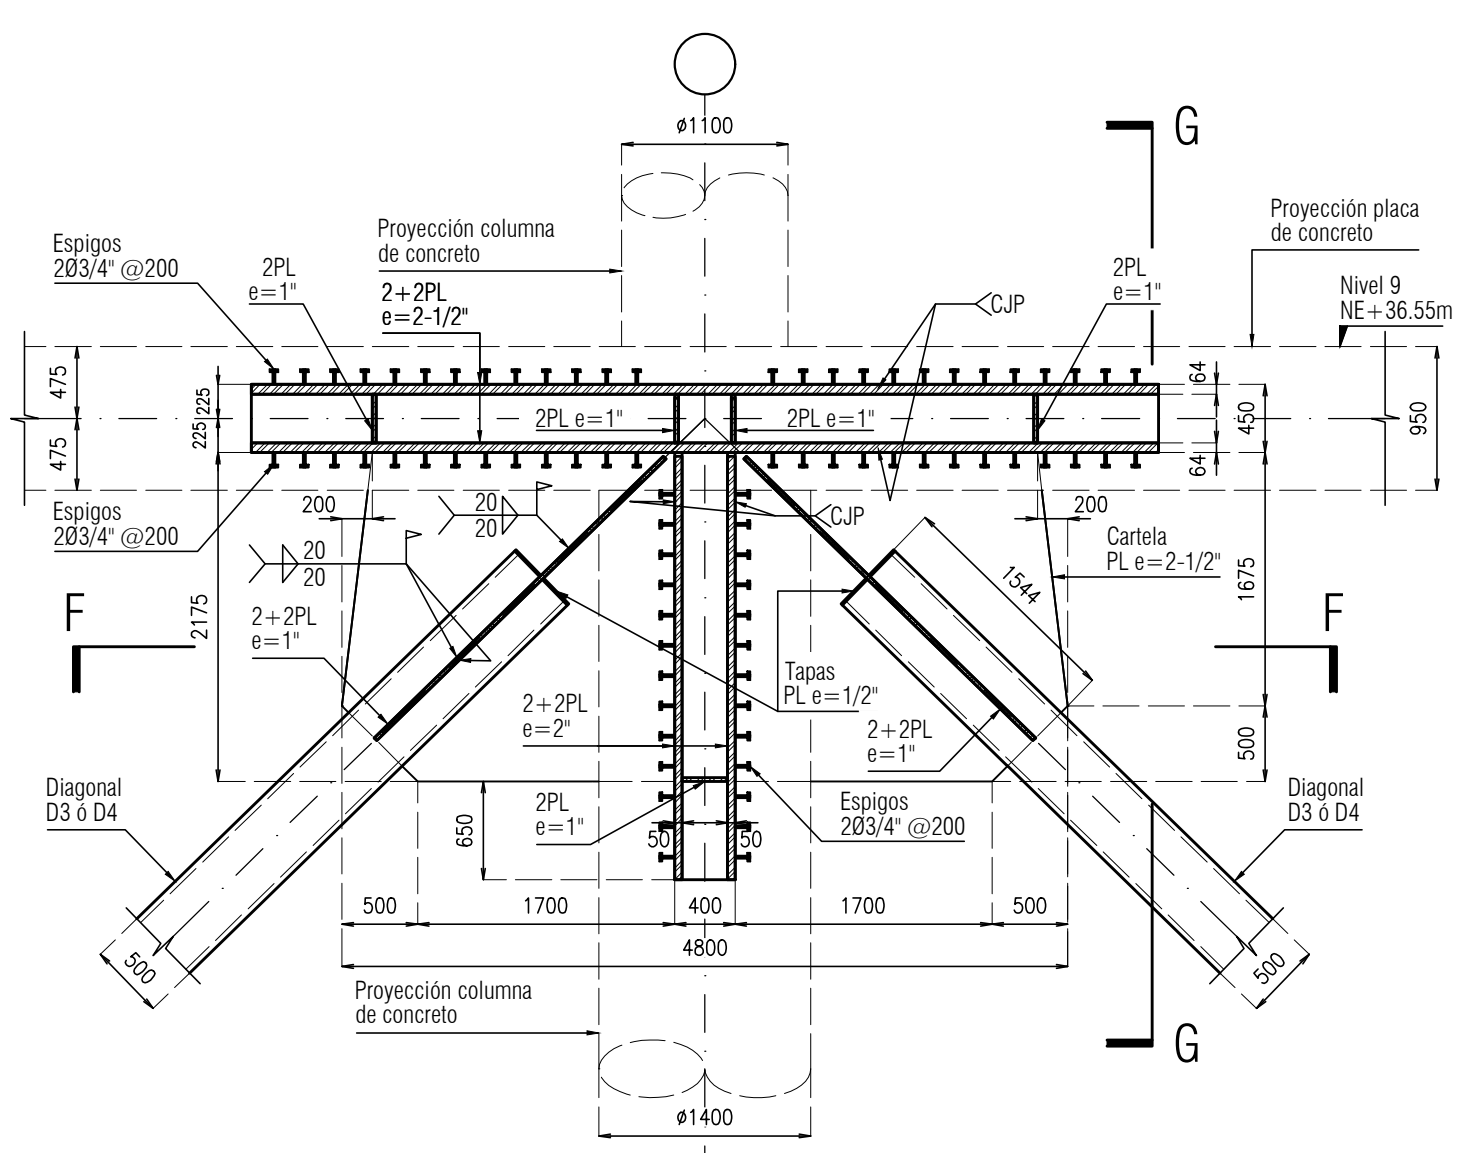


Corte H-H
escala 1:50

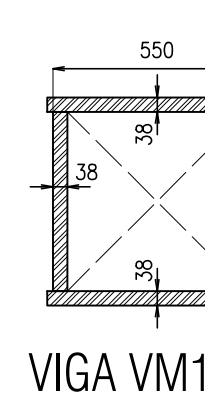


VIGA VM1
escala 1:20

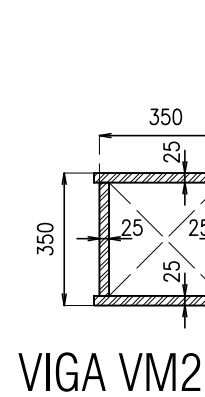


VIGA VM2
escala 1:20

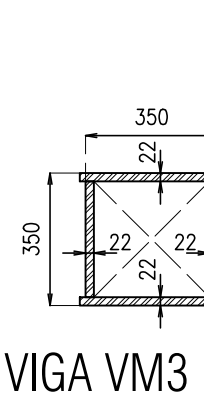


VIGA VM3
escala 1:20

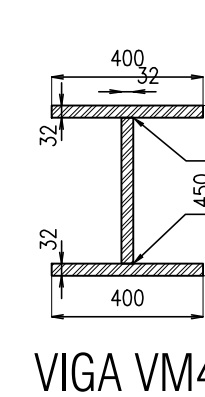

VIGA VM4
escala 1:20

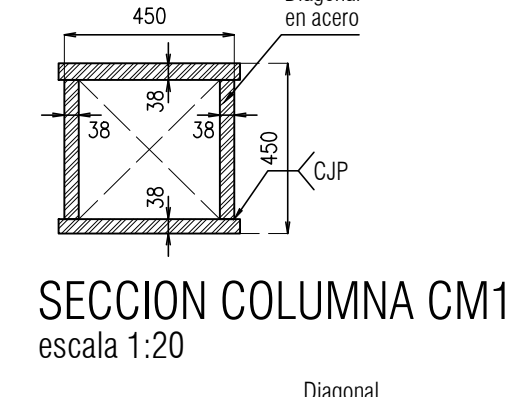


SECCION COLUMNA CM1
escala 1:20

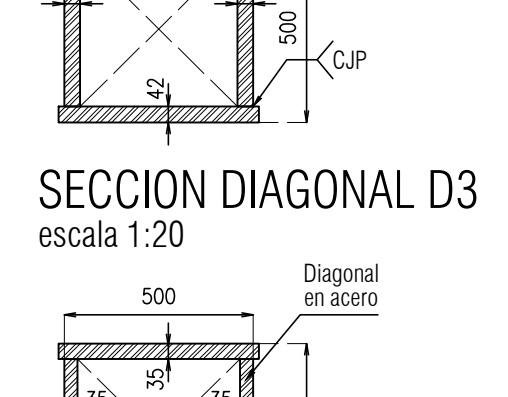


SECCION DIAGONAL D3
escala 1:20




SECCION DIAGONAL D4
escala 1:20

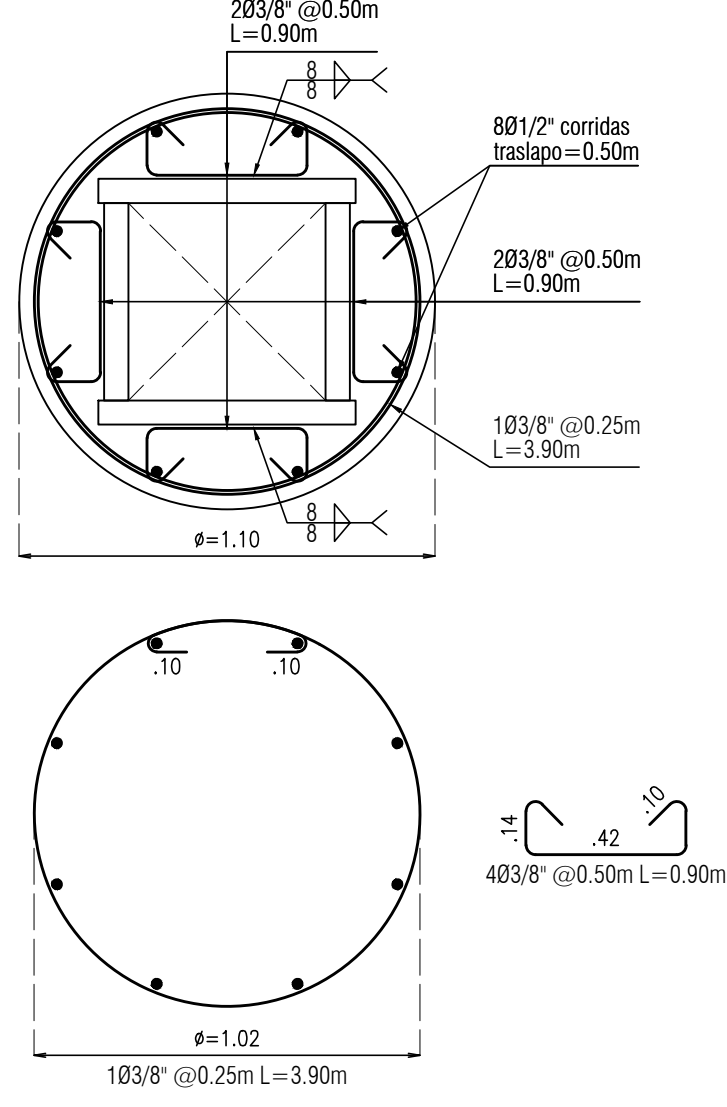


REFUERZO CAMISA DIAGONALES
D1 Y D2
escala 1:20

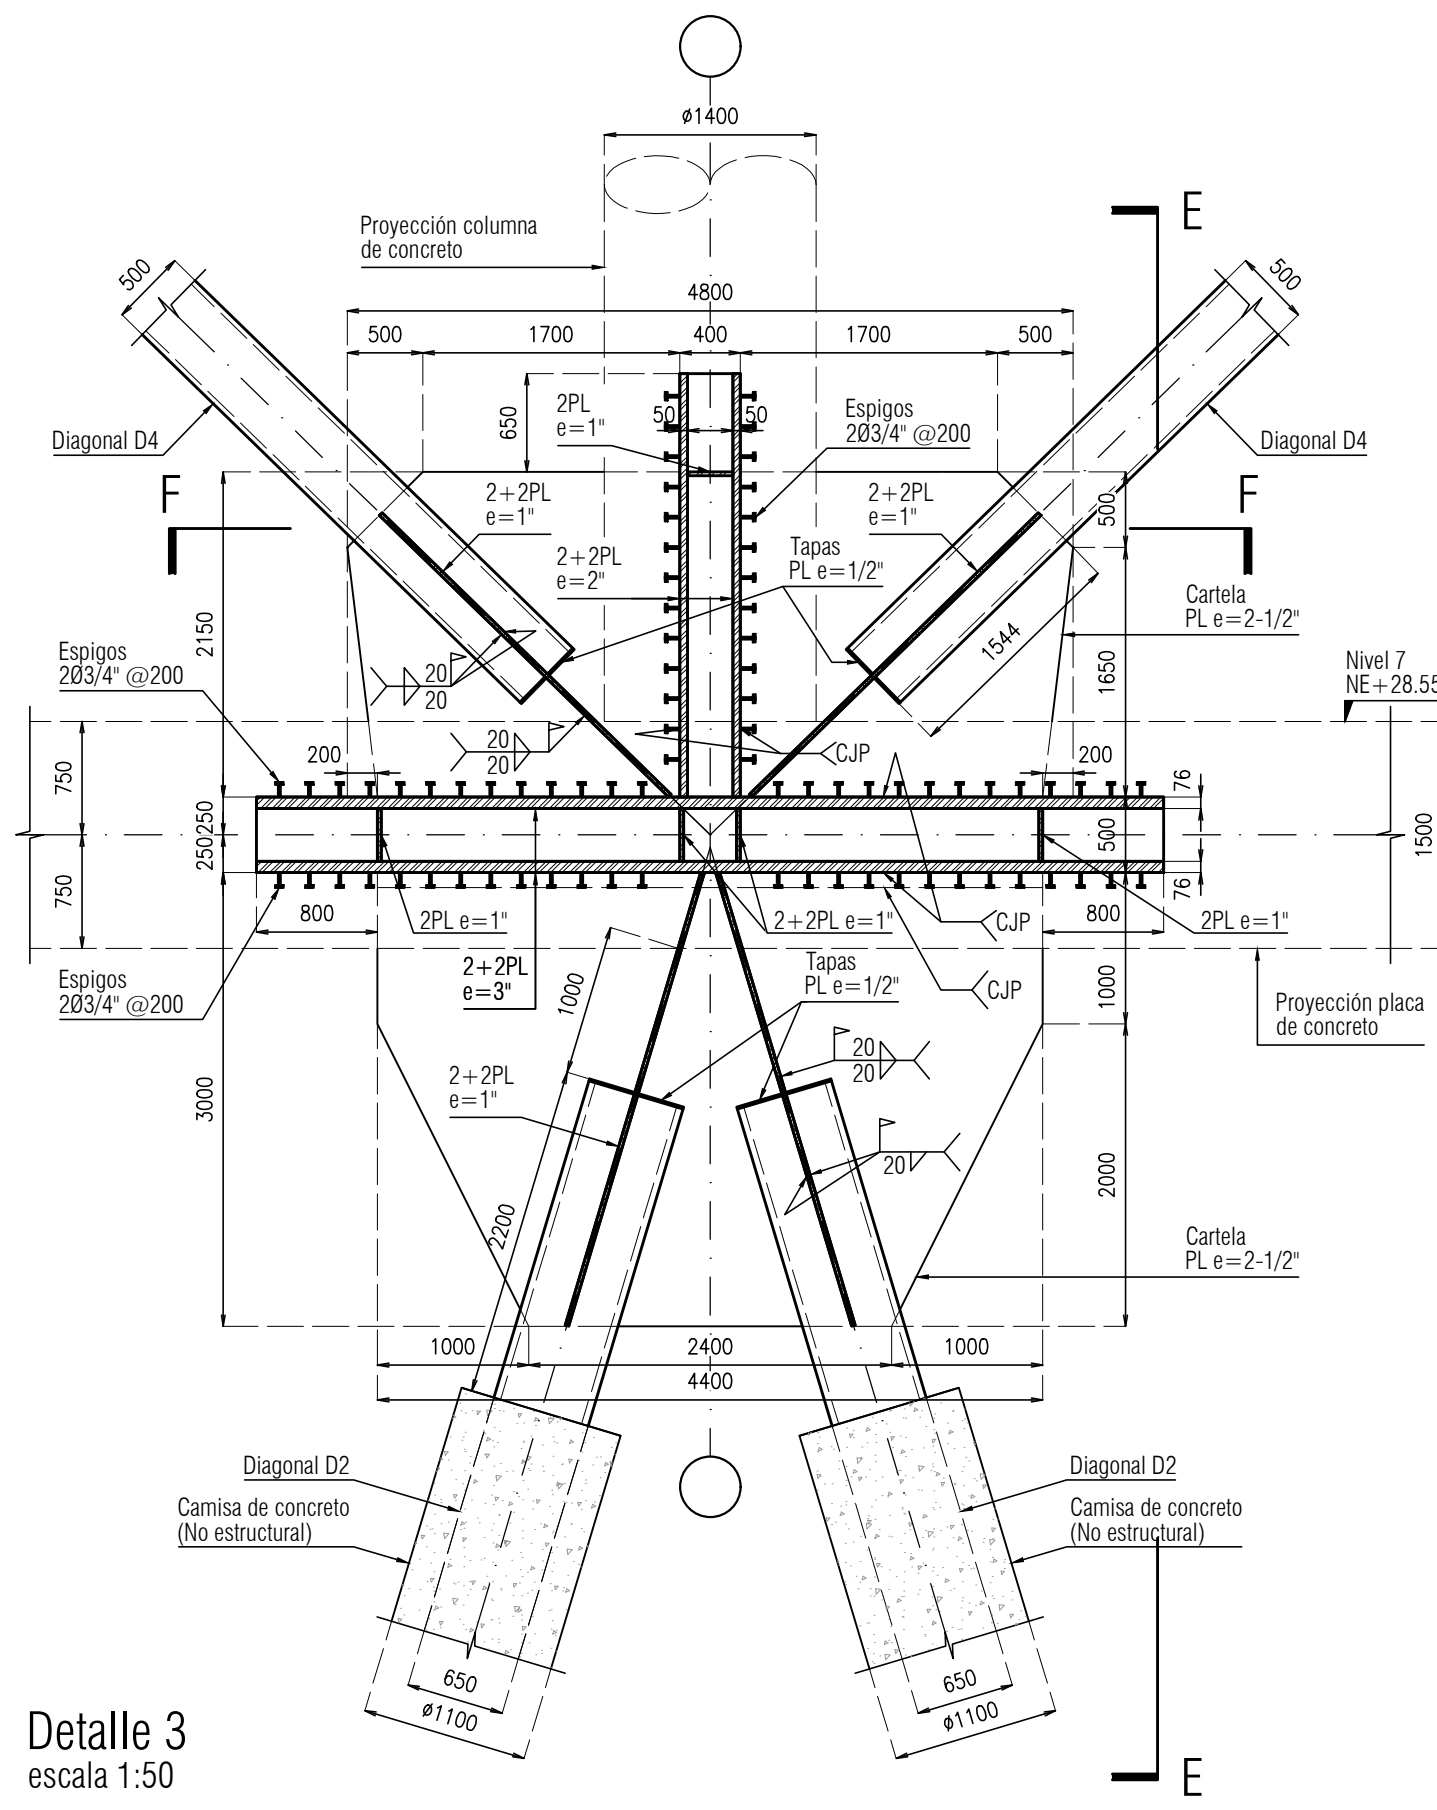


Detalle 3
escala 1:50

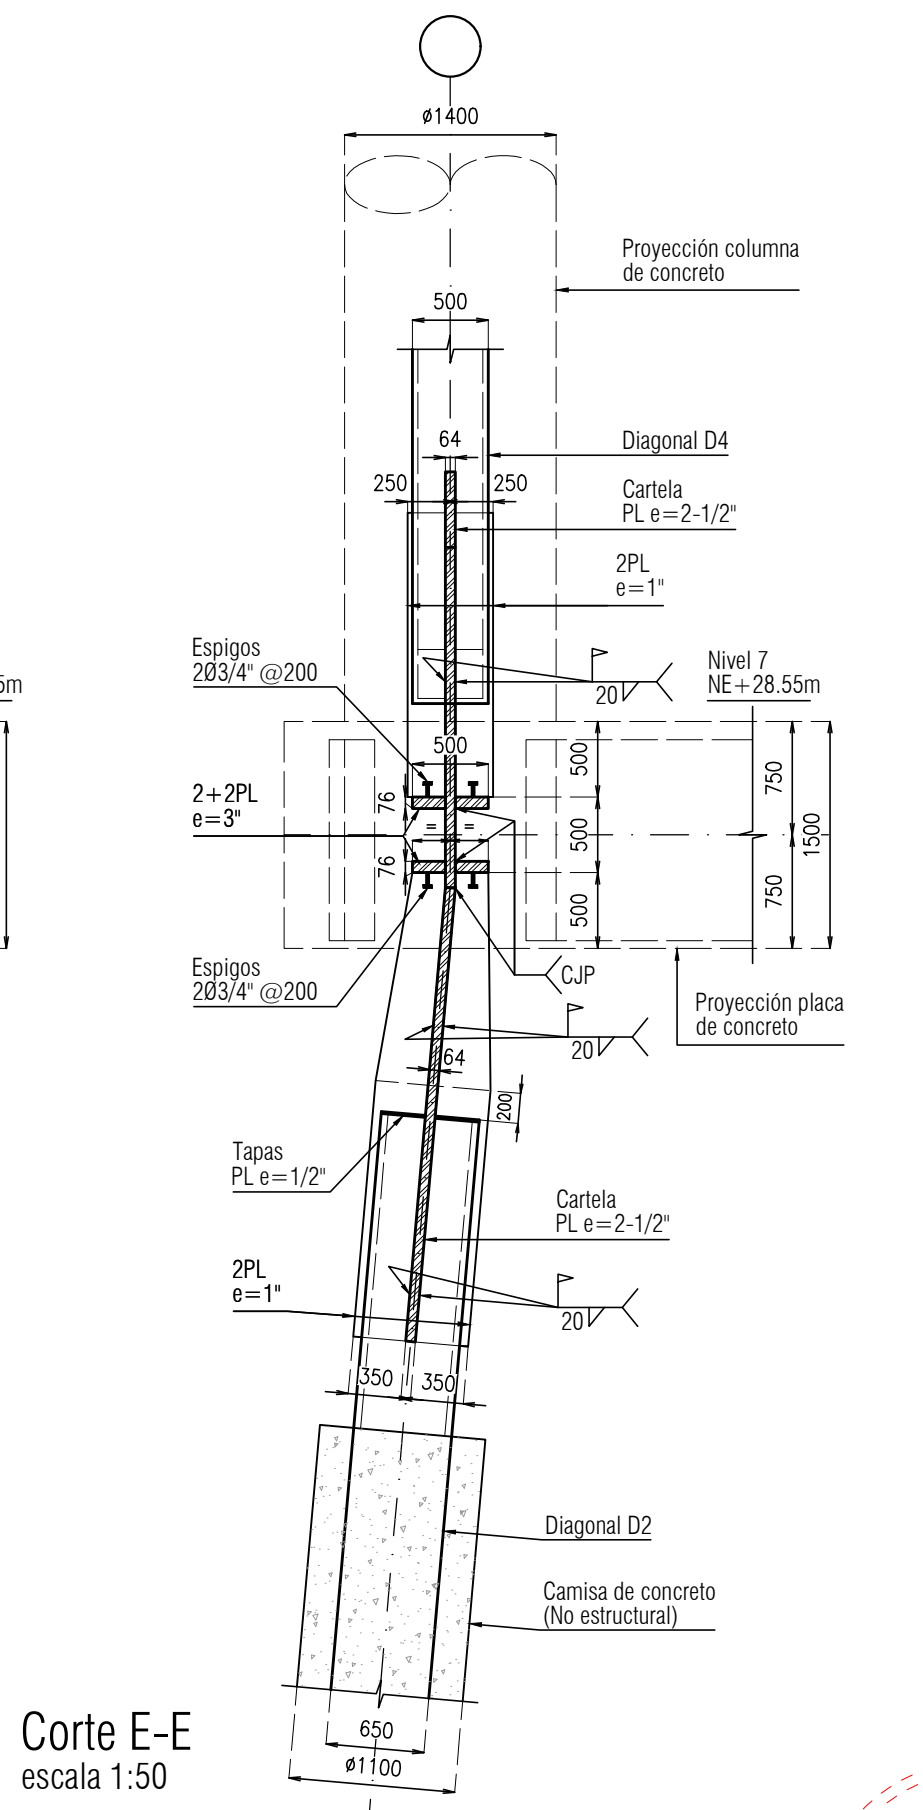


Corte E-E
escala 1:50

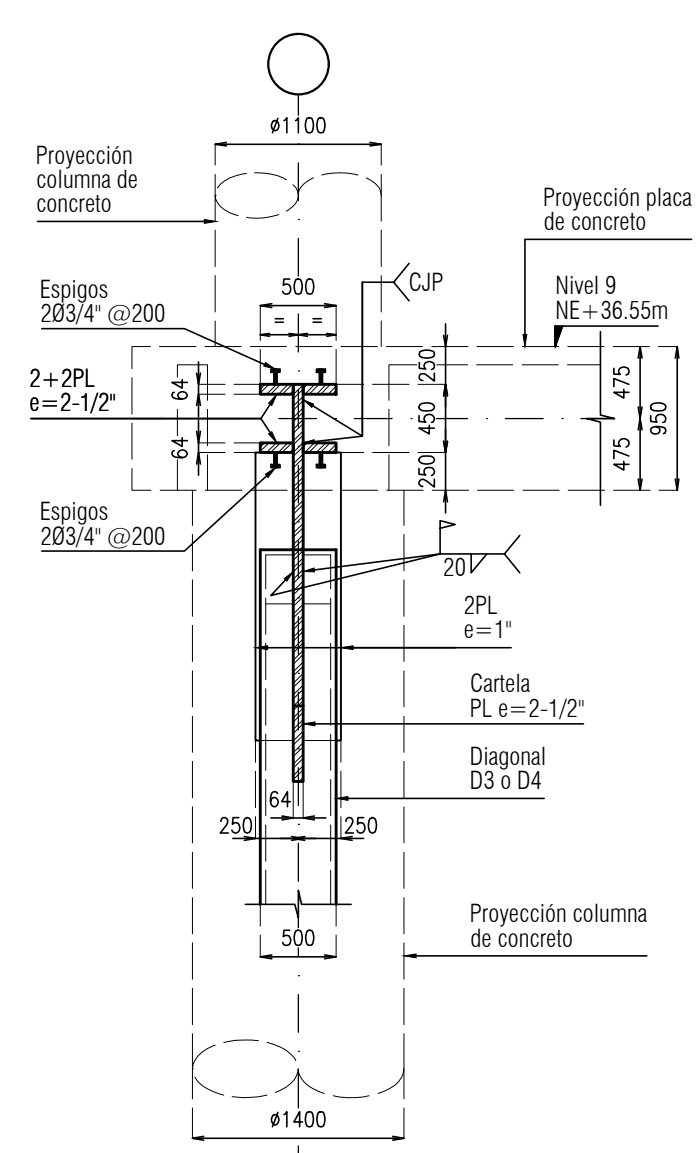


Corte G-G
escala 1:50

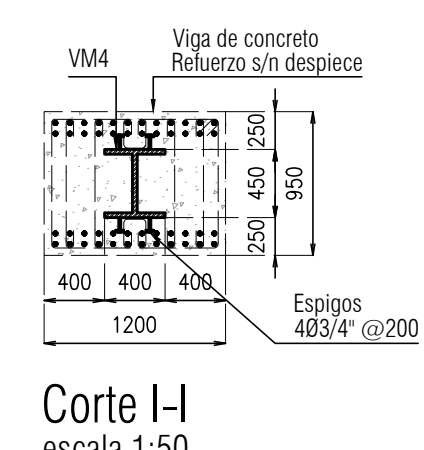

Corte I-I
escala 1:50

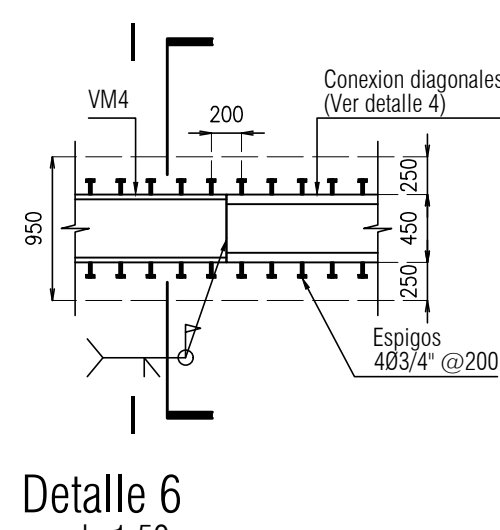

Detalle 6
escala 1:50

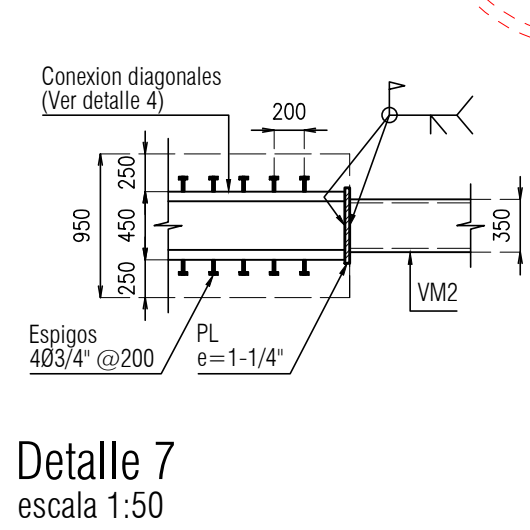

Detalle 7
escala 1:50

NOTAS IMPORTANTES:

- Ver especificaciones de materiales en plano CTIB_CNI_EST_000_GEN_XXX
- Los presentes planos son de diseño. El fabricante de la estructura metálica debe elaborar los respectivos planos de taller, los cuales deben ser revisados y aprobados por la interventoría y la supervisión técnica de la obra.
- En los detalles se indican cantidad y diámetro de pernos de conexión.
- Ver detalles 2A y 8 en plano CTIB_CNI_EST_513_DET_XXX.

AA	15-06-2023	Ingeniería básica
AB	04-08-2023	Anteproyecto
AC	01-11-2023	Anteproyecto V2 50%
AD	15-12-2023	Anteproyecto V2 100%
DD	13-03-2024	Entrega curaduría
EE	10-05-2024	Proyecto Final 100%
EF	31-05-2024	Respuesta Obs 100%
FF	21-06-2024	Entrega Final
01	28-07-2024	ENTREGA FINAL

Curaduría	☐	Coordinación	☐
Revisión	☐	Construcción	☐
Entrega Cliente	☒		

Nivel 24	
Nivel 23	
Nivel 22	
Nivel 21	
Nivel 20	
Nivel 19	
Nivel 18	
Nivel 17	
Nivel 16	
Nivel 15	
Nivel 14	
Nivel 13	
Nivel 12	
Nivel 11	
Nivel 10	
Nivel 9	
Nivel 8	
Nivel 7	
Nivel 6	
Nivel 5	
Nivel 4	
Nivel 3	
Nivel 2	
Nivel 1	
Nivel 0	

