




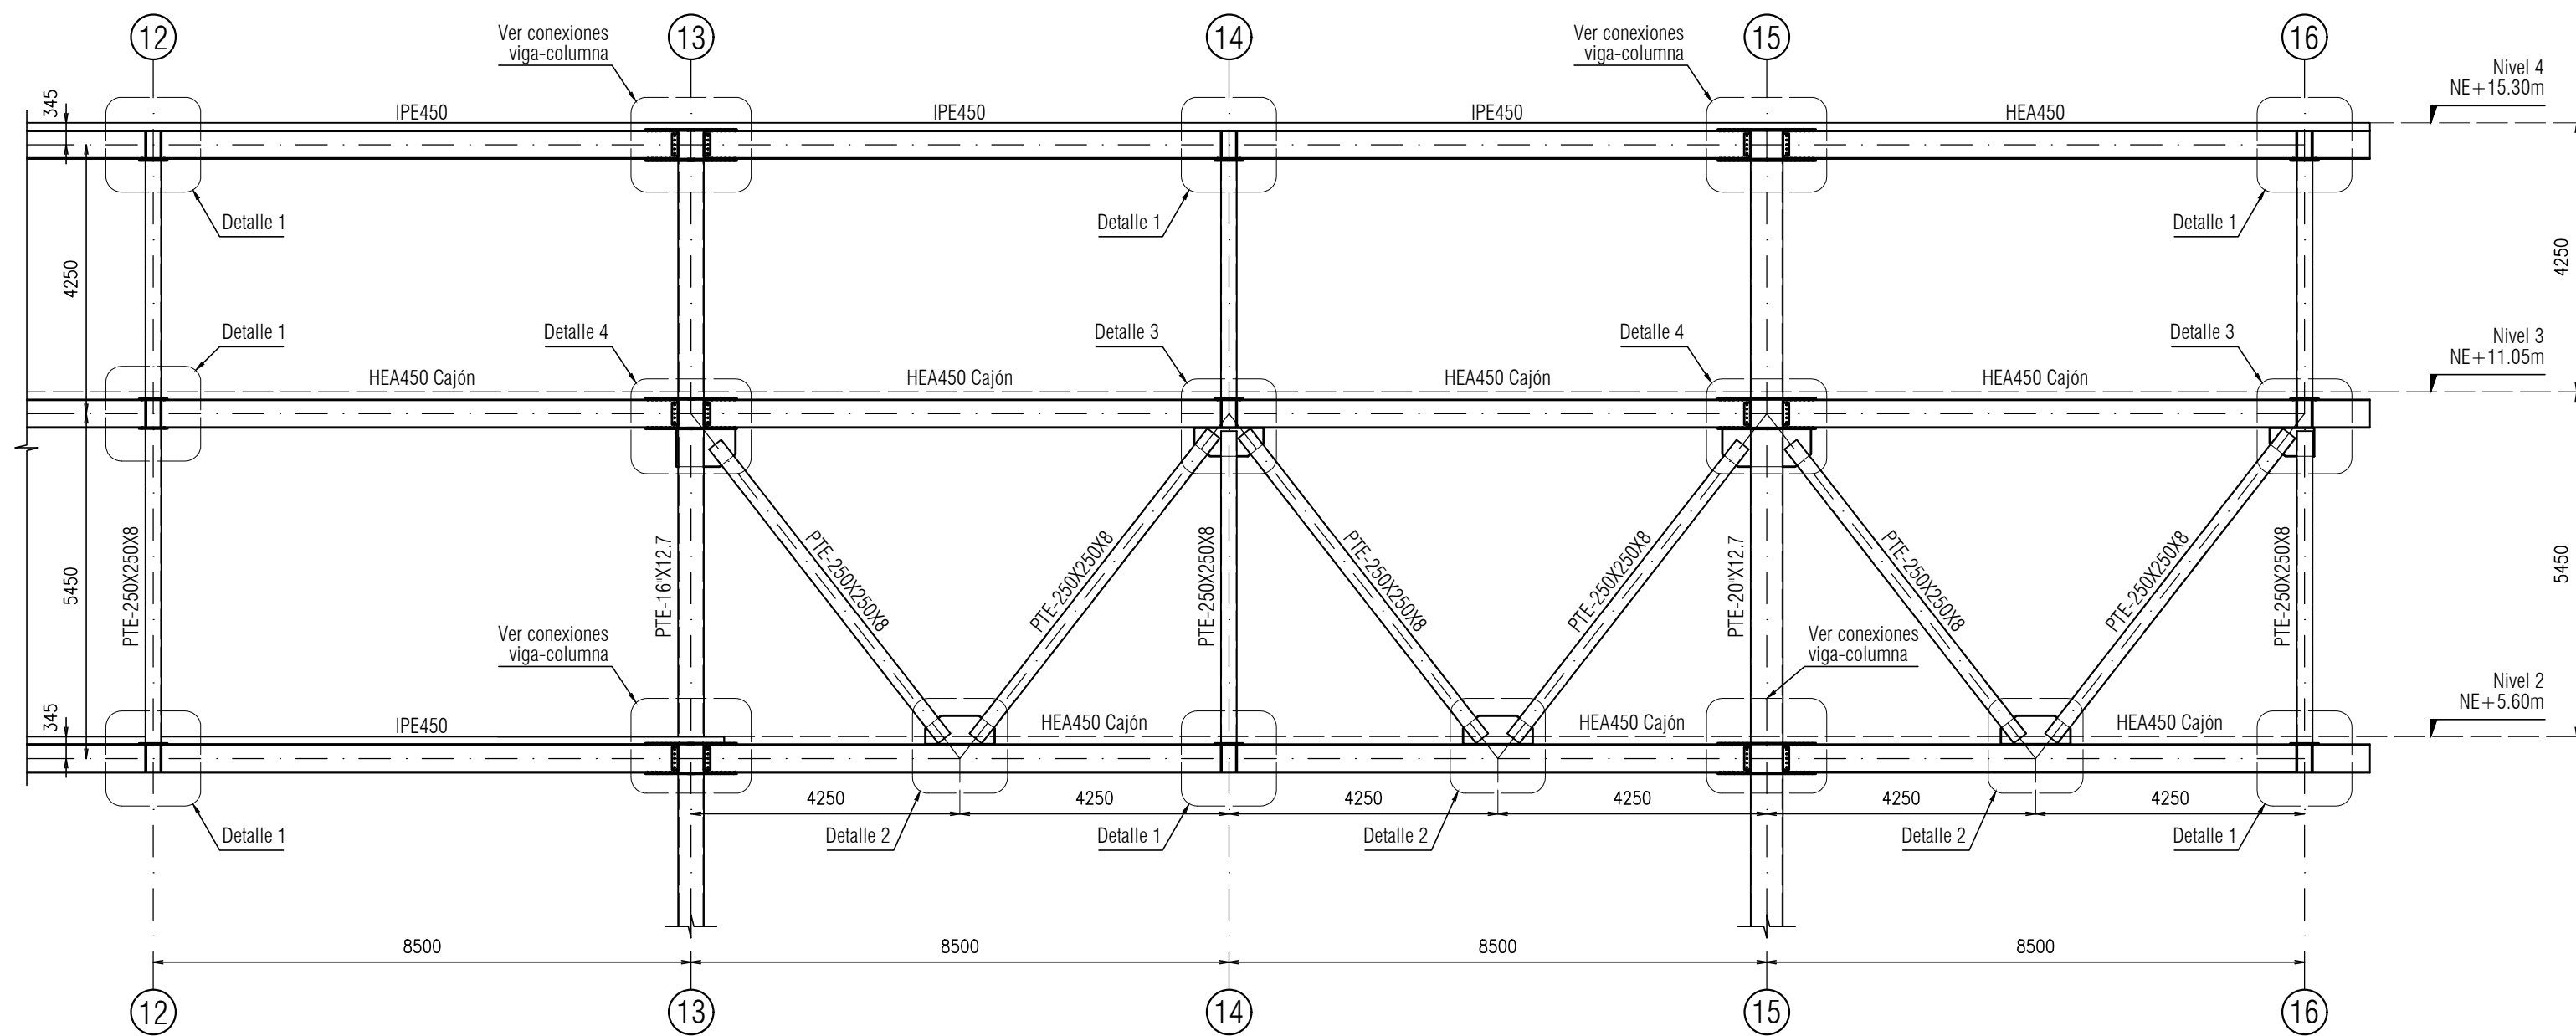


ALZADO FACHADA EJE N
escala 1:100

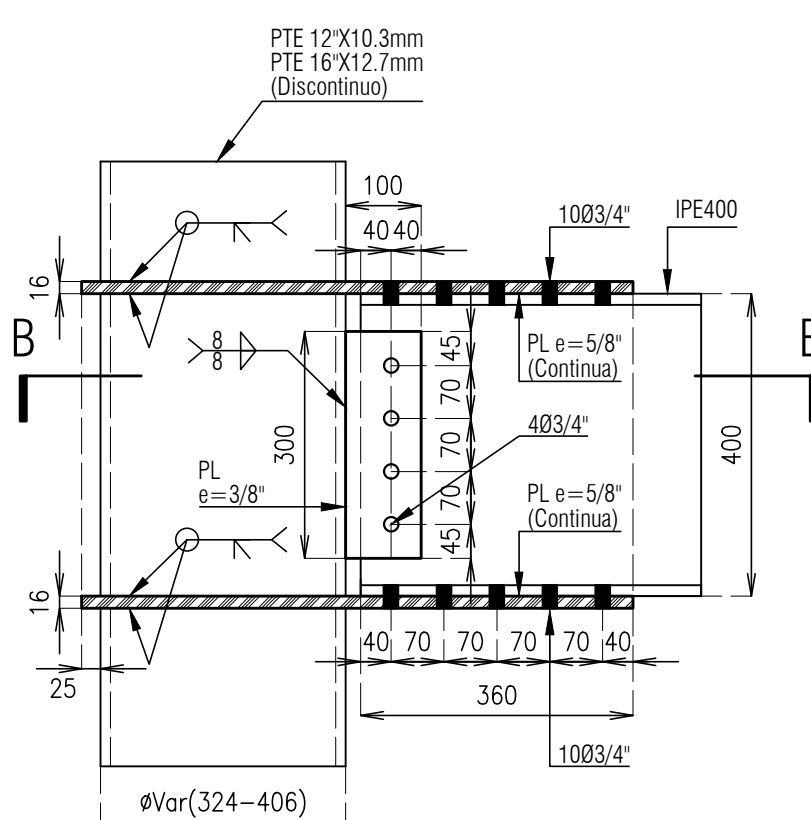


Conexión IPE400 a Columna
escala 1:10

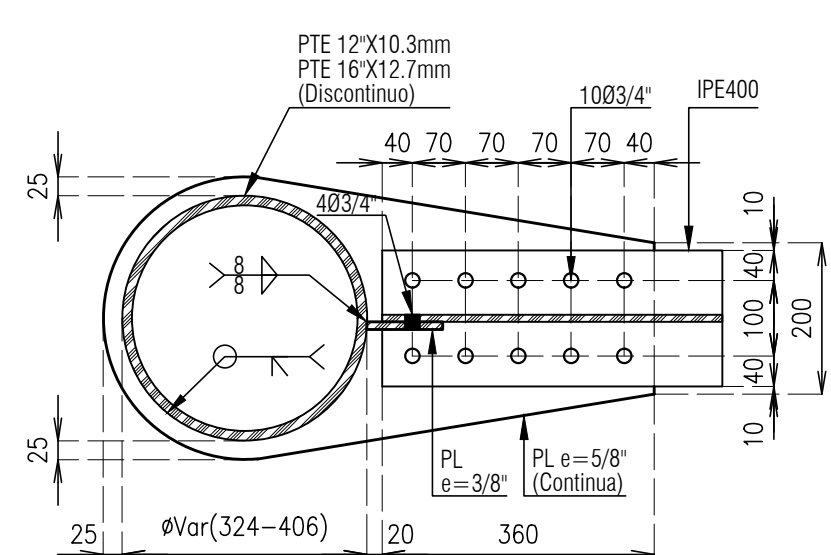


Corte B-B
escala 1:10

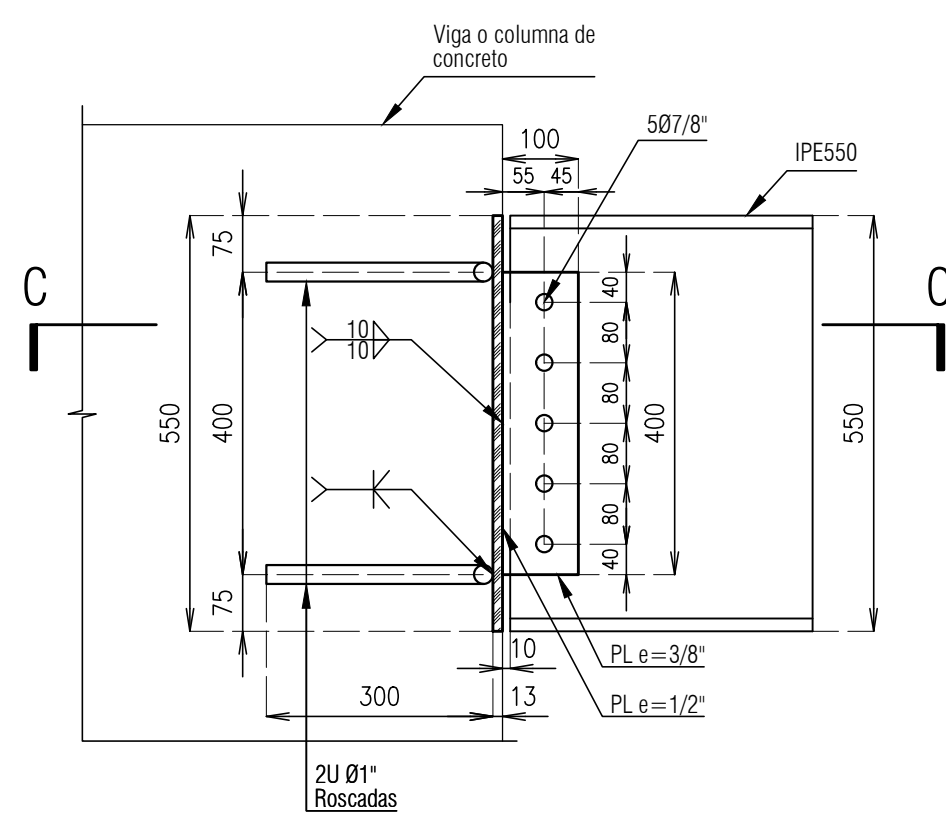


Conexión IPE550 a Concreto (N5 a N7)
escala 1:10

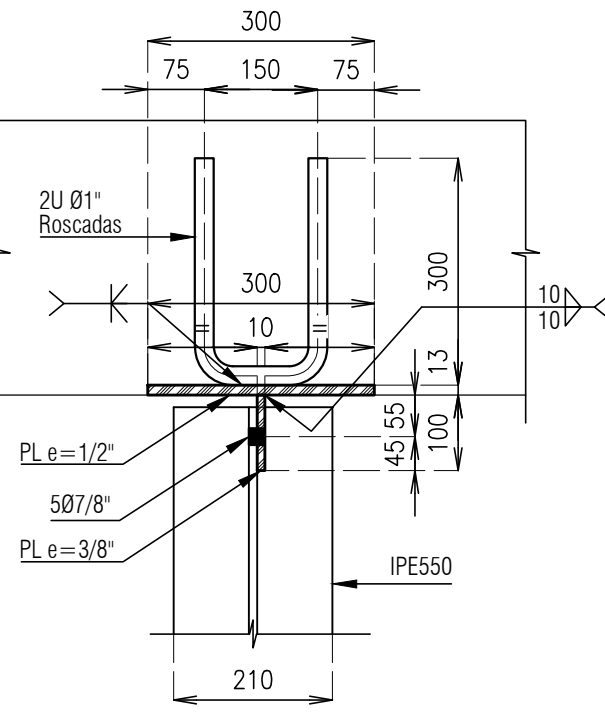


Sección C-C
escala 1:10

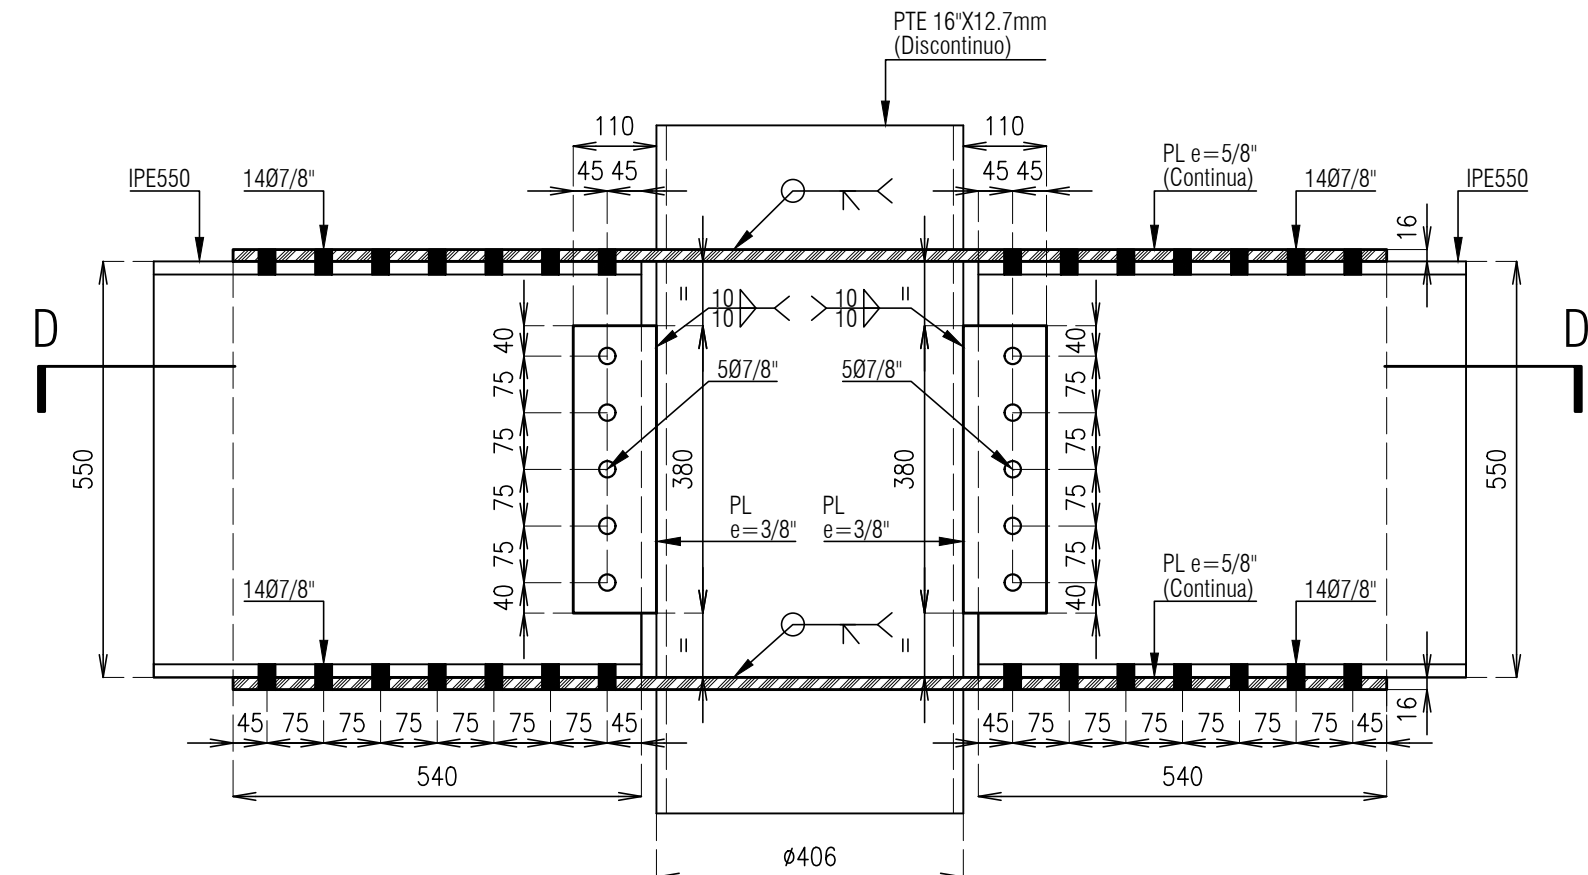


Conexión IPE550 a Columna
escala 1:10

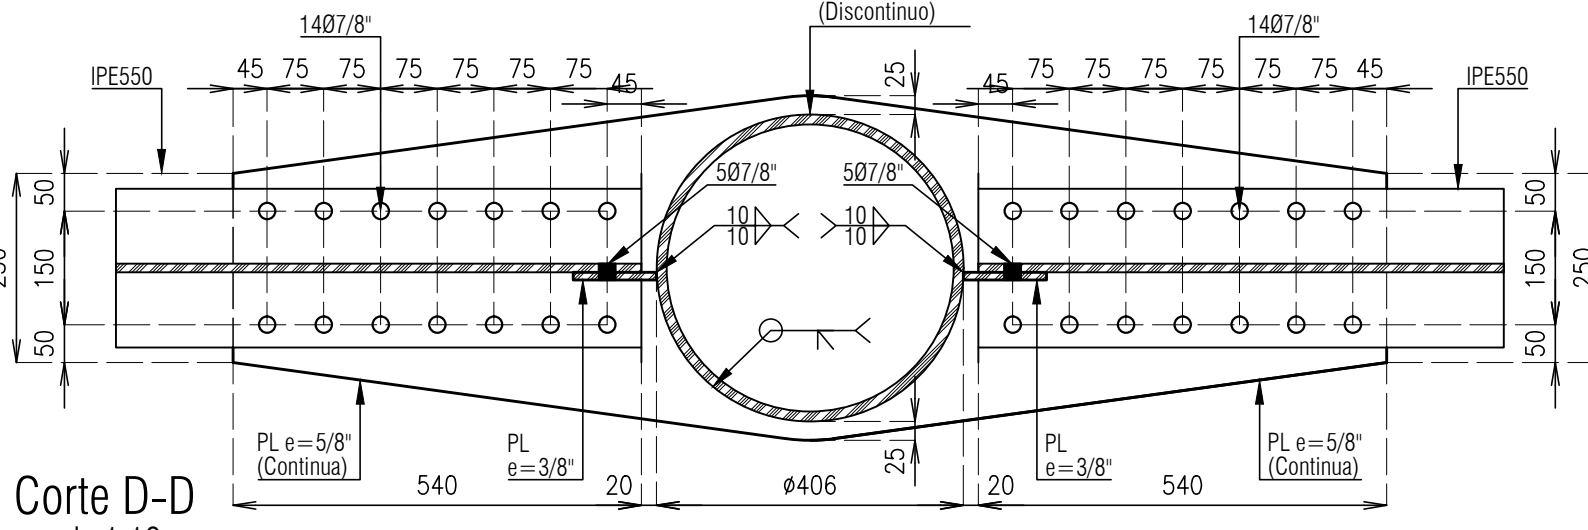


Corte D-D
escala 1:10

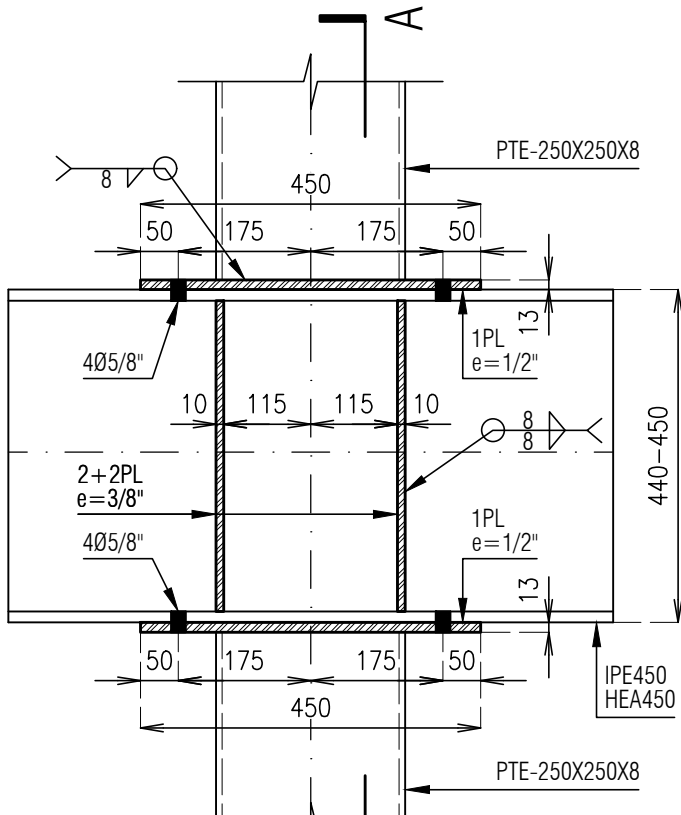


Detalle 1
escala 1:10

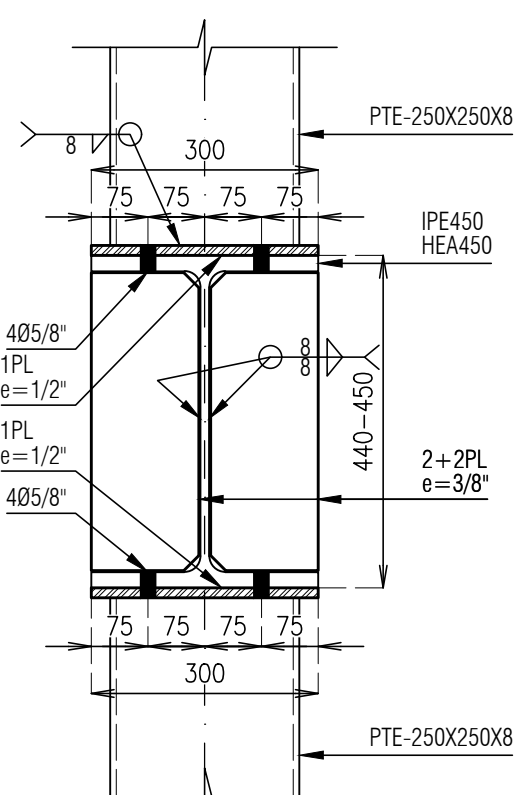


Corte A-A
escala 1:10

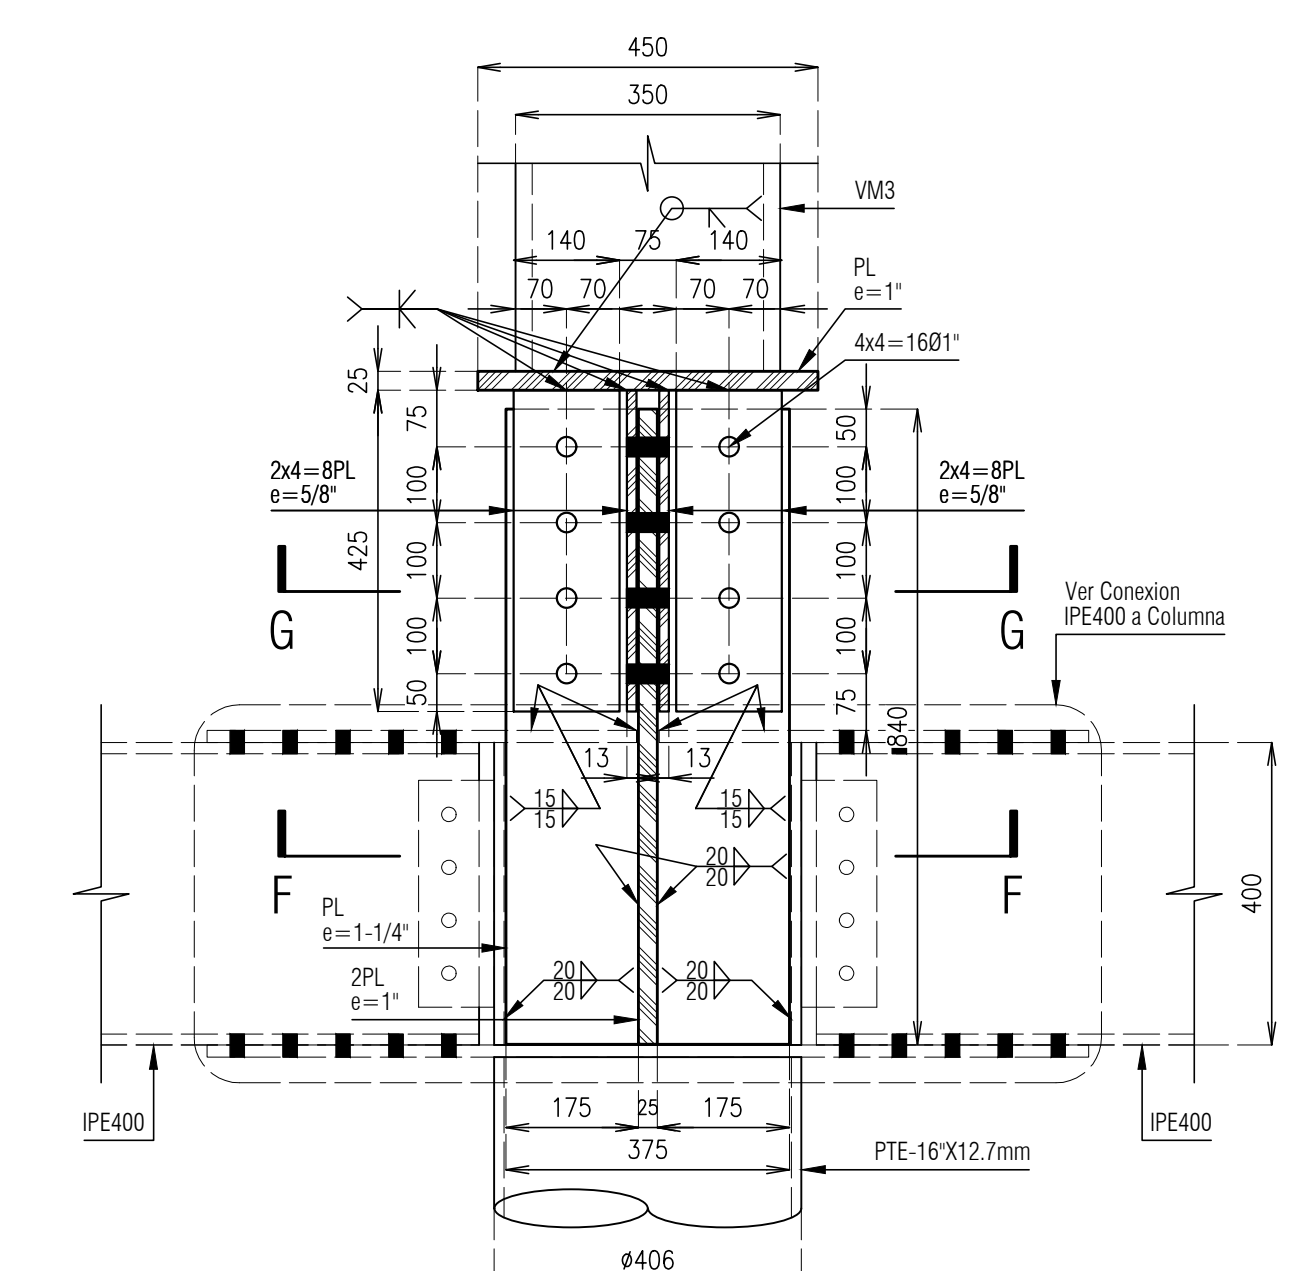


Conexión VM3 a Tensor PTE-16\"/>

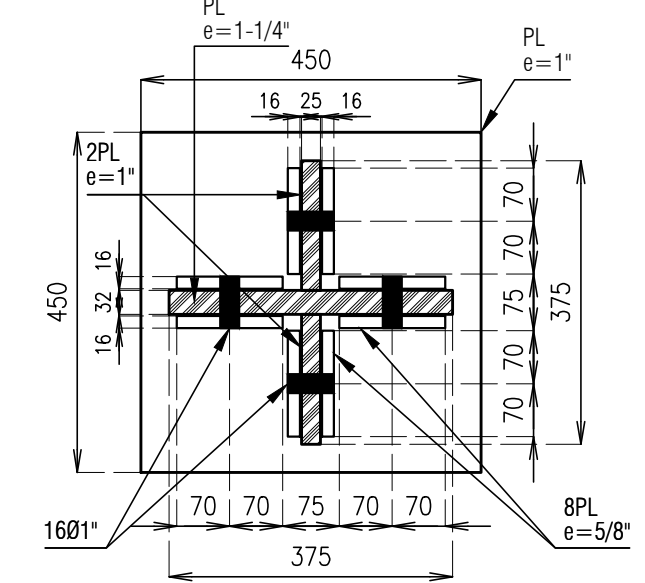


Sección G-G
escala 1:10

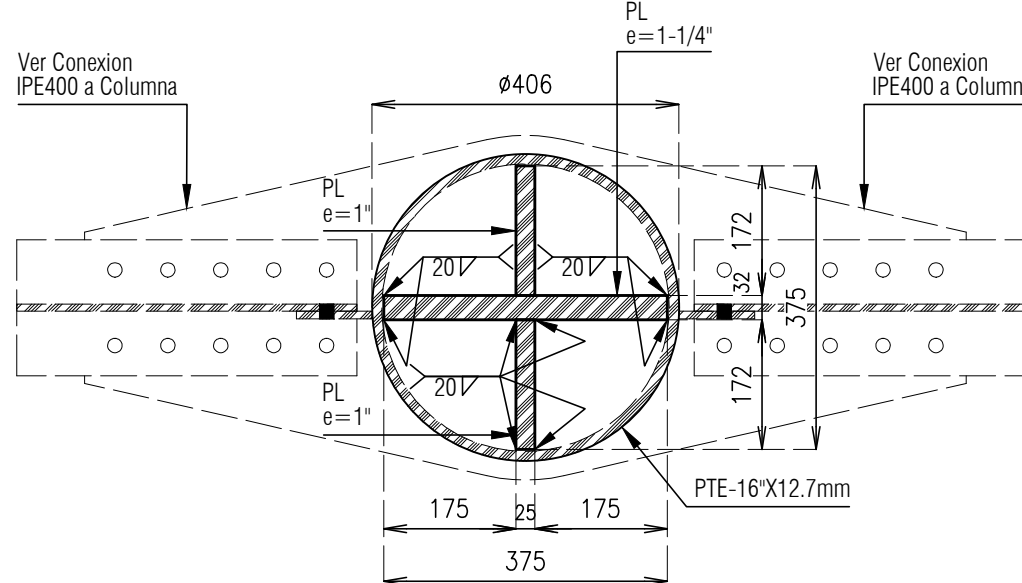


Sección F-F
escala 1:10

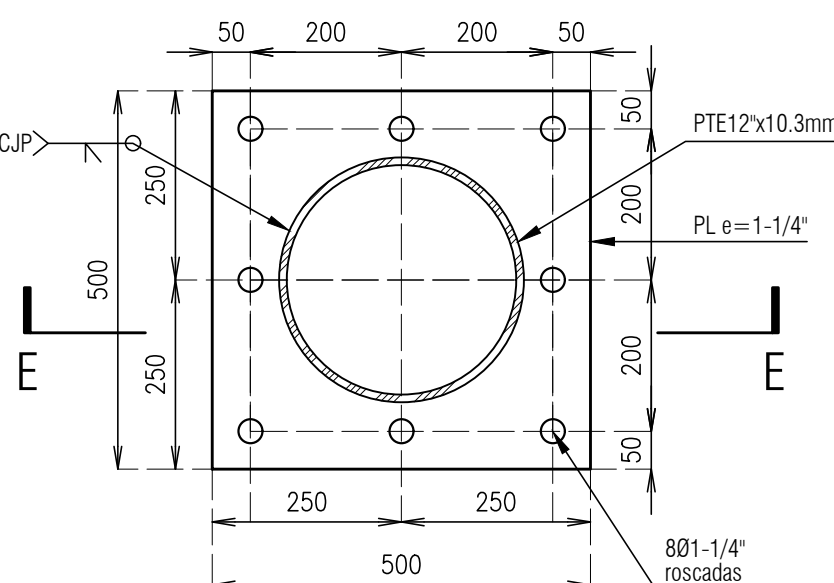


Placa Base Tensor PTE 12\"/>

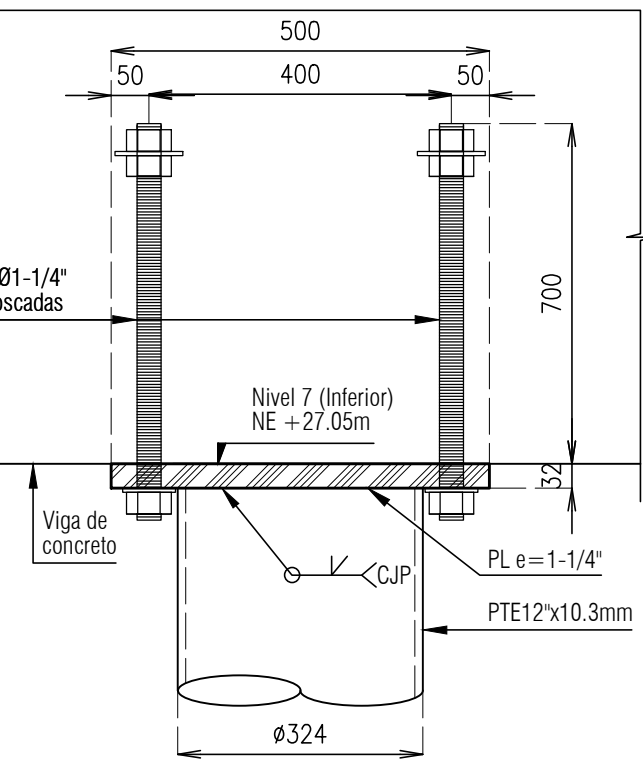


Sección E-E
escala 1:10

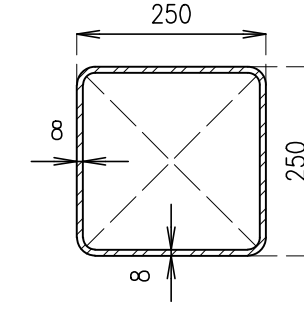


PTE-250X250X8
escala 1:10

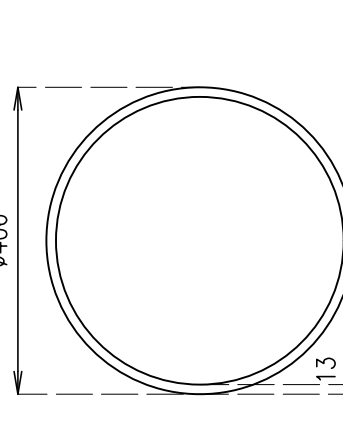


PTE 16\"/>

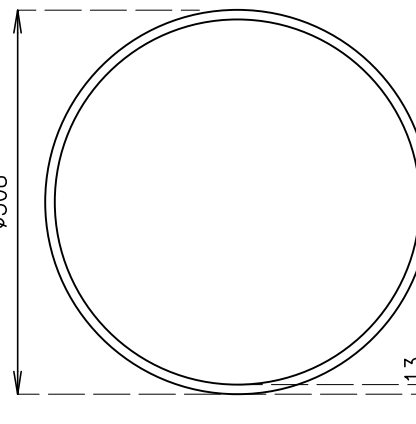


PTE 20\"/>

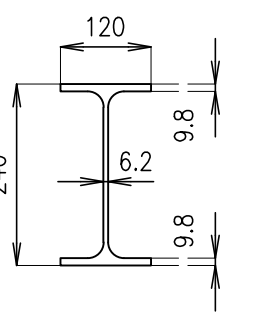


Sección IPE240
escala 1:10

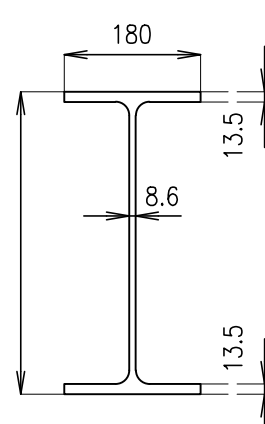


Sección IPE400
escala 1:10

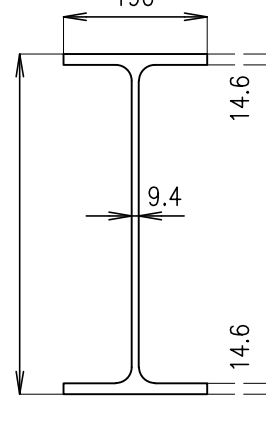


Sección IPE450
escala 1:10

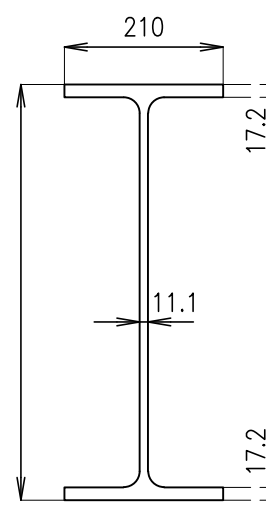

Sección IPE550
escala 1:10

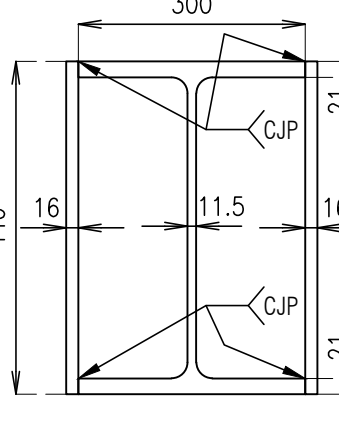

HEA450 Cajón
escala 1:10

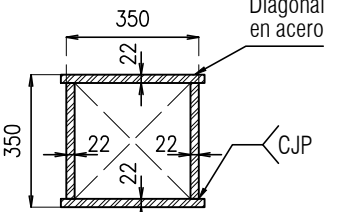

SECCION VIGA VM3
escala 1:20

CTIB

Campus de Ciencia, Tecnología e
Innovación de Bogotá - Región

corferias
Generadores de
Oportunidades y Progreso

Cámara
de Comercio
de Bogotá
Secretaría Distrital de
Economía Financiera

ARQUITECTO COORDINADOR

ELEQUIPO
MAZZANTI + Gensler

DISÑO ESTRUCTURAL

CNI

ING. NICOLÁS PARRA GARCÍA
MAT. 232021 148063 QND

INTERVENTORIA

GUTIERREZ DÍAZ S.A.S.
SUPERVISOR Y LABORATORIO PROYECTOS DE CONSTRUCCIÓN

Director de Interventoría: Ing. Jorge Iván García Mancilla
Mat. 632021 148063 QND

Versión Emisión Descripción

AA	15-06-2023	Ingeniería básica
AB	04-08-2023	Anteproyecto
AC	01-11-2023	Anteproyecto V2 50%
AD	15-12-2023	Anteproyecto V2 100%
DD	13-03-2024	Entrega curaduría
EE	10-05-2024	Proyecto Final 100%
EF	31-05-2024	Respuesta Obs 100%
FF	21-06-2024	Entrega Final
01	28-07-2024	ENTREGA FINAL


PROYECTO:
CAMPUS DE CIENCIA TECNOLOGÍA E
INNOVACIÓN DE BOGOTÁ
MAT. No. 502-00252470

FASE
ENTREGA FINAL

PROPÓSITO DE EMISIÓN
Curaduría ☐ Coordinación ☐
Revisión ☐ Construcción ☐
Entrega Cliente ☒

ZNIFICACIÓN

Nivel 24	
Nivel 23	
Nivel 22	
Nivel 21	
Nivel 20	
Nivel 19	
Nivel 18	
Nivel 17	
Nivel 16	
Nivel 15	
Nivel 14	
Nivel 13	
Nivel 12	
Nivel 11	
Nivel 10	
Nivel 9	
Nivel 8	
Nivel 7	
Nivel 6	
Nivel 5	
Nivel 4	
Nivel 3	
Nivel 2	
Nivel 1	
Nivel B1	
Nivel B2	

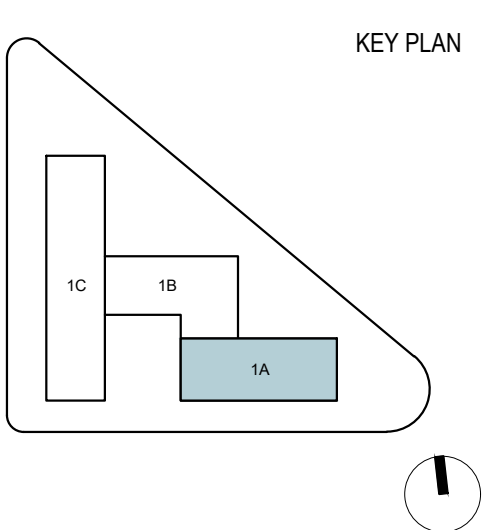

Fecha: 28-07-2024

Escala: As Indicated

DETALLES DE
CONEXIONES
CTIB_CNI_EST_514_DET_XXX_01