


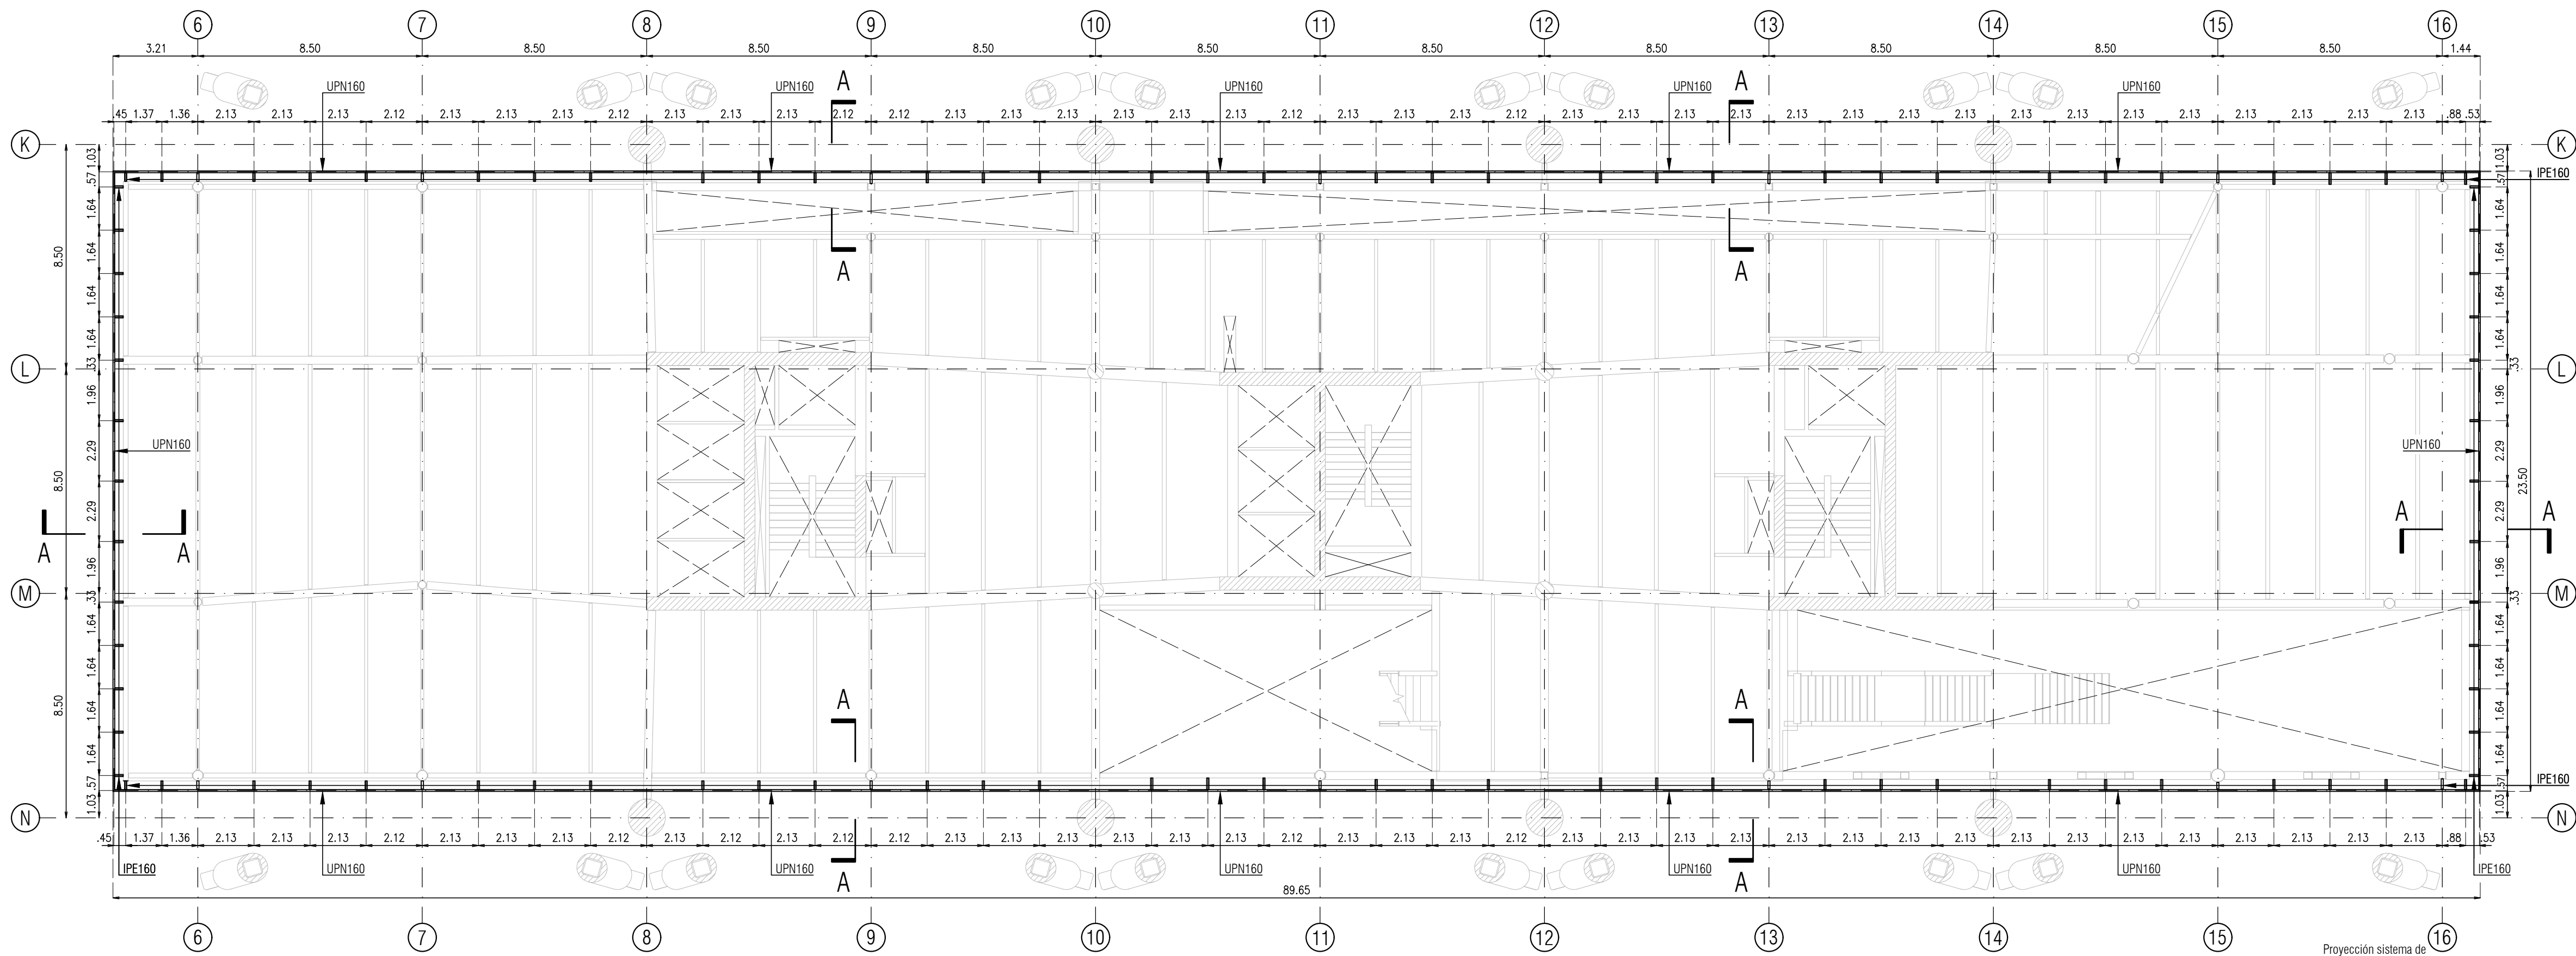


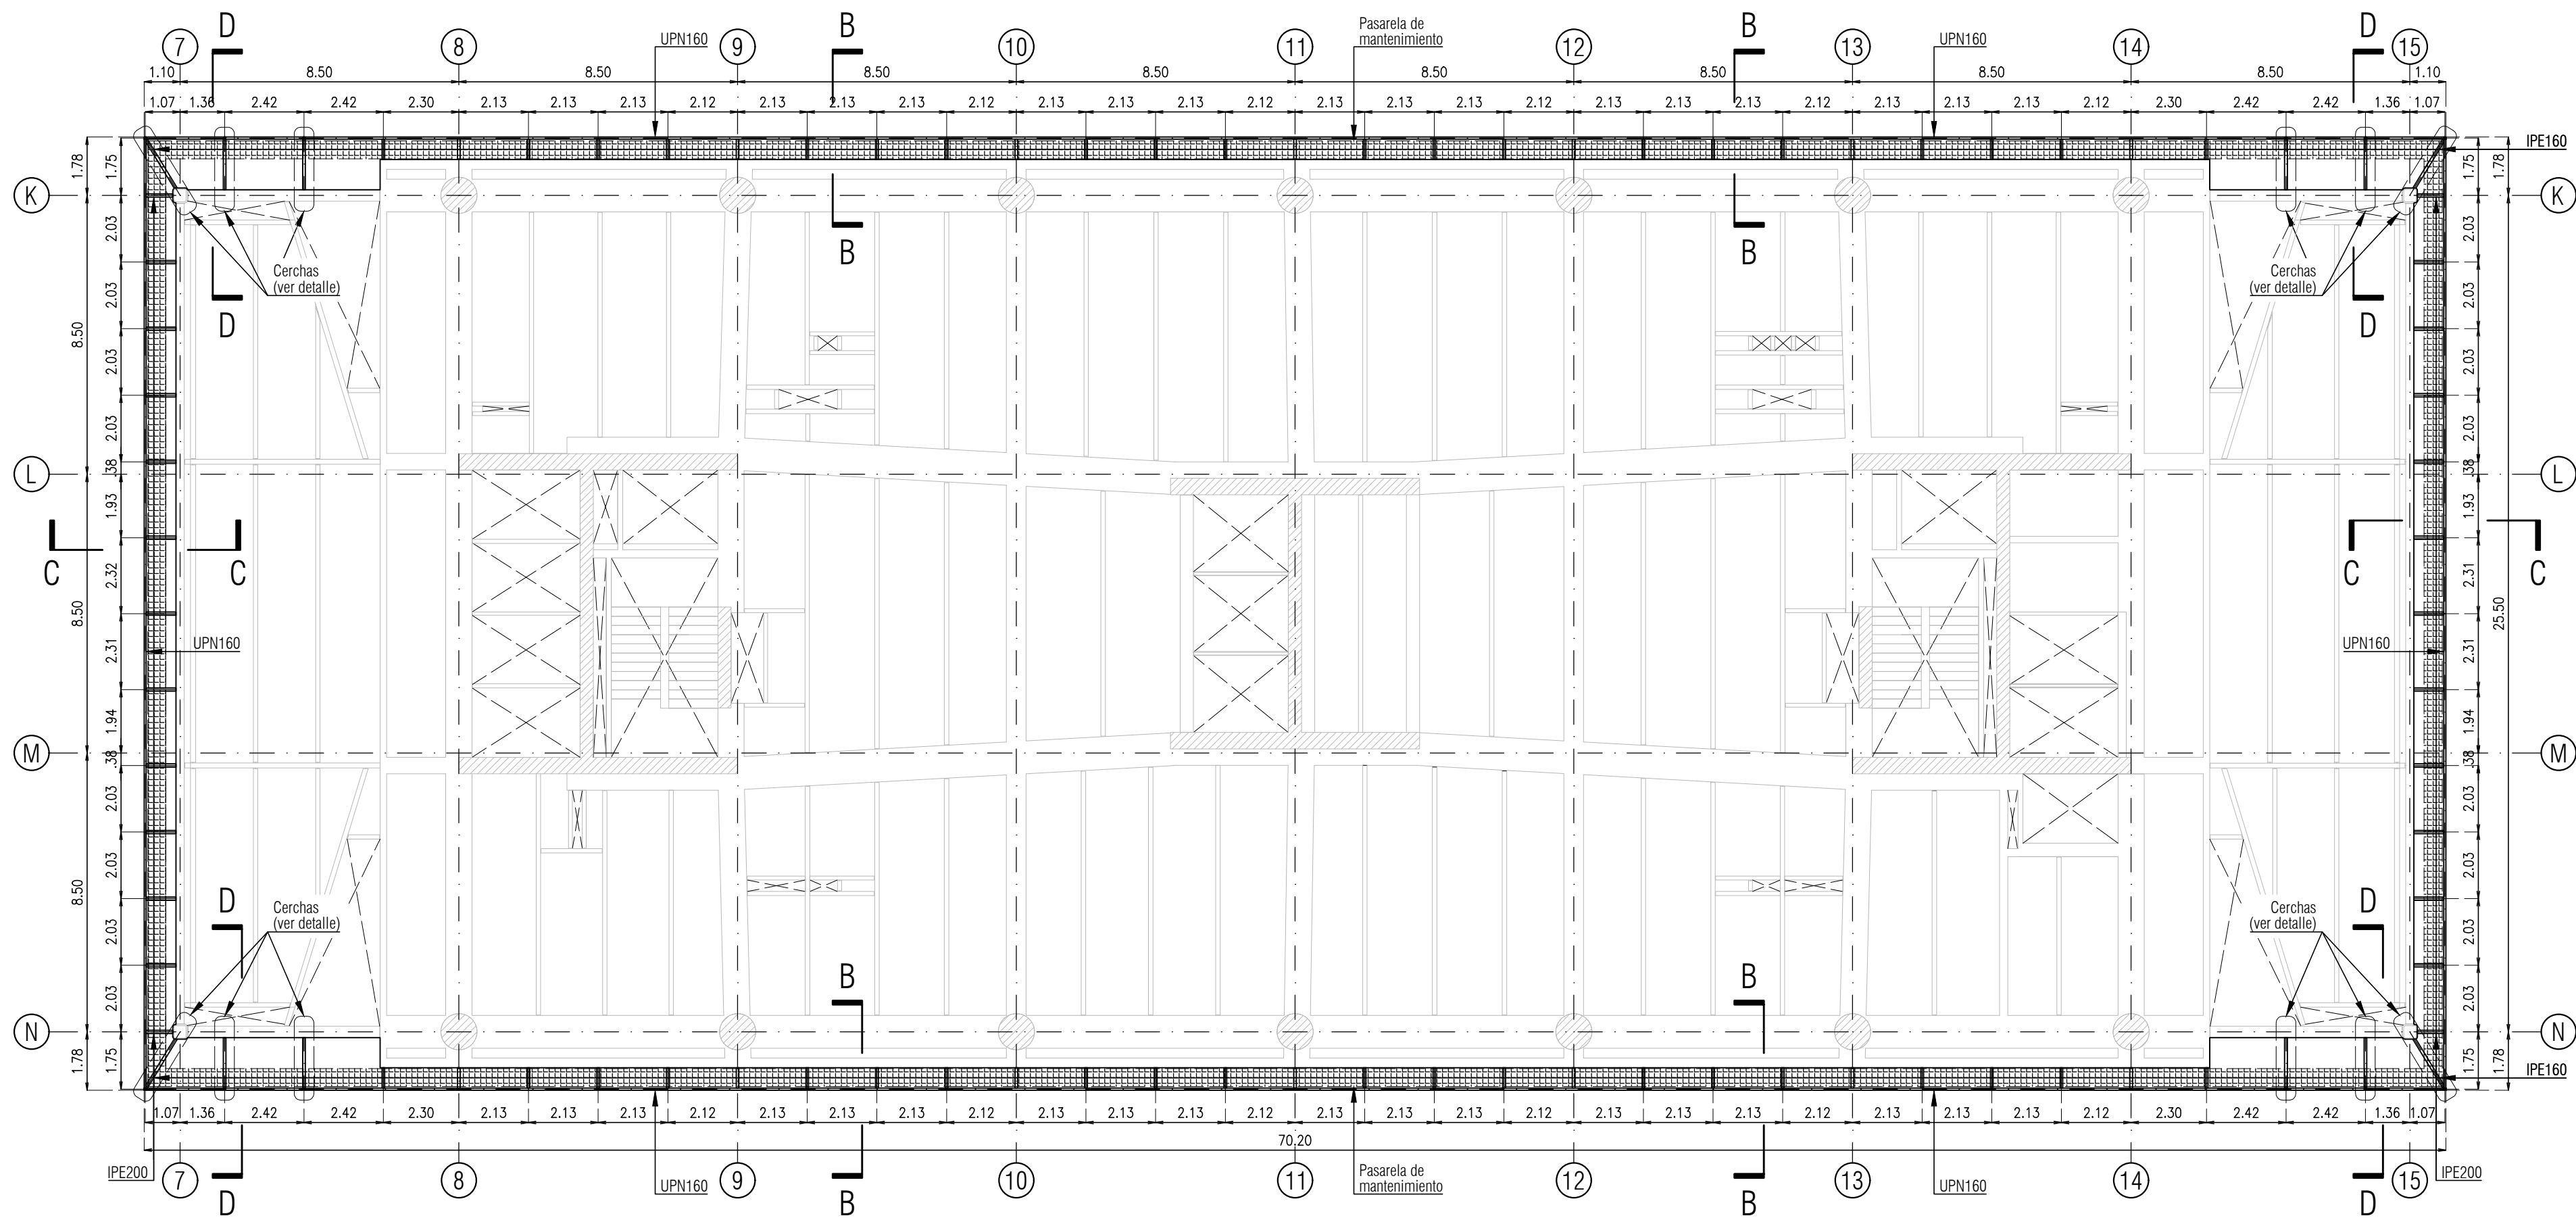

Subestructura de Fachada Niveles 2 a 4
escala 1:150

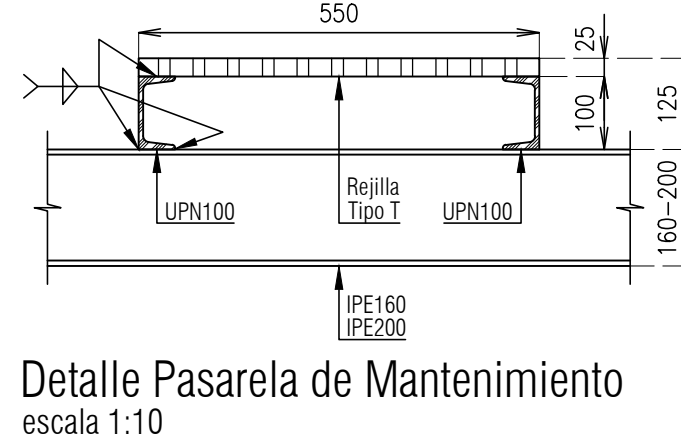


Subestructura de Fachada Niveles 7 a Terraza
escala 1:150

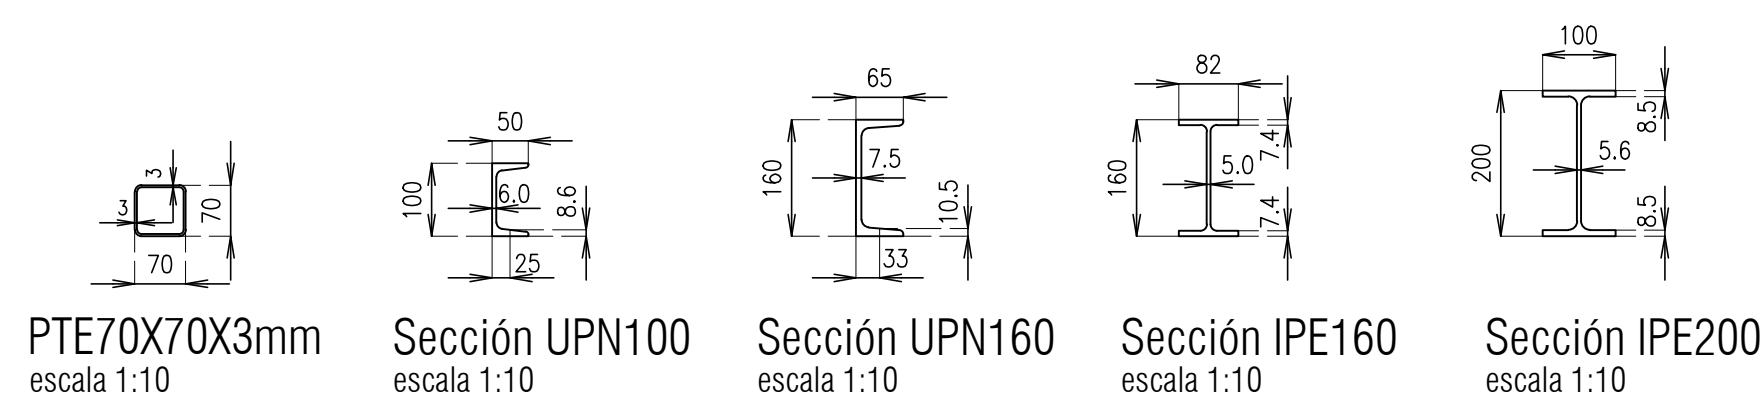


NOTAS IMPORTANTES:

- Ver detalles y especificaciones de sistema de fachada y de sus conexiones a la subestructura de soporte en planos arquitectónicos y/o del respectivo proveedor.
- Los presentes planos son de diseño. El fabricante de la estructura metálica debe elaborar los respectivos planos de taller, los cuales deben ser revisados y aprobados por la interventoría y la supervisión técnica de la obra.
- Los valores entre parentesis del corte A-A aplican para la conexión al nivel 4.
- Los valores entre parentesis de los cortes B-B y C-C aplican para la conexión al nivel 7.

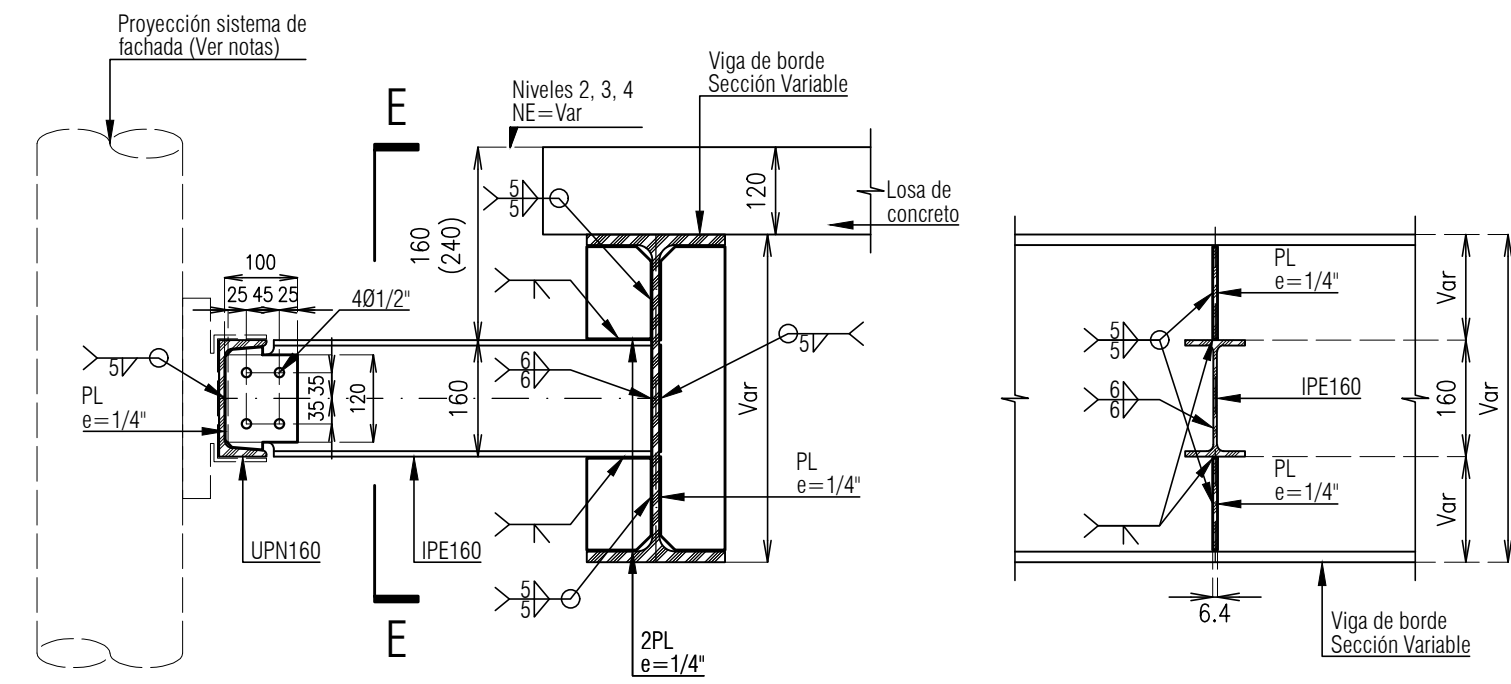


Corte A-A
escala 1:10

Corte E-E
escala 1:10

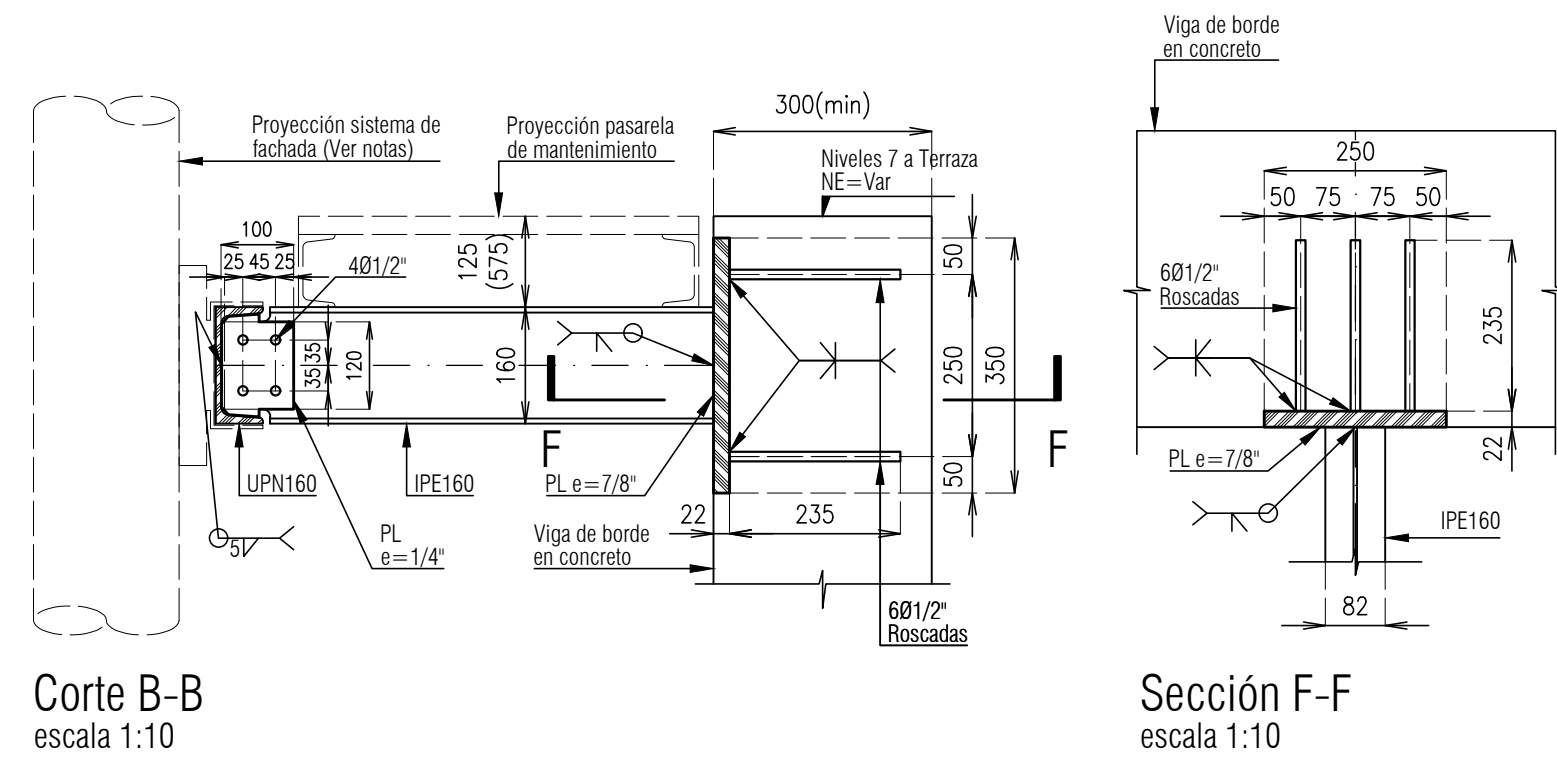


Corte B-B
escala 1:10

Sección F-F
escala 1:10

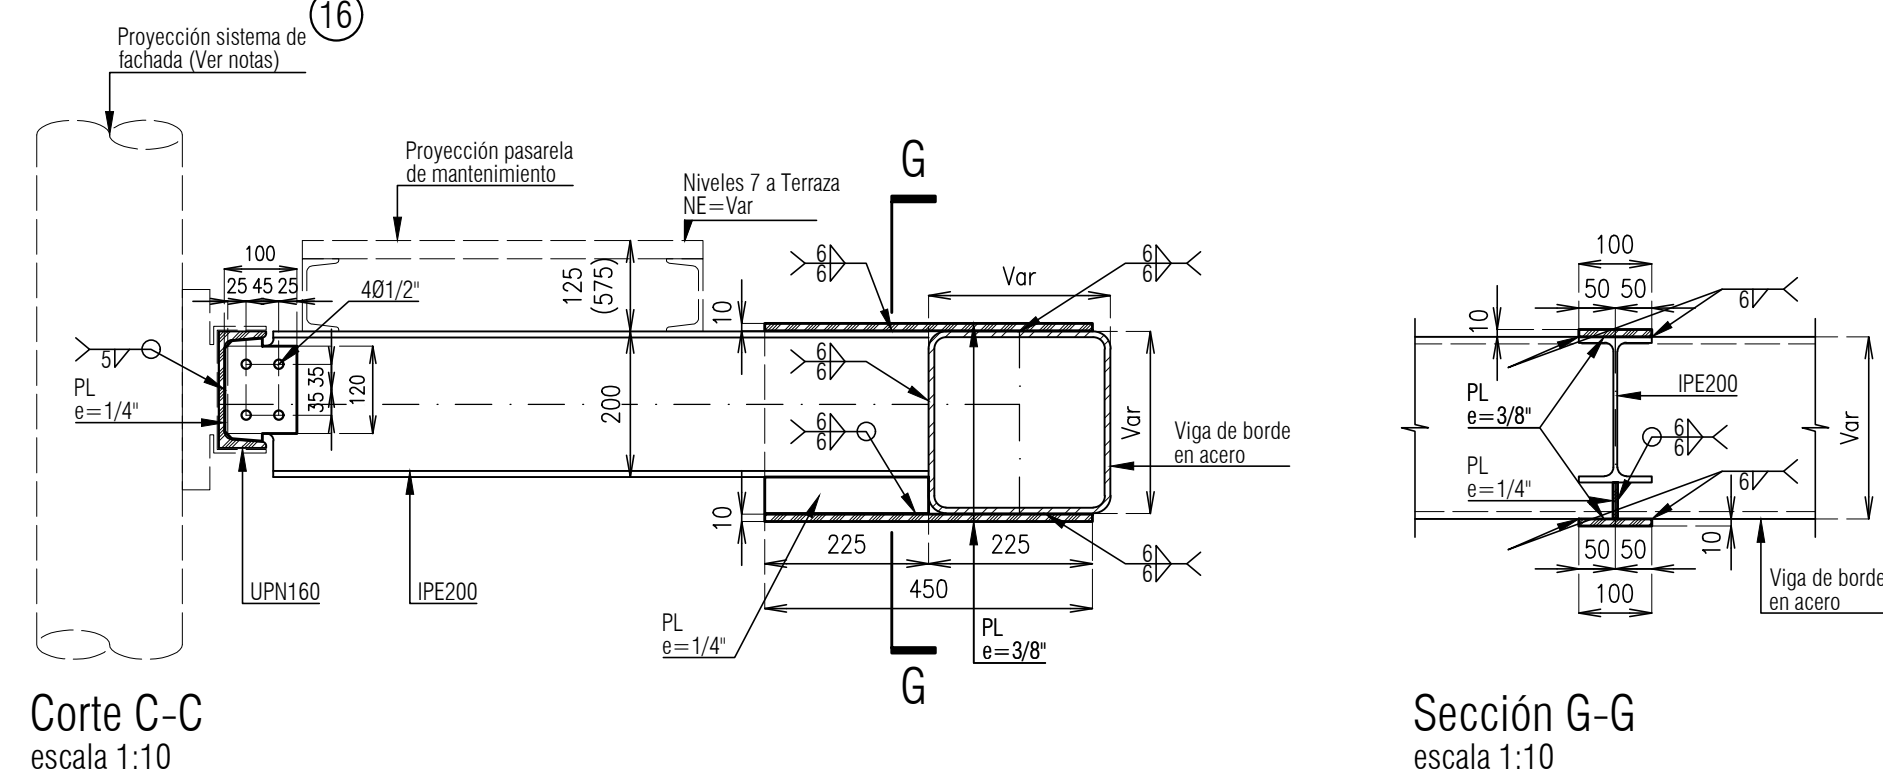


Corte C-C
escala 1:10

Sección G-G
escala 1:10

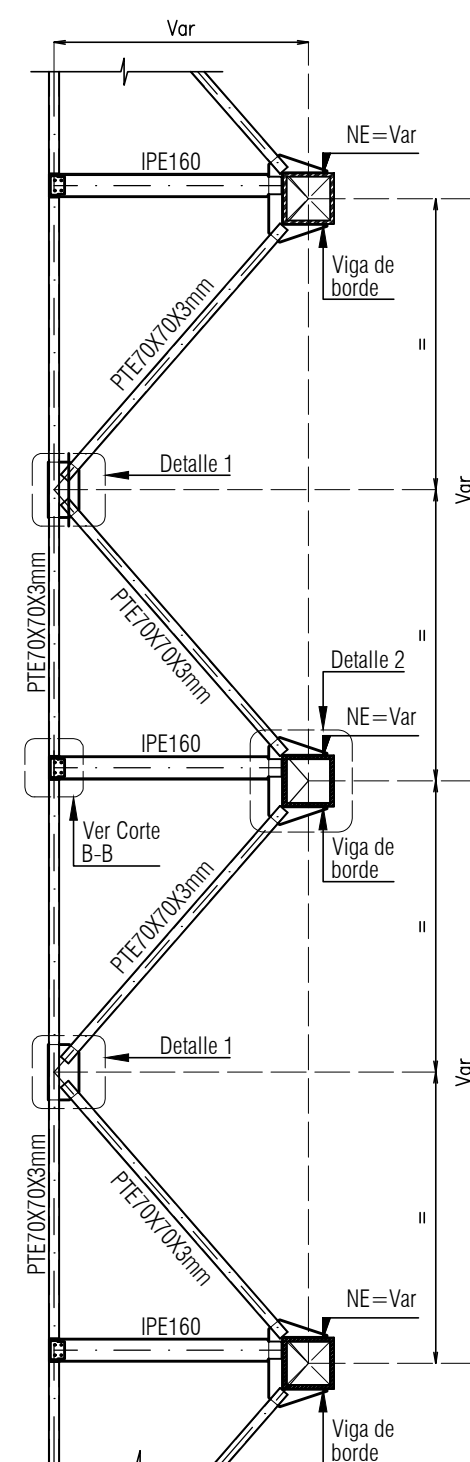

Corte D-D
escala 1:50

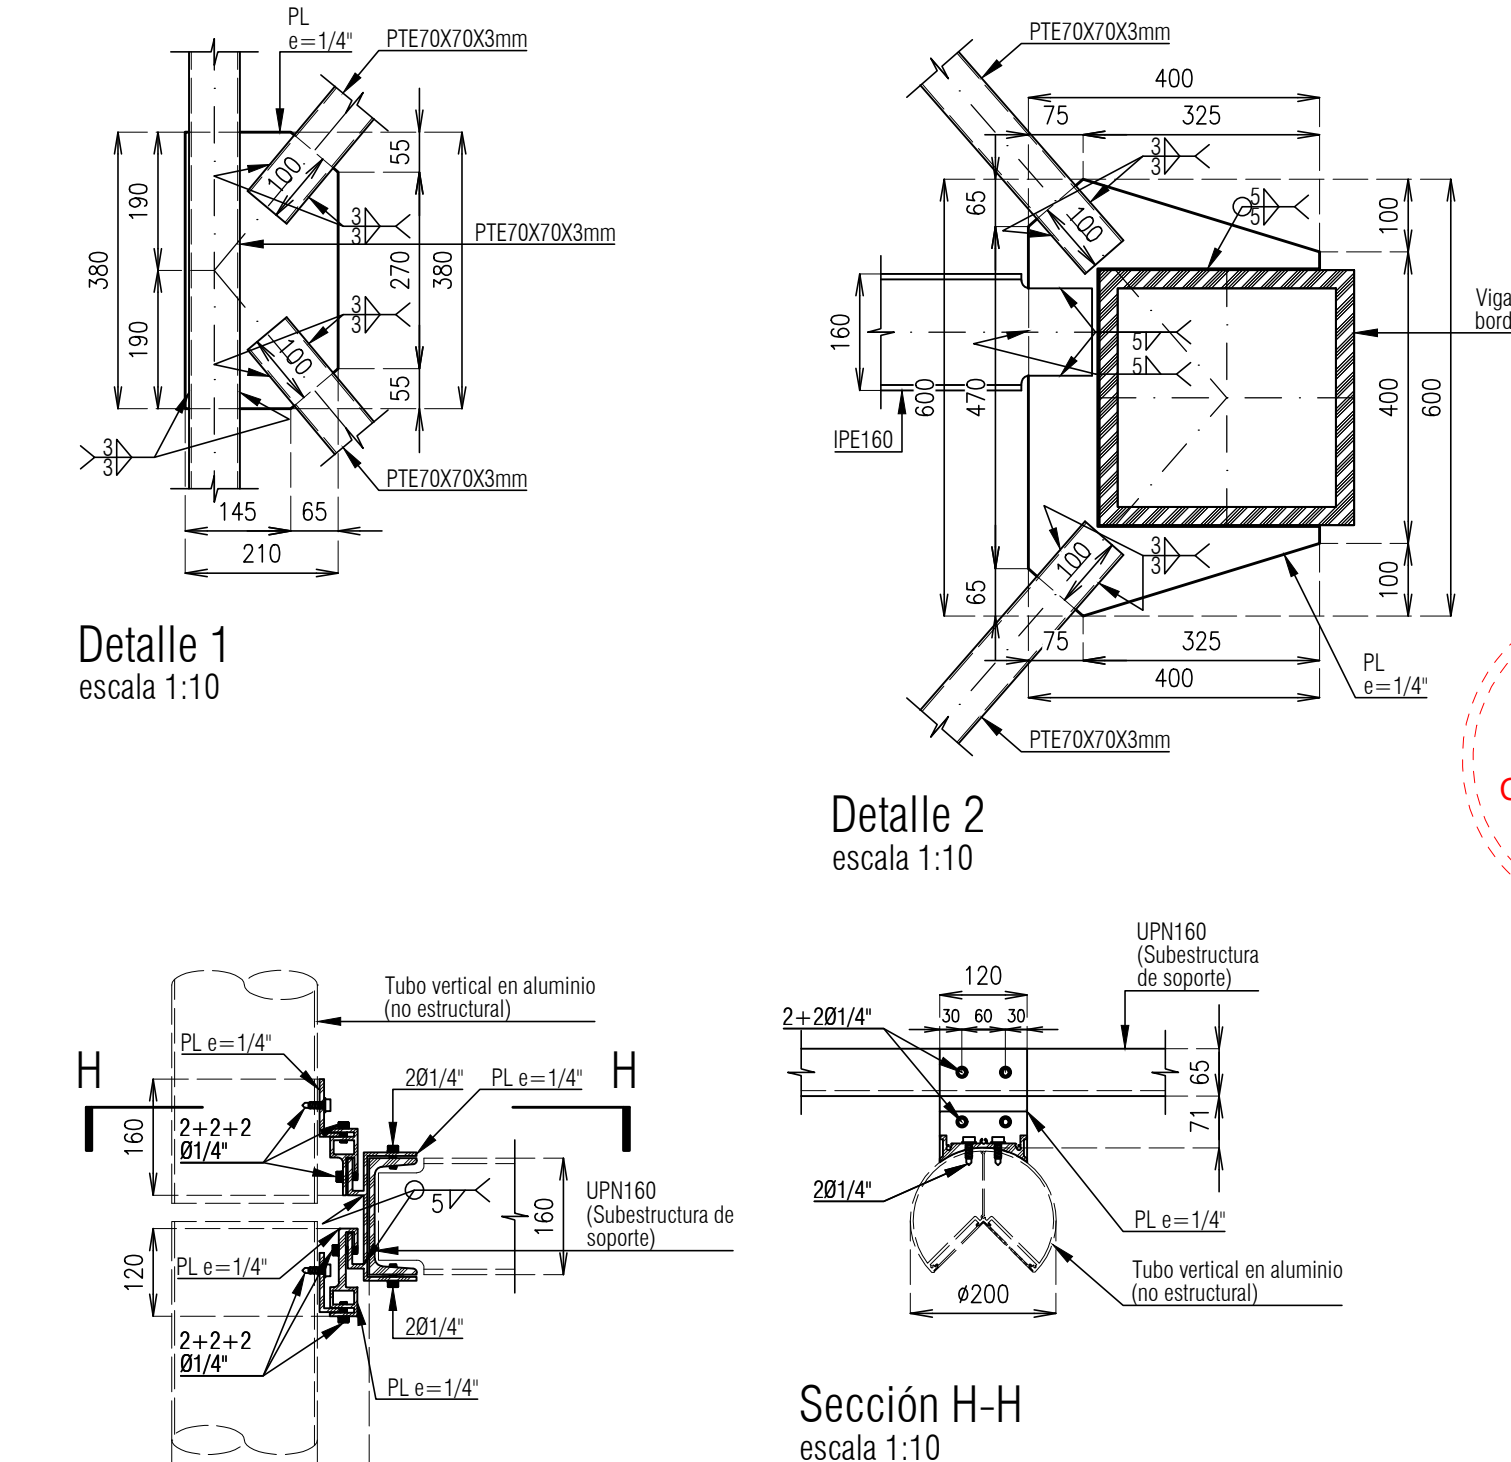

Detalle 1
escala 1:10

Detalle 2
escala 1:10

Sección H-H
escala 1:10

Conexión típica de tubos de aluminio de fachadas
escala 1:10

NOTAS IMPORTANTES:

- El grado mínimo de desempeño de los elementos no estructurales de fachada debe ser Bueno.
- Se debe evitar el par galvánico por contacto entre acero estructural y aluminio, mediante la implementación del material de separación que recomiende el proveedor del sistema de fachada.
- El proveedor final del sistema de fachada puede proponer una conexión alternativa acorde con el sistema que proponga, siempre y cuando suministre al constructor responsable los soportes de cálculo que garanticen la resistencia requerida y el grado de desempeño de las conexiones y del elemento no estructural que cponforma la fachada.

ARQUITECTO COORDINADOR

**EL EQUIPO
MAZZANTI + Gensler**

DISEÑO ESTRUCTURAL



CNI
INGENIEROS

DISEÑADOR: ING. NICOLÁS PARRA GARCÍA
MAT. 52502 62063 CND

INTERVENTORIA



GUTIERREZ DIAZ S.A.S.
Ingeniería y Construcción

Jorge Luis Gera H

Director de Interventoria: Ing. Jorge Iván Garza Mancilla
Mat. 63057 14803 CND

Versión	Emisión	Descripción
AA	15-06-2023	Ingeniería básica
AB	04-08-2023	Anteproyecto
AC	01-11-2023	Anteproyecto V2 50%
AD	15-12-2023	Anteproyecto V2 100%
DD	13-03-2024	Entrega curaduría
EE	10-05-2024	Proyecto Final 100%
EF	31-05-2024	Respuesta Obs 100%
FF	21-06-2024	Entrega Final
01	26-07-2024	ENTREGA FINAL


PROYECTO:
CAMPUS DE CIENCIA TECNOLOGIA E
INNOVACIÓN DE BOGOTÁ
MAT. No. 900-00254970

FASE: ENTREGA FINAL

PROPÓSITO DE EMISIÓN

Curaduría	☐	Coordinación	☐
Revisión	☐	Construcción	☒
Entrega Cliente	☒		

ZONIFICACIÓN
Nivel 24
Nivel 23
Nivel 22
Nivel 21
Nivel 20
Nivel 19
Nivel 18
Nivel 17
Nivel 16
Nivel 15
Nivel 14
Nivel 13
Nivel 12
Nivel 11
Nivel 10
Nivel 9
Nivel 8
Nivel 7
Nivel 6
Nivel 5
Nivel 4
Nivel 3
Nivel 2
Nivel 1
Nivel 01
Nivel 02

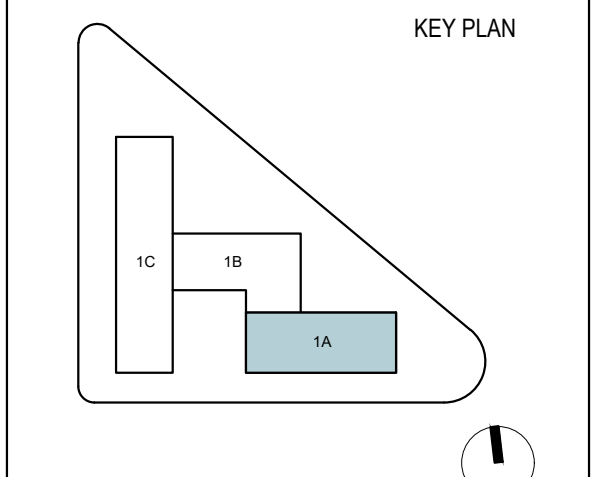

Fecha: 26-07-2024

Escala: As Indicated

DETALLES DE
SUBESTRUCTURAS DE
SOPORTE DE FACHADA
CTIB_EST_516_DET_XXX_01