


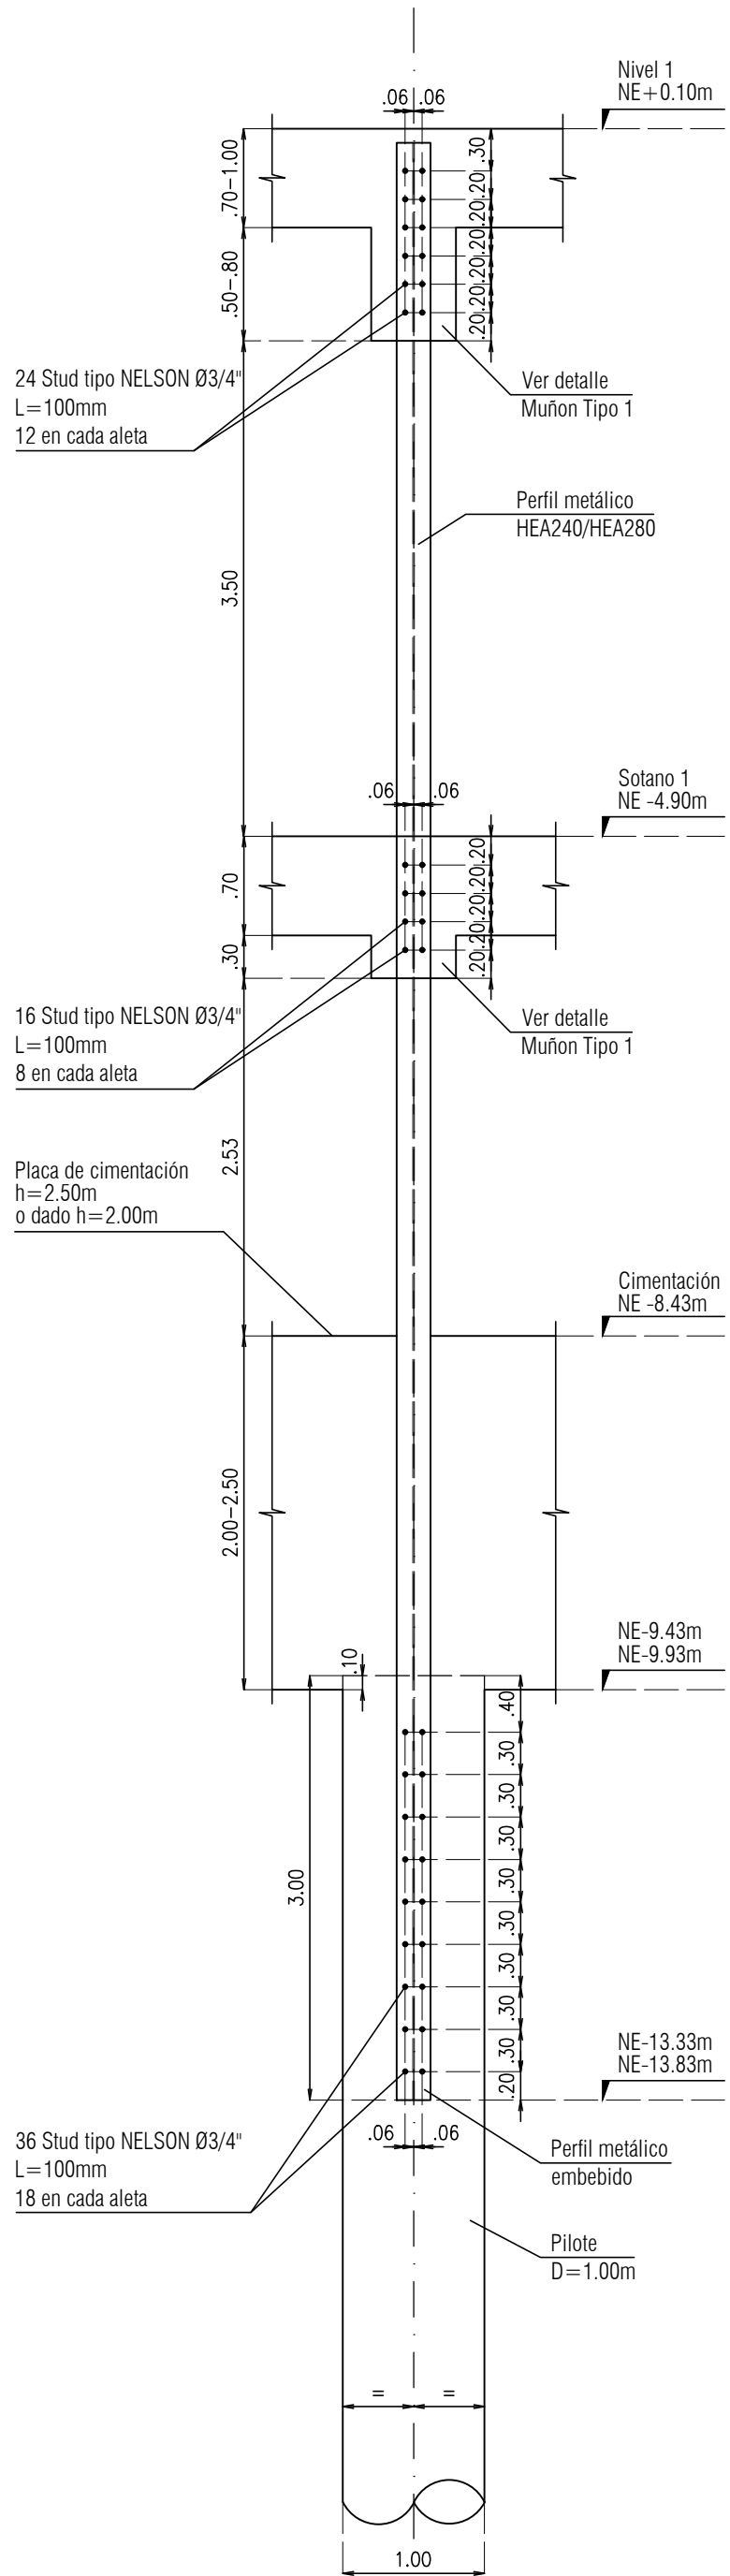


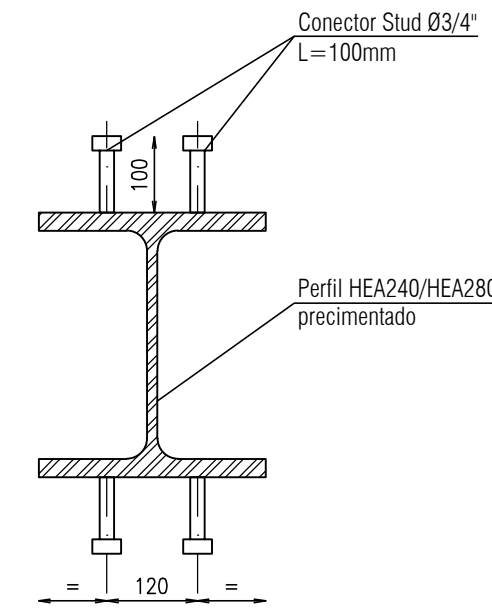



DETALLES TÍPICOS DE PERFILES HEA EMBEBIDOS PARA APOYO TEMPORAL DE PLACAS ANDEN
escala 1:50

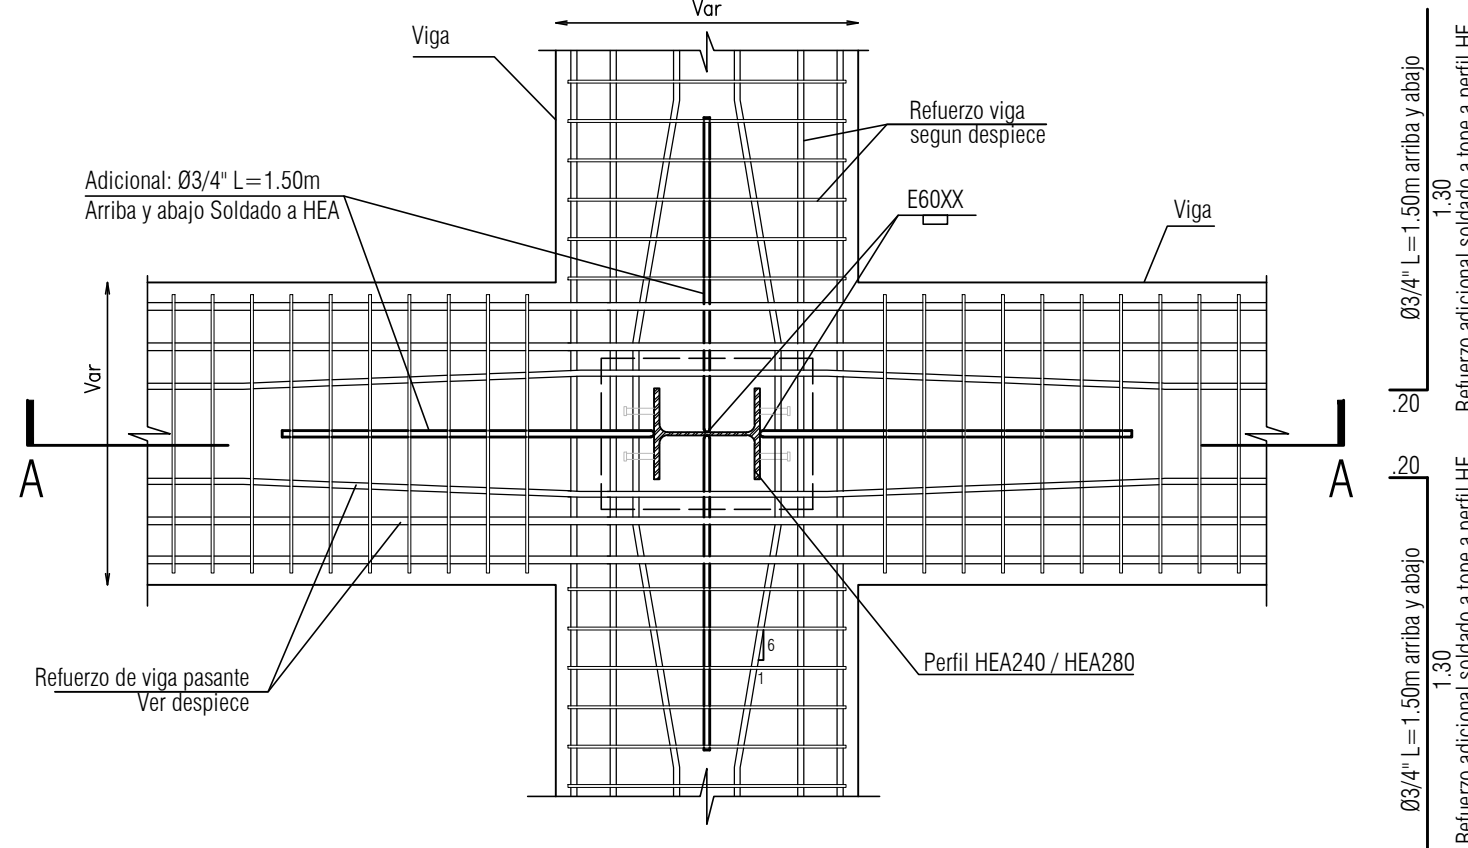

DETALLE CONECTORES A PERFIL HEA
escala 1:10

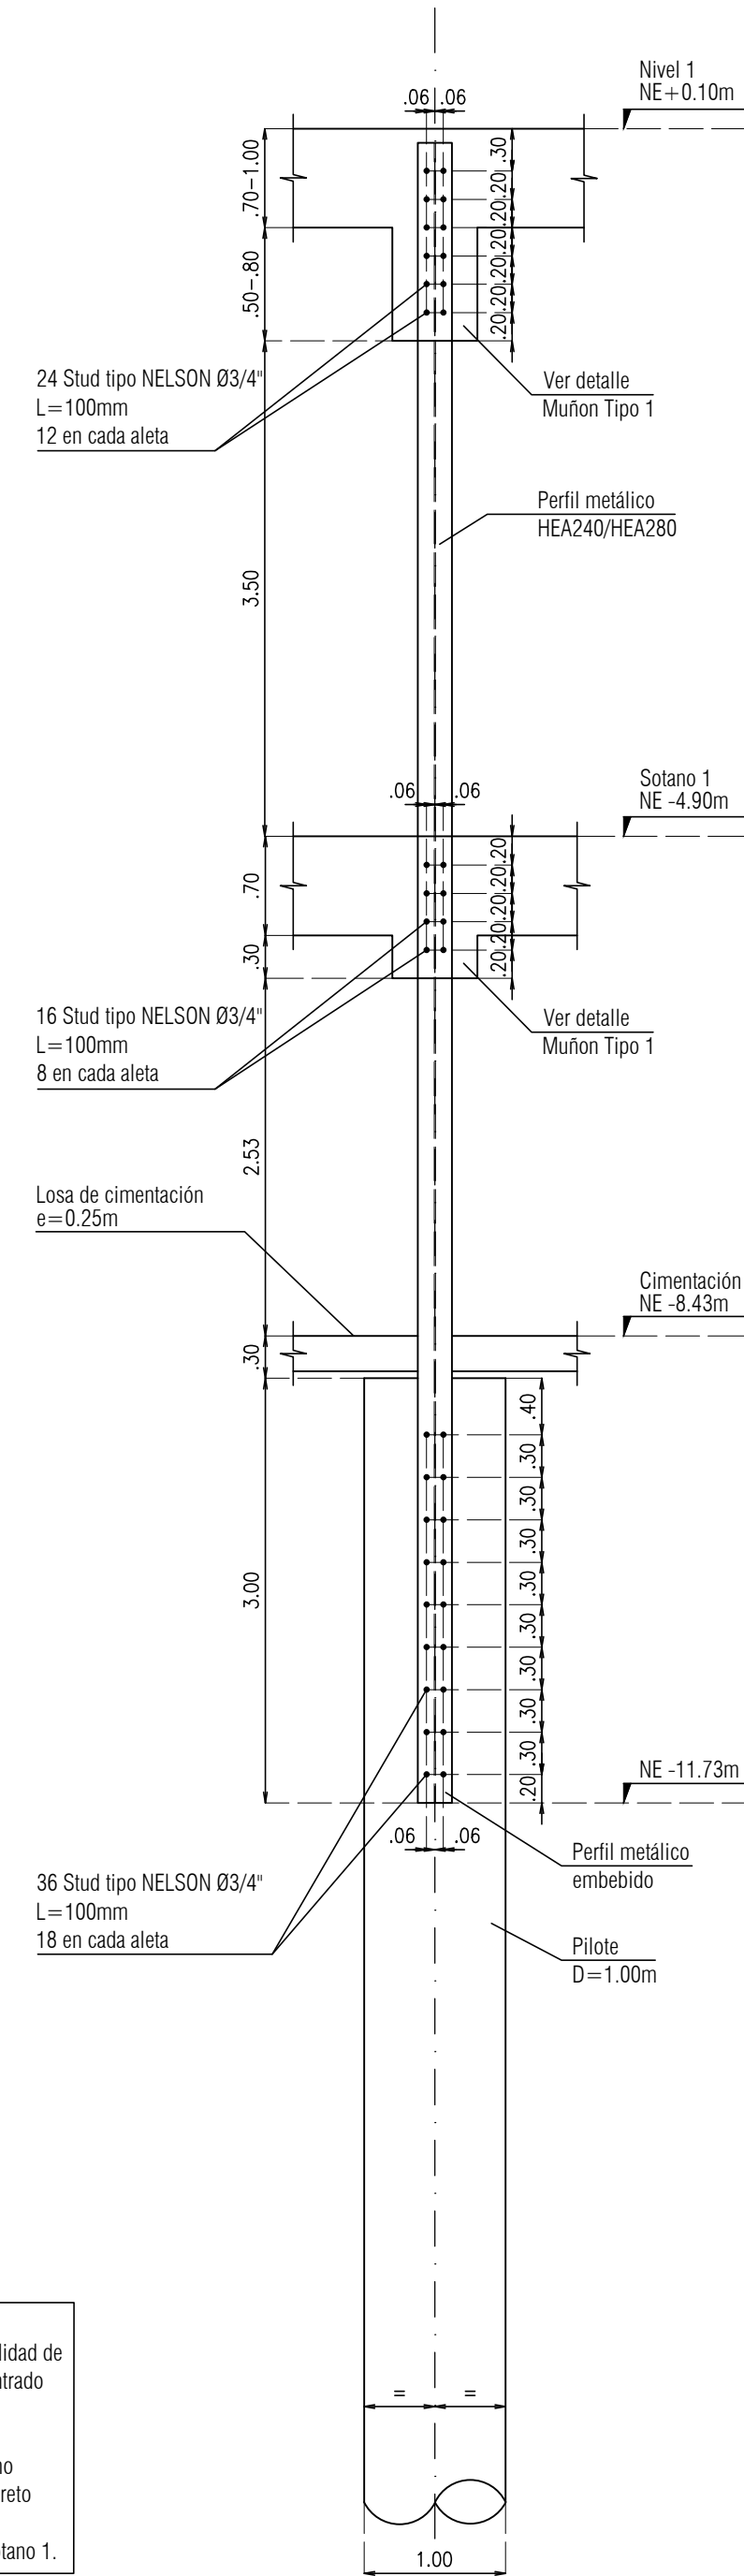


NOTA:
- Máxima inclinación para el doblado en planta de las barras de refuerzo: 1:6

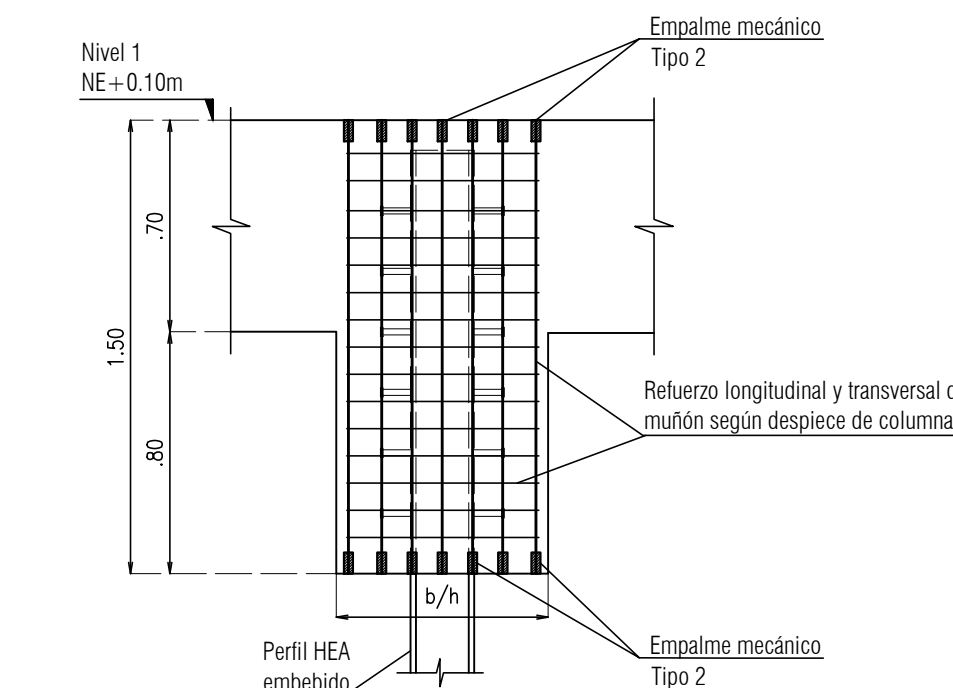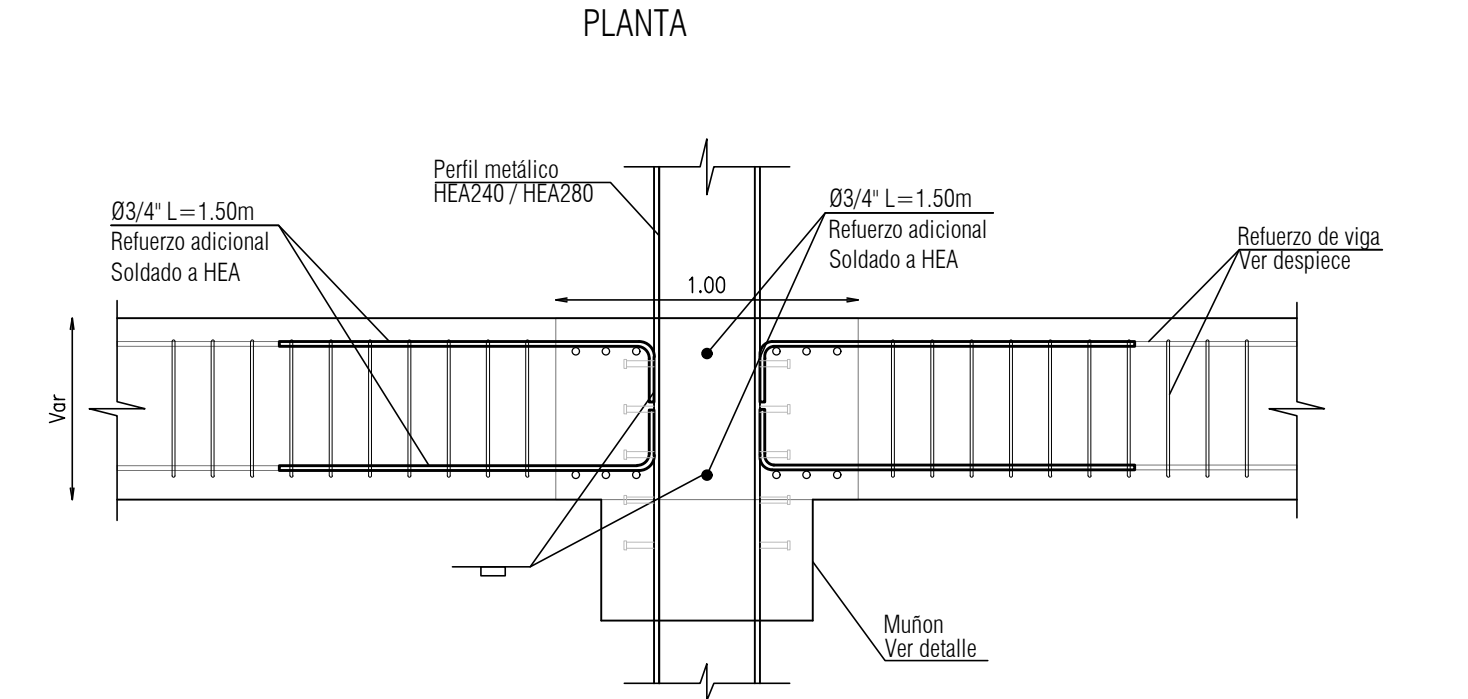


DETALLE MUÑÓN TIPO 1
escala 1:25


NOTAS:
* Las dimensiones de la sección del muñón Tipo 1 y 2 (b/h) corresponden a las de la columna definitiva en cada caso
* El f'c del concreto del muñón es el mismo de las columnas

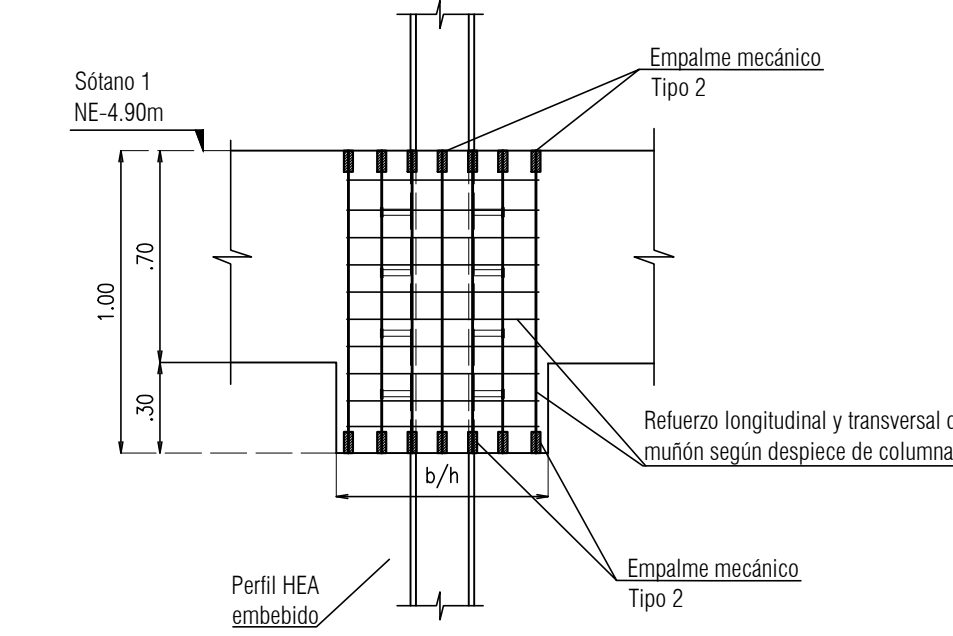


REFUERZO MUÑÓN TIPO 2
escala 1:25

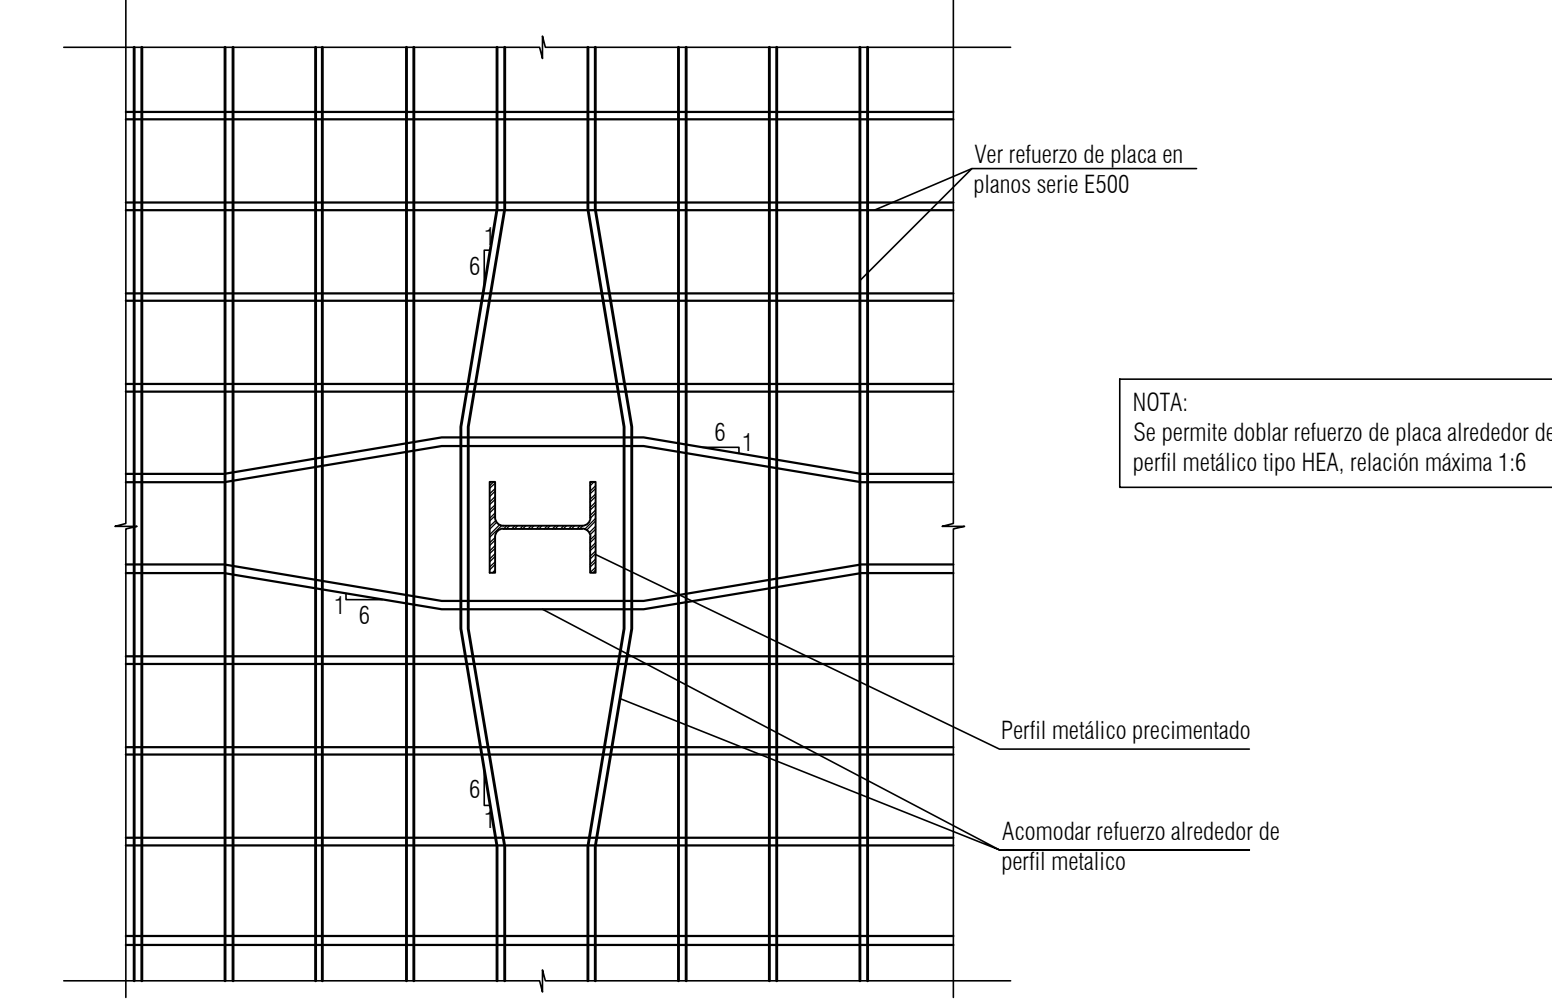


DETALLE ARMADO DE REFUERZO DE PLACA DE SUBPRESIÓN SOBRE PERFIL METÁLICO TIPO HEA
escala 1:25

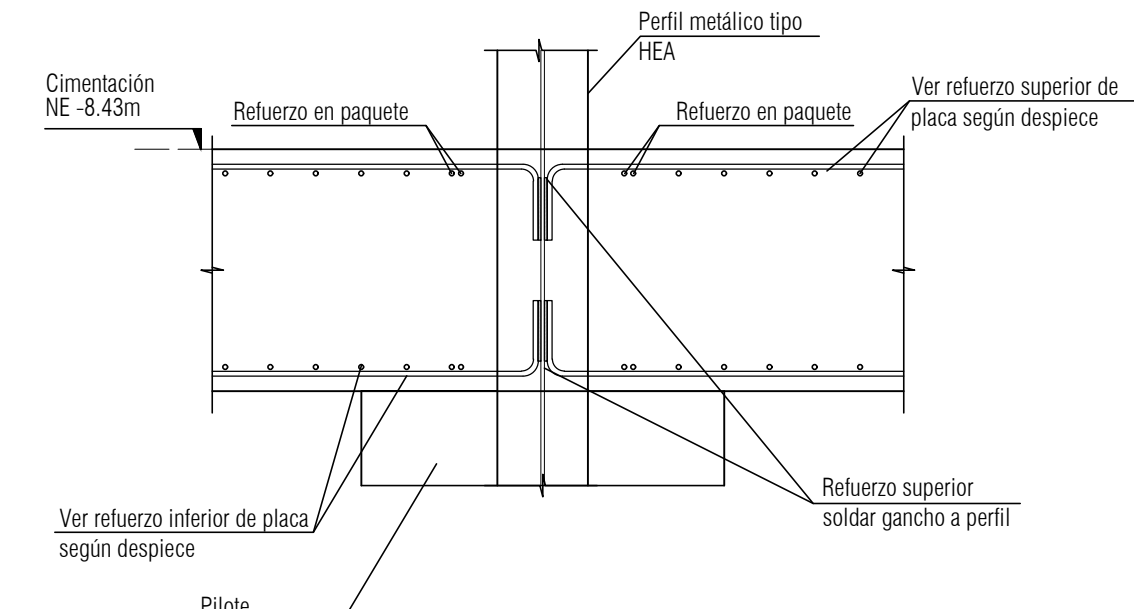


DETALLE ARMADO DE REFUERZO DE PLACA DE SUPRESIÓN SOBRE PERFIL METÁLICO TIPO HEA (ALTERNATIVA)
escala 1:25

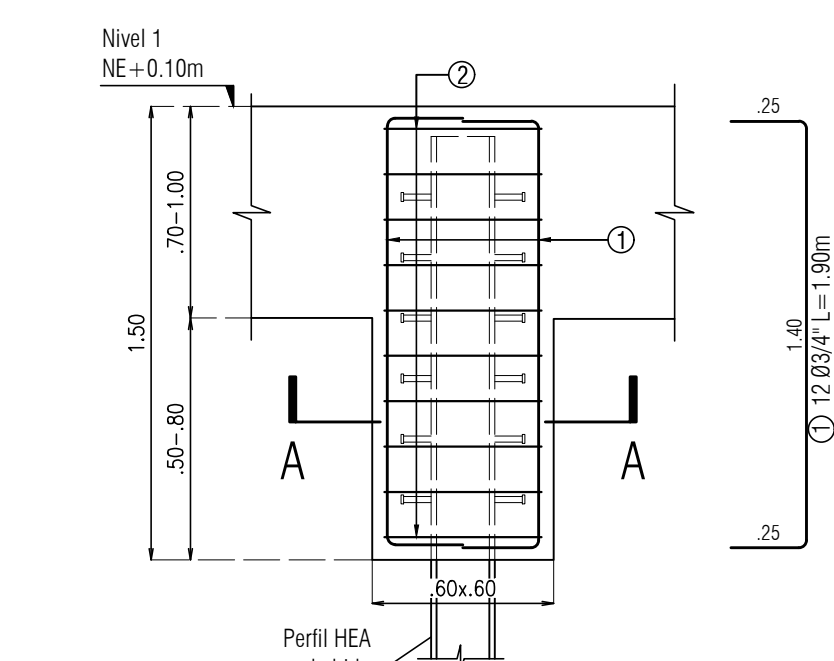

DETALLE MUÑÓN TIPO 3
escala 1:25

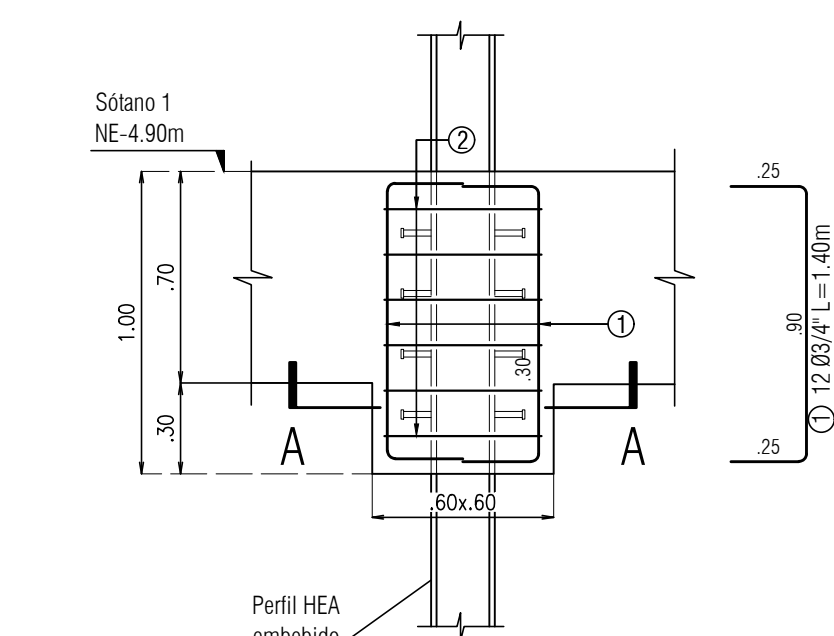

REFUERZO MUÑÓN TIPO 4
escala 1:25

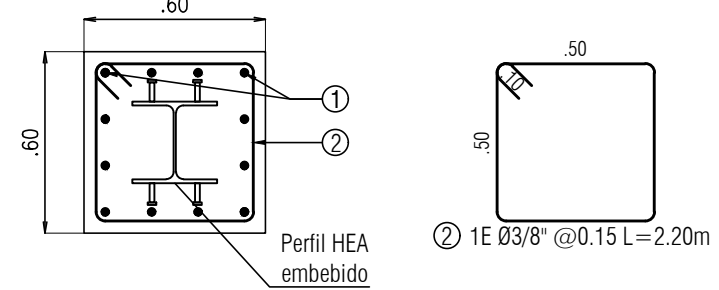

CORTE A-A
escala 1:25

PROYECTO DETALLADO
APTO PARA CONSTRUCCIÓN (APC)

Versión	Emisión	Descripción
AA	15-06-2023	Ingeniería básica
AB	04-08-2023	Anteproyecto
AC	01-11-2023	Anteproyecto V2 50%
AD	15-12-2023	Anteproyecto V2 100%
DD	13-03-2024	Entrega curaduría
EE	10-05-2024	Proyecto Final 100%
EF	31-05-2024	Respuesta Obs 100%
FF	21-06-2024	Entrega Final
01	28-07-2024	ENTREGA FINAL

PROPÓSITO DE EMISIÓN			
Curaduría	☐	Coordinación	☐
Revisión	☐	Construcción	☒
Entrega Cliente	☒		

TO
DO

ARA
CCION
()

ZONIFICACIÓN

Nivel 24
Nivel 23
Nivel 22
Nivel 21
Nivel 20
Nivel 19
Nivel 18
Nivel 17
Nivel 16
Nivel 15
Nivel 14
Nivel 13
Nivel 12
Nivel 11
Nivel 10
Nivel 9
Nivel 8
Nivel 7
Nivel 6
Nivel 5
Nivel 4
Nivel 3
Nivel 2
Nivel 1
Nivel B1
Nivel B2

