




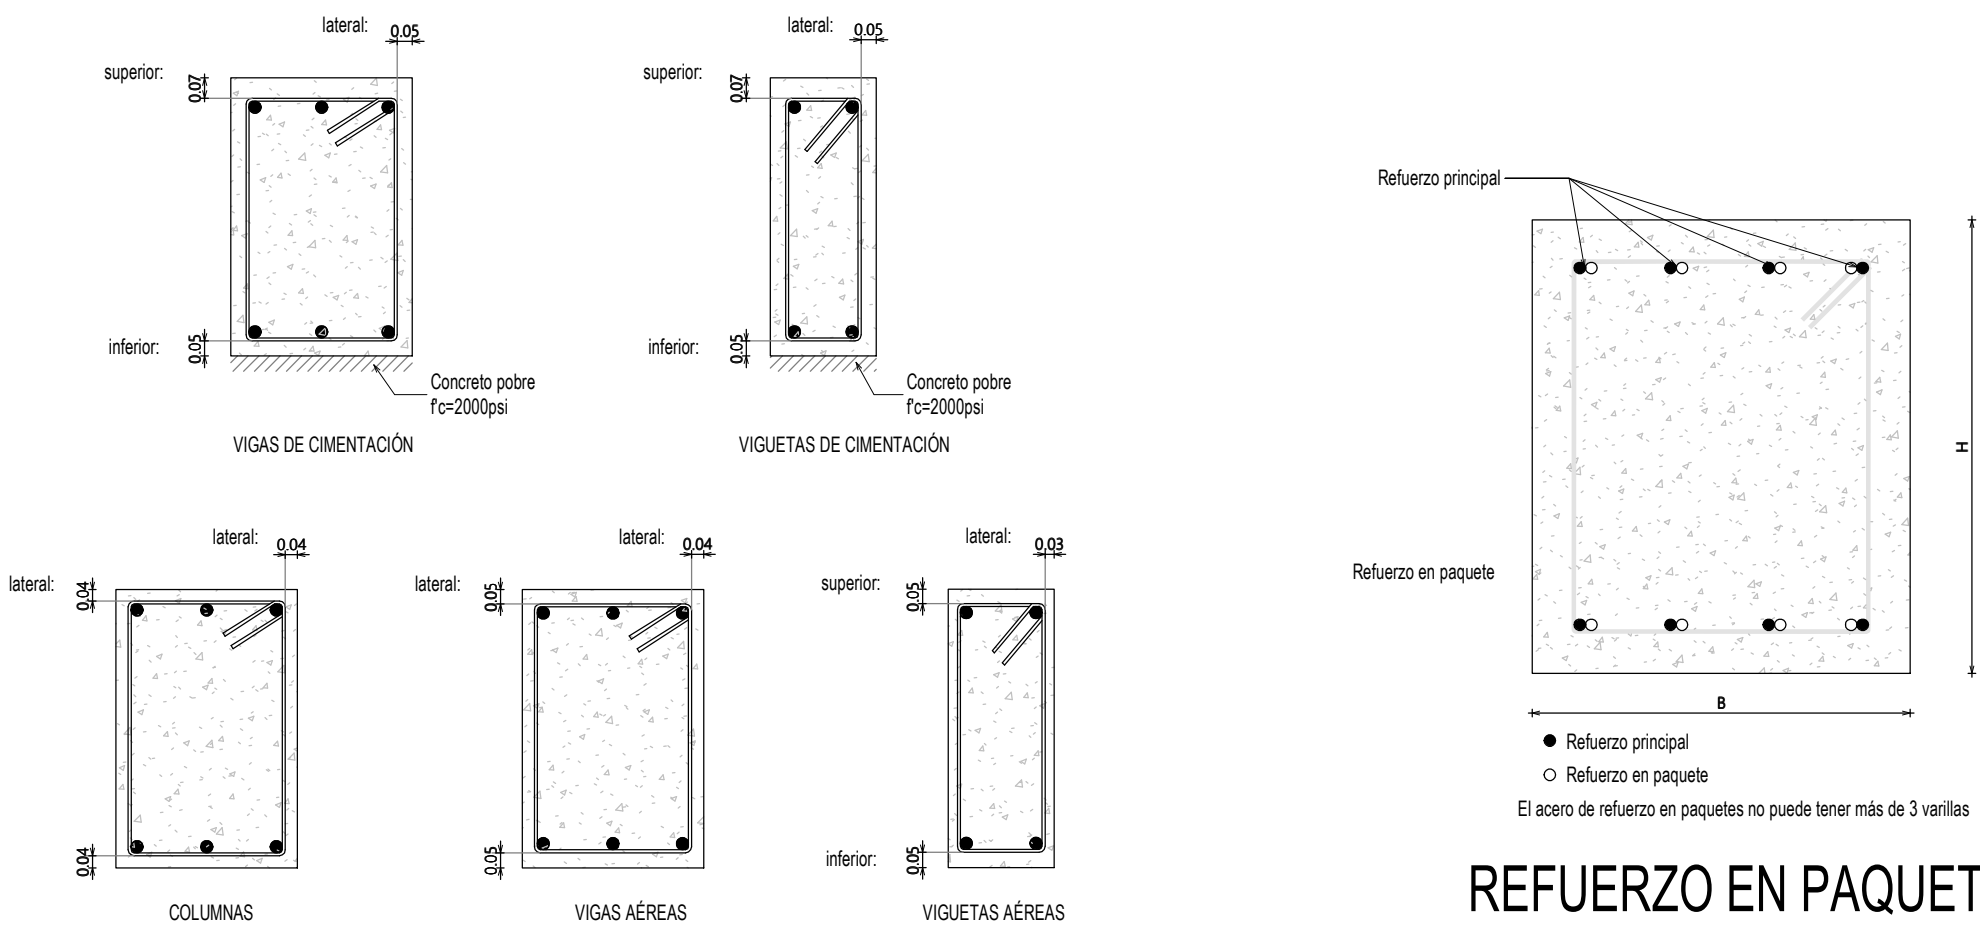

RECUBRIMIENTOS MÍNIMOS AL FLEJE

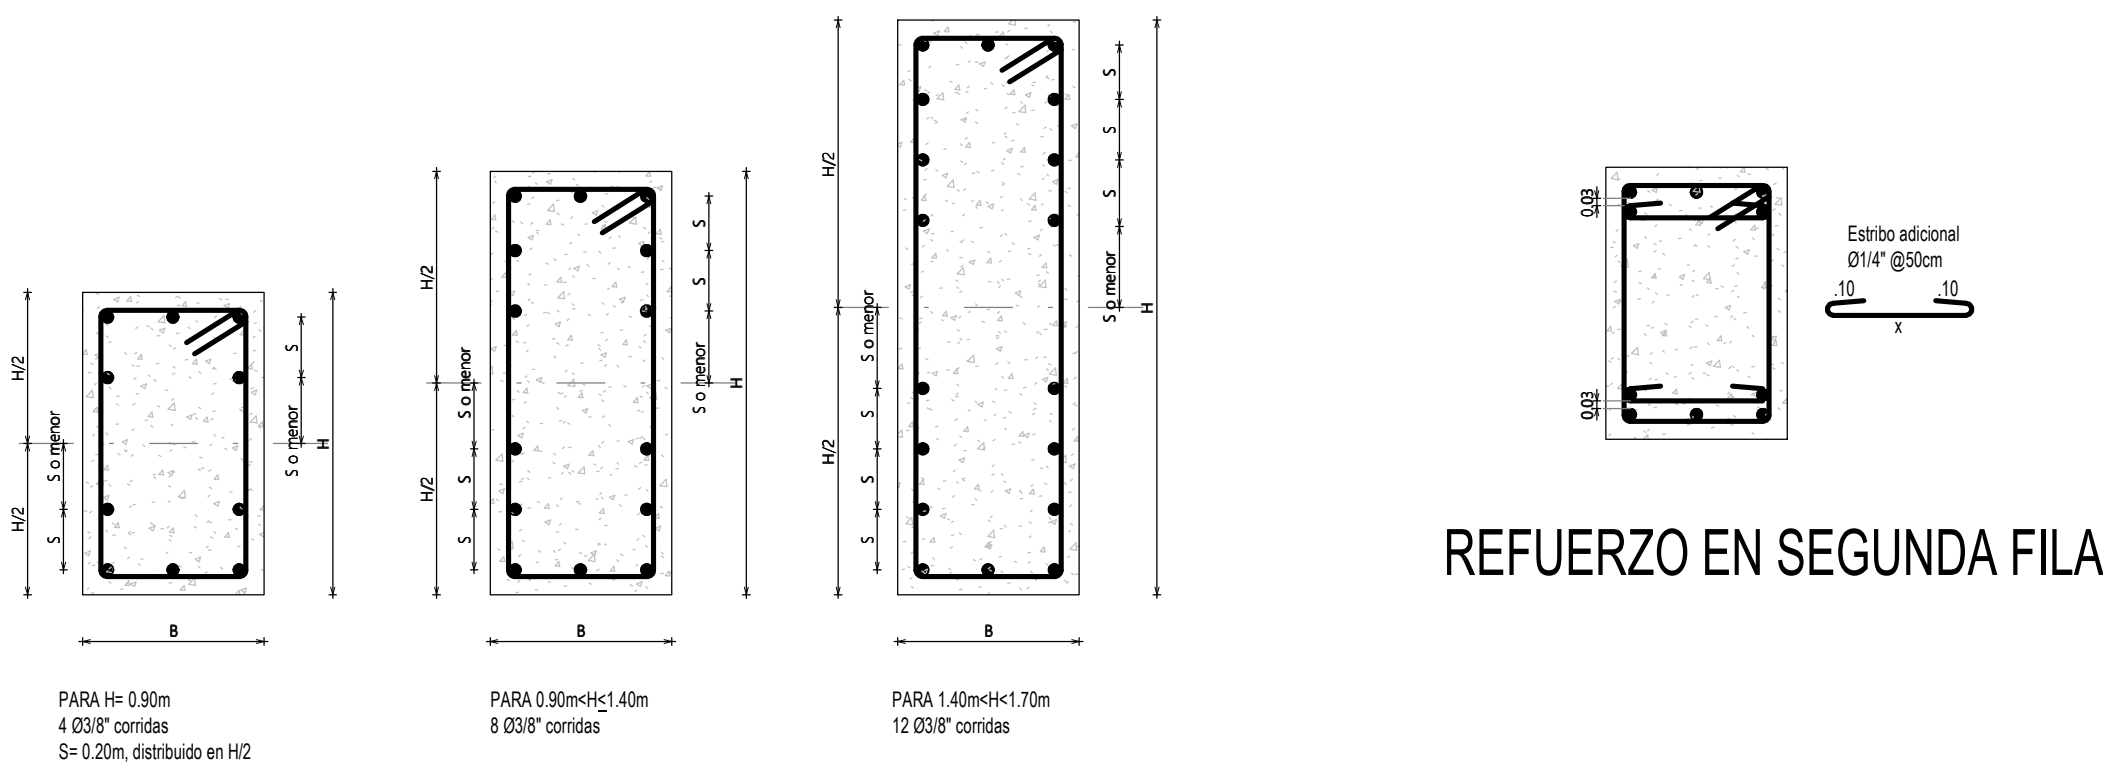


REFUERZO ADICIONAL EN VIGAS ALTAS

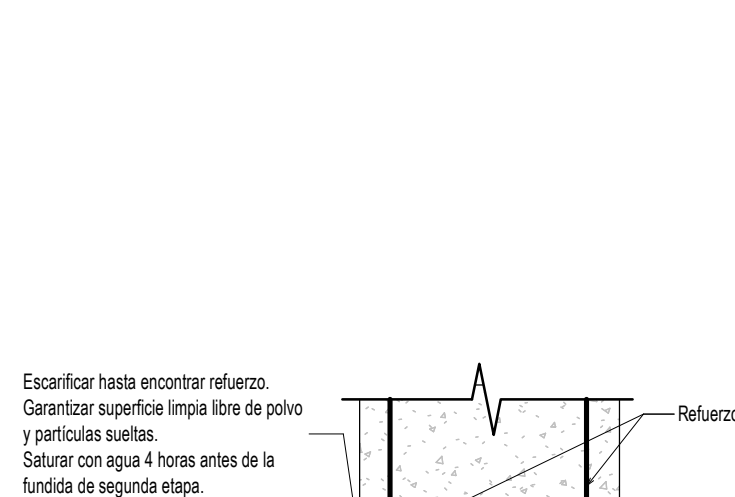


ANCLAJE EPÓXICO TÍPICO

escala 1:20

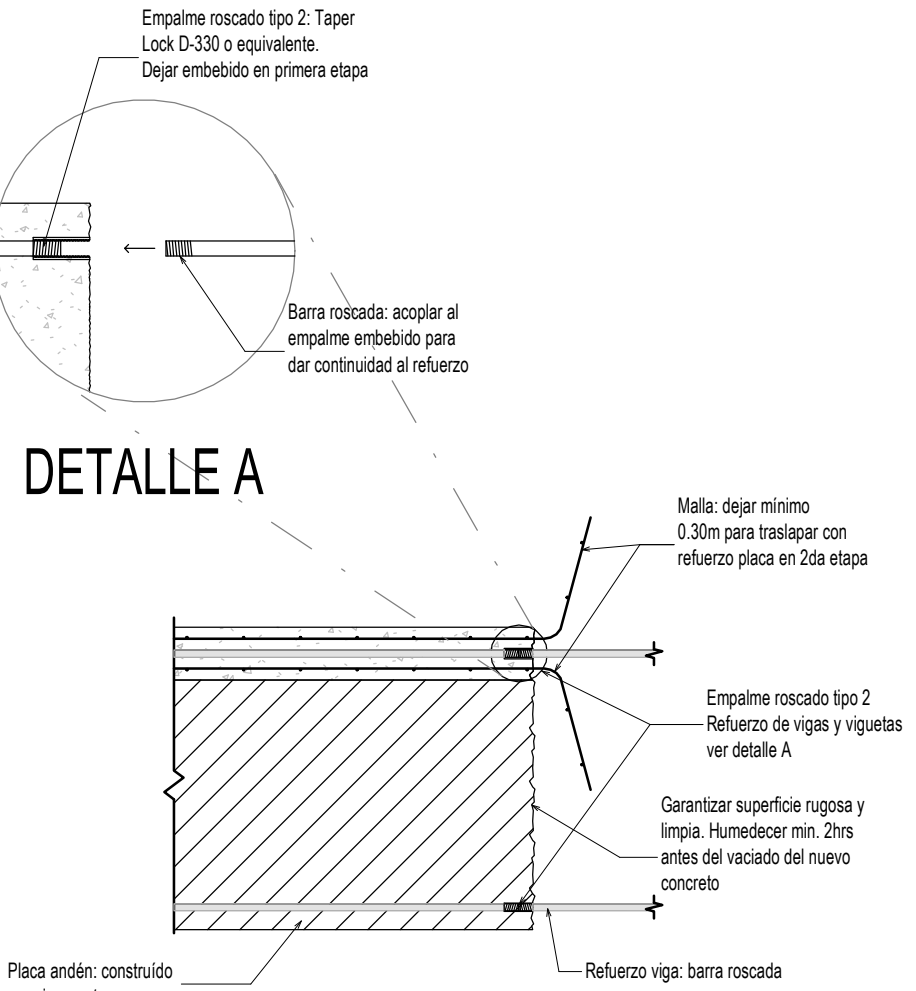


DETALLE TÍPICO EMPALME EN PLACA ANDEN

escala 1:20

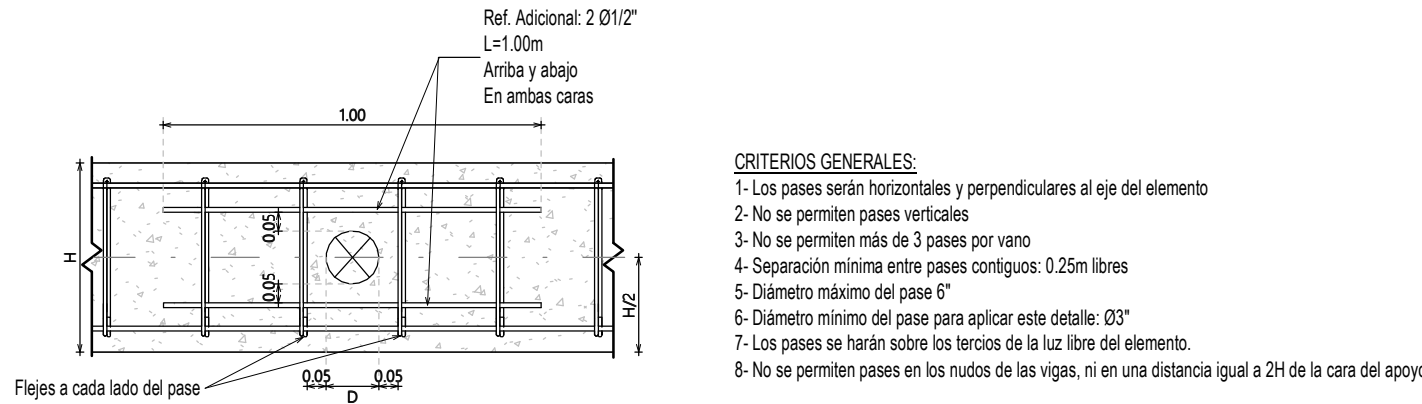


ALZADO TÍPICO PASE DE TUBERÍA EN VIGAS Y VIGUETAS

escala 1:20

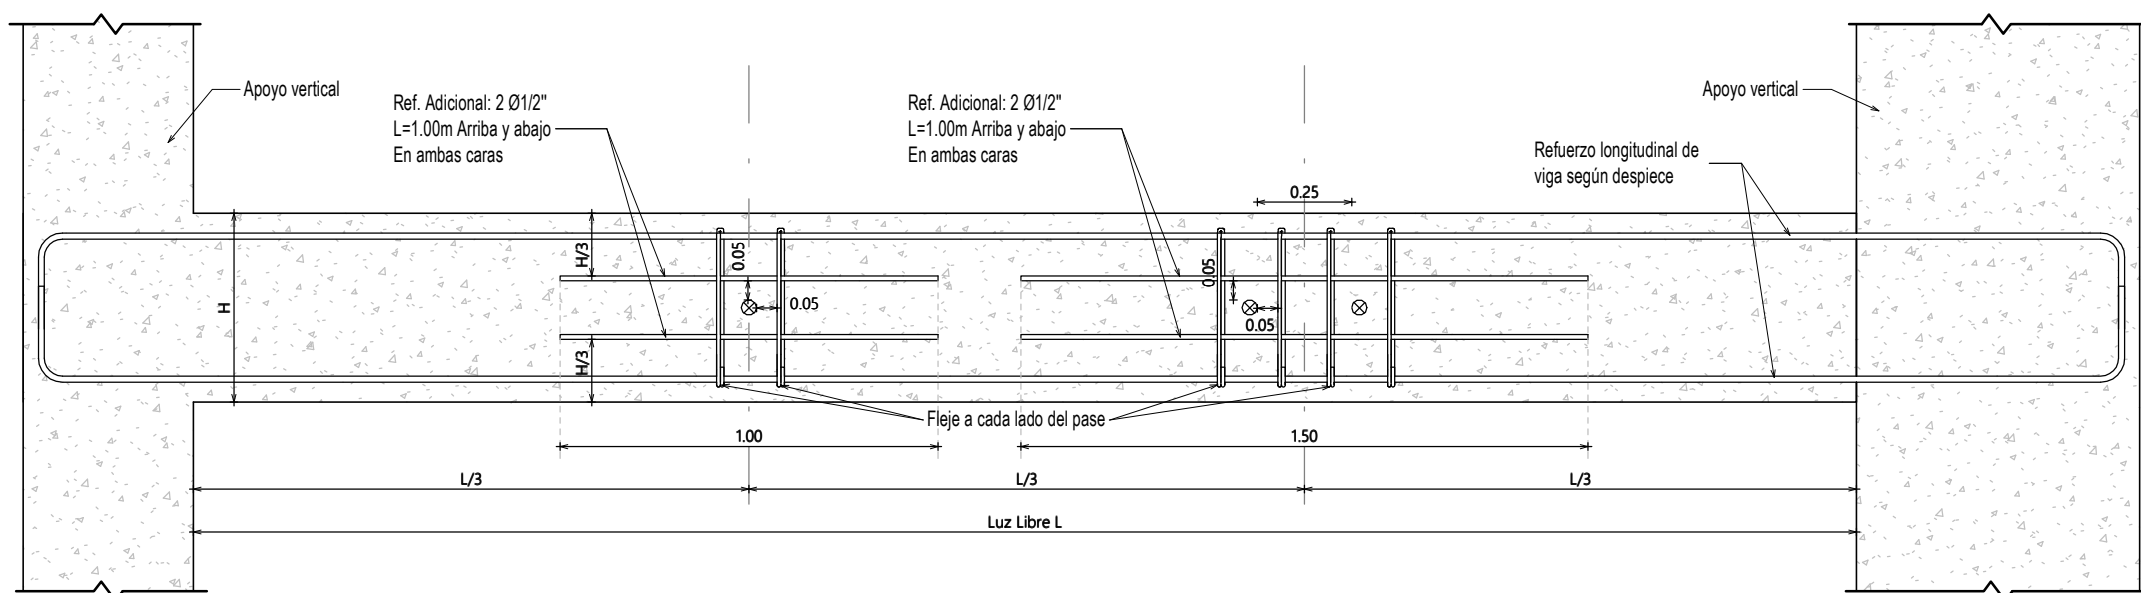


ALZADO TÍPICO DE PASE DE TUBERÍA EN VIGAS Y VIGUETAS

escala 1:20

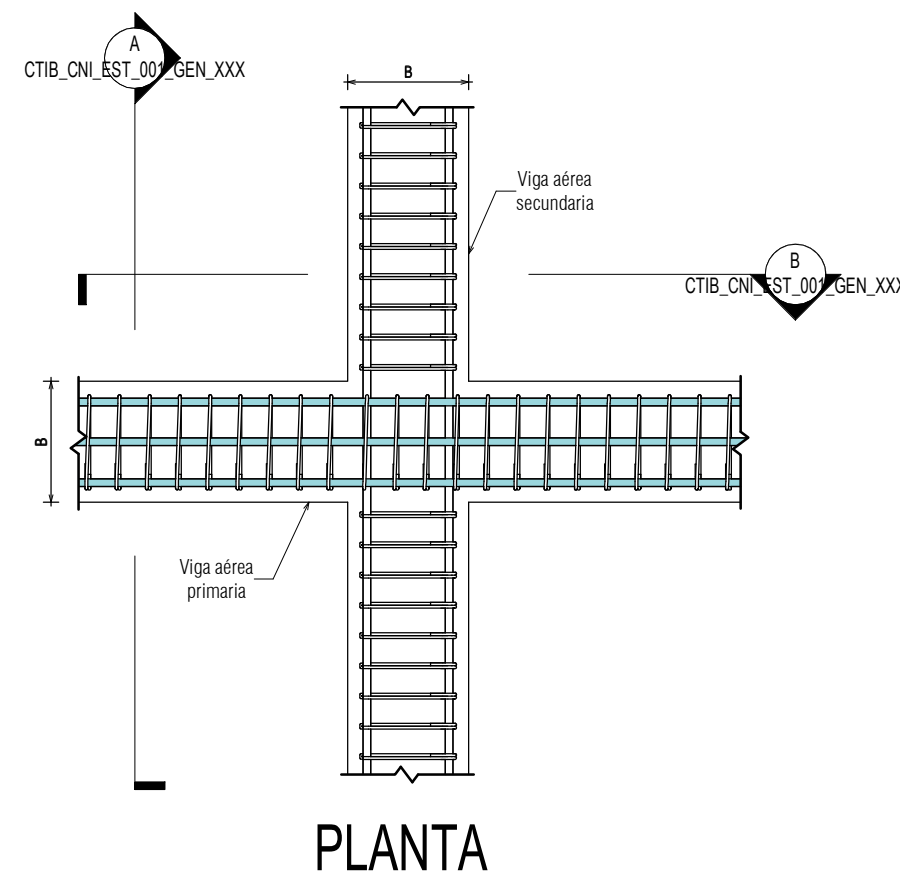

PLANTA

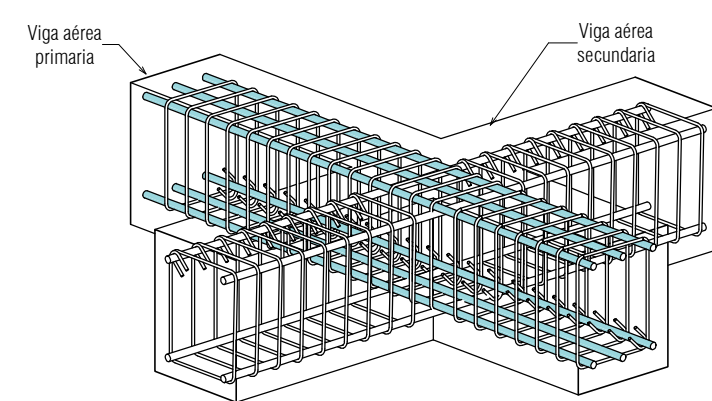


AXONOMETRÍA


escala

DETALLE TÍPICO DE UNIÓN DE VIGAS AÉREAS

escala 1:25

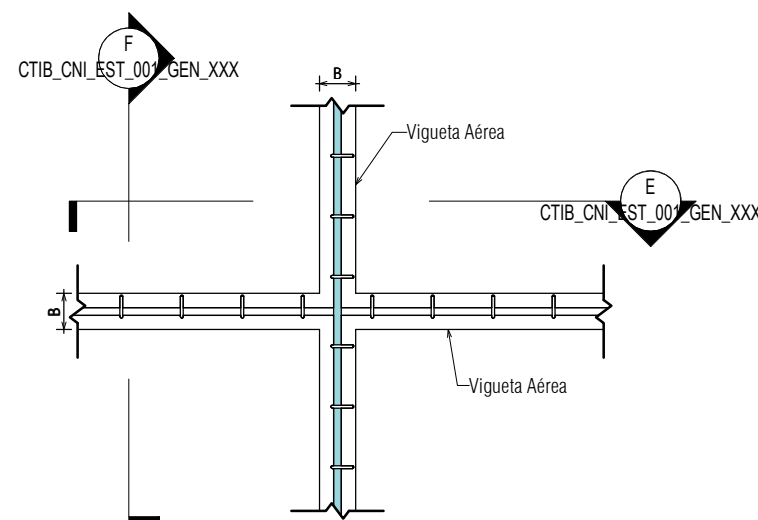

PLANTA

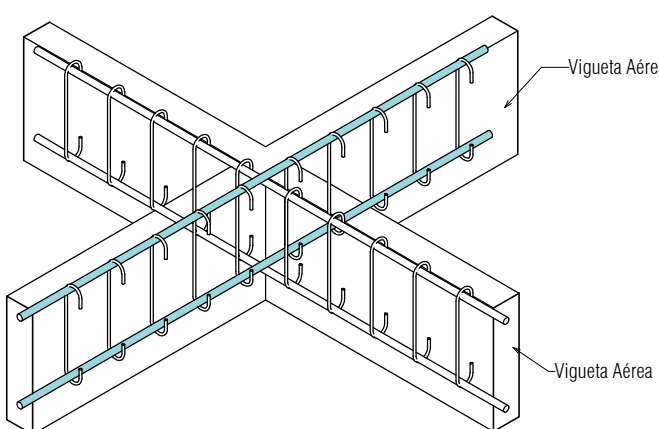


AXONOMETRÍA


escala

DETALLE TÍPICO DE UNIÓN DE VIGUETA-VIGUETA

escala 1:25

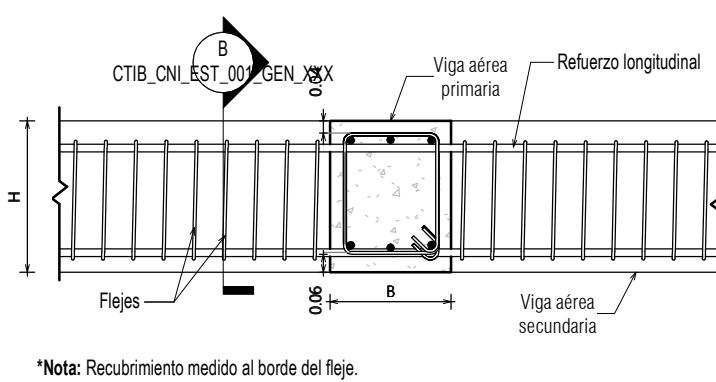


CORTE A-A

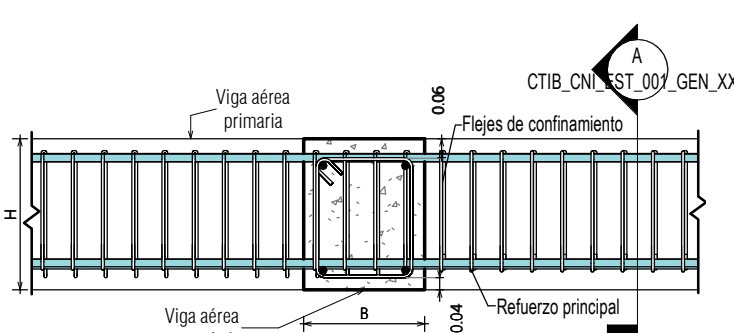


CORTE B-B




CORTE E-E

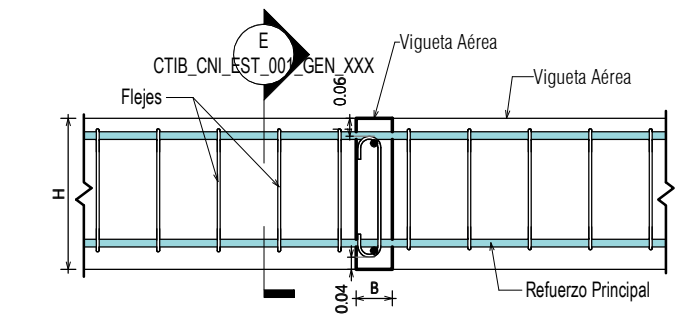

CORTE F-F

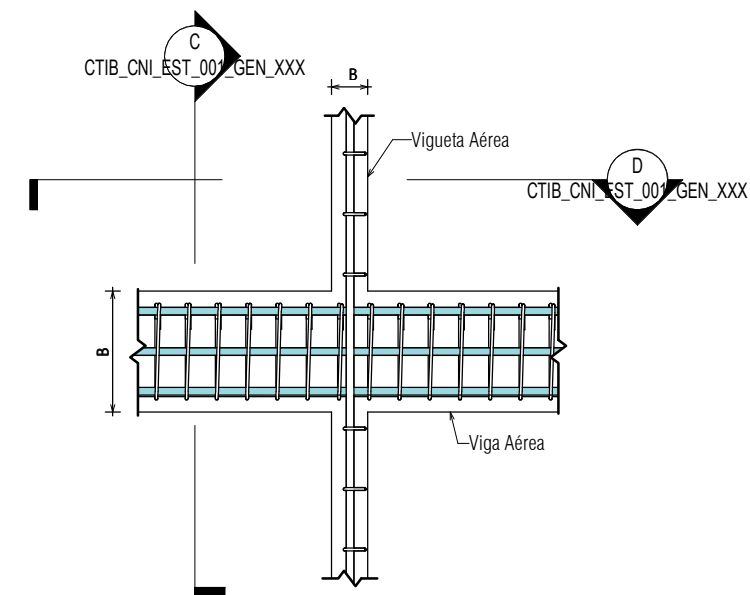

PLANTA

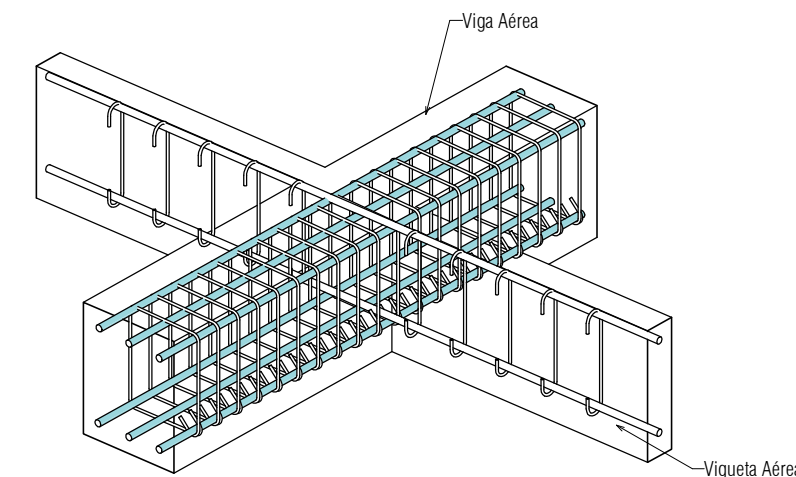


AXONOMETRÍA


escala

DETALLE TÍPICO DE UNIÓN DE VIGA AÉREA-VIGUETA

escala 1:25

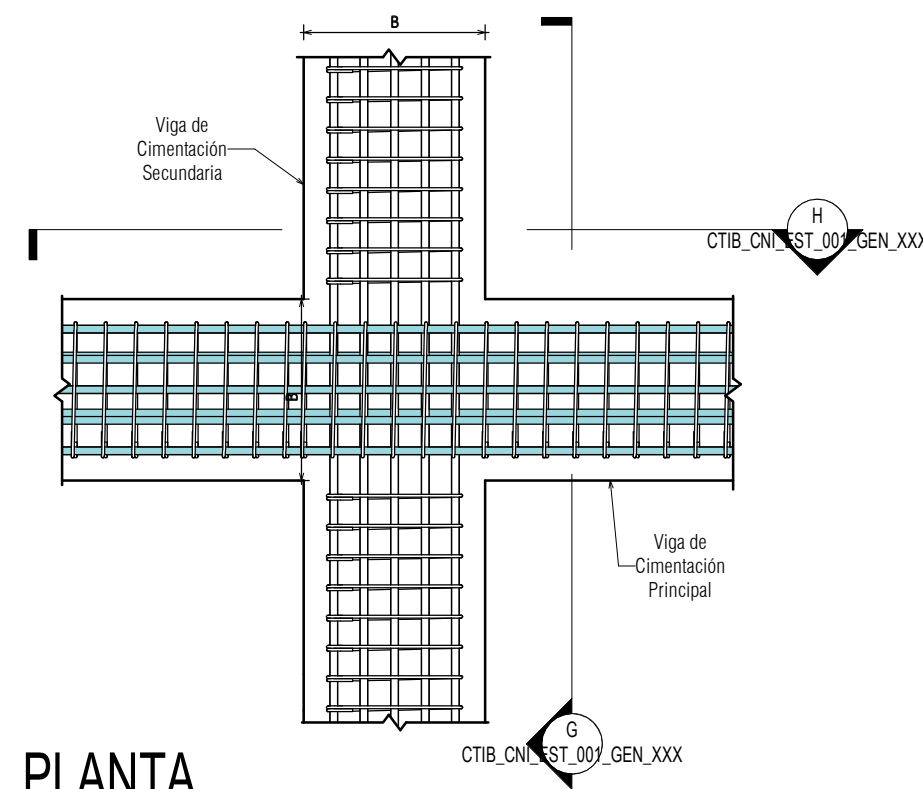

PLANTA

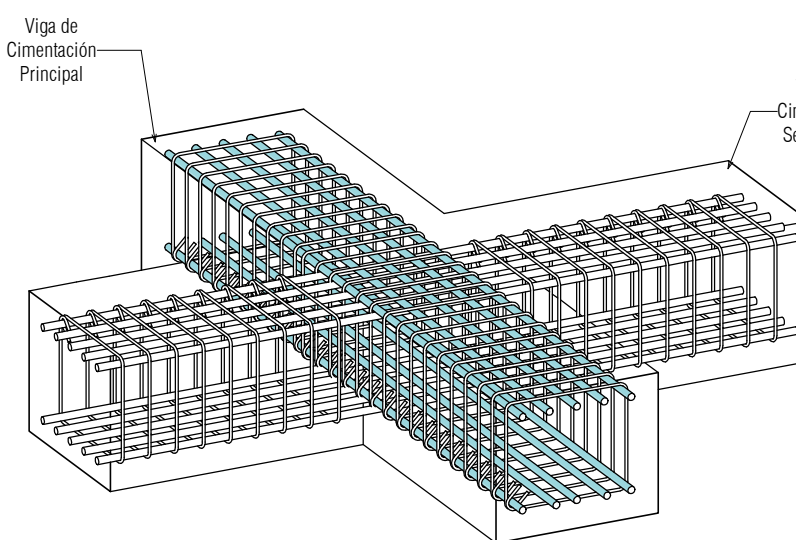


AXONOMETRÍA


escala

DETALLE TÍPICO DE UNIÓN DE VIGAS DE CIMENTACIÓN

escala 1:25

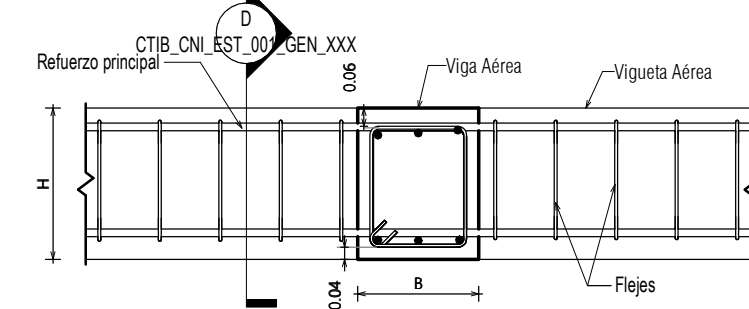


CORTE C-C

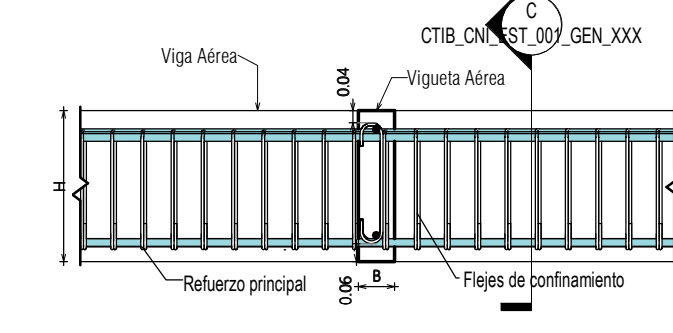

CORTE D-D



CORTE G-G

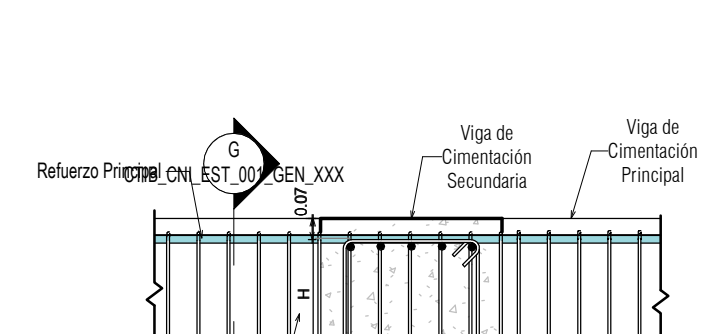

CORTE H-H

*NOTAS GENERALES:

- Los detalles presentados en los planos son detalles típicos y deben emplearse a criterio del constructor, es su responsabilidad enviar las especificaciones de recubrimiento de los elementos estructurales indicados.
 - Las especificaciones de los materiales se muestran en el plano E000, y deberán ser de conocimiento por parte del constructor, interventor y supervisor de obra, previo al inicio de la obra.
- VIGA PRINCIPAL:
Son los encargados de transmitir las cargas y dar rigidez, se apoyan en los elementos verticales de la estructura.
- VIGA o VIGUETA SECUNDARIA:
Elemento horizontal que se apoyan y transmiten sus cargas a las vigas primarias.

CTIB

Campus de Ciencia, Tecnología e Innovación de Bogotá - Región



ARQUITECTO COORDINADOR

ELEQUIPO MAZZANTI + Gensler

DISEÑO ESTRUCTURAL



GUTIERREZ DÍAZ S.A.S.

SUPERVISIÓN Y GESTIÓN DE PROYECTOS DE CONSTRUCCIÓN



Director de Interventoría: Ing. Jorge Iván García Mancilla
MAT. 632021-148063 QND

Versión	Emisión	Descripción
AA	15-06-2023	Ingeniería básica
AB	04-08-2023	Anteproyecto
AC	01-11-2023	Anteproyecto V2 50%
AD	15-12-2023	Anteproyecto V2 100%
DD	13-03-2024	Curaduría V2
EE	10-05-2024	Proyecto final 100%
EF	31-05-2024	Respuesta Obs.100%
FF	21-06-2024	Entrega final
01	26-07-2024	ENTREGA FINAL

PROYECTO:
CAMPUS DE CIENCIA, TECNOLOGÍA E INNOVACIÓN DE BOGOTÁ
MAT. No. 50C-0205470

FASE
PROYECTO CONSTRUCTIVO

PROPOSITO DE EMISION


Curaduría	☐	Coordinación	☐
Revisión	☐	Construcción	☐
Entrega Cliente	☒		

ZONIFICACIÓN

Nivel S1	
Nivel S2	
ENTREGA FINAL
APTO PARA CONSTRUCCIÓN

KEY PLAN

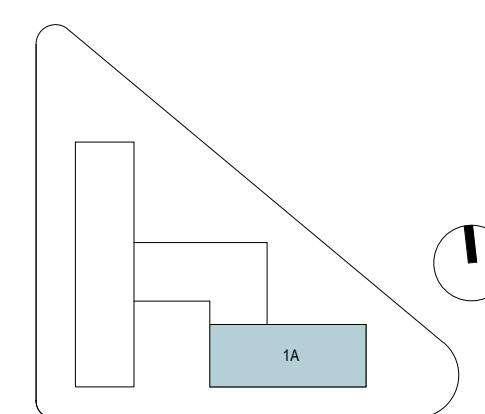

Fecha: 26-07-2024

Escala: As indicated

ESPECIFICACIONES GENERALES

CTIB_CN_EST_001_GEN_XXX_01