
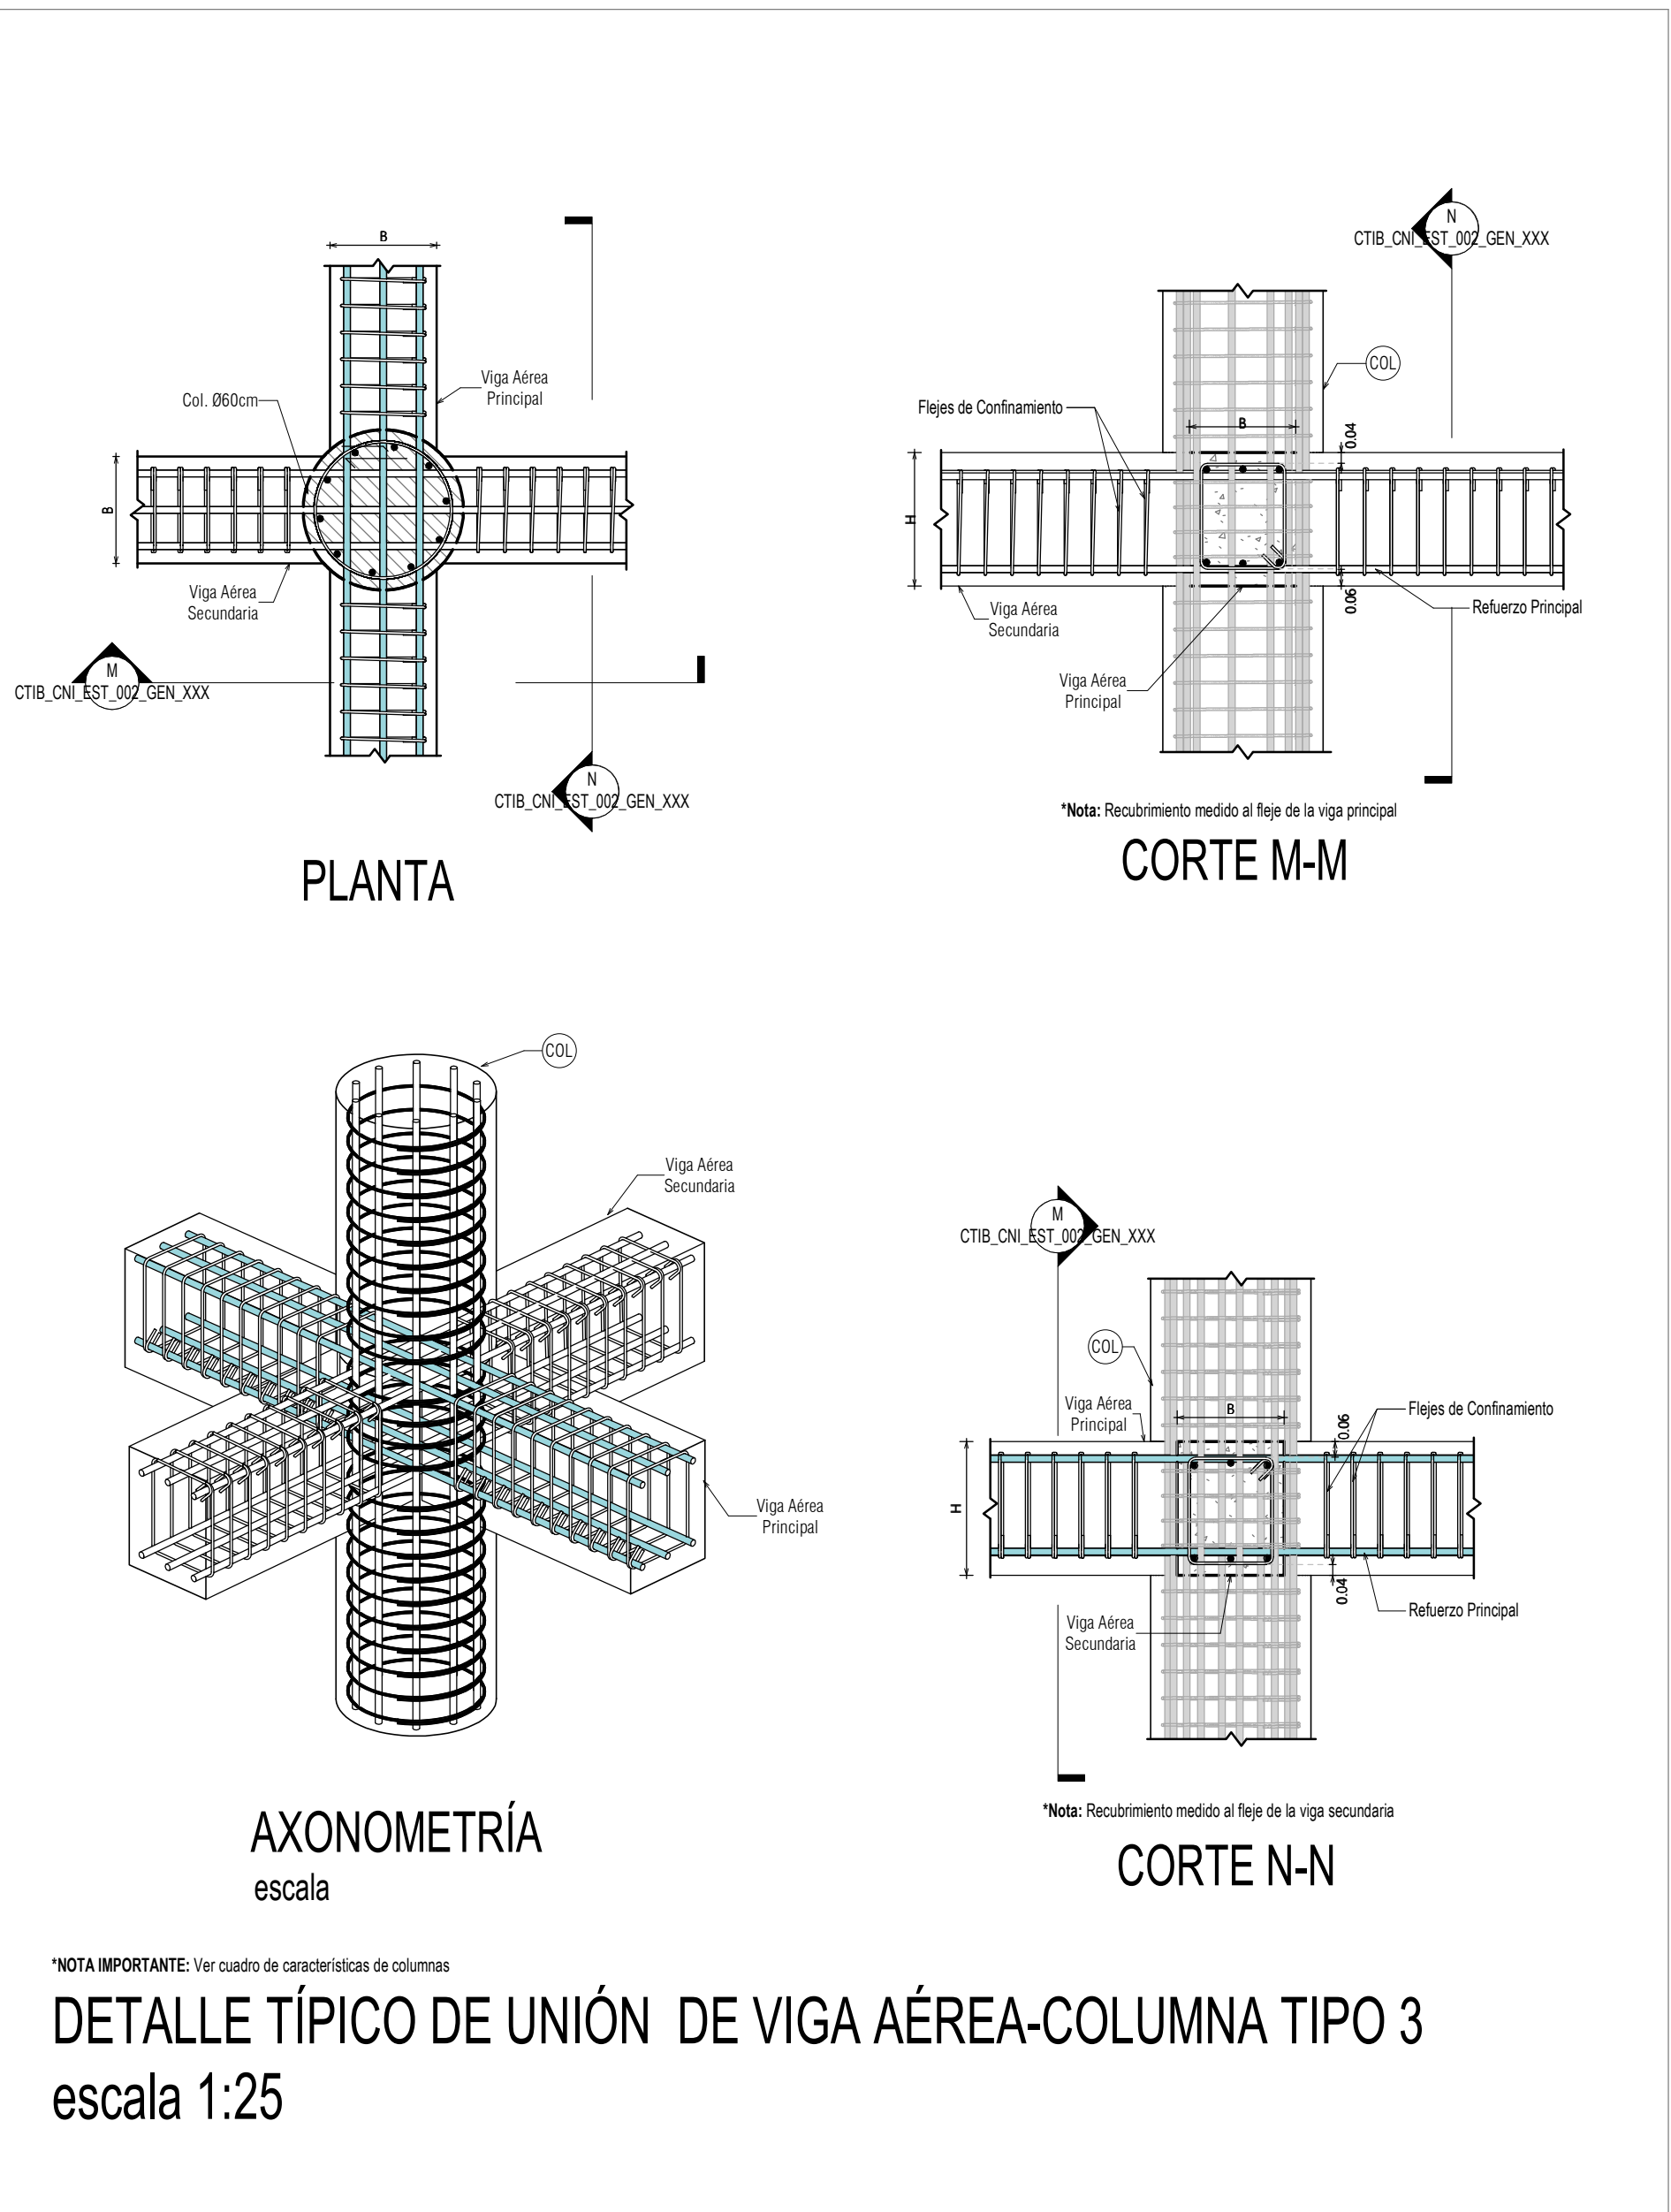
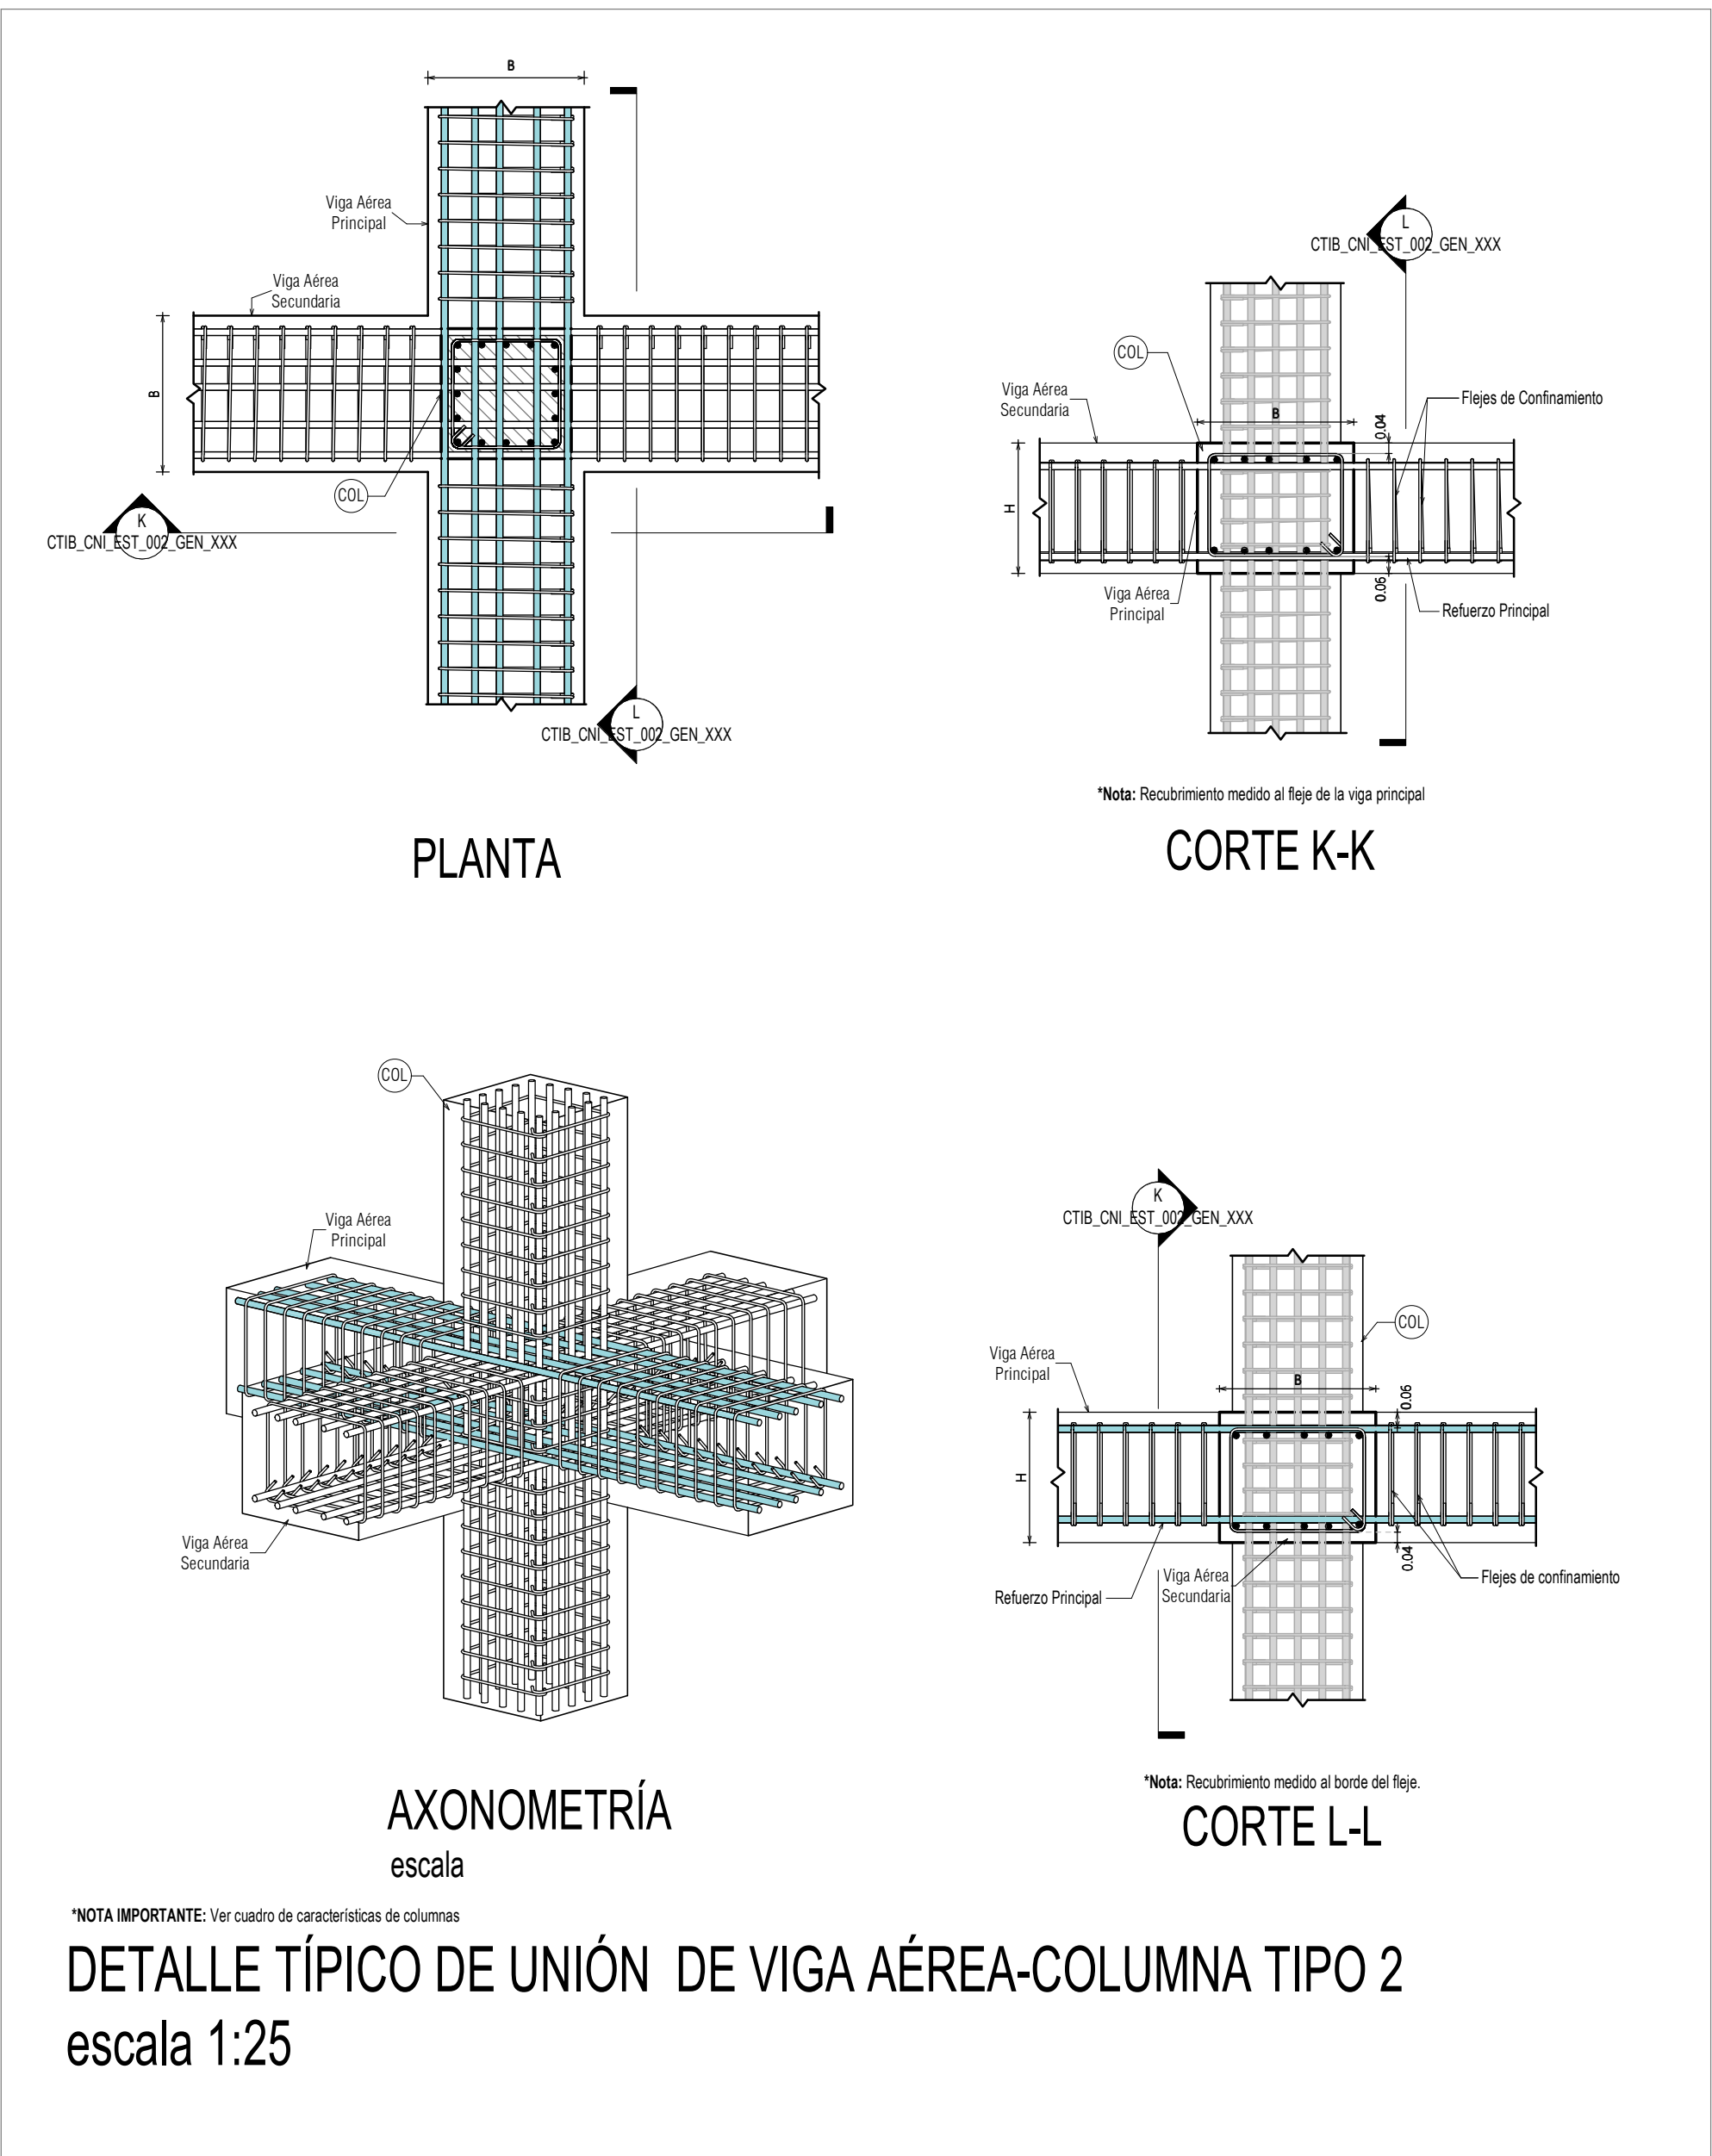


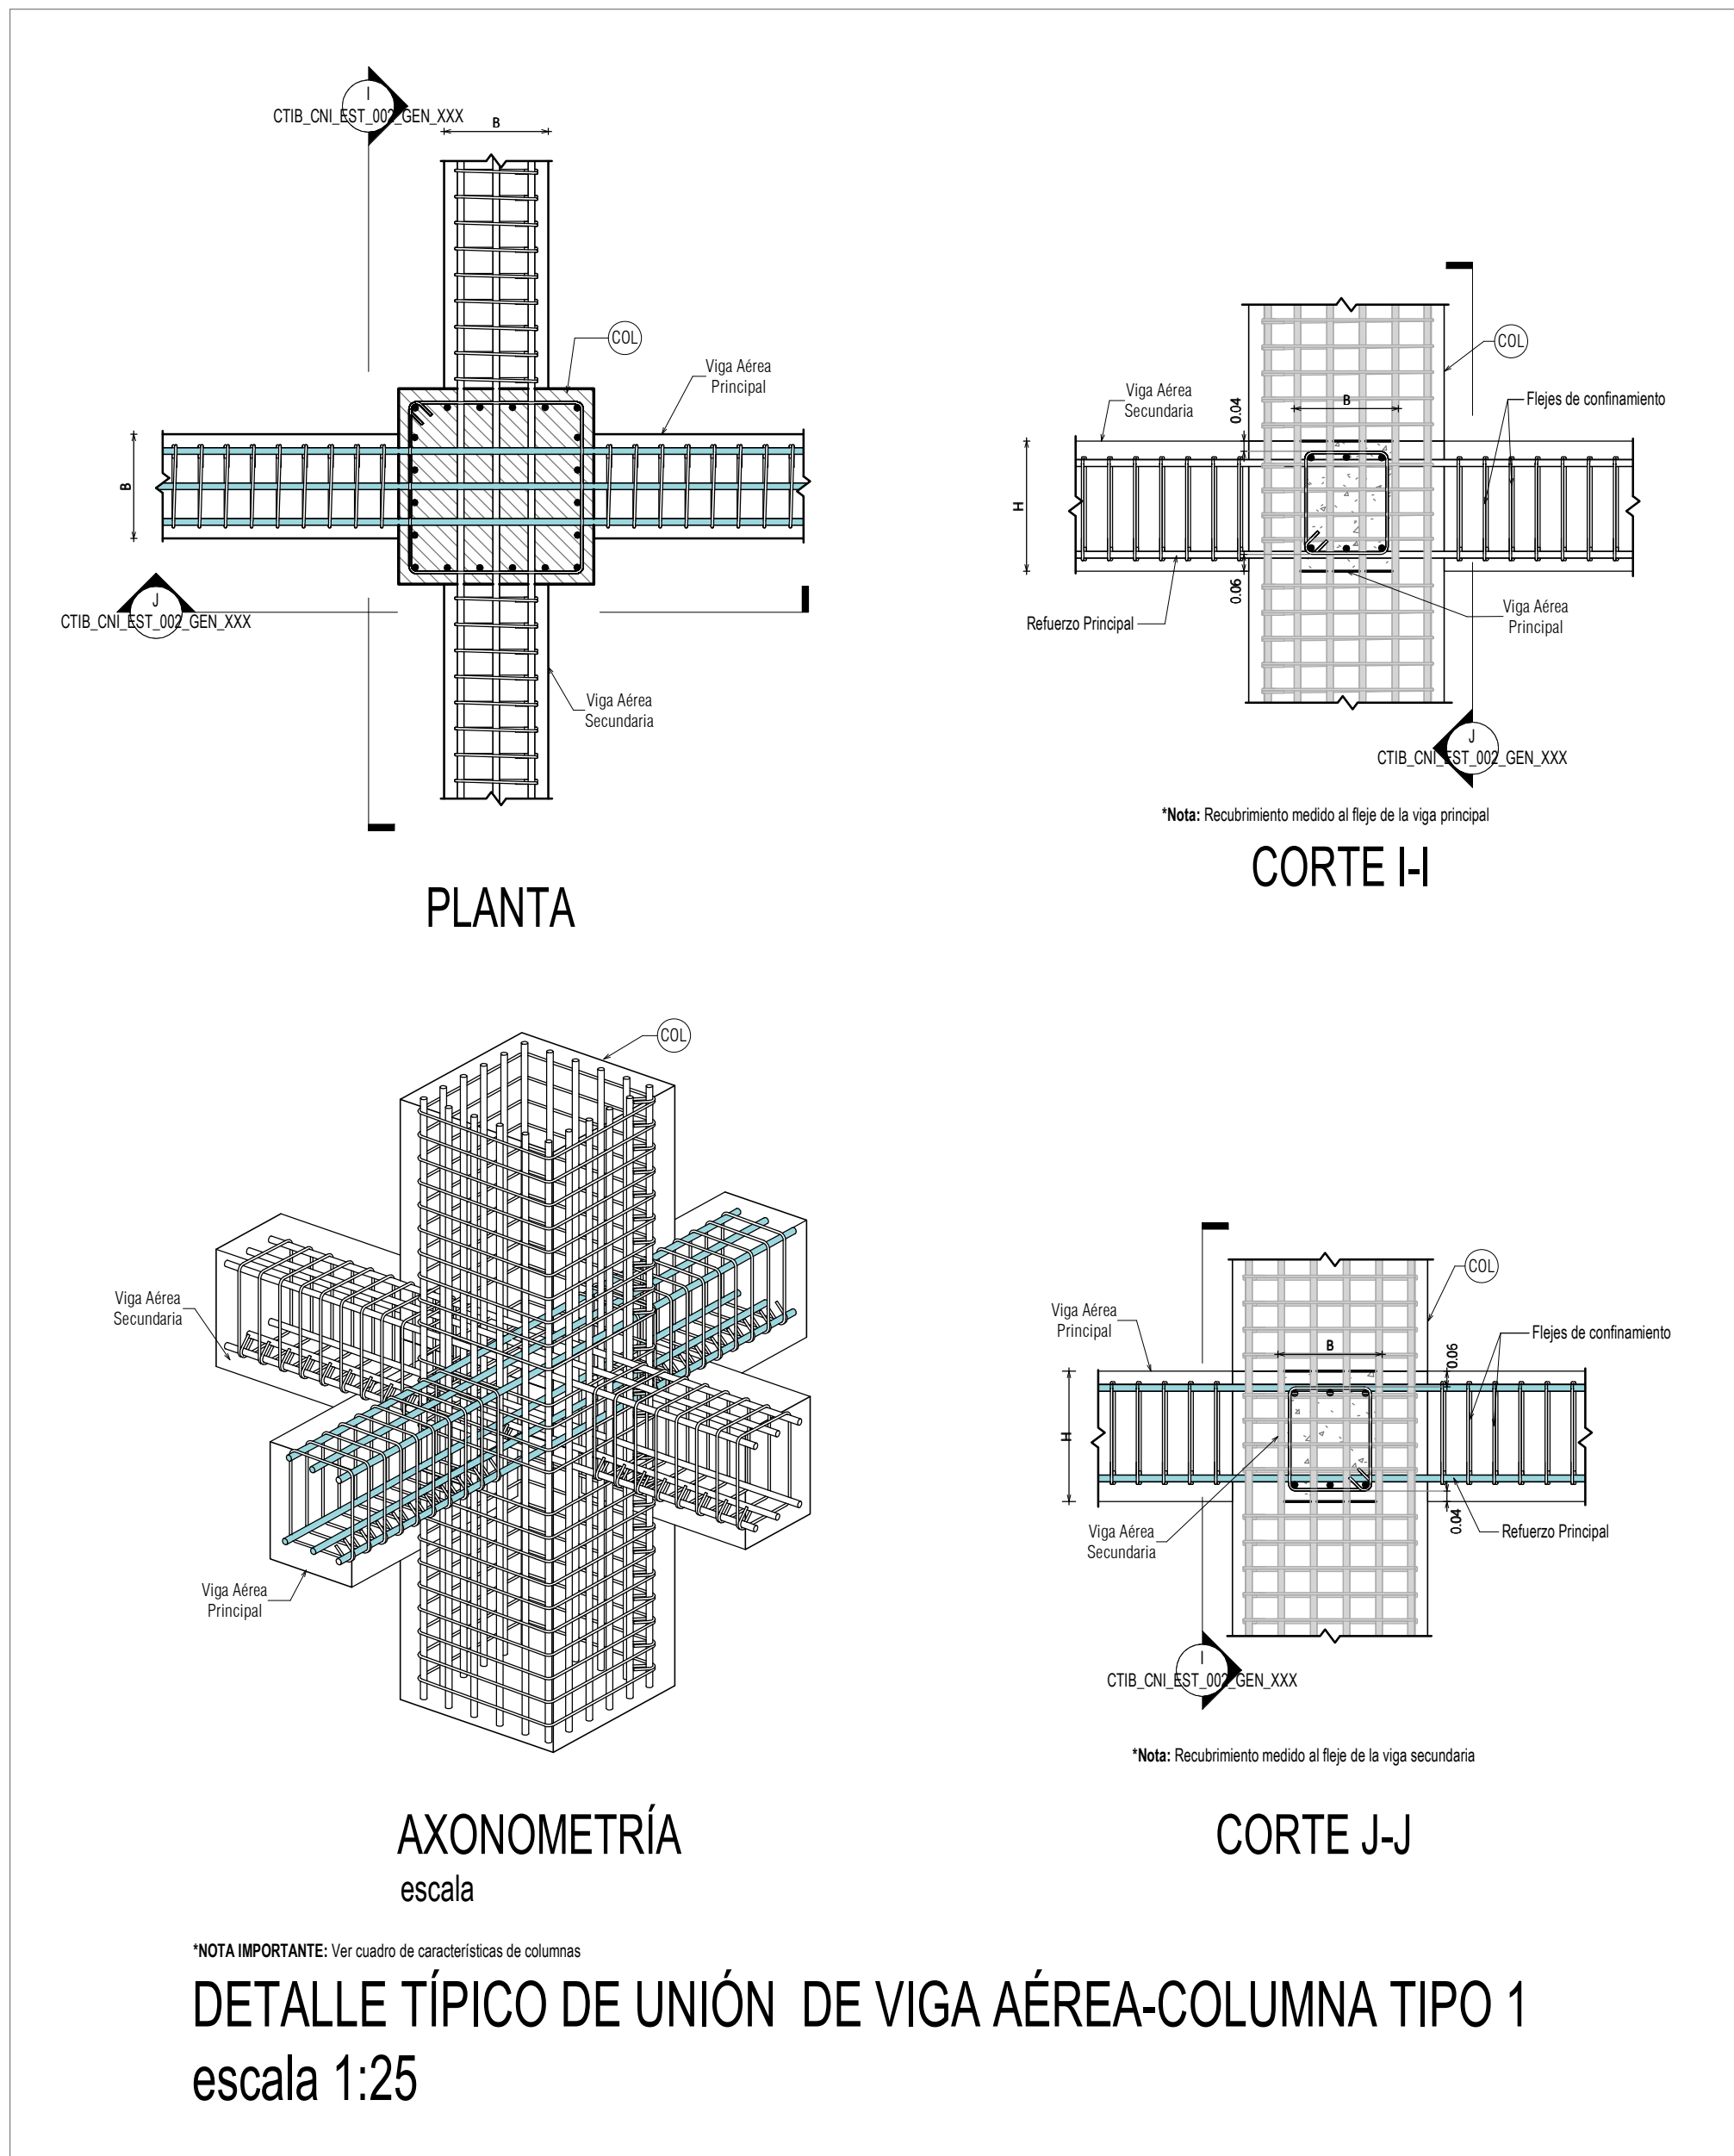




NOTAS GENERALES:

- Los detalles presentados en los planos son detalles típicos y deben emplearse a criterio del constructor, es su responsabilidad revisar las especificaciones de recubrimiento de los elementos estructurales indicados.
- Las especificaciones de los materiales se muestran en el plano E004, y deberán ser de conocimiento por parte del constructor, interventor y supervisor de obra, previo al inicio de la misma.

VIGA PRINCIPAL
Son las encargadas de transmitir las cargas y dar rigidez, se apoyan en los elementos verticales de la estructura.

VIGA o VIGUETA SECUNDARIA
Elementos horizontales que se apoyan y transmiten sus cargas a las vigas principales.

Tipo de Columna	Características
Tipo 1	Columna cuadrada con dimensiones mayores a la base de la viga.
Tipo 2	Columna cuadrada con dimensiones menores a la base de la viga.
Tipo 3	Columna circular de diámetro menor a la base de la viga de ornamentación.
Tipo 4	Columna circular de diámetro mayor a la base de la viga de ornamentación.

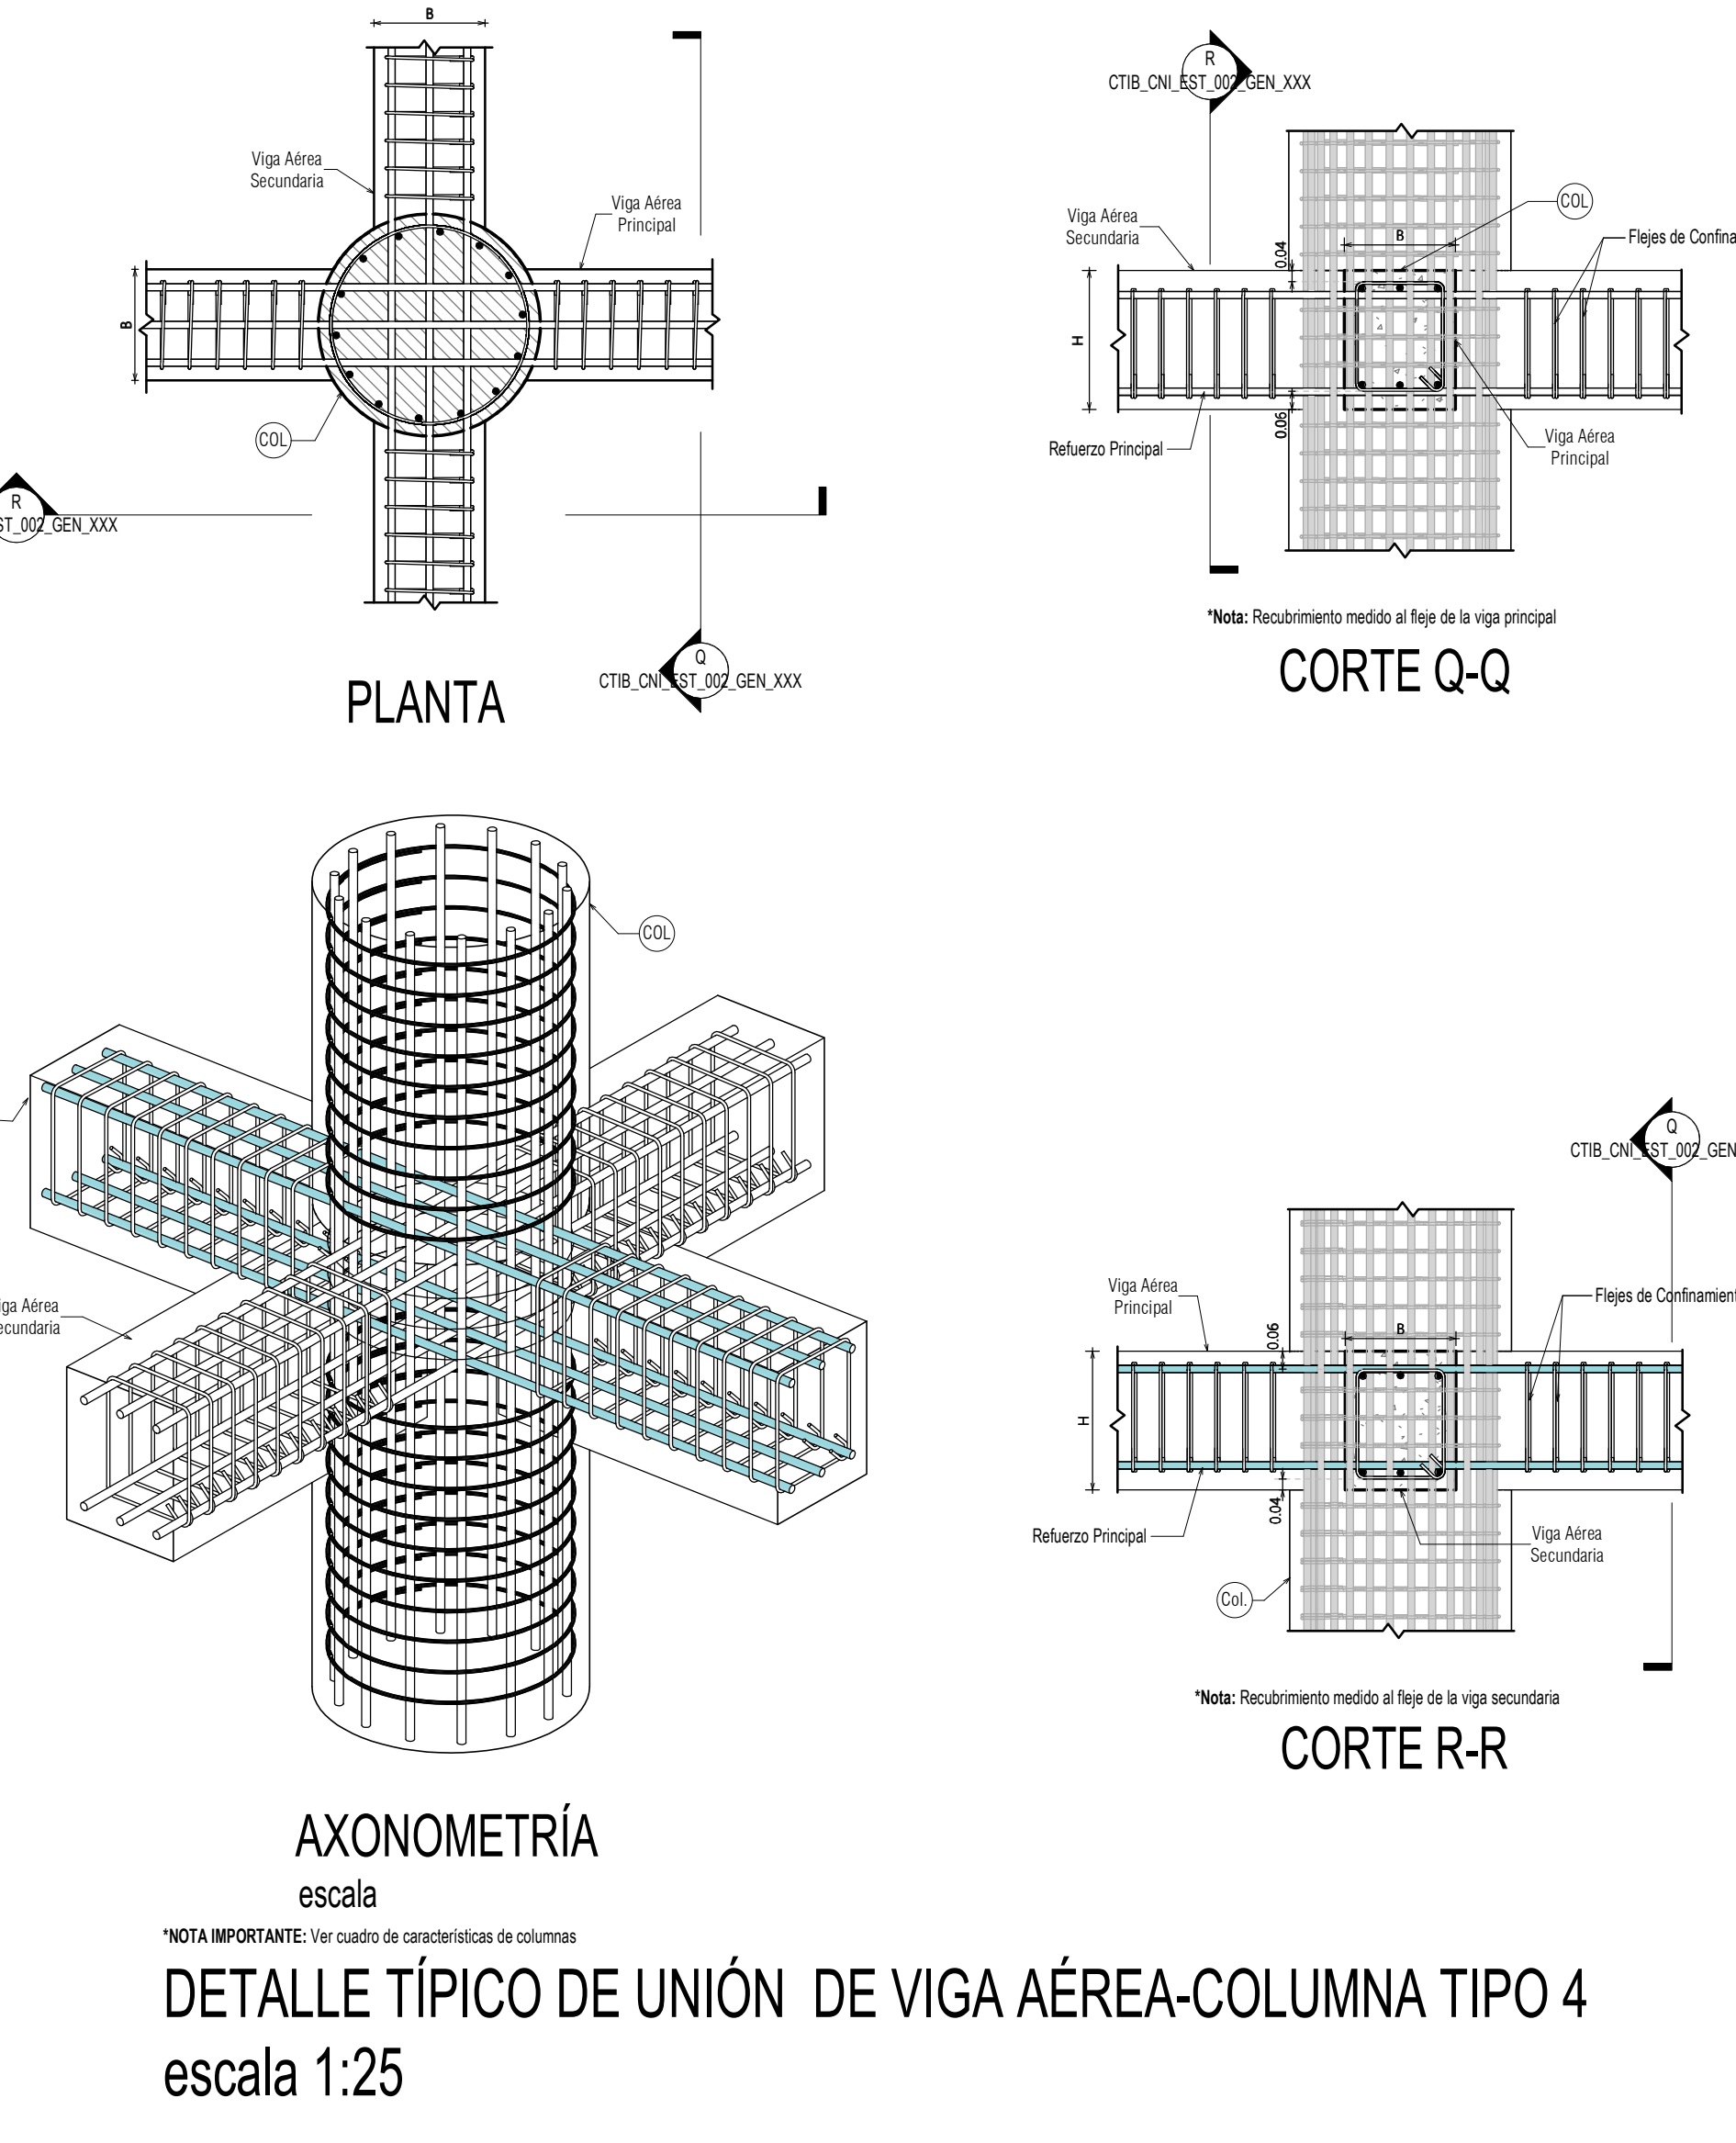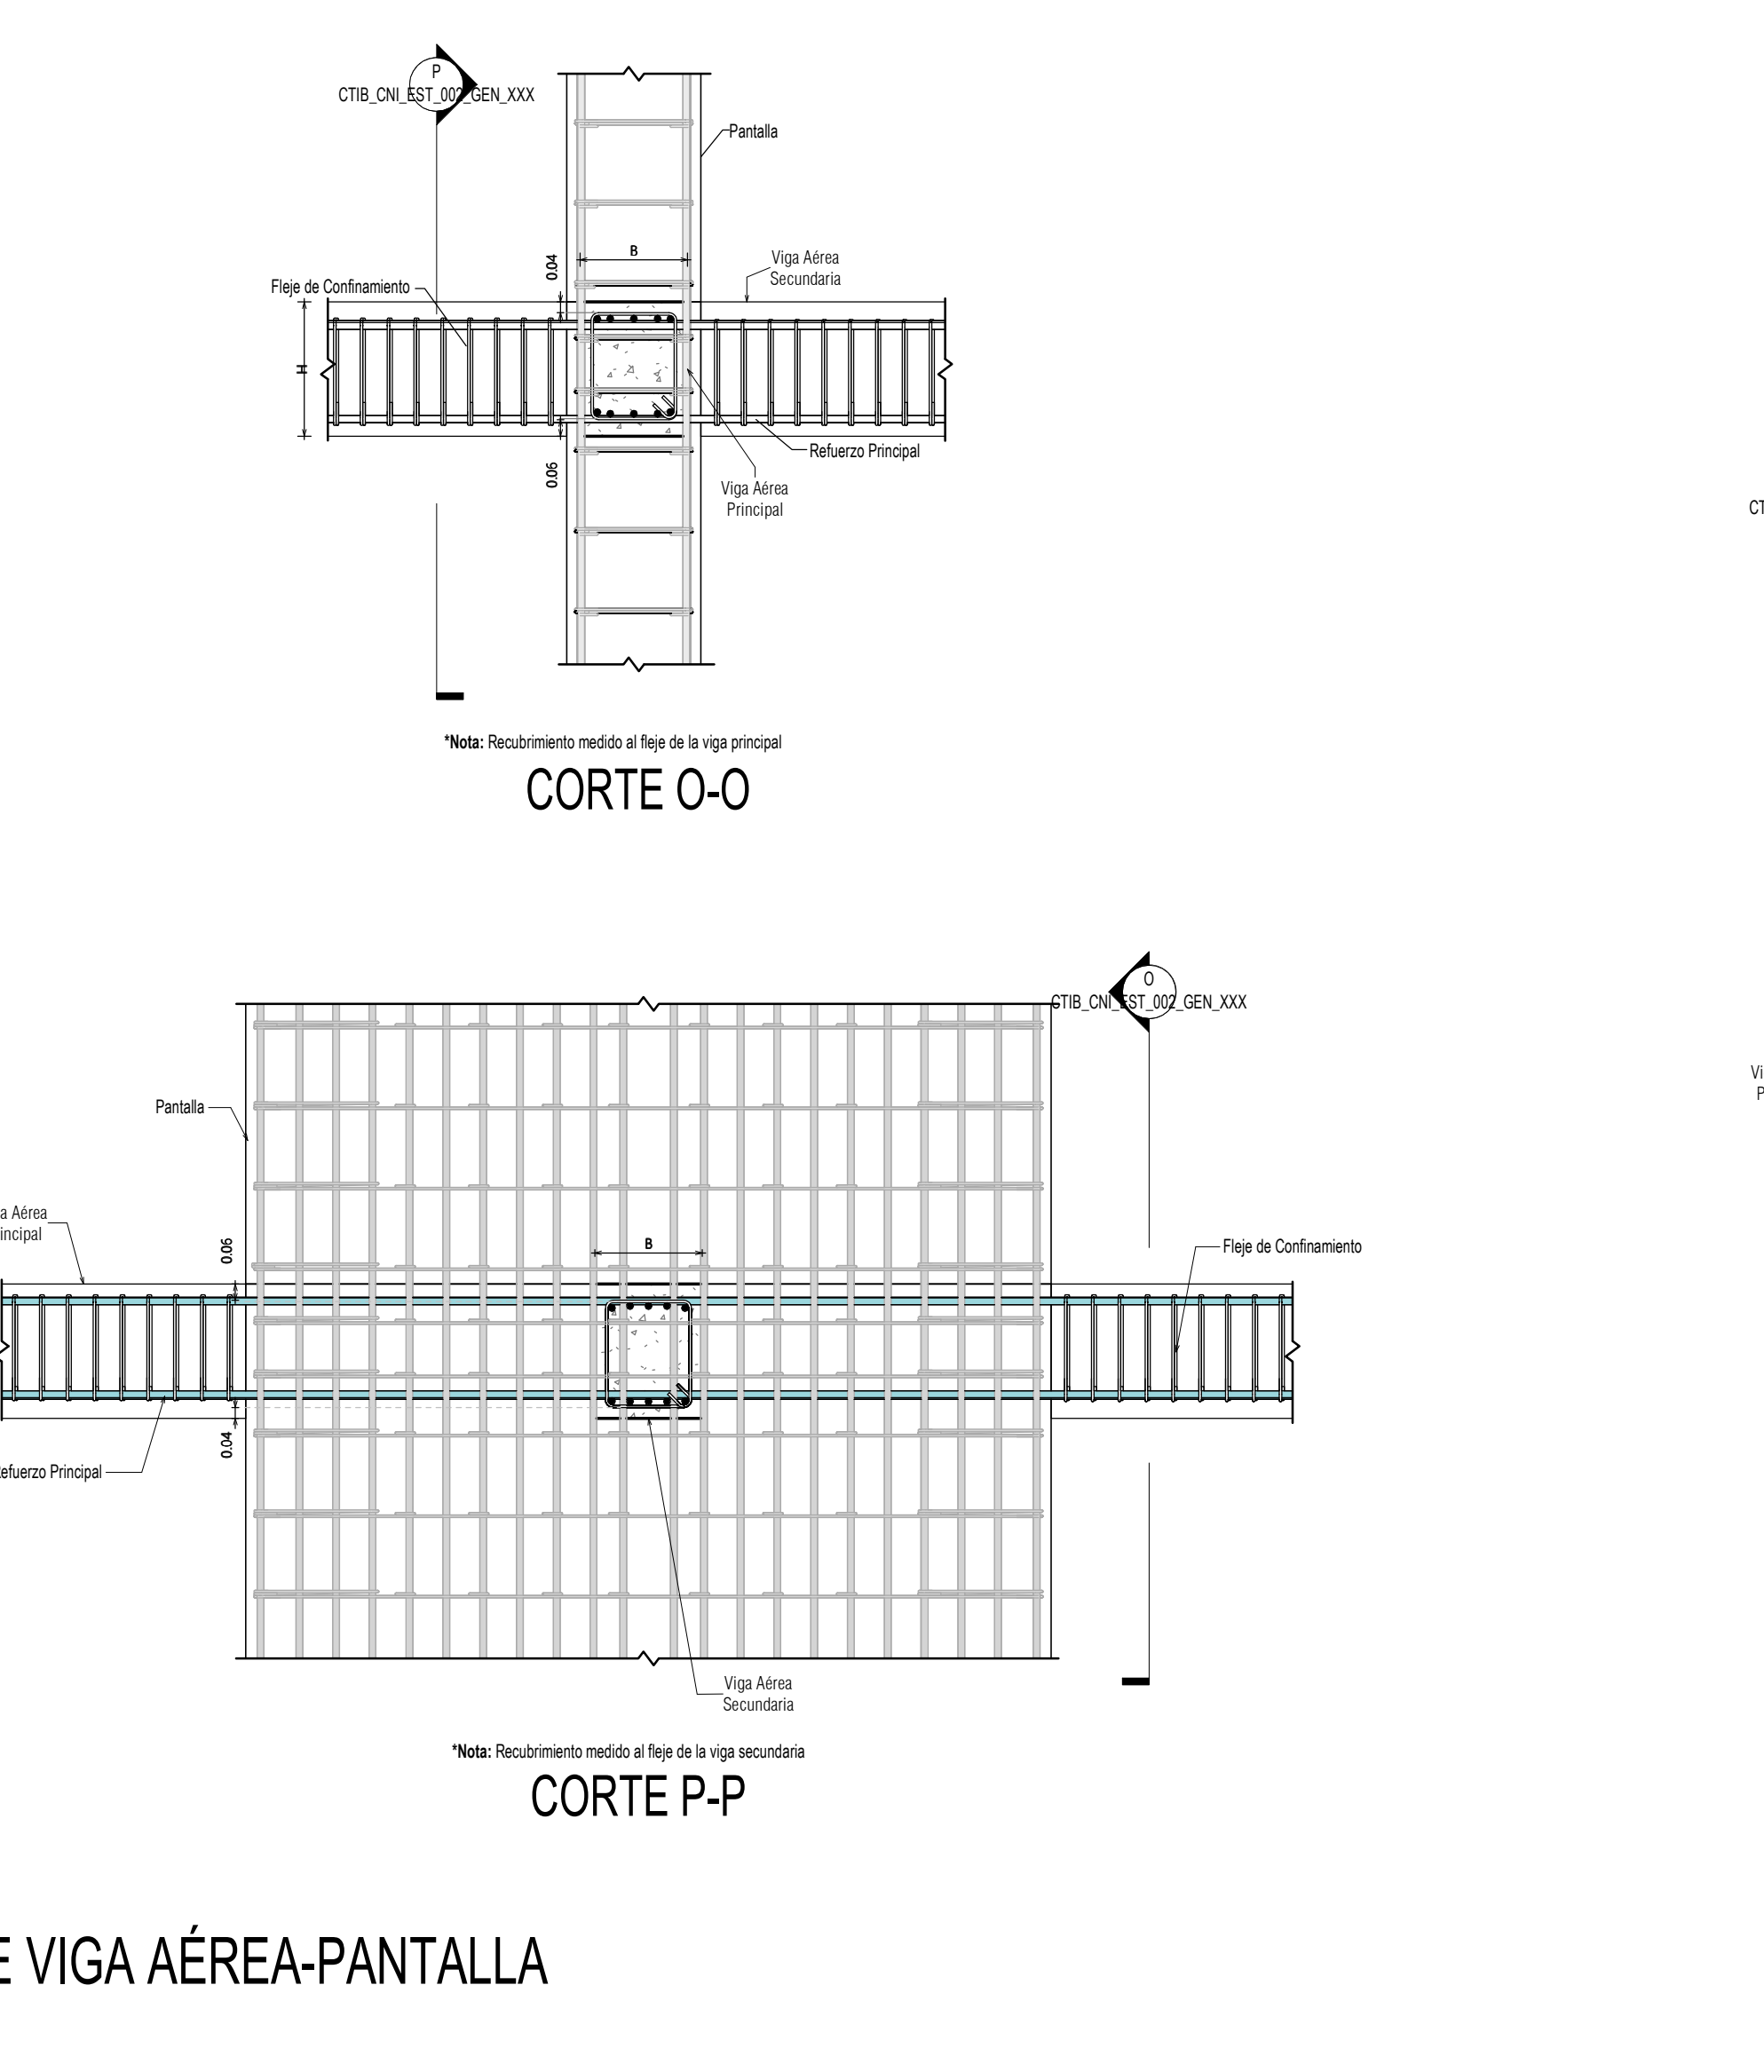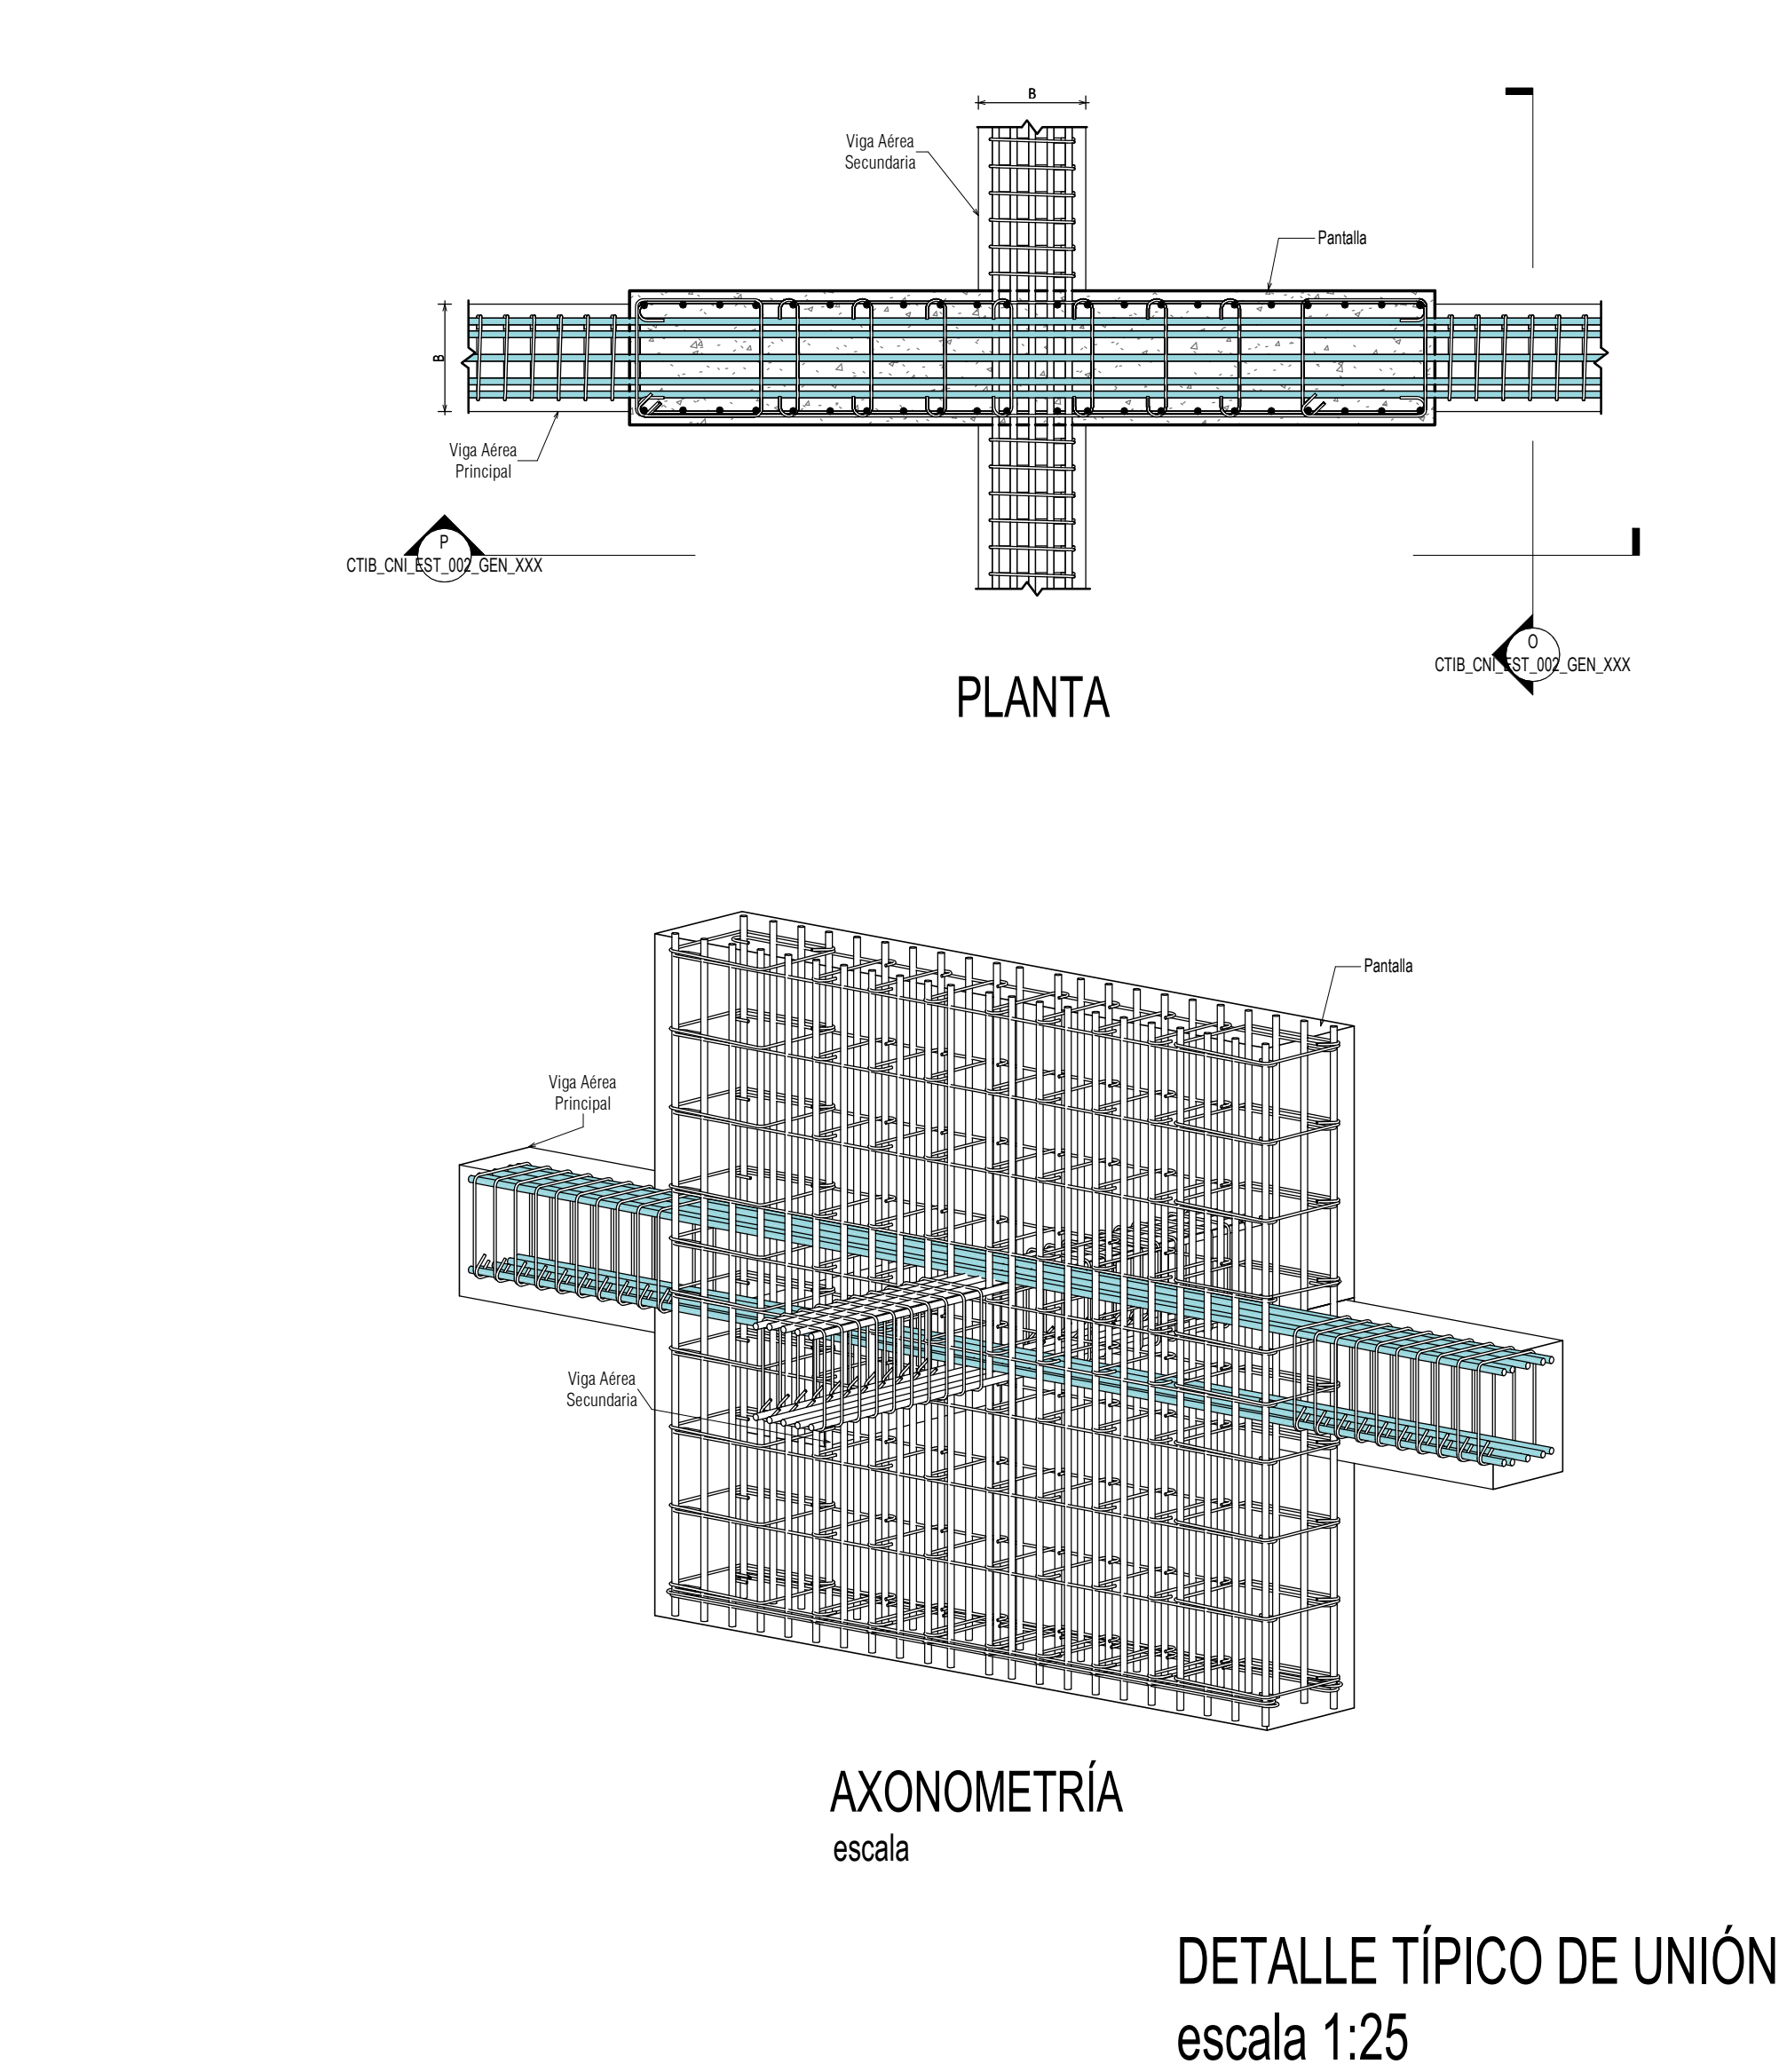

CTIB
Campus de Ciencia, Tecnología e Innovación de Bogotá - Región

corferias
Generadores de Oportunidades y Progreso

Cámara de Comercio de Bogotá
Secretaría Distrital de Desarrollo Económico

ARQUITECTO COORDINADOR

ELEQUIPO MAZZANTI + Gensler

DISÑO ESTRUCTURAL

ING. NICOLÁS PARRA GARCÍA
MAT. 23202-62063 QND

INTERVENTORIA

GUTIÉRREZ DÍAZ S.A.S.
SUPERVISIÓN Y GESTIÓN DE PROYECTOS DE CONSTRUCCIÓN

Director de Interventoría : Ing. Jorge Iván García Mancilla
Mat. 632021 148063 QND

Versión	Emisión	Descripción
AA	15-06-2023	Ingeniería básica
AB	04-08-2023	Anteproyecto
AC	01-11-2023	Anteproyecto V2 50%
AD	15-12-2023	Anteproyecto V2 100%
DD	13-03-2024	Curaduría V2
EE	10-05-2024	Proyecto final 100%
EF	31-05-2024	Respuesta Obs.100%
FF	21-06-2024	Entrega final
01	26-07-2024	ENTREGA FINAL

PROYECTO:

CAMPUS DE CIENCIA, TECNOLOGÍA E INNOVACIÓN DE BOGOTÁ
MAT. No. 50C-0025470

FASE

PROYECTO CONSTRUCTIVO

PROPÓSITO DE EMISIÓN

Curaduría	☐	Coordinación	☐
Revisión	☐	Construcción	☒
Entrega Cliente	☒		

ENTREGA FINAL

APTO PARA CONSTRUCCIÓN

KEY PLAN

Fecha: 26-07-2024

Escala: 1 : 25

ESPECIFICACIONES GENERALES

CTIB_CNI_EST_002_GEN_XXX_01