




15/05/2024 13:03:44 p. m.

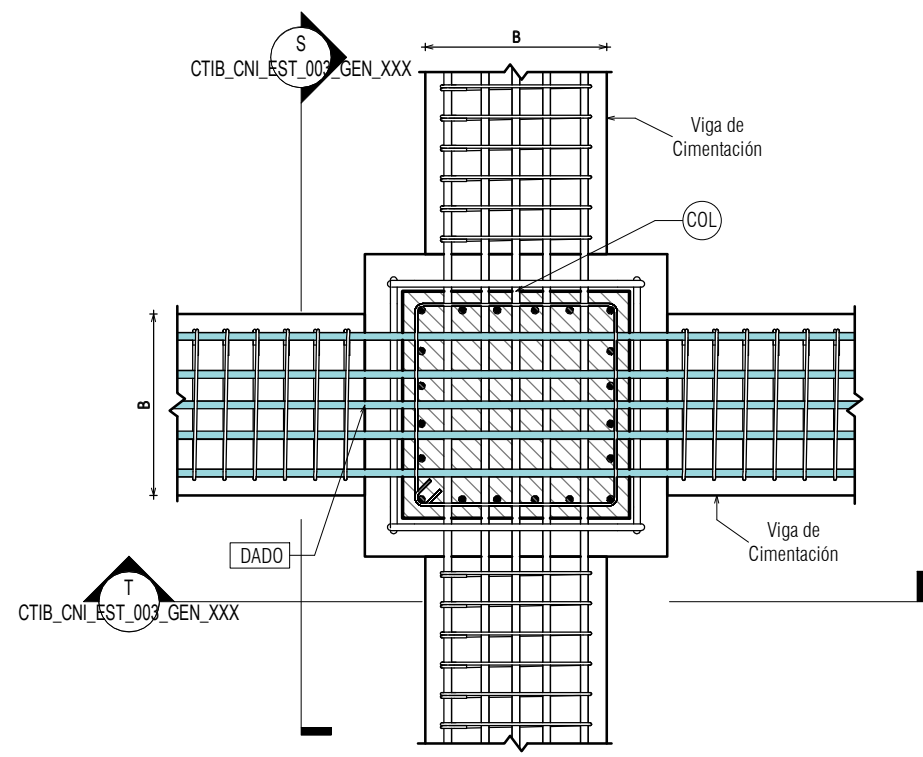


PLANTA

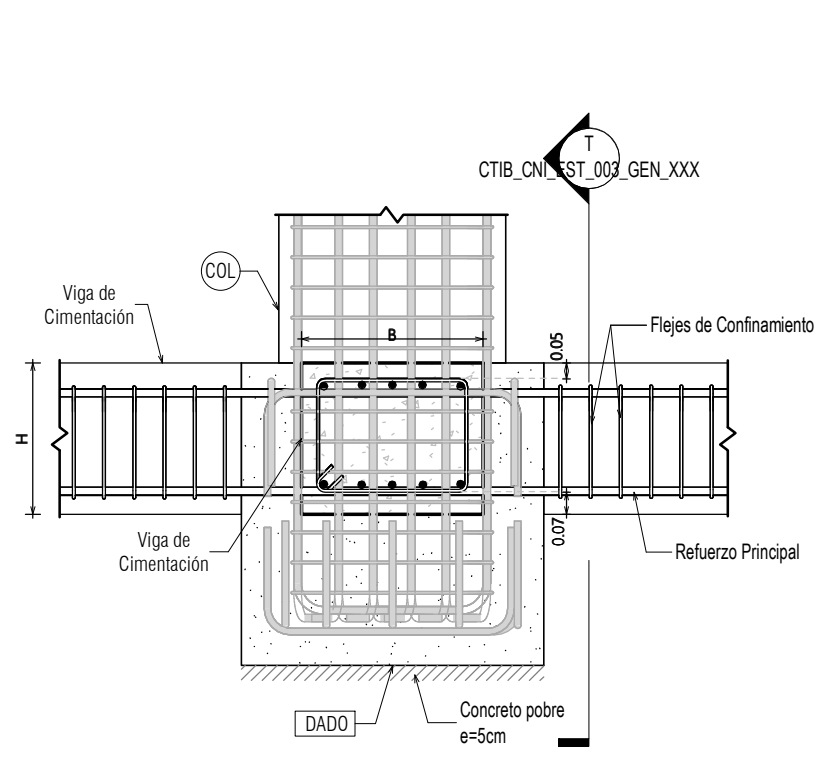


CORTE S-S

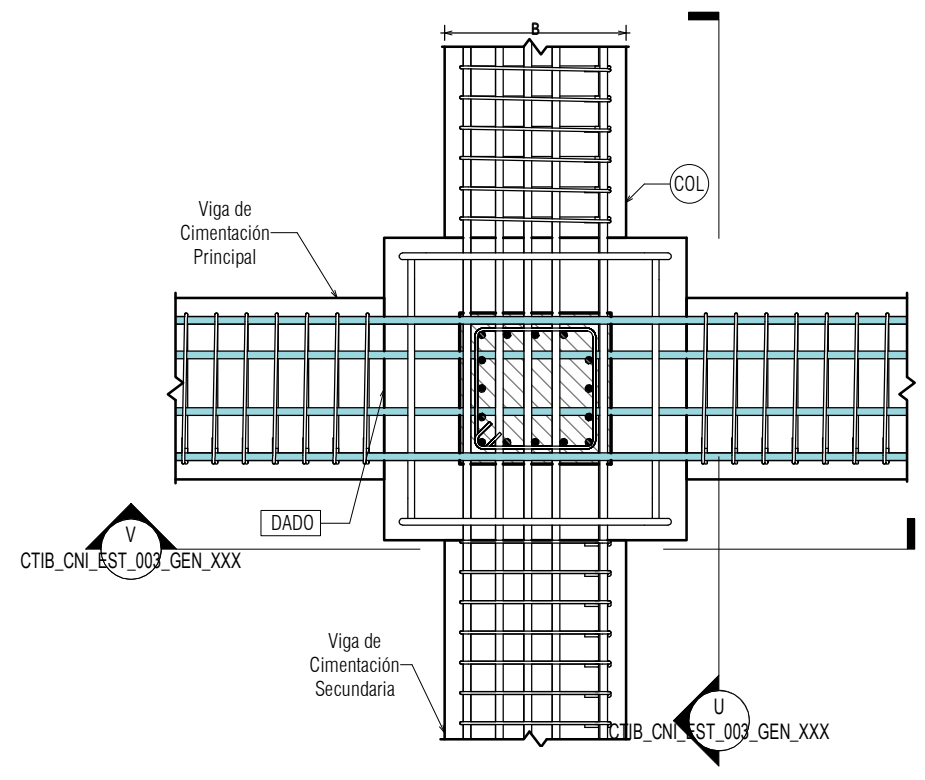


PLANTA

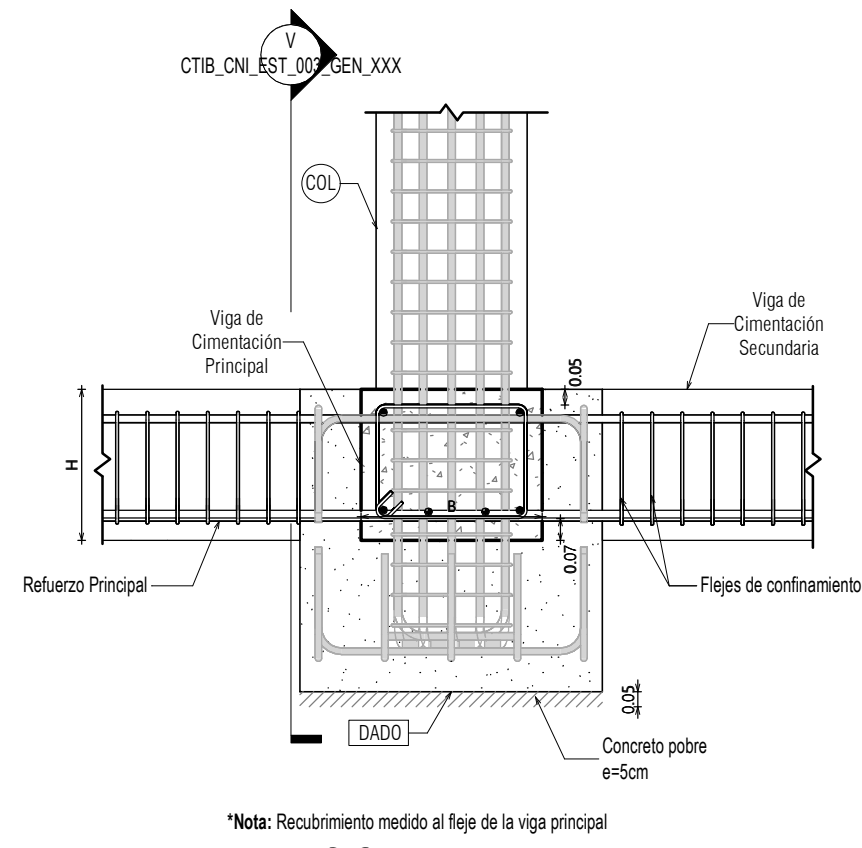


CORTE U-U

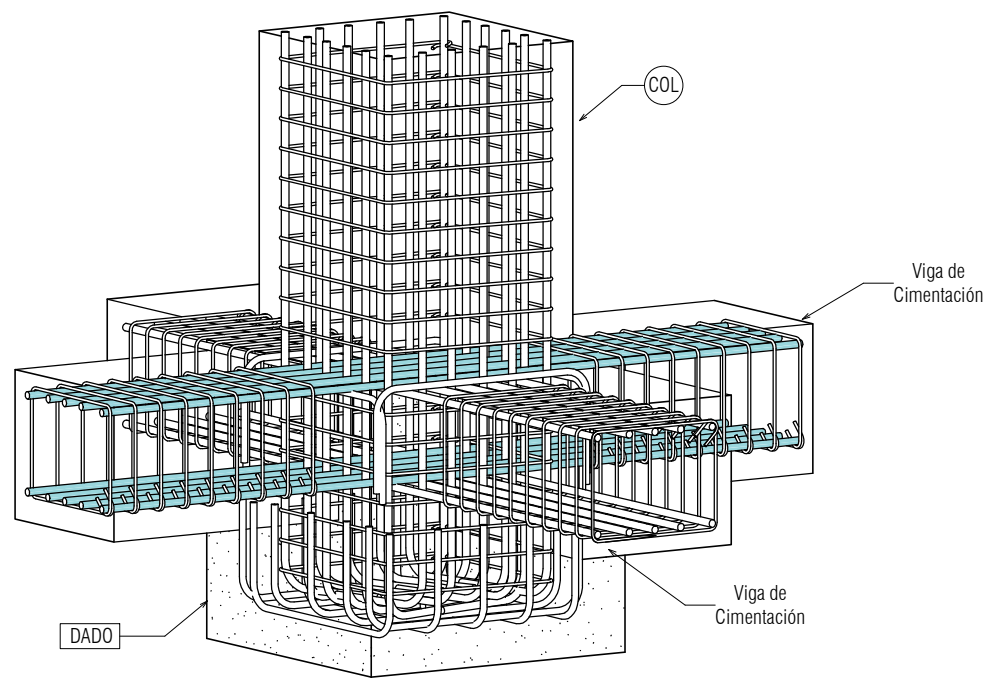


AXONOMETRÍA  
escala

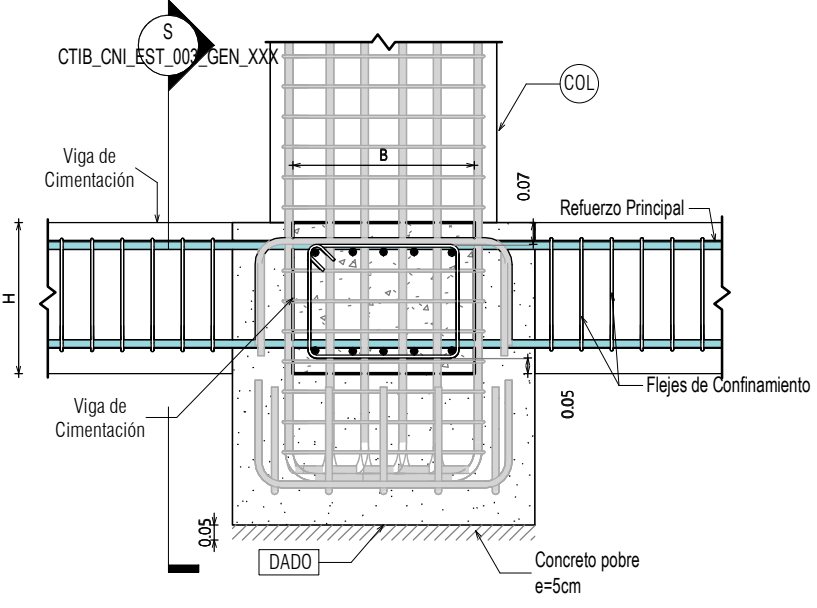

CORTE T-T

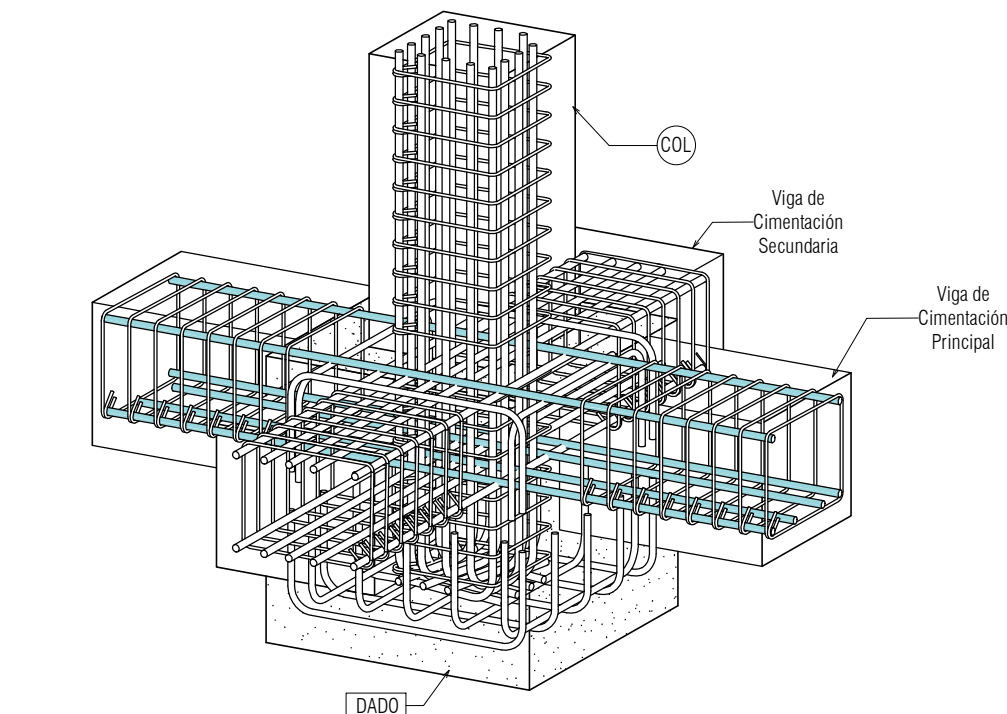

AXONOMETRÍA  
escala

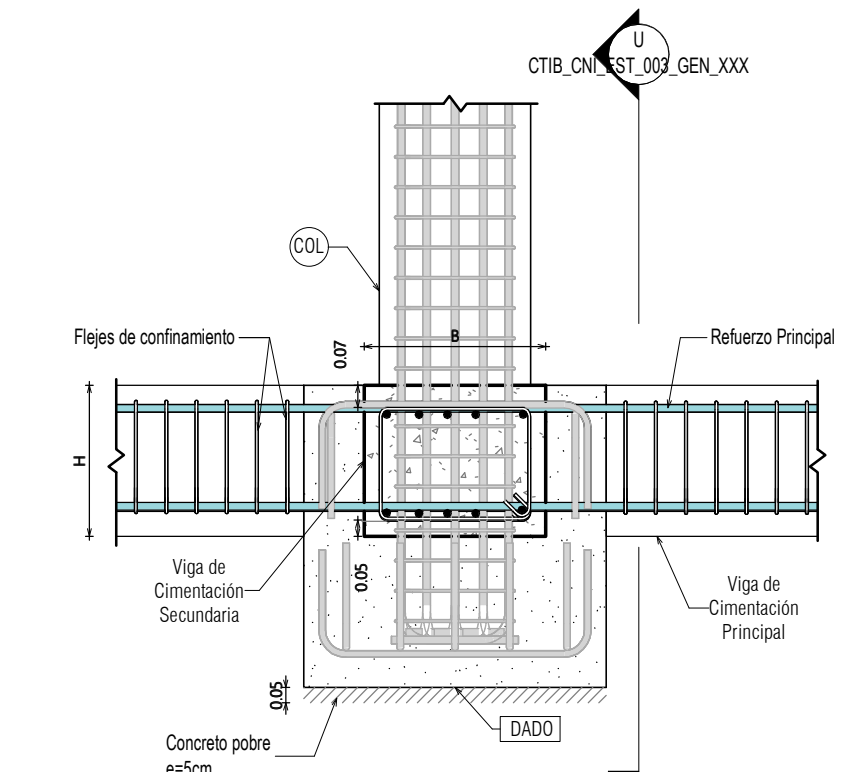

CORTE V-V

\*NOTA IMPORTANTE: Ver cuadro de características de columnas


## DETALLE TÍPICO DE UNIÓN DE VIGA CIM-COLUMNA TIPO 1

escala 1:25


\*NOTA IMPORTANTE: Ver cuadro de características de columnas

## DETALLE TÍPICO DE UNIÓN DE VIGA CIM-COLUMNA TIPO 2


escala 1:25

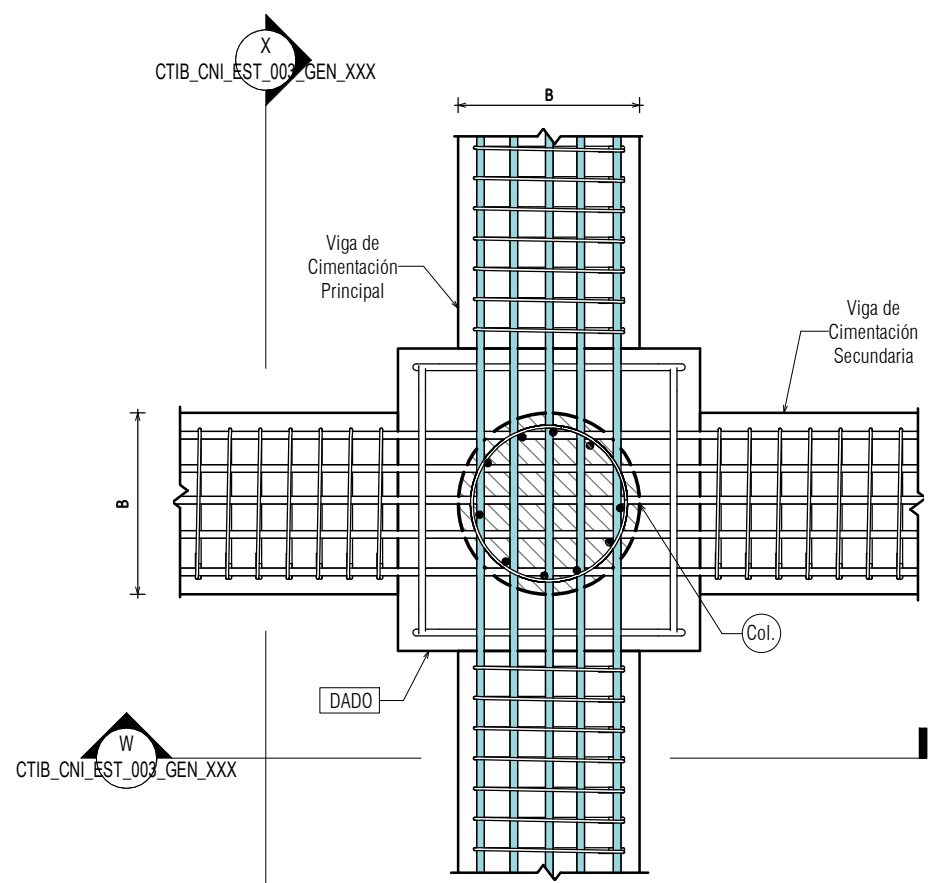


PLANTA

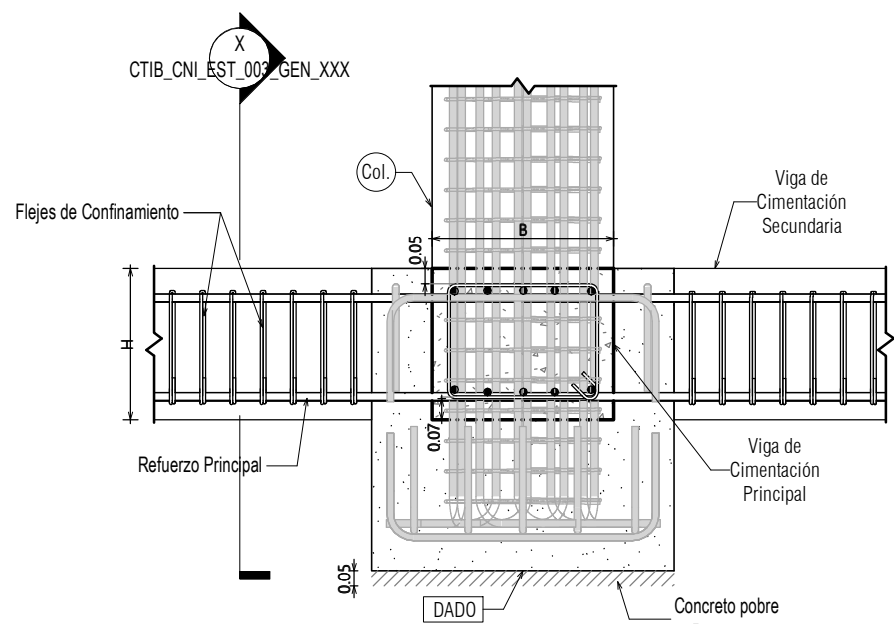


CORTE W-W

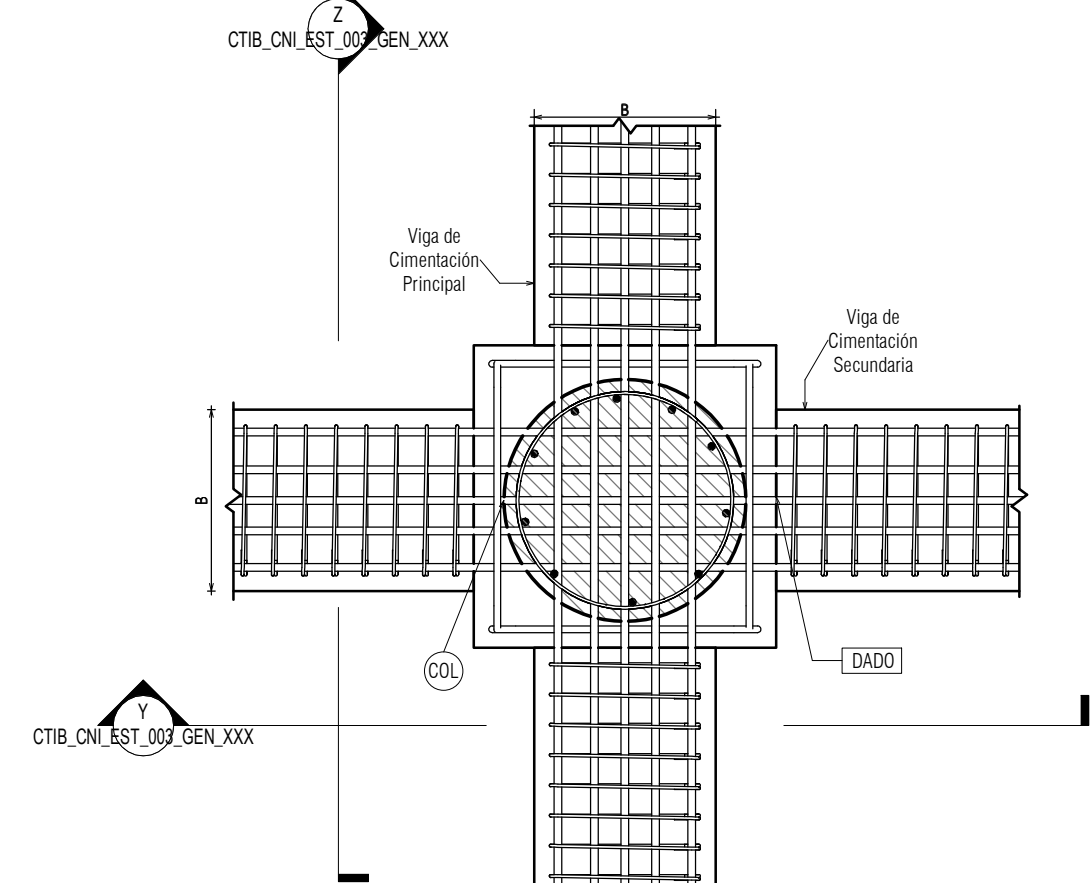


PLANTA

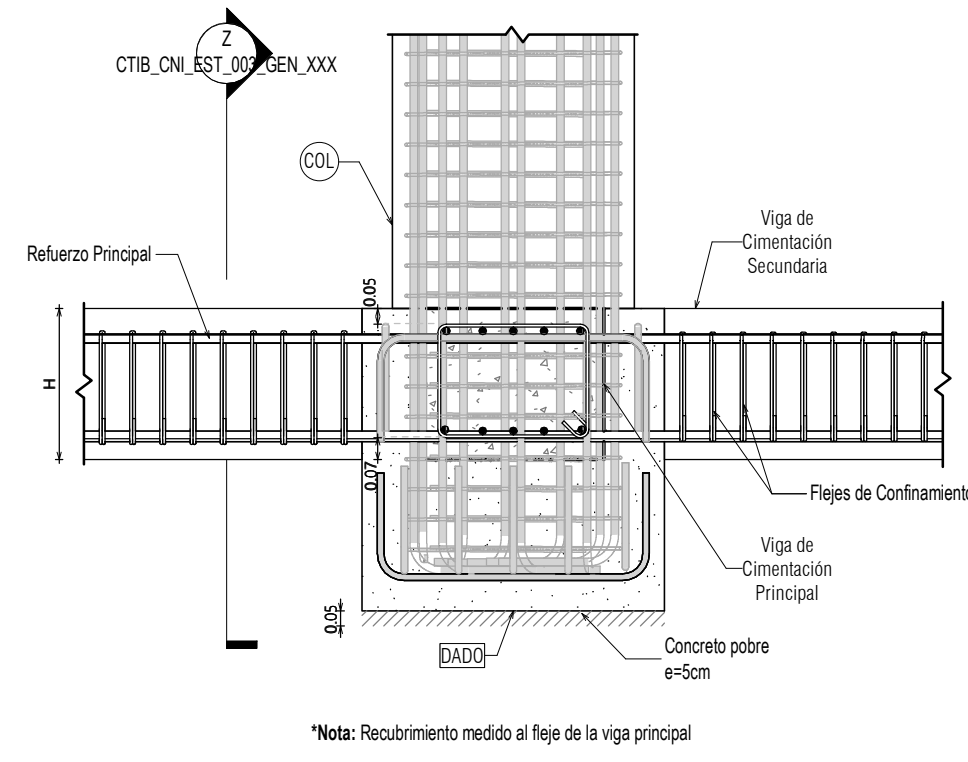


CORTE Y-Y

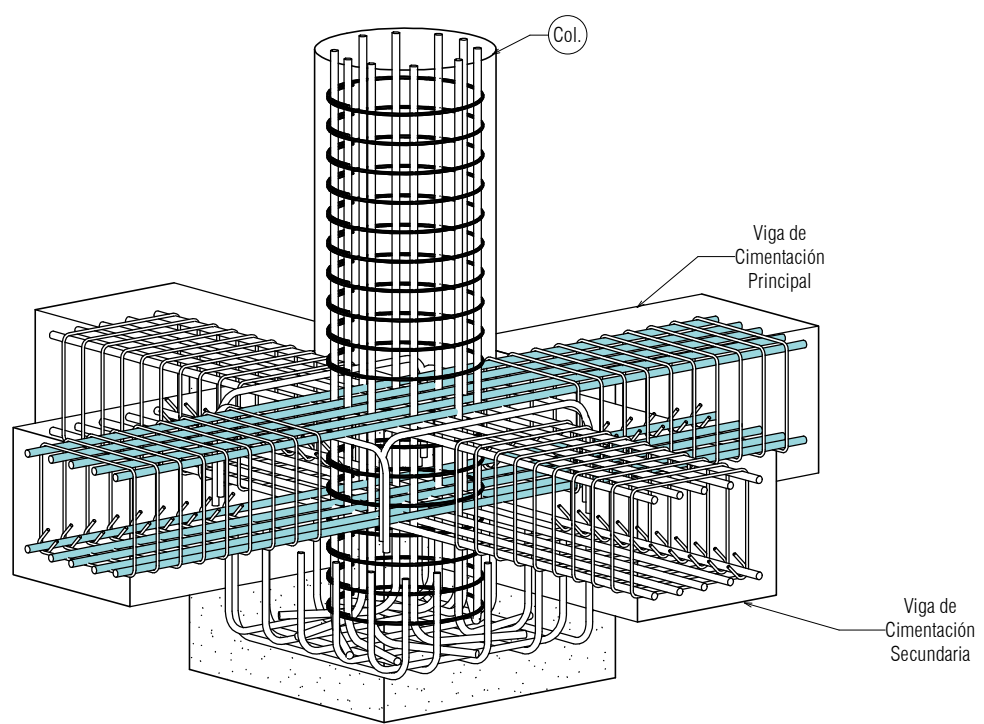


AXONOMETRÍA  
escala

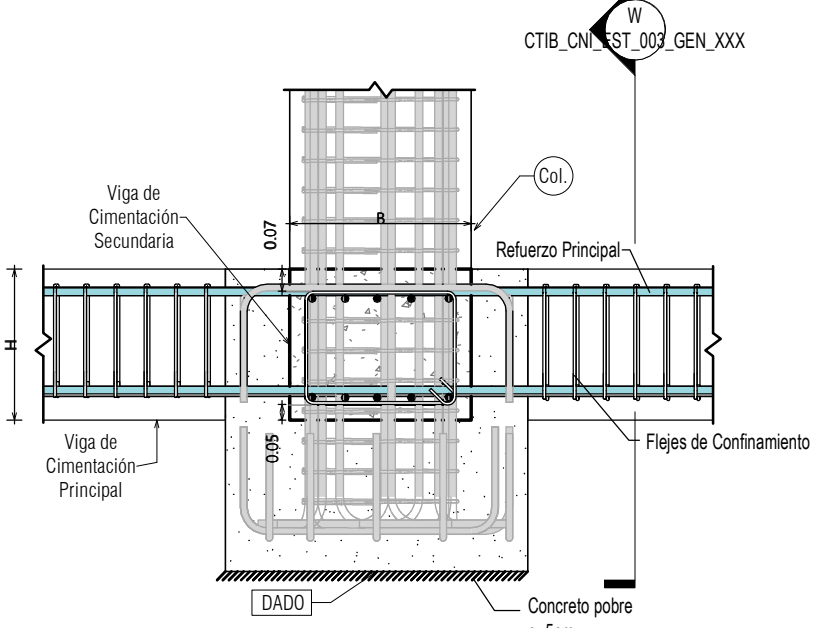

CORTE X-X

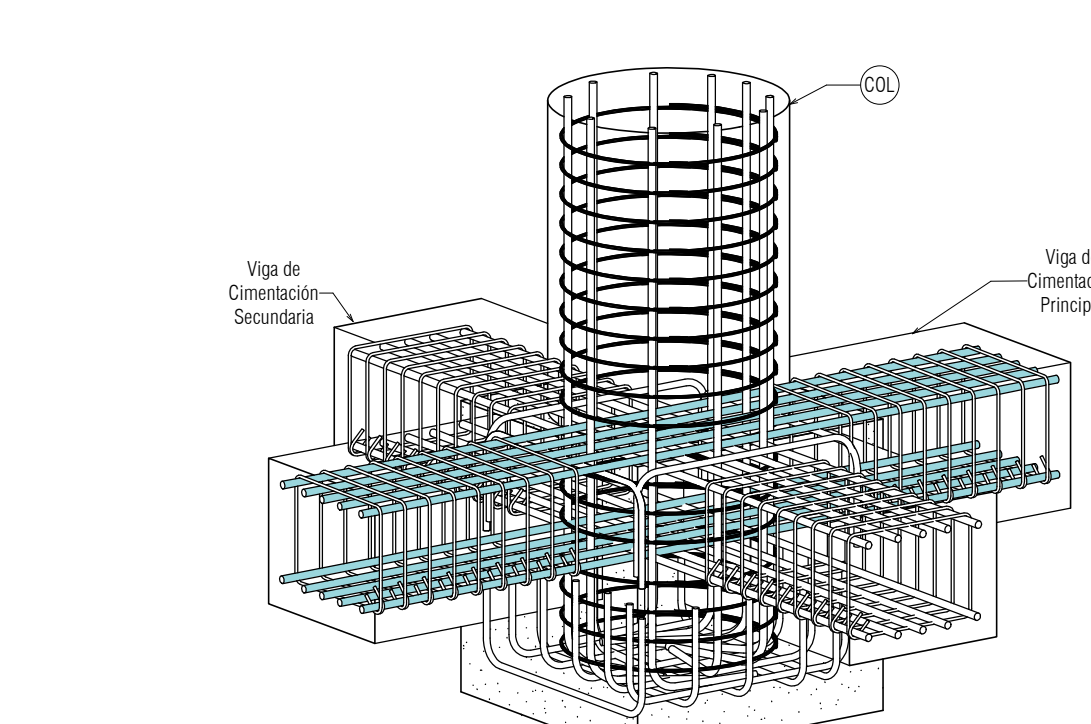

AXONOMETRÍA  
escala

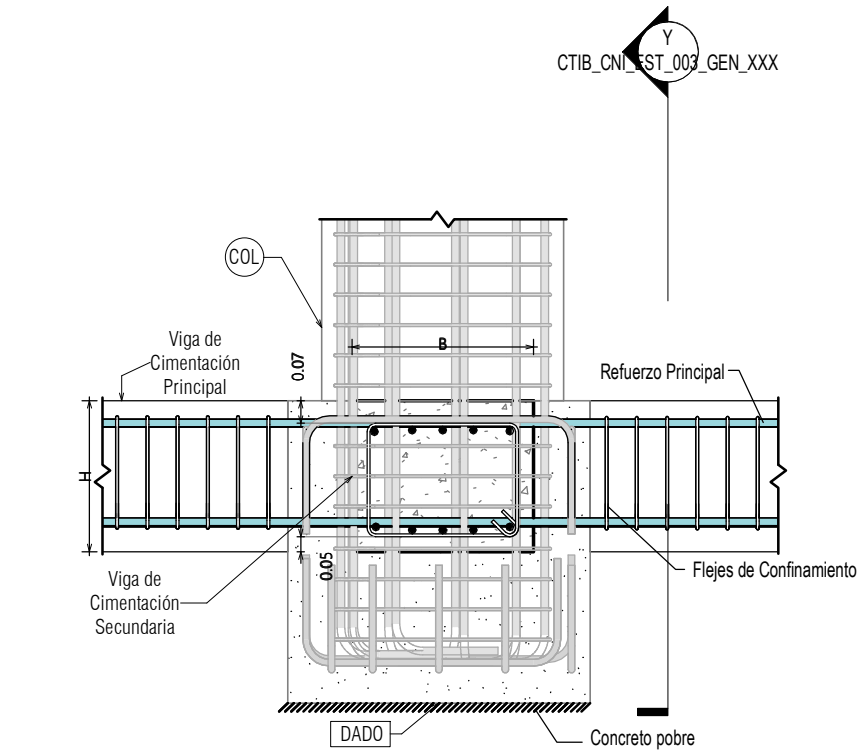

CORTE Z-Z

\*NOTA IMPORTANTE: Ver cuadro de características de columnas

## DETALLE TÍPICO DE UNIÓN DE VIGA CIM-COLUMNA TIPO 3

escala 1:25

\*NOTA IMPORTANTE: Ver cuadro de características de columnas

## DETALLE TÍPICO DE UNIÓN DE VIGA CIM-COLUMNA TIPO 4

escala 1:25

### NOTAS GENERALES:

- Los detalles presentados en los planos son detalles típicos y deben emplearse a criterio del constructor, de su responsabilidad revisar las especificaciones de recubrimiento de los elementos estructurales indicados.
- Las especificaciones de los materiales se muestran en el plano E000, y deberán ser de conocimiento por parte del constructor, interventor y supervisor de obra, previo al inicio de la misma.

VIGA PRINCIPAL  
Son las encargadas de transmitir las cargas y dar rigidez, se apoyan en los elementos verticales de la estructura.

VIGA u VIGUETA SECUNDARIA  
Elementos horizontales que se apoyan y transmiten sus cargas a las vigas principales.

| Tipo de Columna | Características                                                         |
|-----------------|-------------------------------------------------------------------------|
| Tipo 1          | Columna cuadrada con dimensiones mayores a la base de la viga.          |
| Tipo 2          | Columna cuadrada con dimensiones menores a la base de la viga.          |
| Tipo 3          | Columna circular de diámetro menor a la base de la viga de cimentación. |
| Tipo 4          | Columna circular de diámetro mayor a la base de la viga de cimentación. |

**CTIB**

Campus de Ciencia, Tecnología e Innovación de Bogotá - Región



ARQUITECTO COORDINADOR

**ELEQUIPO MAZZANTI + Gensler**

DISEÑO ESTRUCTURAL



*Ing. Nicolás Farrar García*

DISEÑADOR: ING. NICOLÁS FARRAR GARCÍA  
MAT. 23202-62063 QND

INTERVENTORIA



**GUTIÉRREZ DÍAZ S.A.S.**  
SUPERVISIÓN Y GESTIÓN DE PROYECTOS DE CONSTRUCCIÓN

*Ing. Jorge Iván García Mancilla*

Director de Interventoría: Ing. Jorge Iván García Mancilla  
Mat. 632021-148063 QND

| Versión | Emisión    | Descripción          |
|---------|------------|----------------------|
| AA      | 15-06-2023 | Ingeniería básica    |
| AB      | 04-08-2023 | Anteproyecto         |
| AC      | 01-11-2023 | Anteproyecto V2 50%  |
| AD      | 15-12-2023 | Anteproyecto V2 100% |
| DD      | 13-03-2024 | Curaduría V2         |
| EE      | 10-05-2024 | Proyecto final 100%  |
| FF      | 31-05-2024 | Respuesta Obs.100%   |
| FF      | 21-06-2024 | Entrega final        |
| 01      | 26-07-2024 | ENTREGA FINAL        |

PROYECTO:

CAMPUS DE CIENCIA, TECNOLOGÍA E INNOVACIÓN DE BOGOTÁ  
MAT. No. SOC-00252470

FASE

PROYECTO CONSTRUCTIVO

PROPÓSITO DE EMISIÓN


|                 |                                     |              |                                     |
|-----------------|-------------------------------------|--------------|-------------------------------------|
| Curaduría       | <input type="checkbox"/>            | Coordinación | <input type="checkbox"/>            |
| Revisión        | <input type="checkbox"/>            | Construcción | <input checked="" type="checkbox"/> |
| Entrega Cliente | <input checked="" type="checkbox"/> |              |                                     |

ZONIFICACIÓN

|          |
|----------|
| Nivel 24 |
| Nivel 23 |
| Nivel 22 |
| Nivel 21 |
| Nivel 20 |
| Nivel 19 |
| Nivel 18 |
| Nivel 17 |
| Nivel 16 |
| Nivel 15 |
| Nivel 14 |
| Nivel 13 |
| Nivel 12 |
| Nivel 11 |
| Nivel 10 |
| Nivel 9  |
| Nivel 8  |
| Nivel 7  |
| Nivel 6  |
| Nivel 5  |
| Nivel 4  |
| Nivel 3  |
| Nivel 2  |
| Nivel 1  |
| Nivel B1 |
| Nivel B2 |

ENTREGA FINAL  
APTO PARA CONSTRUCCIÓN

KEY PLAN

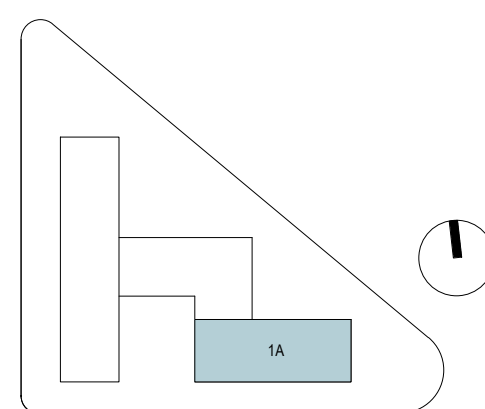

Fecha: 26-07-2024

Escala: 1 : 25

ESPECIFICACIONES GENERALES

CTIB\_CN\_EST\_003\_GEN\_XXX\_01