
1/08/2024 12:17:01 p. m.

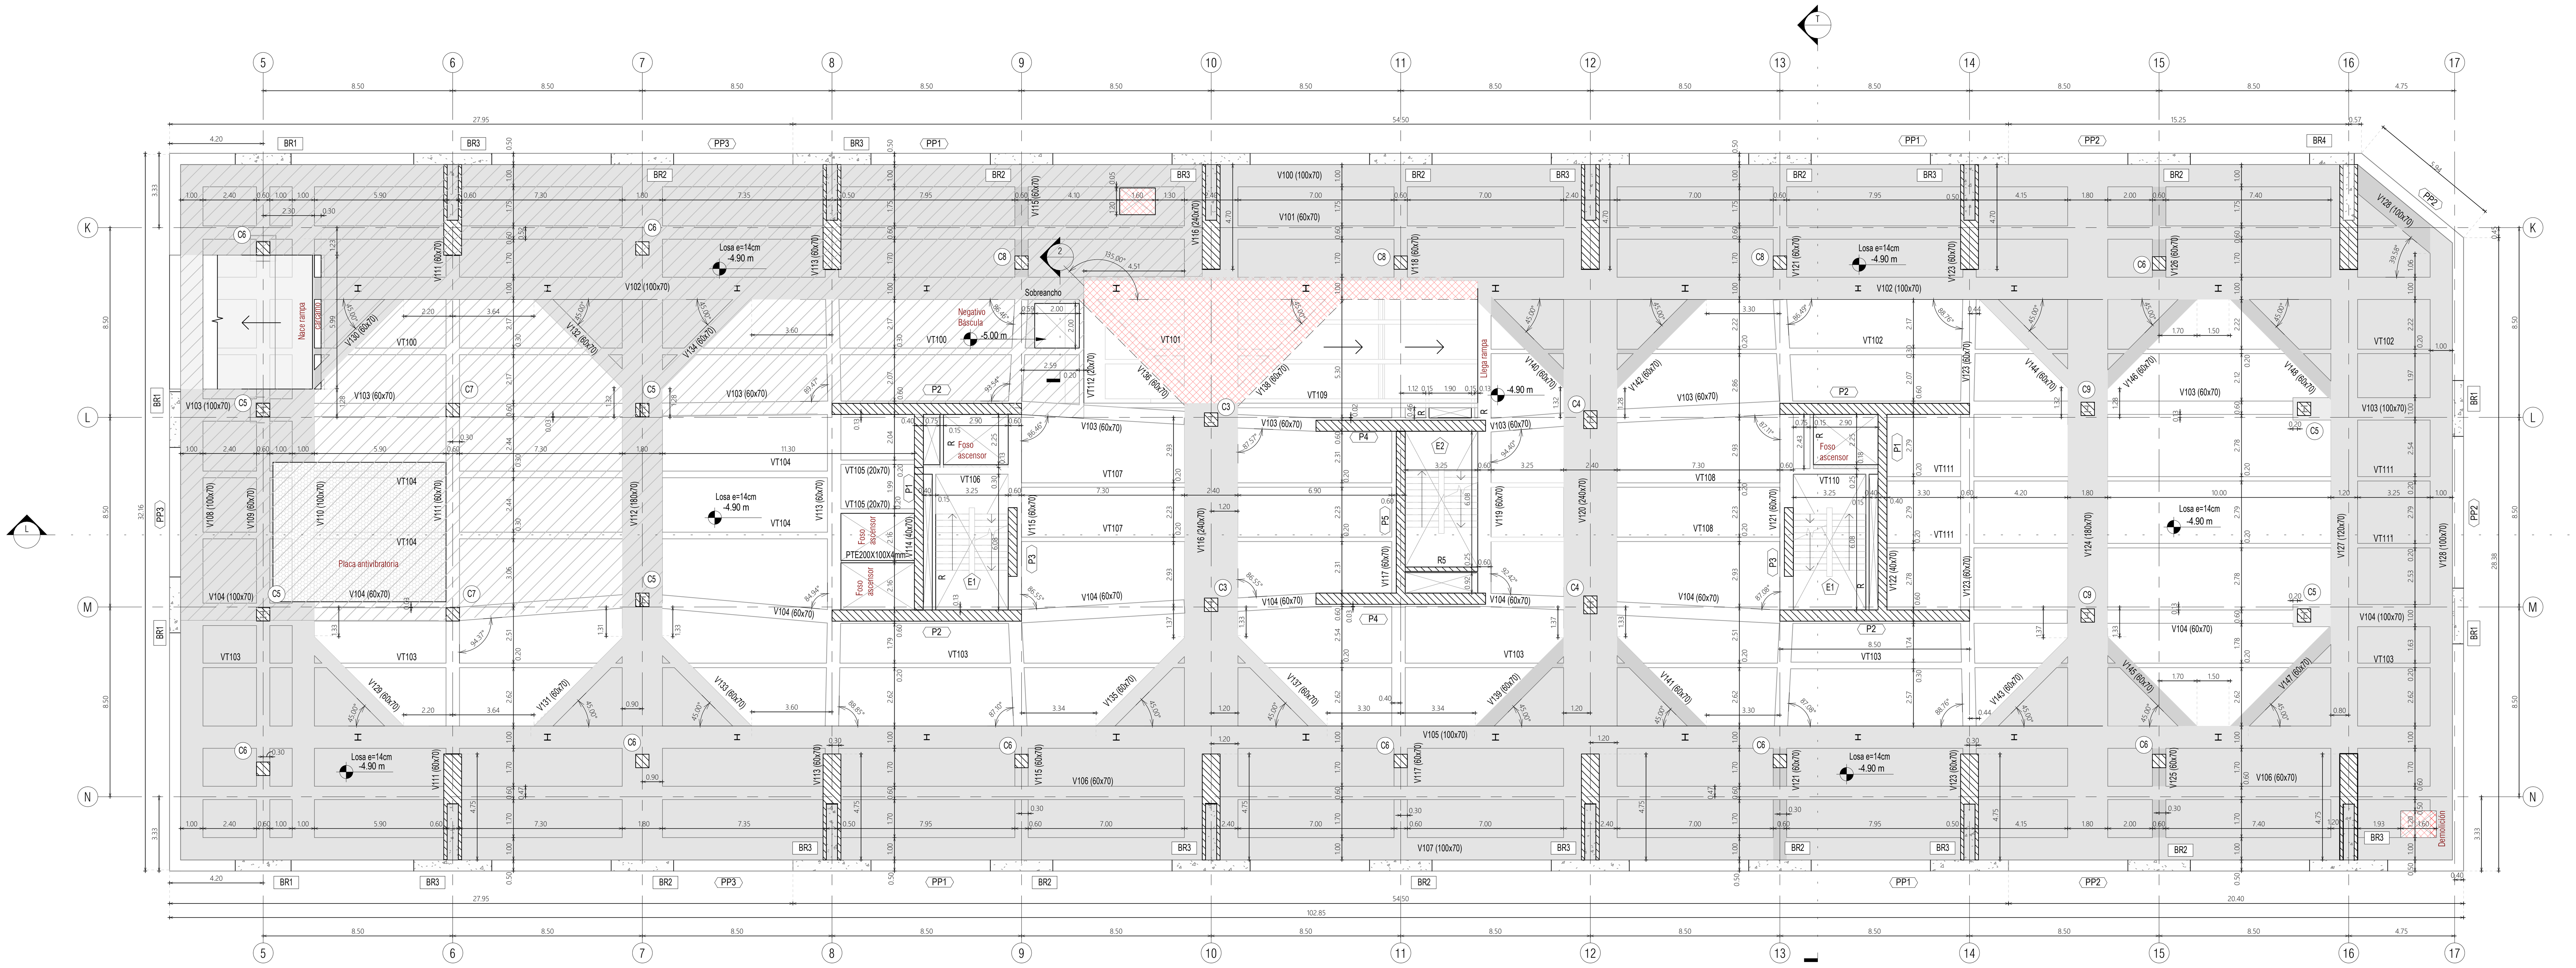

PLANTA DE SÓTANO 1 N.E. -4.90m

escala 1 : 150

***NOTAS IMPORTANTES:**

- Ver especificaciones generales en los planos EST-000 al EST-003.
- Ver alzados en planos EST-200, EST-201, y EST-202.
- Ver cortes en planos EST-300 y EST-301.
- Ver despiece de pantallas en planos EST-400 al EST-404.
- Ver despiece de columnas en planos EST-405 y EST-406.
- Ver despiece de vigas en planos del EST-410 al EST-414.
- Ver despiece de viguetas en planos EST-440 y EST-441.
- Ver detalles de los tanques en planos EST-505 y EST-506.
- Ver detalles de escaleras en planos EST-507 y EST-508.
- Ver detalles rampas vehiculares en plano EST-509.
- Ver detalle de capiteles en plano EST-515.
- Ver proceso constructivo en los planos EST-600 al EST-604.
- Ver detalle de placas antivibratorias en plano EST-701.
- Ver localización y dimensiones de placas antivibratorias en planos hidráulicos, eléctricos, acústicos y de HVAC.


Indica zona de placa andén en planta

Indica zona de demolición

Indica en planta sobreancho


Indica en planta placa antivibratoria

Indica en planta perfiles temporales

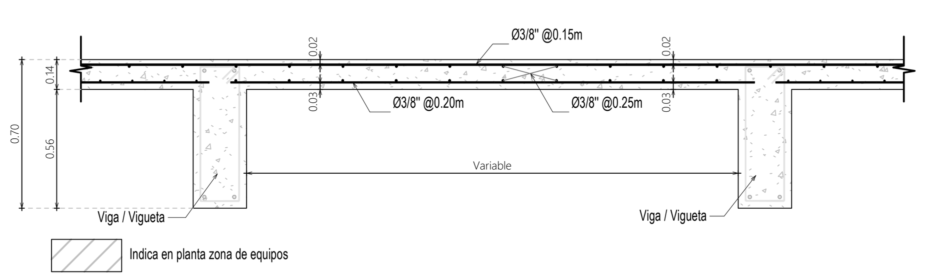


SECCIÓN TÍPICA DE PLACA e=14cm ZONA EQUIPOS

escala 1 : 25

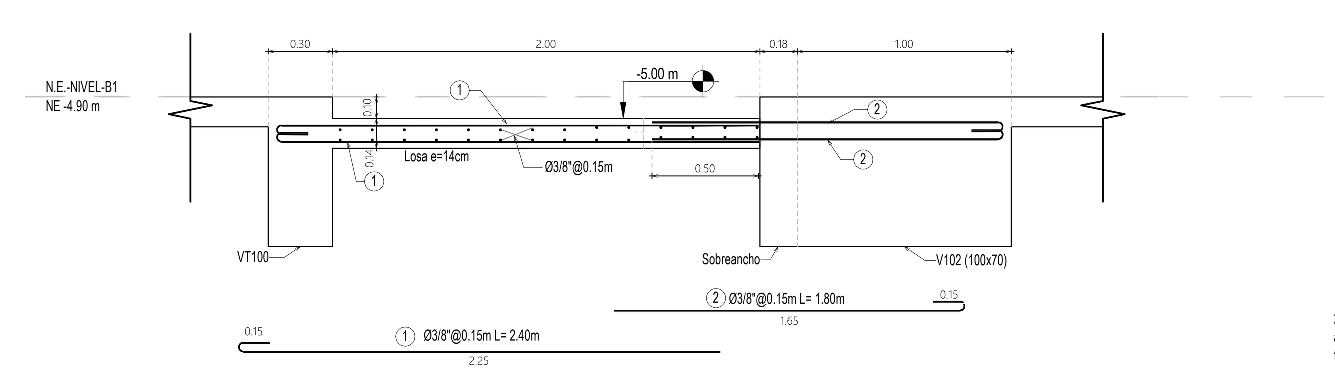


CORTE 2 - SECCIÓN TÍPICA NEGATIVO BÁSCULA

escala 1 : 25

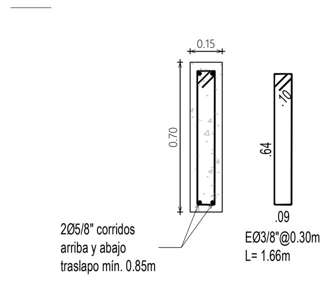


DETALLE RIOSTRA 2 RAMAS

escala 1 : 25

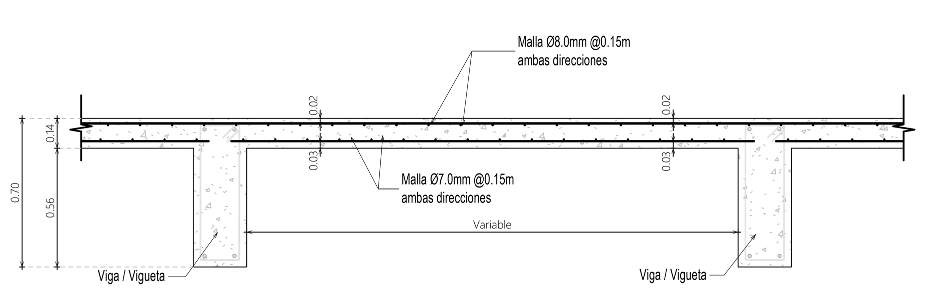


SECCIÓN TÍPICA DE PLACA e=14cm

escala 1 : 25

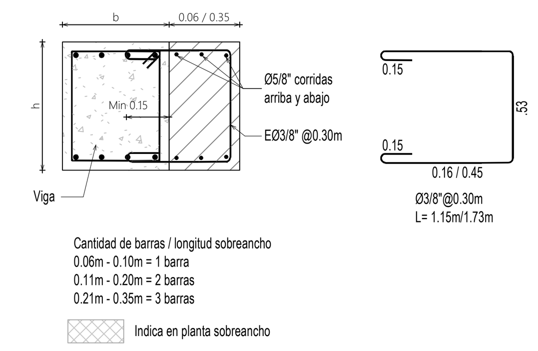

SECCIÓN TÍPICA DE SOBREANCHO

escala 1 : 25

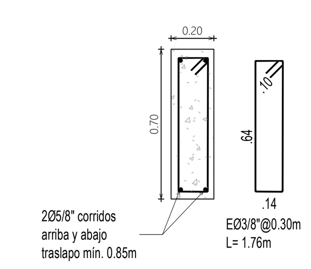

DETALLE RIOSTRA 2 RAMAS R5

escala 1 : 25

CTIB

Campus de Ciencia, Tecnología e Innovación de Bogotá - Región

corferias — Generadores de Oportunidades y Progreso

Cámara de Comercio de Bogotá

BOGOTÁ — Secretaría Distrital de Desarrollo Económico

ARQUITECTO COORDINADOR

EL EQUIPO MAZZANTI + Gensler

DISEÑO ESTRUCTURAL

CNI INGENIEROS

DISEÑADOR: ING. NICOLÁS PARRA GARCÍA
MAT. 25202-62063 CND

INTERVENTORÍA

GUTIÉRREZ DÍAZ S.A.S.
SUPERVISIÓN Y GESTIÓN DE PROYECTOS DE CONSTRUCCIÓN

Director de interventoría : Ing. Jorge Iván García Mancilla
Mat: 632021 148063 QND

Versión	Emisión	Descripción
AA	15-06-2023	Ingeniería básica
AB	04-08-2023	Anteproyecto
AC	01-11-2023	Anteproyecto V2 50%
AD	15-12-2023	Anteproyecto V2 100%
DD	13-03-2024	Curaduria V2
EE	10-05-2024	Proyecto final 100%
EF	31-05-2024	Respuestas Obs. 100%
FF	21-06-2024	Entrega final
01	26-07-2024	ENTREGA FINAL

PROYECTO:

CAMPUS DE CIENCIA, TECNOLOGÍA E INNOVACIÓN DE BOGOTÁ
MAT : No. 50C-00252470

FASE


ENTREGA FINAL

PROPÓSITO DE EMISIÓN


Curaduría	☐	Coordinación	☐
Revisión	☐	Construcción	☒
Entrega Cliente	☒		

ENTREGA FINAL
APTO PARA CONSTRUCCIÓN

ZONIFICACIÓN

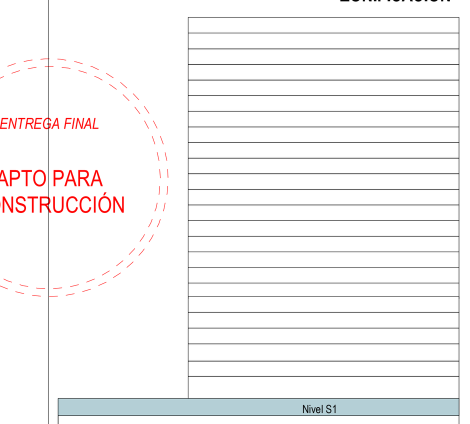

KEY PLAN

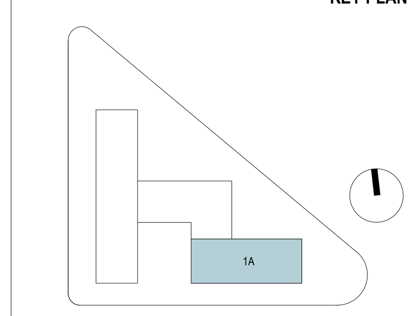

Fecha: 26-07-2024

Escala: As indicated

PLANTA DE SÓTANO 1

CTIB_CNI_EST_103_PLA_S01_01