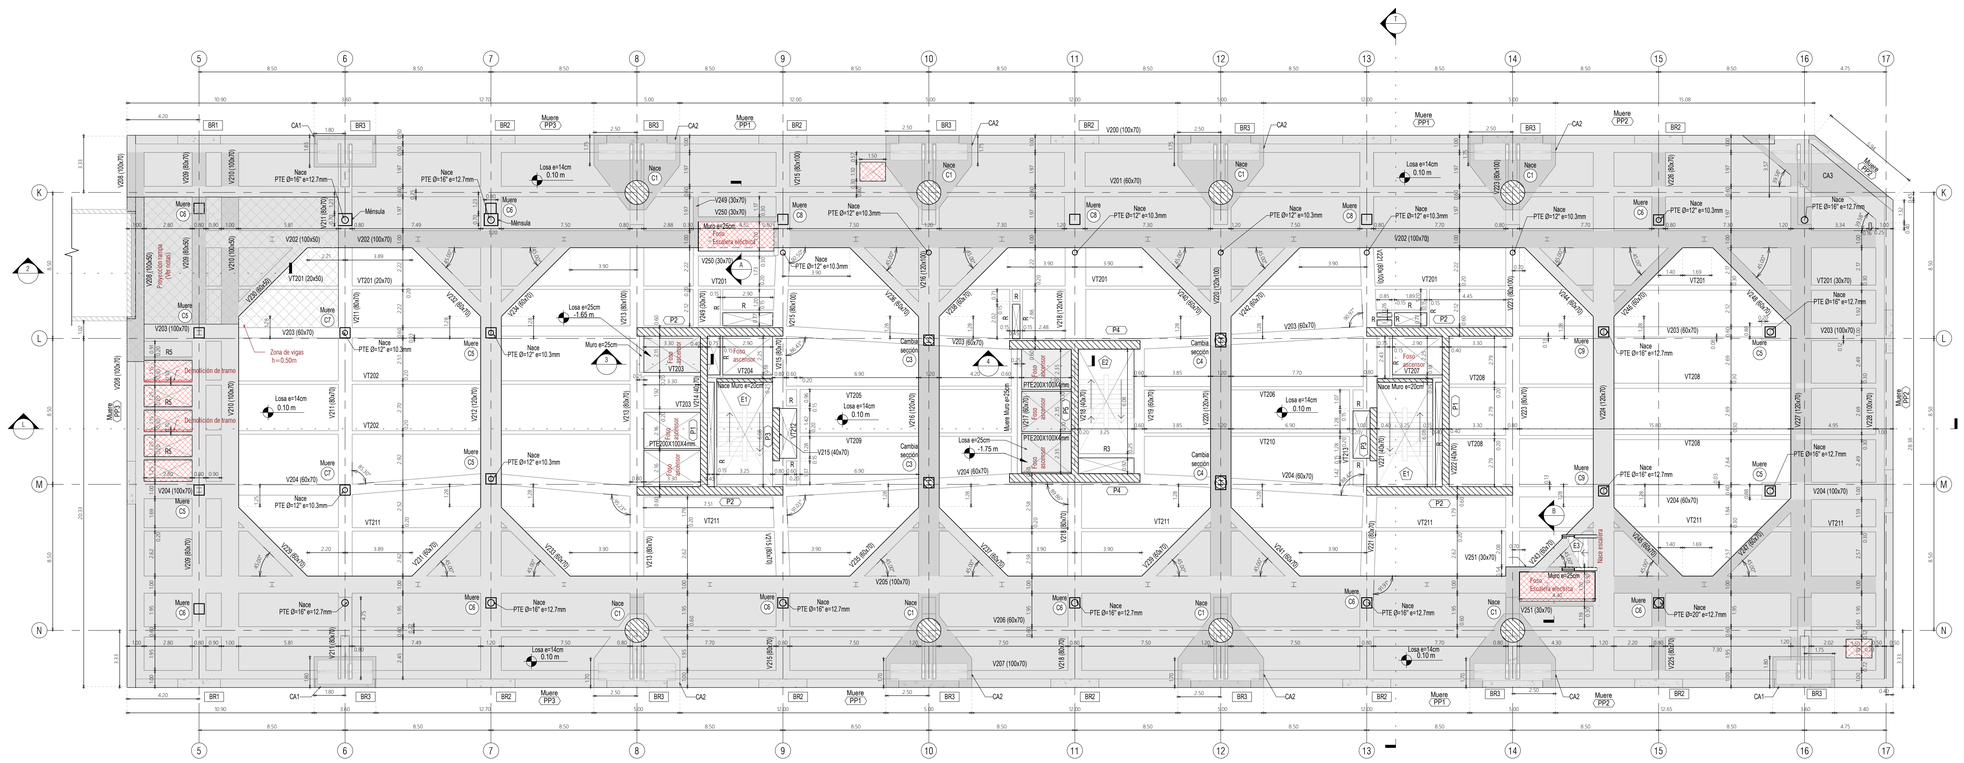

PLANTA DE PISO 1 N.E. +0.10m
escala 1 : 150

***NOTAS IMPORTANTES:**

- Ver especificaciones generales en los planos EST-000 al EST-003.
- Ver alzados en planos EST-200, EST-201, y EST-202.
- Ver cortes en planos EST-300 y EST-301.
- Ver despiece de pantallas en planos EST-400 al EST-404.
- Ver despiece de columnas en planos EST-405 y EST-406.
- Ver despiece de vigas en planos del EST-415 al EST-421.
- Ver despiece de viguetas en planos EST-440 y EST-441.
- Ver detalles de escaleras en planos EST-507 y EST-508.
- Ver detalles rampas vehiculares y fosos de ascensor en plano EST-509.
- Ver detalles de conexiones en planos EST-510 al EST-514.
- Ver detalle de capiteles y ménsulas en plano EST-515.
- Ver proceso constructivo en los planos EST-600 al EST-604.

Indica zona de placa andén en planta

Indica zona de demolición

Indica en planta sobreancho

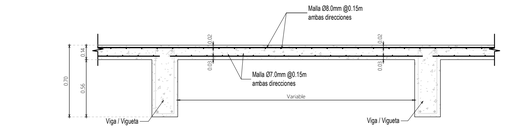

SECCIÓN TÍPICA DE PLACA e=14cm
escala 1 : 25

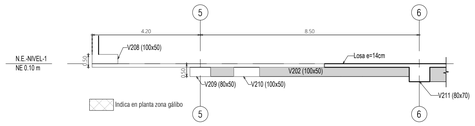

CORTE 2 ZONA ACCESO VEHICULO DE CARGA
escala 1 : 100

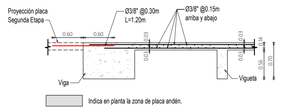

SECCIÓN TÍPICA DE PLACA ANDÉN
escala 1 : 50

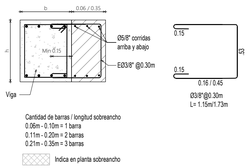

SECCIÓN TÍPICA DE SOBREANCHO
escala 1 : 25

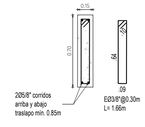

DETALLE RIOSTRA 2 RAMAS
escala 1 : 25

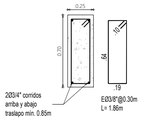

DETALLE RIOSTRA 2 RAMAS R3
escala 1 : 25

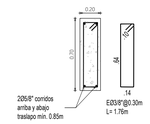

DETALLE RIOSTRA 2 RAMAS R5
escala 1 : 25

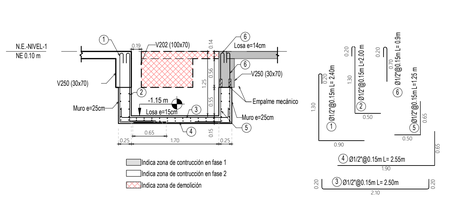

CORTE A DETALLE FOSO DE ESCALERA ELECTRICA
escala 1 : 50

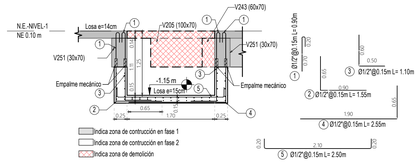

CORTE B DETALLE FOSO DE ESCALERA ELECTRICA
escala 1 : 50

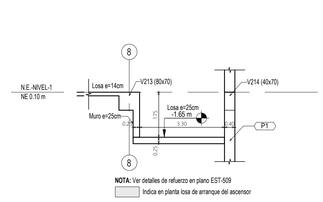

CORTE 3 LOSA DE ARRANQUE DE ASCENSOR
escala 1 : 100

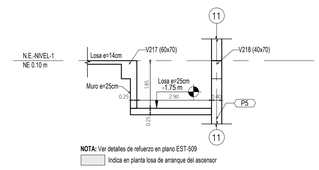

CORTE 4 LOSA DE ARRANQUE DE ASCENSOR
escala 1 : 100

ENTREGA FINAL

APTO PARA CONSTRUCCIÓN

CTIB
Campus de Ciencia, Tecnología e Innovación de Bogotá - Región

corferias
Generadores de Oportunidades y Progreso

Cámara de Comercio de Bogotá
BOGOTÁ Secretaría Distrital de Desarrollo Económico

ARQUITECTO COORDINADOR

EL EQUIPO MAZZANTI + Gensler

DISEÑO ESTRUCTURAL

CNI INGENIEROS

DISEÑADOR: ING. NICOLÁS PARRA GARCÍA
MAT. 25202-62063 CND

INTERVENTORÍA

GUTIÉRREZ DÍAZ S.A.S.
SUPERVISIÓN Y GESTIÓN DE PROYECTOS DE CONSTRUCCIÓN

Director de interventoría : Ing. Jorge Iván García Mancilla
Mat: 632021 148063 QND

Versión	Emisión	Descripción
AA	15-06-2023	Ingeniería básica
AB	04-08-2023	Anteproyecto
AC	01-11-2023	Anteproyecto V2 50%
AD	15-12-2023	Anteproyecto V2 100%
DD	13-03-2024	Curaduría V2
EE	10-05-2024	Proyecto final 100%
EF	31-05-2024	Respuestas Obs. 100%
FF	21-06-2024	Entrega final
01	26-07-2024	ENTREGA FINAL

PROYECTO:
CAMPUS DE CIENCIA, TECNOLOGÍA E INNOVACIÓN DE BOGOTÁ
MAT : No. 50C-00252470

FASE
ENTREGA FINAL

PROPÓSITO DE EMISIÓN

Curaduría	☐	Coordinación	☐
Revisión	☐	Construcción	☒
Entrega Cliente	☒		

ZONIFICACIÓN

Nivel 1

KEY PLAN

1A

Fecha: 26-07-2024

Escala: As indicated

PLANTA DE PISO 1

CTIB_CNI_EST_105_PLA_N01_01

19/06/2024 12:17:49 p. m.