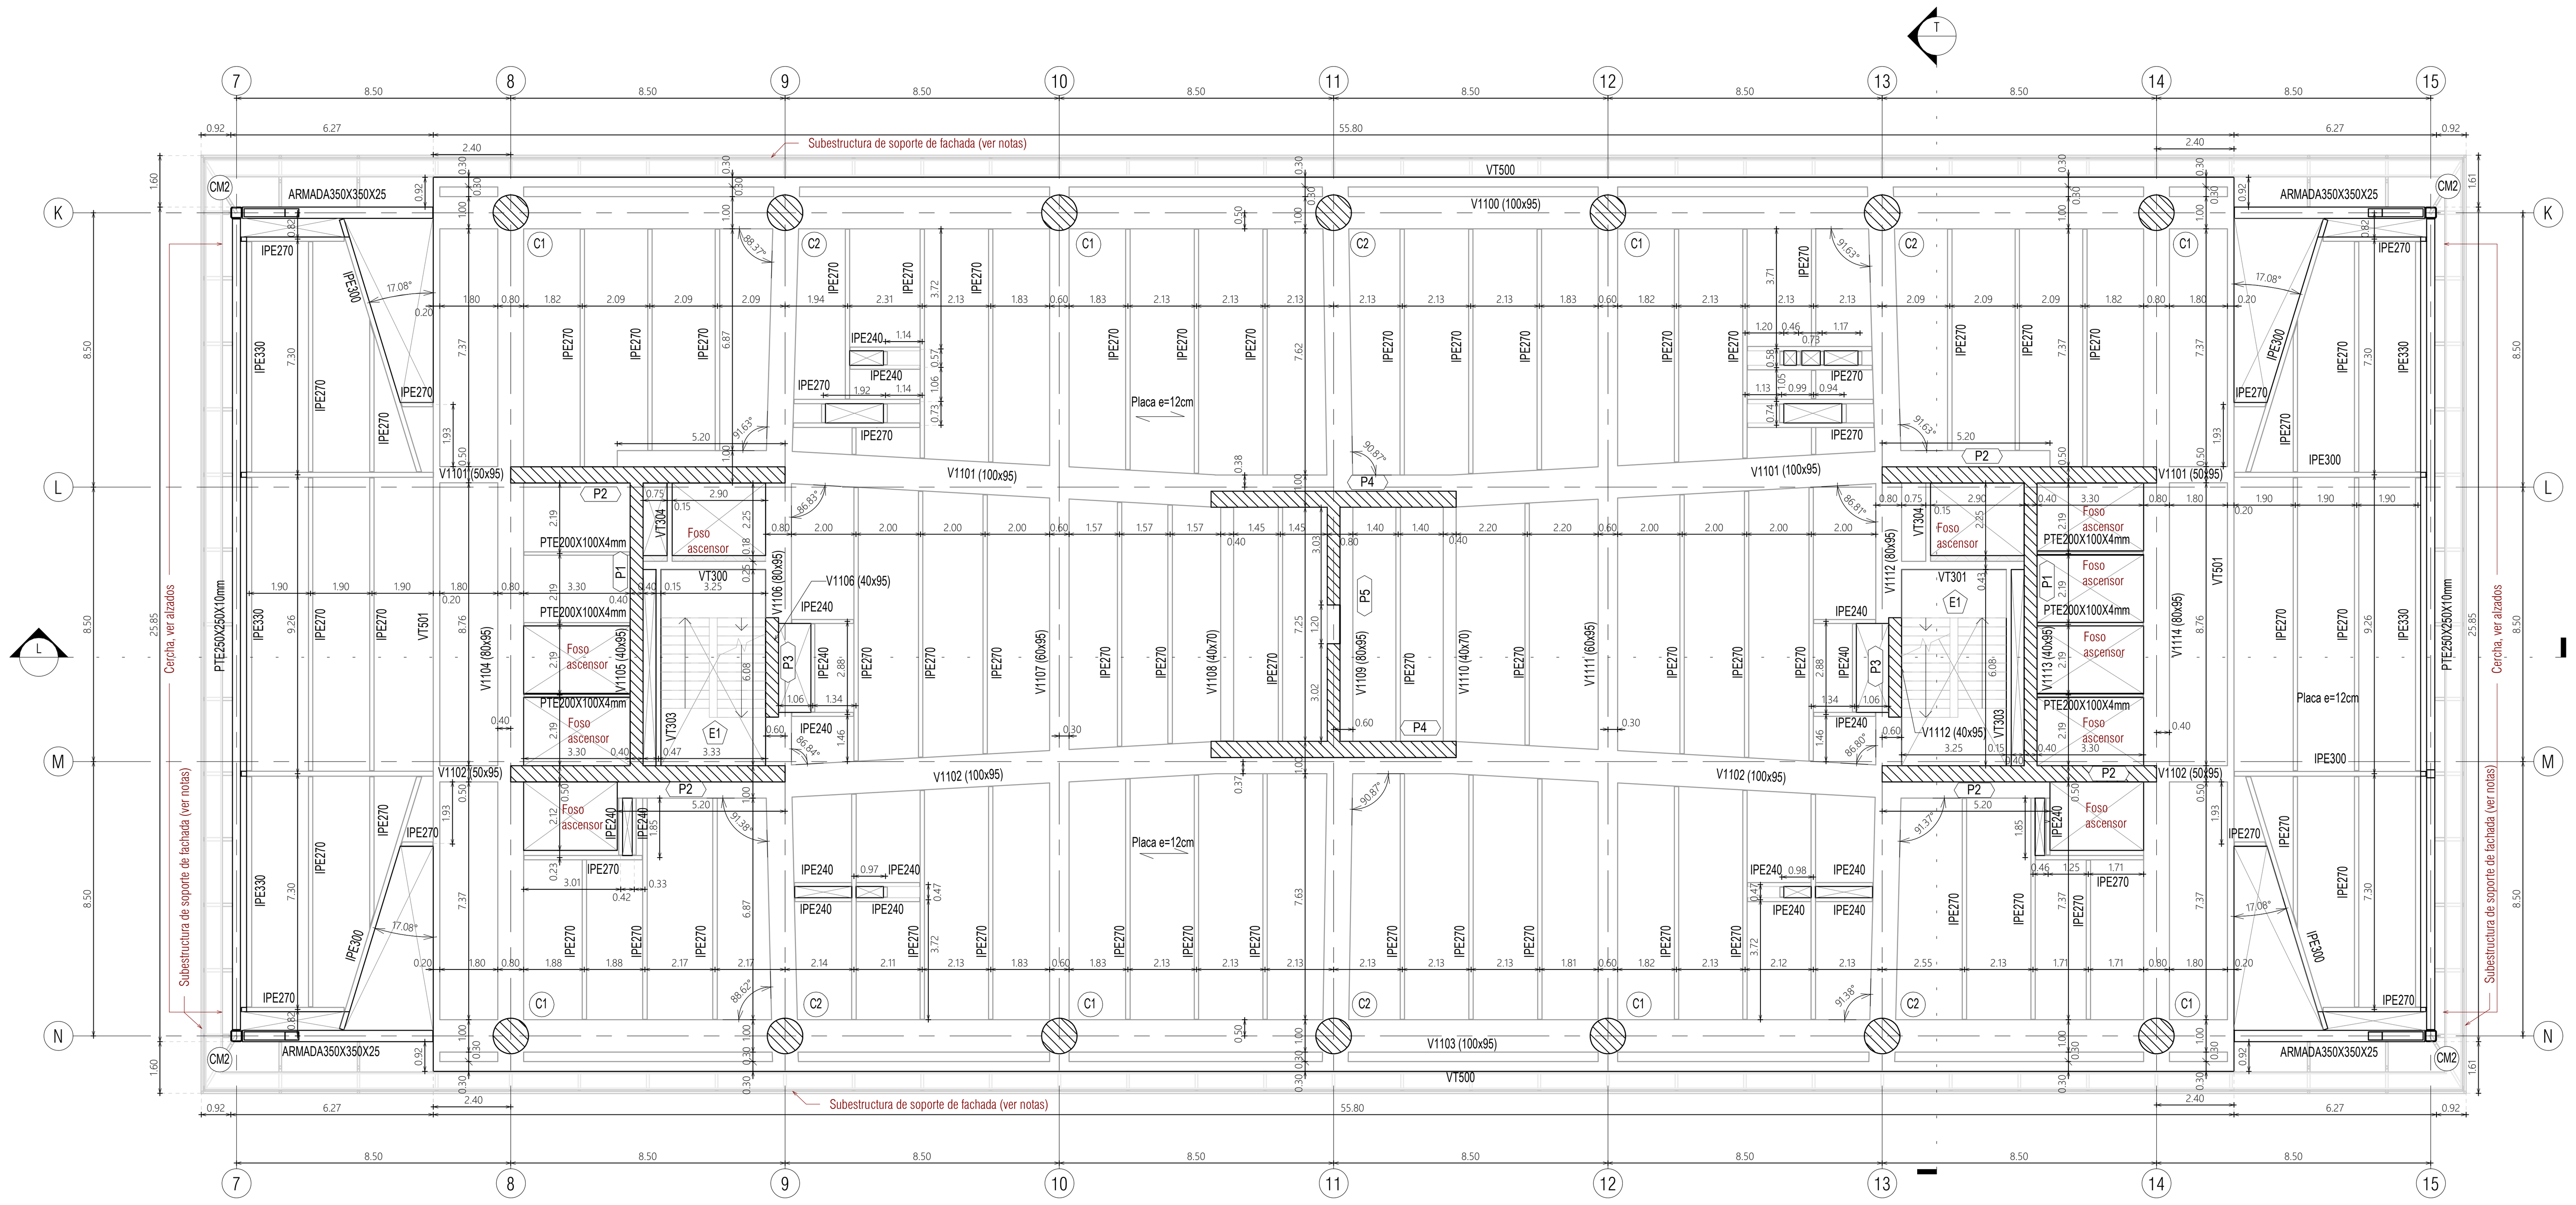

PLANTA TIPO PISO 15 A PISO 17

escala 1 : 150

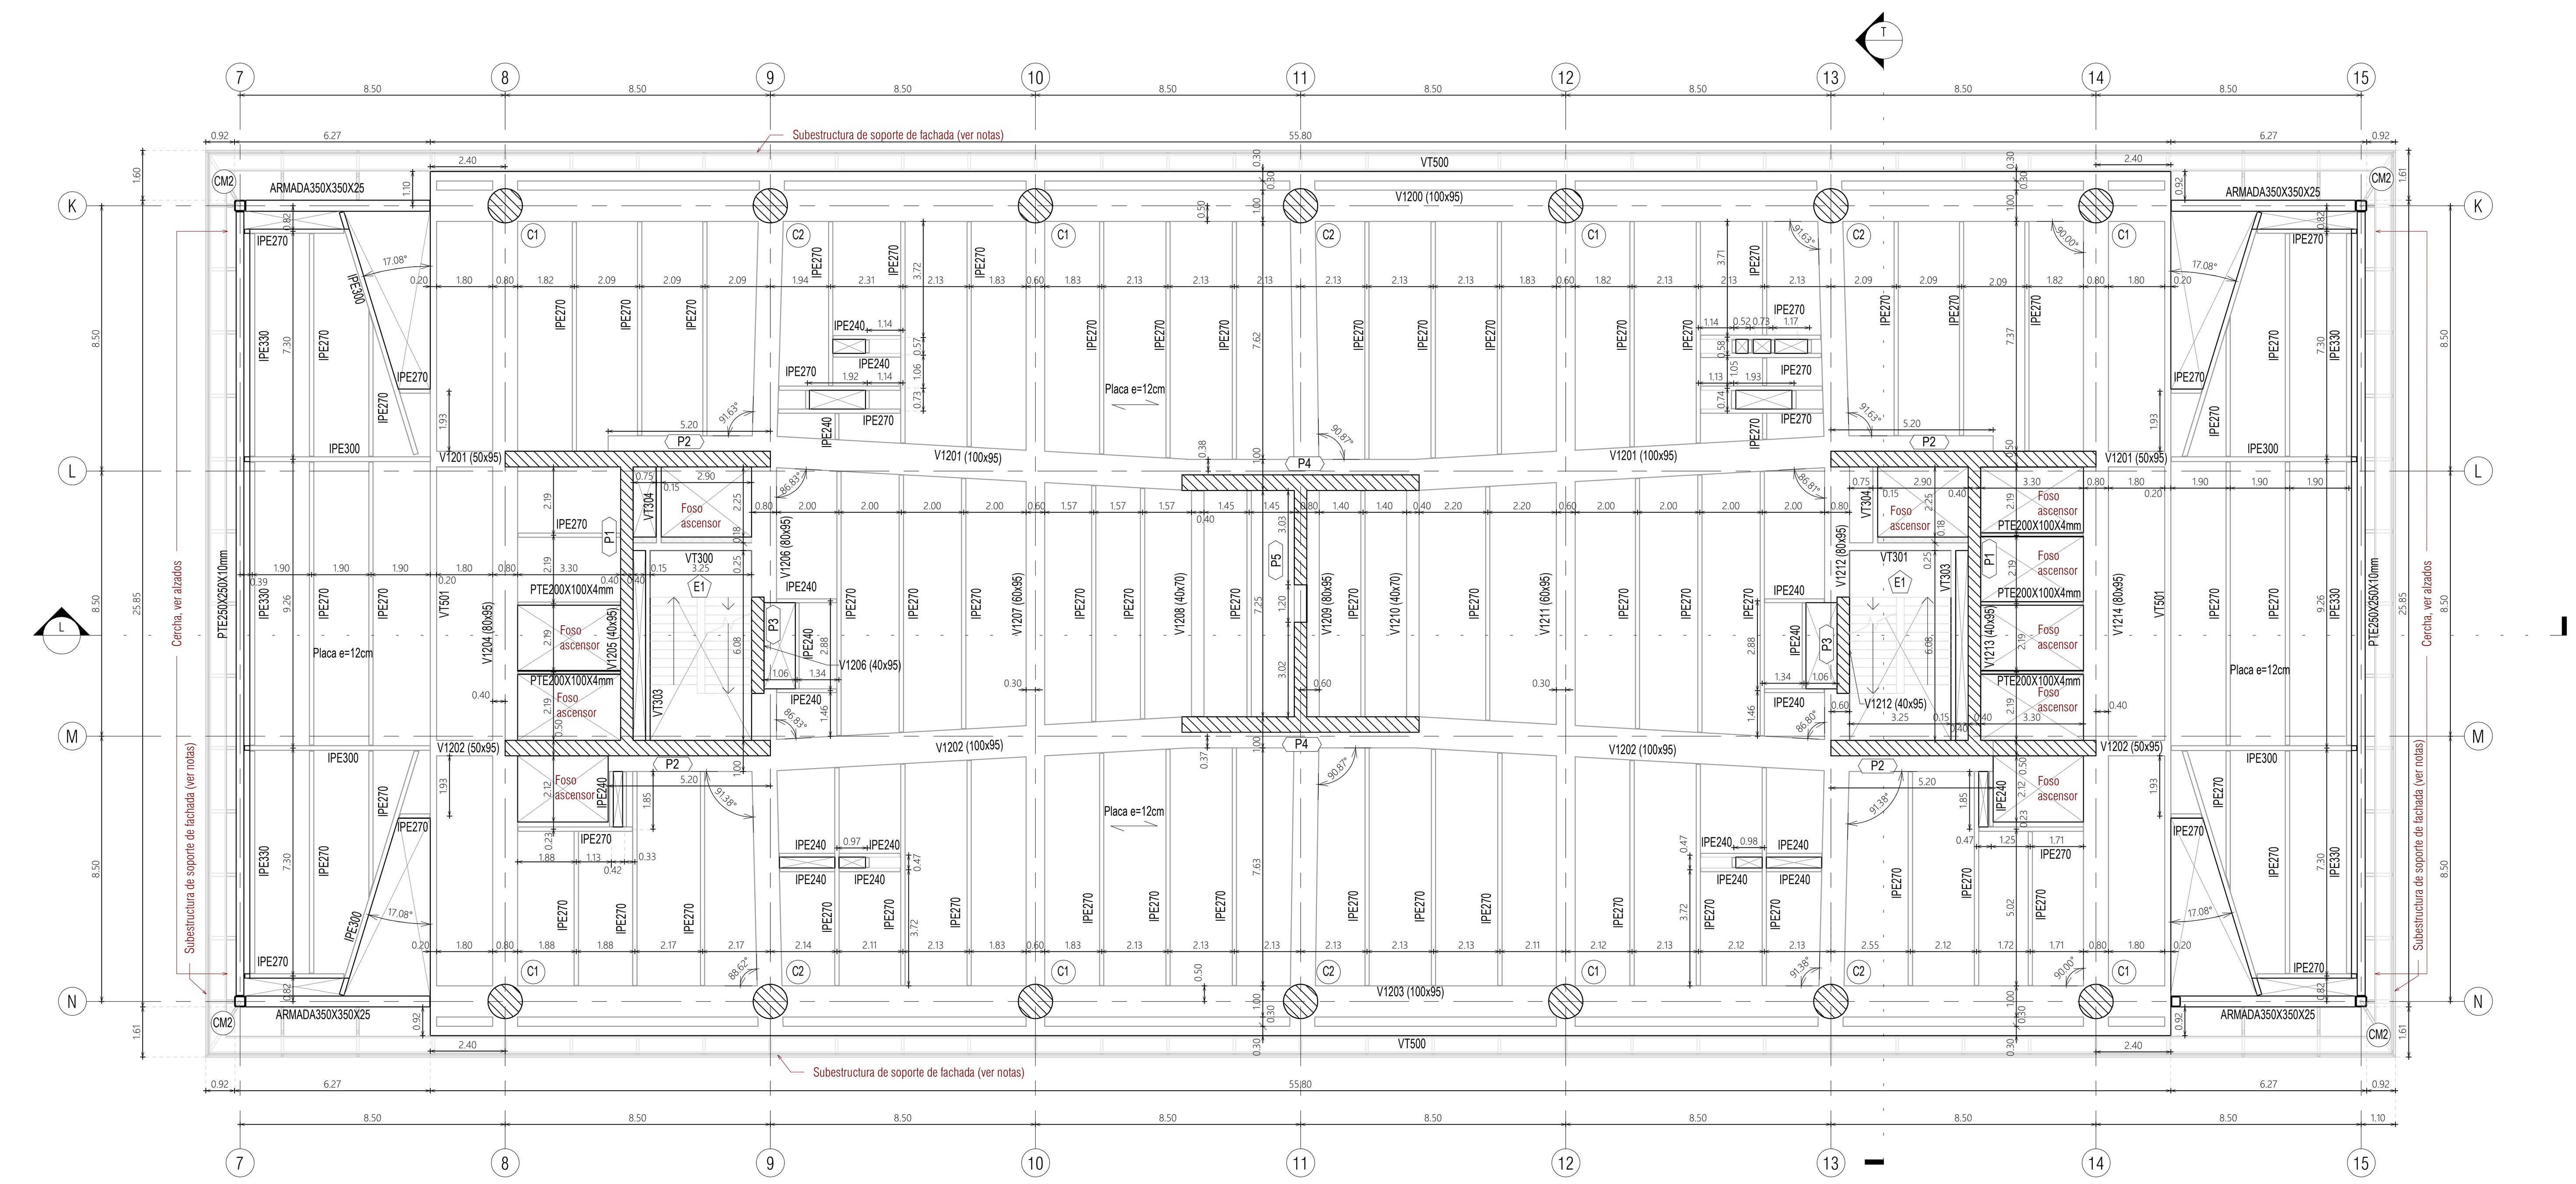

PLANTA TIPO PISO 18 A PISO 23

escala 1 : 150

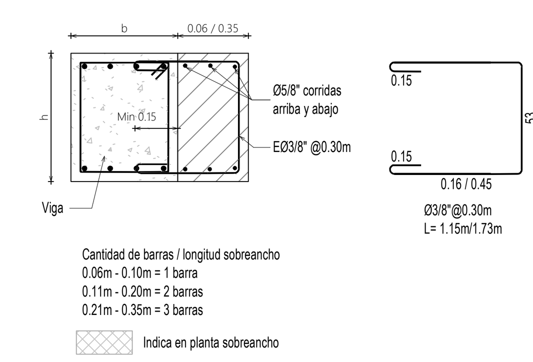

SECCIÓN TÍPICA DE SOBREANCHO

escala 1 : 25

***NOTAS IMPORTANTES:**

- Ver especificaciones generales en los planos EST-000 al EST-003.
- Ver alzados en planos EST-200, EST-201, y EST-202.
- Ver cortes en planos EST-300 y EST-301.
- Ver despiece de columnas en planos EST-405 y EST-406.
- Ver despiece de vigas en planos del EST-422 al EST-439.
- Ver despiece de viguetas en planos EST-440 y EST-441.
- Ver detalles de escaleras en planos EST-507 y EST-508.
- Ver detalles rampas vehiculares y fosos de ascensor en plano EST-509.
- Ver detalles de conexiones en planos EST-510 al EST-514.
- Ver detalle de perfiles metálicos en planos EST-510 al EST-514.
- Ver plantas y de detalles de subestrucura de soporte de fachcada en plano EST-516.
- Las cerchas de fachada ubicada entre los ejes K y N, tienen una contraflecha de 30mm en el centro de su luz.

Sentido del Steel Deck

Indica en planta sobreancho

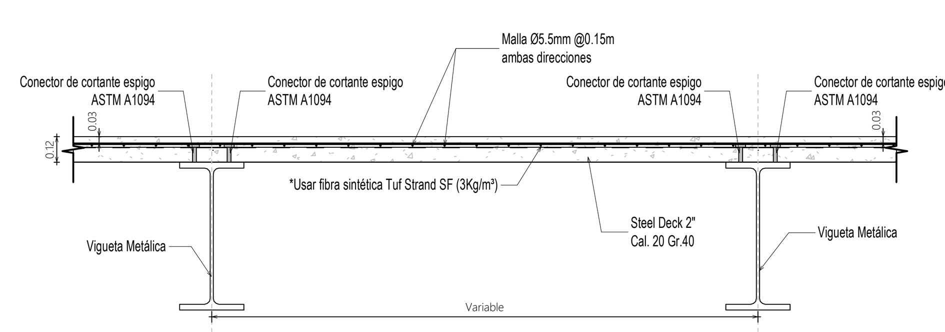

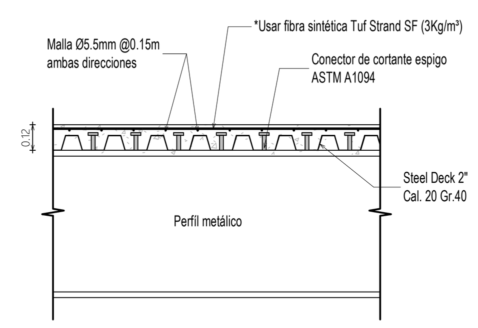

SECCIÓN TÍPICA STEEL DECK

escala 1 : 25

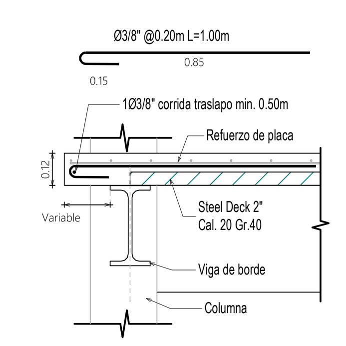

DETALLE TERMINACIÓN BORDES DE PLACA

escala 1 : 20

CTIB
Campus de Ciencia, Tecnología e Innovación de Bogotá - Región

corferias — Generadores de Oportunidades y Progreso

Cámara de Comercio de Bogotá — BOGOTÁ Secretaría Distrital de Desarrollo Económico

ARQUITECTO COORDINADOR

EL EQUIPO MAZZANTI + Gensler

DISEÑO ESTRUCTURAL

CNI INGENIEROS

DISEÑADOR: ING. NICOLÁS PARRA GARCÍA
MAT. 25202-62063 CND

INTERVENTORÍA

GUTIÉRREZ DÍAZ S.A.S.
SUPERVISIÓN Y GESTIÓN DE PROYECTOS DE CONSTRUCCIÓN

Director de interventoría : Ing. Jorge Iván García Mancilla
Mat: 632021 148063 QND

Versión	Emisión	Descripción
AA	15-06-2023	Ingeniería básica
AB	04-08-2023	Anteproyecto
AC	01-11-2023	Anteproyecto V2 50%
AD	15-12-2023	Anteproyecto V2 100%
DD	13-03-2024	Curaduria V2
EE	10-05-2024	Proyecto final 100%
EF	31-05-2024	Respuestas Obs. 100%
FF	21-06-2024	Entrega final
01	26-07-2024	ENTREGA FINAL

PROYECTO:

CAMPUS DE CIENCIA, TECNOLOGÍA E INNOVACIÓN DE BOGOTÁ

MAT : No. 50C-00252470

FASE

ENTREGA FINAL

PROPÓSITO DE EMISIÓN

Curaduría	☐	Coordinación	☐
Revisión	☐	Construcción	■
Entrega Cliente	■		

ZONIFICACIÓN

Nivel 23
Nivel 22
Nivel 21
Nivel 20
Nivel 19
Nivel 18
Nivel 17
Nivel 16
Nivel 15

ENTREGA FINAL — APTO PARA CONSTRUCCIÓN

KEY PLAN

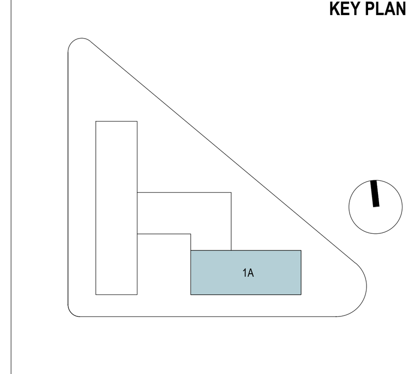

Fecha: 26-07-2024

Escala: As indicated

PLANTA DE PISOS TIPO (15 A 17) Y (18 A 23)

CTIB_CNI_EST_113_PLA_ZZZ_01