



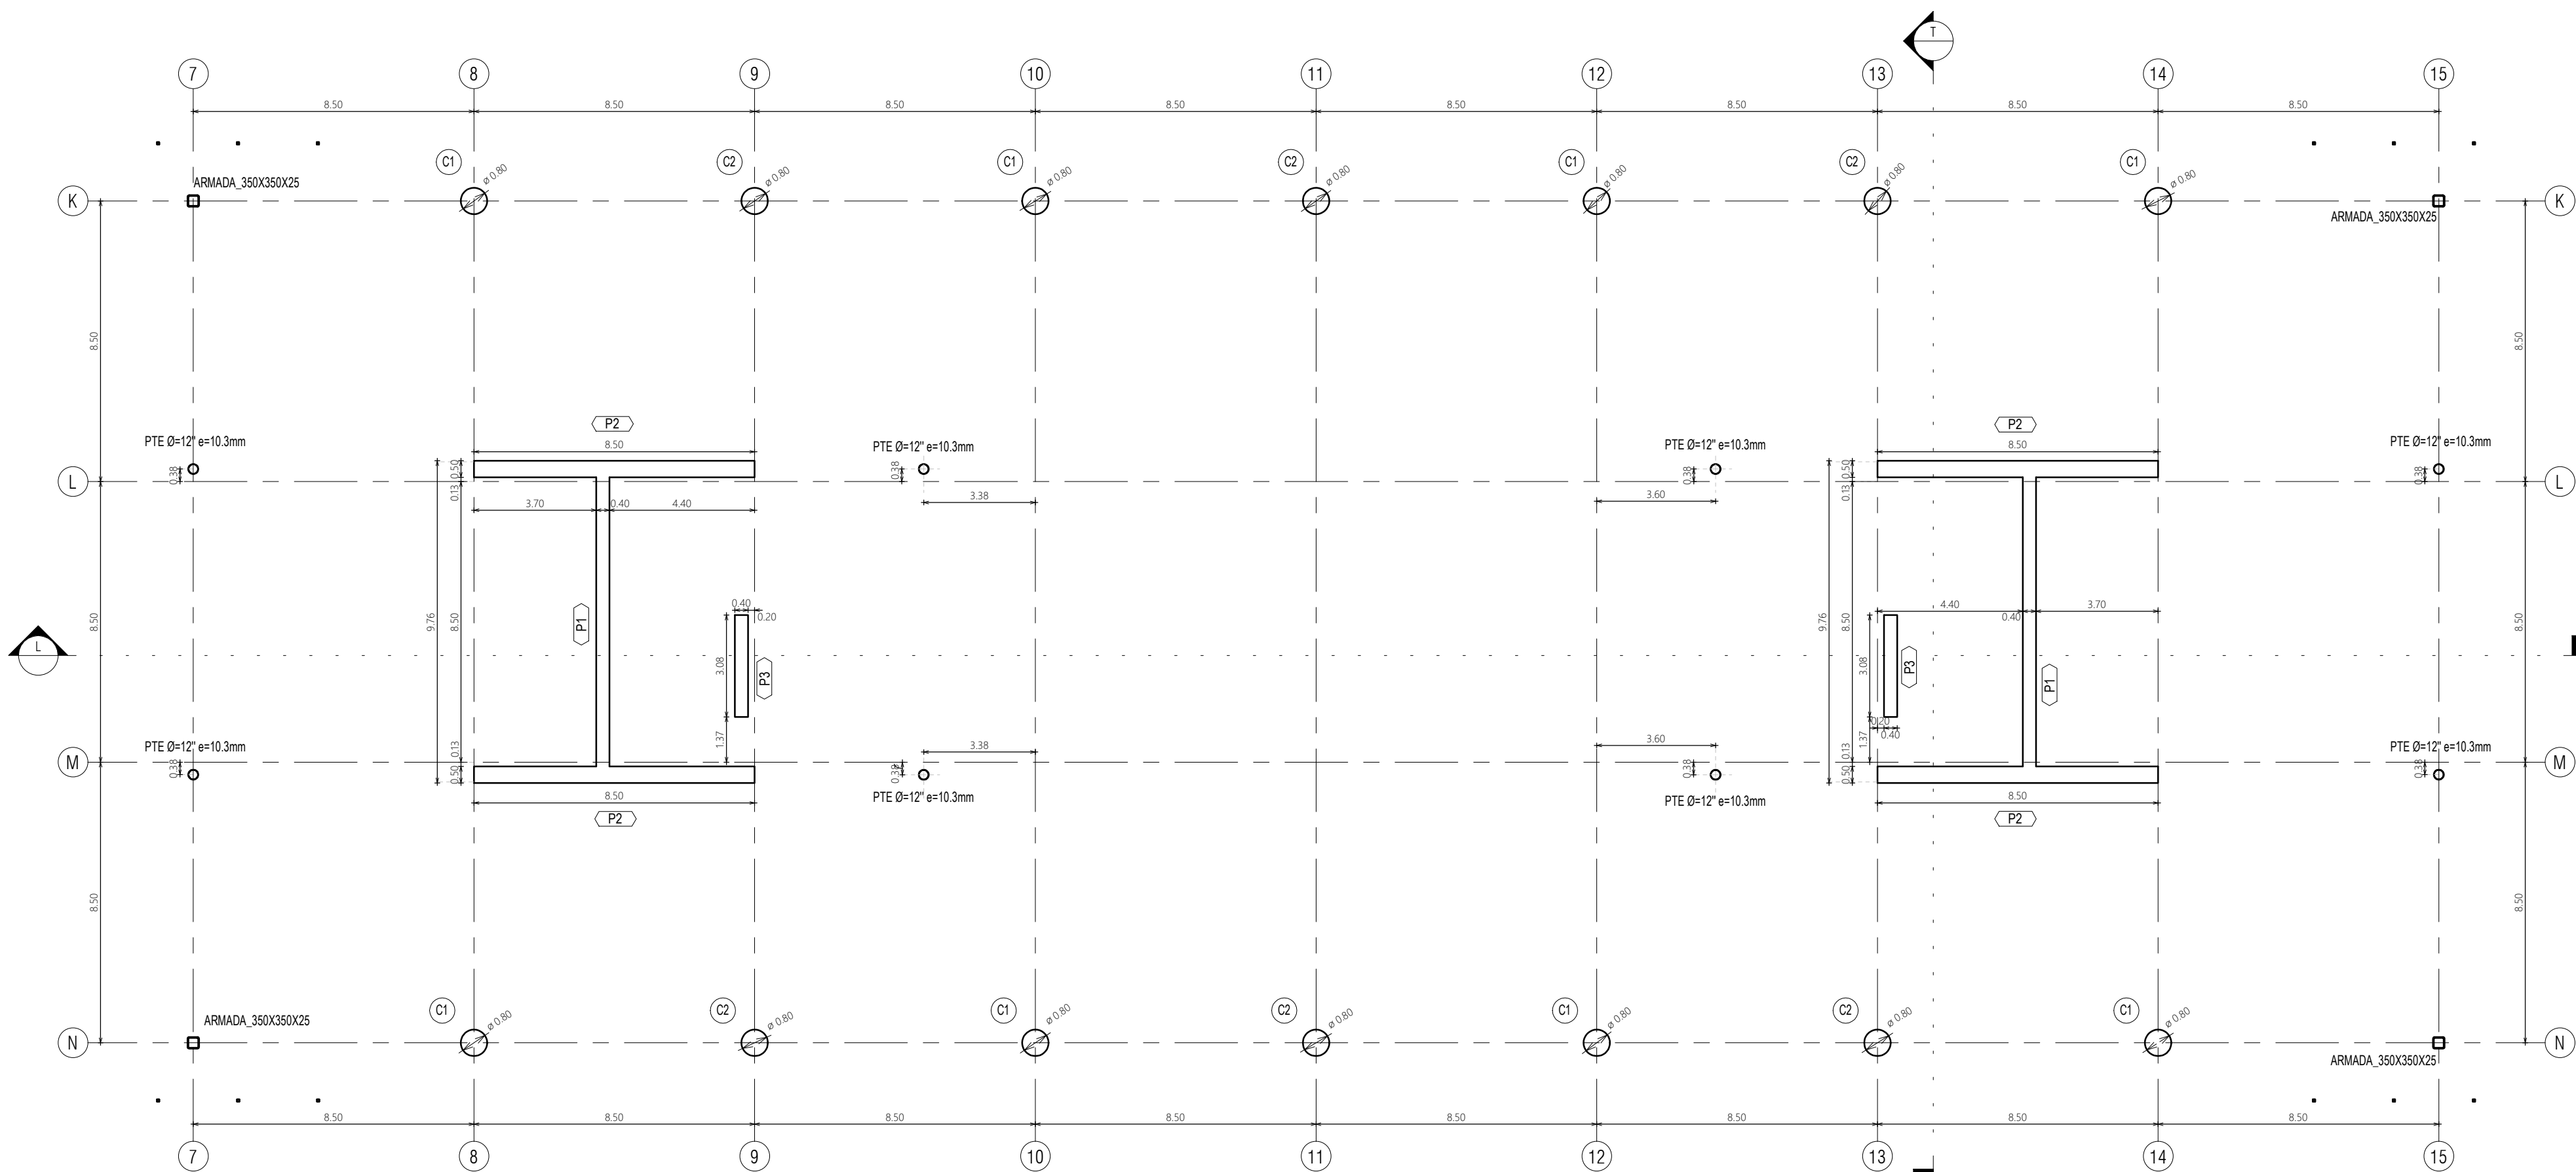

LOCALIZACIÓN DE COLUMNA Y MUROS TERRAZA - CUBIERTA  
escala 1 : 150

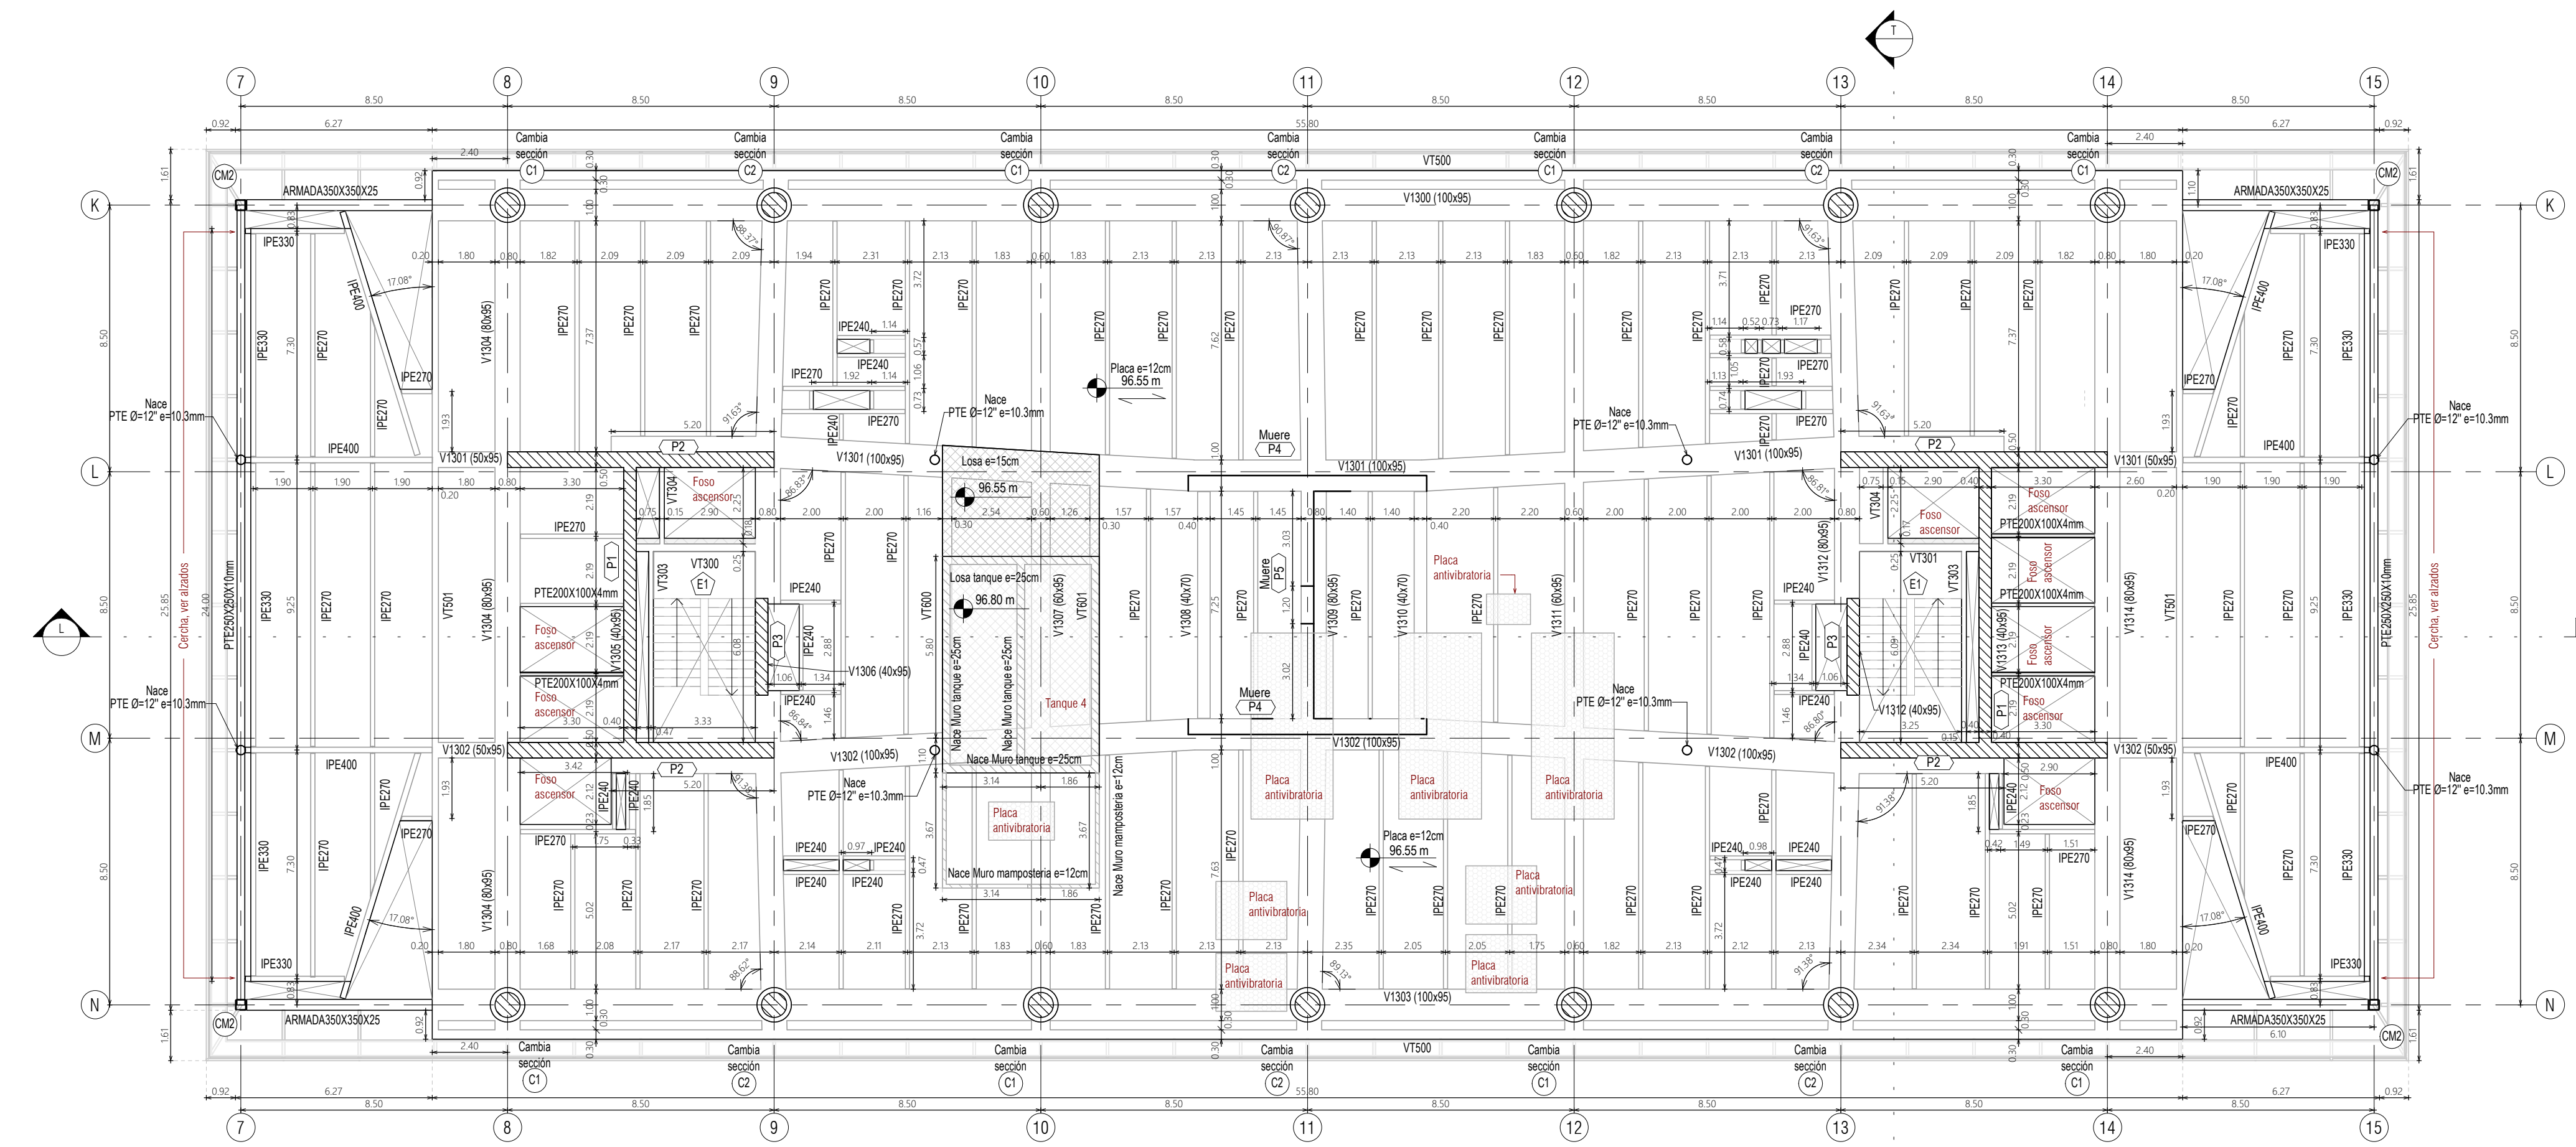

PLANTA DE N.E. TERRAZA N.E. +96.55m  
escala 1 : 150


- \*NOTAS IMPORTANTES:**
- Ver especificaciones generales en los planos EST-000 al EST-003.
  - Ver alzados en planos serie EST-200.
  - Ver cortes en planos serie EST-300.
  - Ver desplaza de columnas en planos EST-405 y EST-406.
  - Ver desplaza de vigas en planos del EST-422 al EST-438.
  - Ver desplaza de viguetas en planos EST-440 y EST-441.
  - Ver detalles de los tanques en planos EST-505 y EST-506.
  - Ver detalles de escaleras en planos EST-507 y EST-508.
  - Ver detalles de rampas vehiculares y fosa de ascensor en plano EST-509.
  - Ver detalles de conexiones en planos EST-510 al EST-514.
  - Ver detalle de perfiles metálicos en planos EST-510 al EST-514.
  - Ver plantas y/o detalles de subestructura de soporte de fachada en plano EST-516.
  - Ver detalle de placas antivibratorias en plano EST-701.
  - Ver localización y dimensiones de placas antivibratorias en planos hidráulicos, eléctricos, acústicos y de HVAC.
1. Sentido del Steel Deck
- Indica en planta sobrecanto
- Indica en planta placa antivibratoria

DETALLE TERMINACIÓN BORDES DE PLACA  
escala 1 : 20


SECCIÓN TÍPICA STEEL DECK  
escala 1 : 25

| CUADRO GENERAL DE COLUMNAS TERRAZA - CUBIERTA |                    |                                             |          |         |          |
|-----------------------------------------------|--------------------|---------------------------------------------|----------|---------|----------|
| TIPO                                          | SECCIÓN            | MATERIAL                                    | CANTIDAD | NACE    | MUERE    |
|                                               | PTE Ø=12" e=10.3mm | Acero A500 Grado C                          | 8        | Terraza | Cubierta |
| C1                                            | Col. Ø80cm         | Concreto (f <sub>c</sub> = 56MPa - 8000psi) | 8        | Terraza | Cubierta |
| C2                                            | Col. Ø80cm         | Concreto (f <sub>c</sub> = 56MPa - 8000psi) | 6        | Terraza | Cubierta |
| CM2                                           | ARMADA_350X350X25  | Acero A500 Grado C                          | 4        | Piso 7  | Cubierta |


| CUADRO GENERAL DE MUROS |             |                                             |          |          |          |
|-------------------------|-------------|---------------------------------------------|----------|----------|----------|
| TIPO                    | ESPESOR     | MATERIAL                                    | CANTIDAD | NACE     | MUERE    |
| P1                      | Muro e=40cm | Concreto (f <sub>c</sub> = 56MPa - 8000psi) | 2        | Sótano 2 | Cubierta |
| P2                      | Muro e=50cm | Concreto (f <sub>c</sub> = 56MPa - 8000psi) | 4        | Sótano 2 | Cubierta |
| P3                      | Muro e=40cm | Concreto (f <sub>c</sub> = 56MPa - 8000psi) | 2        | Sótano 2 | Cubierta |
| P4                      | Muro e=50cm | Concreto (f <sub>c</sub> = 56MPa - 8000psi) | 2        | Sótano 2 | Terraza  |
| P5                      | Muro e=40cm | Concreto (f <sub>c</sub> = 56MPa - 8000psi) | 1        | Sótano 2 | Terraza  |

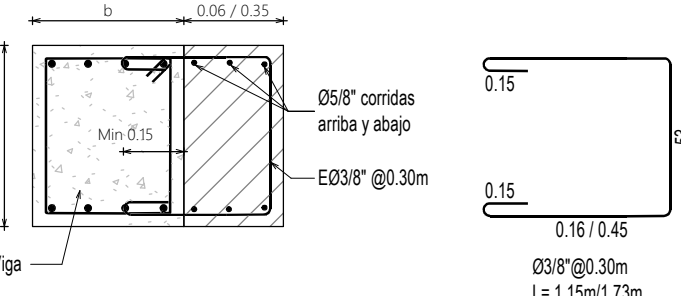

SECCIÓN TÍPICA DE SOBRECANTO  
escala 1 : 25

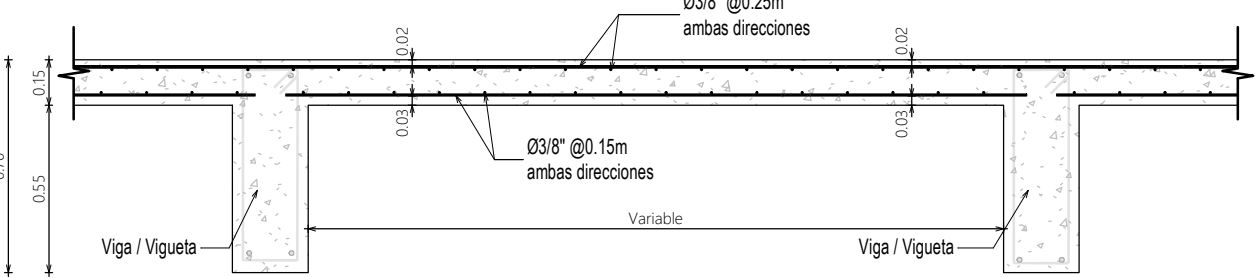

SECCIÓN TÍPICA DE PLACA e=15cm  
escala 1 : 25

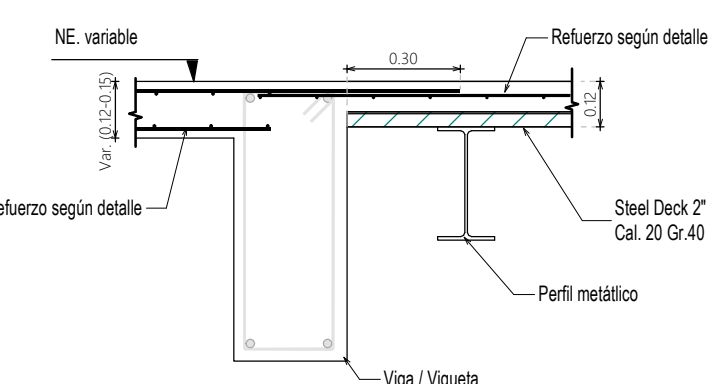

DETALLE TRANSICIÓN PLACA-STEELDECK  
escala 1 : 20

**CTIB**  
Campus de Ciencia, Tecnología e  
Innovación de Bogotá - Región

Generadores de  
Oportunidades y Progreso

Cámara  
de Comercio  
de Bogotá

BOGOTÁ  
Secretaría Distrital de  
Desarrollo Económico

ARQUITECTO COORDINADOR

**ELEQUIPO MAZZANTI + Gensler**

DISEÑO ESTRUCTURAL

DISEÑADOR: ING. NICOLÁS PARRA GARCÍA  
MAT. 23202-62063 QND

INTERVENTORÍA

GUTIÉRREZ DÍAZ S.A.S.  
SUPERVISIÓN Y GESTIÓN DE PROYECTOS DE CONSTRUCCIÓN

Director de intervención : Ing. Jorge Iván García Mancilla  
Mat. 632021 148063 QND

| Versión | Emisión    | Descripción          |
|---------|------------|----------------------|
| AA      | 15-06-2023 | Ingeniería básica    |
| AB      | 04-08-2023 | Anteproyecto         |
| AC      | 01-11-2023 | Anteproyecto V2 50%  |
| AD      | 15-12-2023 | Anteproyecto V2 100% |
| DD      | 13-03-2024 | Curaduría V2         |
| EE      | 10-05-2024 | Proyecto final 100%  |
| EF      | 31-05-2024 | Respuestas Obs. 100% |
| FF      | 21-06-2024 | Entrega final        |
| 01      | 26-07-2024 | ENTREGA FINAL        |

PROYECTO:  
CAMPUS DE CIENCIA, TECNOLOGÍA E  
INNOVACIÓN DE BOGOTÁ  
MAT. No. 500-0025470

FASE  
ENTREGA FINAL

PROPOSITO DE EMISIÓN

☒ Curaduría

☐ Revisión

☐ Entrega Cliente

☐ Coordinación

☐ Construcción

☐

ZONIFICACIÓN

ENTREGA FINAL

APTO PARA CONSTRUCCIÓN

1A

KEY PLAN

1A

Fecha: 26-07-2024

Escala: As indicated

PLANTA DE LOCALIZACIÓN DE COLUMNAS  
TERRAZA-CUBIERTA Y PLANTA N.E. TERRAZA

CTIB\_CNI\_EST\_114\_PLA\_ZZZ\_01