


15000x12 1800 x 1 m

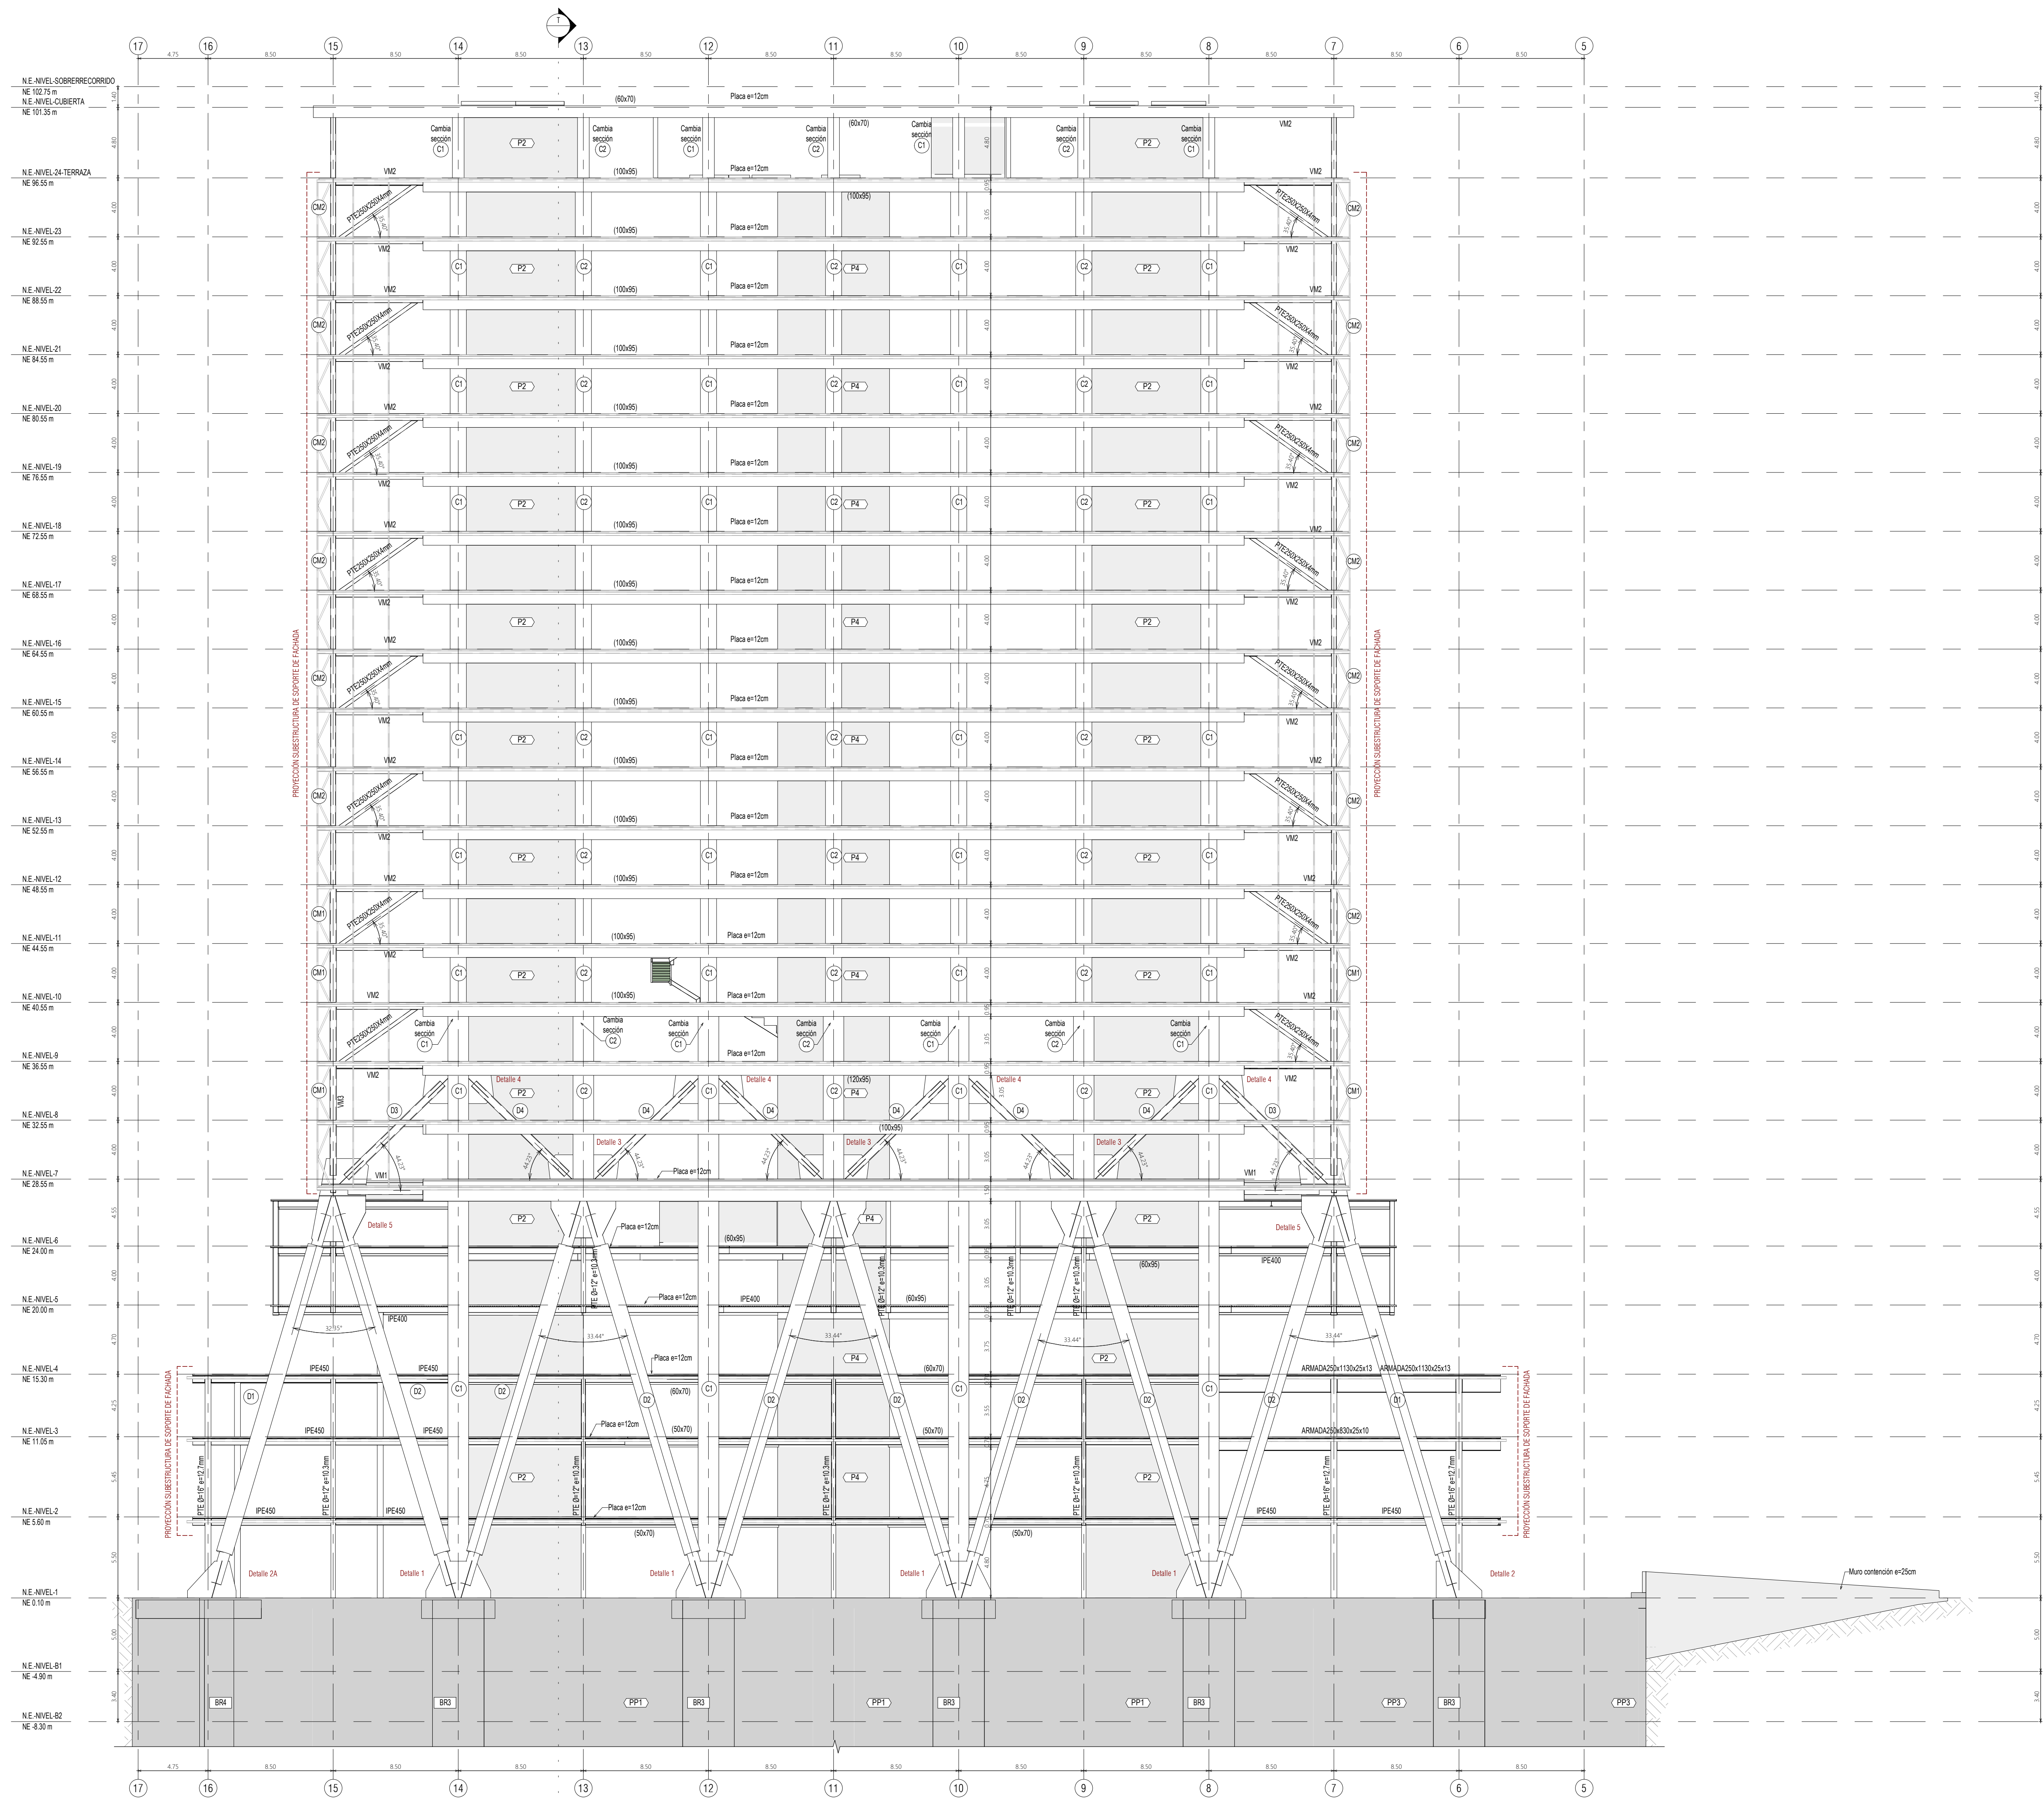

ALZADO NORTE
escala 1 : 200

Versión	Emisión	Descripción
AA	15-06-2023	Ingeniería básica
AB	04-08-2023	Anteproyecto
AC	01-11-2023	Anteproyecto V2 50%
AD	15-12-2023	Anteproyecto V2 100%
DD	13-03-2024	Curaduría V2
EE	10-05-2024	Proyecto final 100%
EF	31-05-2024	Respuestas Obs. 100%
FF	21-06-2024	Entrega final
01	26-07-2024	ENTREGA FINAL

PROYECTO:
CAMPUS DE CIENCIA, TECNOLOGÍA E
INNOVACIÓN DE BOGOTÁ
MAT. No. 500-0025470

FASE
ENTREGA FINAL

PROPÓSITO DE EMISIÓN


Curaduría	☐	Coordinación	☐
Revisión	☐	Construcción	☐
Entrega Cliente	☐		

ZONIFICACIÓN

Nivel 24	
Nivel 23	
Nivel 22	
Nivel 21	
Nivel 20	
Nivel 19	
Nivel 18	
Nivel 17	
Nivel 16	
Nivel 15	
Nivel 14	
Nivel 13	
Nivel 12	
Nivel 11	
Nivel 10	
Nivel 9	
Nivel 8	
Nivel 7	
Nivel 6	
Nivel 5	
Nivel 4	
Nivel 3	
Nivel 2	
Nivel 1	
Nivel 0	

ENTREGA FINAL
APTO PARA
CONSTRUCCIÓN

KEY PLAN

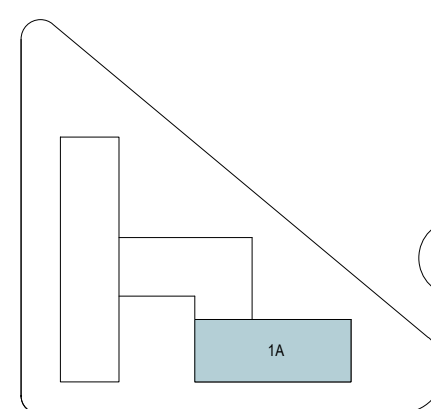

Fecha: 26-07-2024

Escala: 1 : 200

FACHADA NORTE

CTIB_CNI_EST_200_ELE_XXX_01