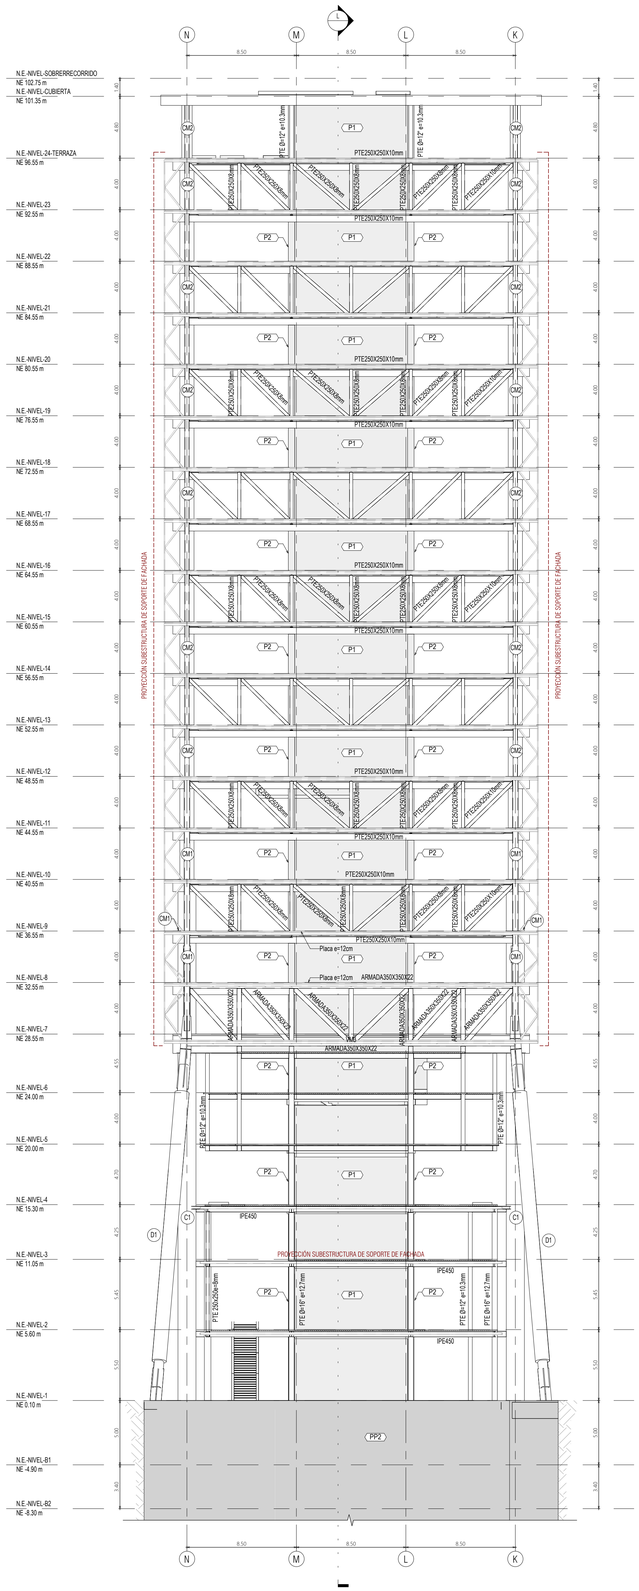

ALZADO ORIENTE
escala 1 : 200

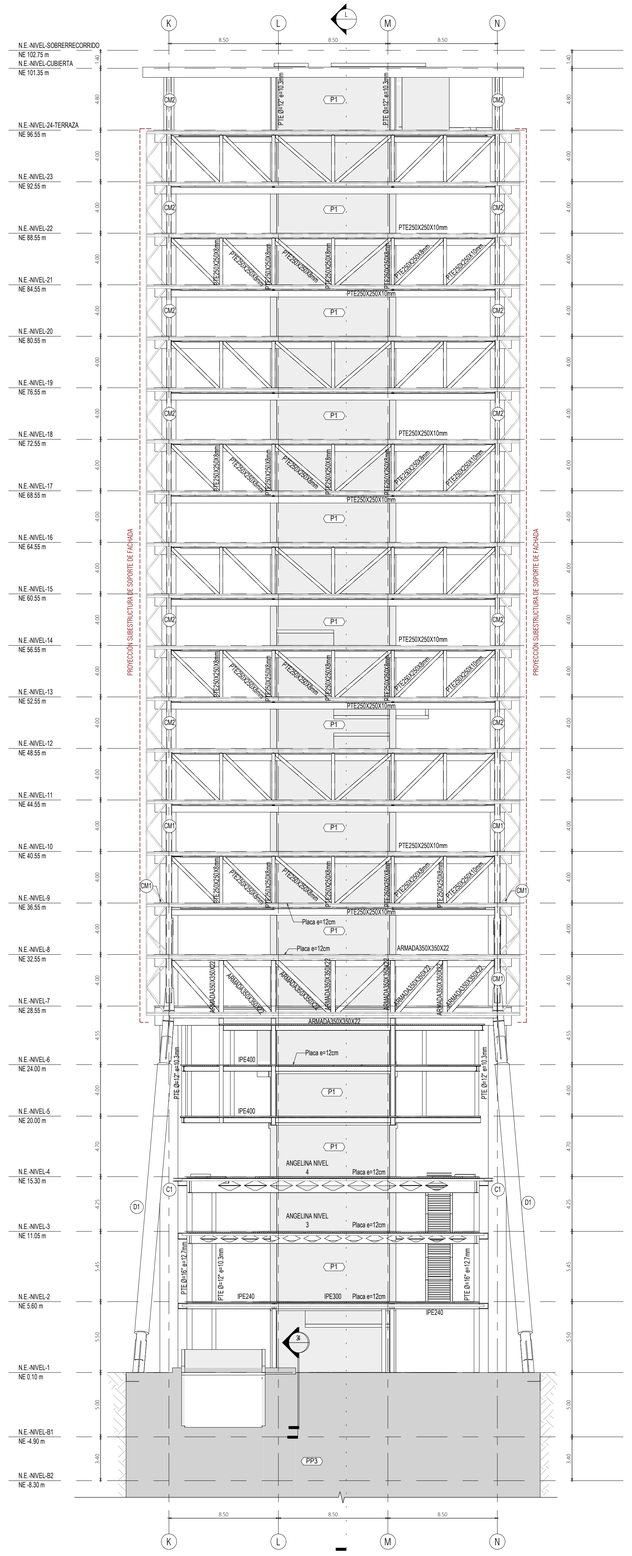

ALZADO OCCIDENTE
escala 1 : 200

CTIB
Campus de Ciencia, Tecnología e Innovación de Bogotá - Región

corferias
Generadores de Oportunidades y Progreso

Cámara de Comercio de Bogotá
BOGOTÁ Secretaría Distrital de Desarrollo Económico

ARQUITECTO COORDINADOR

EL EQUIPO MAZZANTI + Gensler

DISEÑO ESTRUCTURAL

CNI INGENIEROS

DISEÑADOR: ING. NICOLÁS PARRA GARCÍA
MAT. 25202-62063 CND

INTERVENTORÍA

GUTIÉRREZ DÍAZ S.A.S.
SUPERVISIÓN Y GESTIÓN DE PROYECTOS DE CONSTRUCCIÓN

Director de interventoría : Ing. Jorge Iván García Mancilla
Mat: 632021 148063 QND

Versión	Emisión	Descripción
AA	15-06-2023	Ingeniería básica
AB	04-08-2023	Anteproyecto
AC	01-11-2023	Anteproyecto V2 50%
AD	15-12-2023	Anteproyecto V2 100%
DD	13-03-2024	Curaduría V2
EE	10-05-2024	Proyecto final 100%
EF	31-05-2024	Respuestas Obs. 100%
FF	21-06-2024	Entrega final
01	26-07-2024	ENTREGA FINAL

PROYECTO:
CAMPUS DE CIENCIA, TECNOLOGÍA E INNOVACIÓN DE BOGOTÁ
MAT : No. SOC-20252470

FASE
ENTREGA FINAL

PROPÓSITO DE EMISIÓN

Curaduría	☐	Coordinación	☐
Revisión	☐	Construcción	☒
Entrega Cliente	☒		

ZONIFICACIÓN

Nivel 24
Nivel 23
Nivel 22
Nivel 21
Nivel 20
Nivel 19
Nivel 18
Nivel 17
Nivel 16
Nivel 15
Nivel 14
Nivel 13
Nivel 12
Nivel 11
Nivel 10
Nivel 9
Nivel 8
Nivel 7
Nivel 6
Nivel 5
Nivel 4
Nivel 3
Nivel 2
Nivel 1
Nivel S1
Nivel S2

ENTREGA FINAL
APTO PARA CONSTRUCCIÓN

KEY PLAN

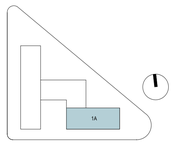

Fecha: 26-07-2024

Escala: 1 : 200

FACHADAS ORIENTE Y OCCIDENTE

CTIB_CNI_EST_202_ELE_XXX_01

10/05/2024 12:18:12 p. m.