


15000x30412 18 16 17 m

N.E. NIVEL SOBRECORRIDO
NE 102.75 m
N.E. NIVEL CUBIERTA
NE 101.35 m
N.E. NIVEL 04 TERRAZA
NE 96.55 m
N.E. NIVEL 23
NE 92.55 m
N.E. NIVEL 22
NE 88.55 m
N.E. NIVEL 21
NE 84.55 m
N.E. NIVEL 20
NE 80.55 m
N.E. NIVEL 19
NE 76.55 m
N.E. NIVEL 18
NE 72.55 m
N.E. NIVEL 17
NE 68.55 m
N.E. NIVEL 16
NE 64.55 m
N.E. NIVEL 15
NE 60.55 m
N.E. NIVEL 14
NE 56.55 m
N.E. NIVEL 13
NE 52.55 m
N.E. NIVEL 12
NE 48.55 m
N.E. NIVEL 11
NE 44.55 m
N.E. NIVEL 10
NE 40.55 m
N.E. NIVEL 9
NE 36.55 m
N.E. NIVEL 8
NE 32.55 m
N.E. NIVEL 7
NE 28.55 m
N.E. NIVEL 6
NE 24.00 m
N.E. NIVEL 5
NE 20.00 m
N.E. NIVEL 4
NE 15.50 m
N.E. NIVEL 3
NE 11.50 m
N.E. NIVEL 2
NE 8.00 m
N.E. NIVEL 1
NE 0.10 m
N.E. NIVEL B1
NE -4.50 m
N.E. NIVEL B2
NE -8.30 m
N.E. NIVEL B3 TANQUE
NE -11.50 m

CORTE LONGITUDINAL
escala 1:200

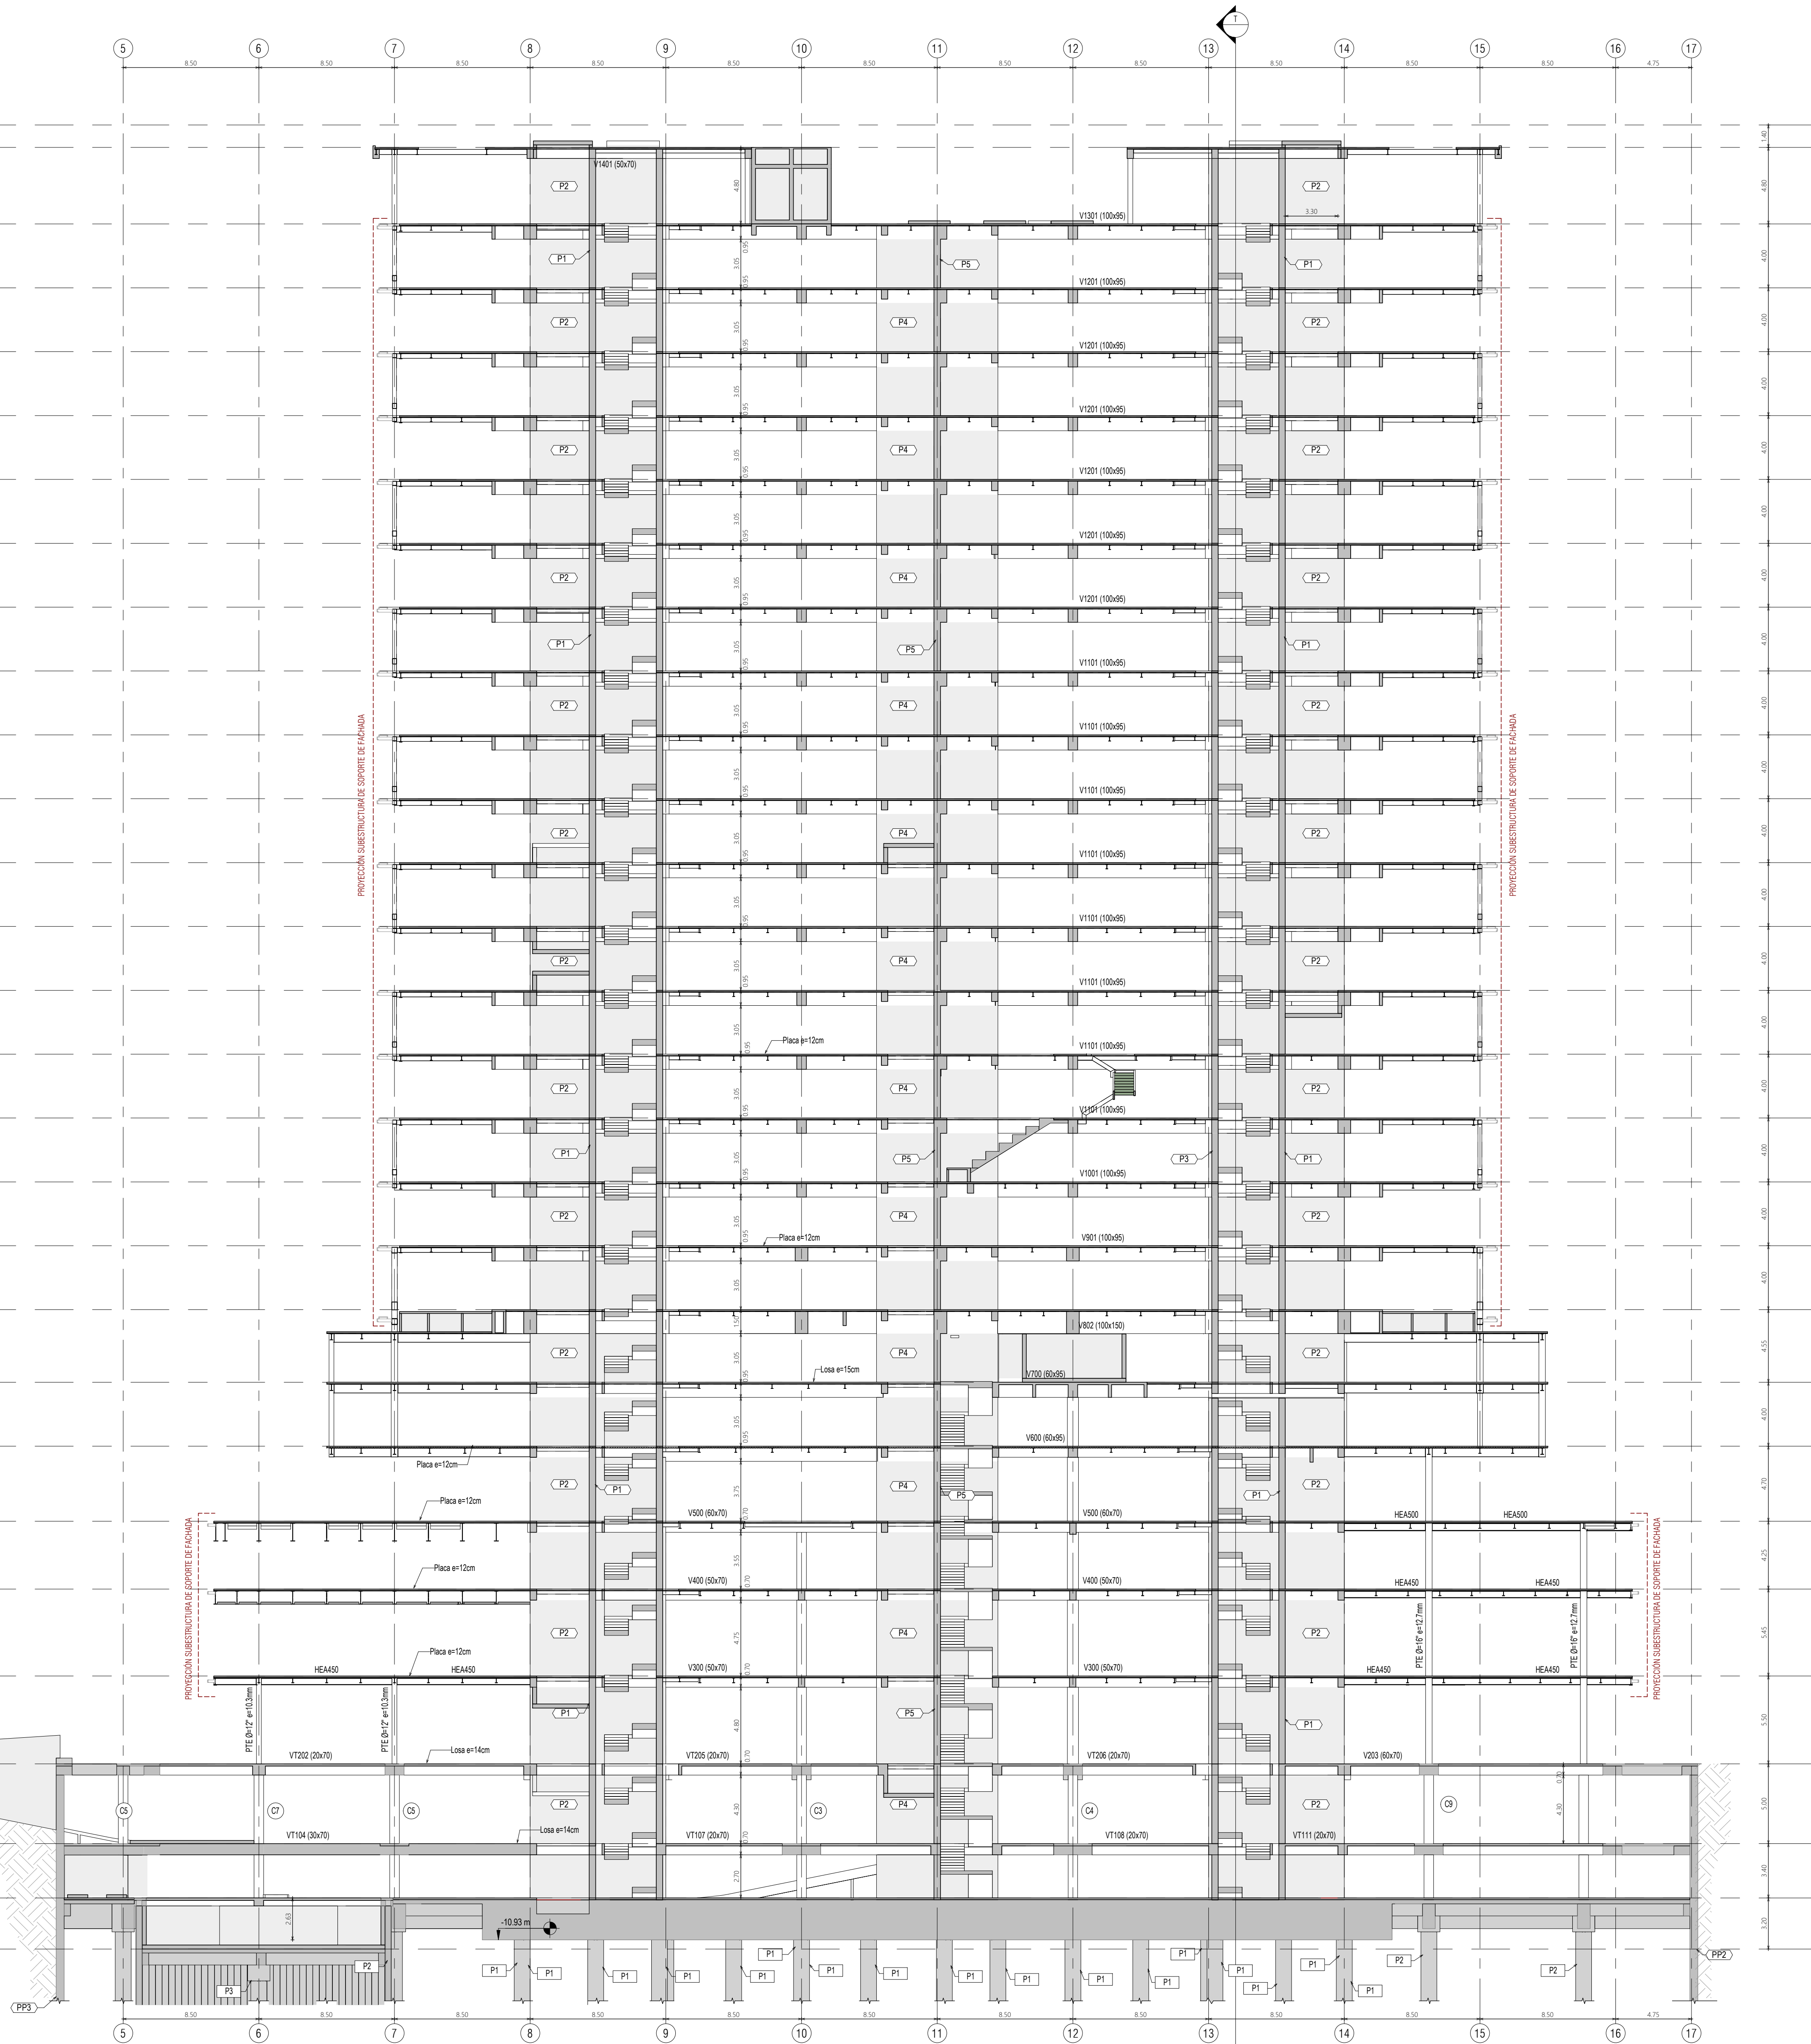


Versión	Emisión	Descripción
AA	15-06-2023	Ingeniería básica
AB	04-08-2023	Anteproyecto
AC	01-11-2023	Anteproyecto V2 50%
AD	15-12-2023	Anteproyecto V2 100%
DD	13-03-2024	Curaduría V2
EE	10-05-2024	Proyecto final 100%
EF	31-05-2024	Respuestas Obs. 100%
FF	21-06-2024	Entrega final
01	26-07-2024	ENTREGA FINAL

PROYECTO:
CAMPUS DE CIENCIA, TECNOLOGÍA E
INNOVACIÓN DE BOGOTÁ
MAT. No. 500-0025470

FASE
ENTREGA FINAL

PROPÓSITO DE EMISIÓN	
Curaduría	☐ Coordinación
Revisión	☐ Construcción
Entrega Cliente	☒

ZONIFICACIÓN	
Nivel 24	
Nivel 23	
Nivel 22	
Nivel 21	
Nivel 20	
Nivel 19	
Nivel 18	
Nivel 17	
Nivel 16	
Nivel 15	
Nivel 14	
Nivel 13	
Nivel 12	
Nivel 11	
Nivel 10	
Nivel 9	
Nivel 8	
Nivel 7	
Nivel 6	
Nivel 5	
Nivel 4	
Nivel 3	
Nivel 2	
Nivel 1	
Nivel B1	
Nivel B2	

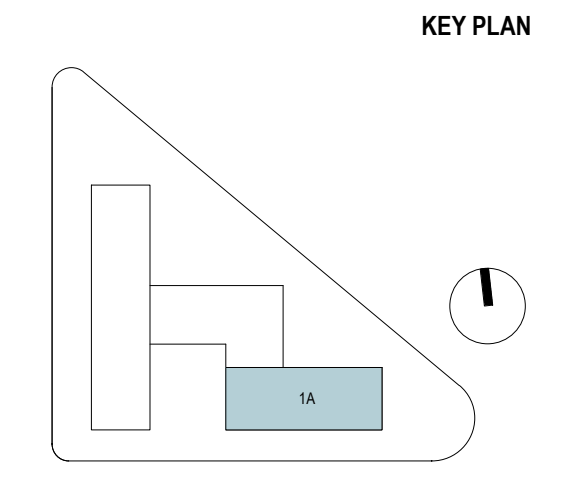

Fecha: 26-07-2024

Escala: 1:200

CORTE LONGITUDINAL

CTIB_CNI_EST_300_SEC_XXX_01