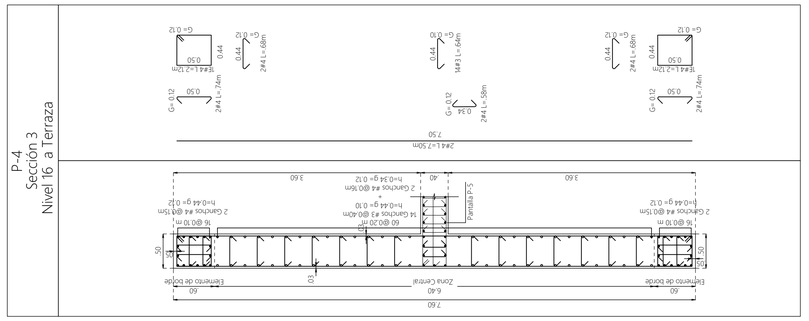

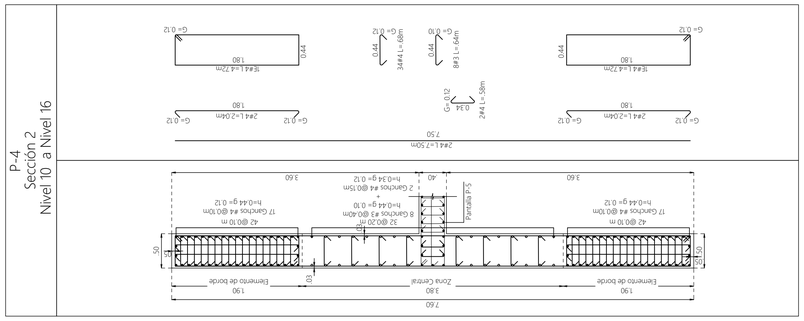

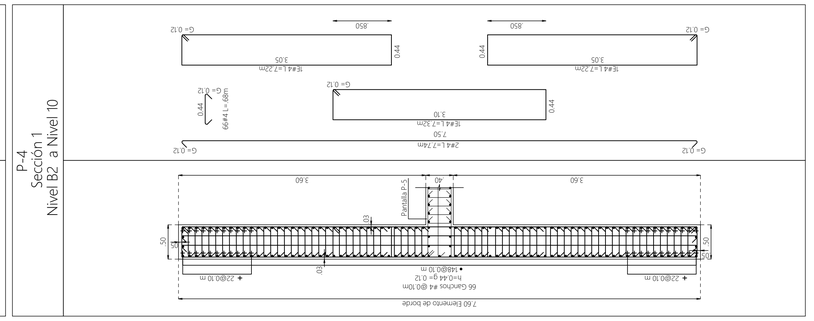

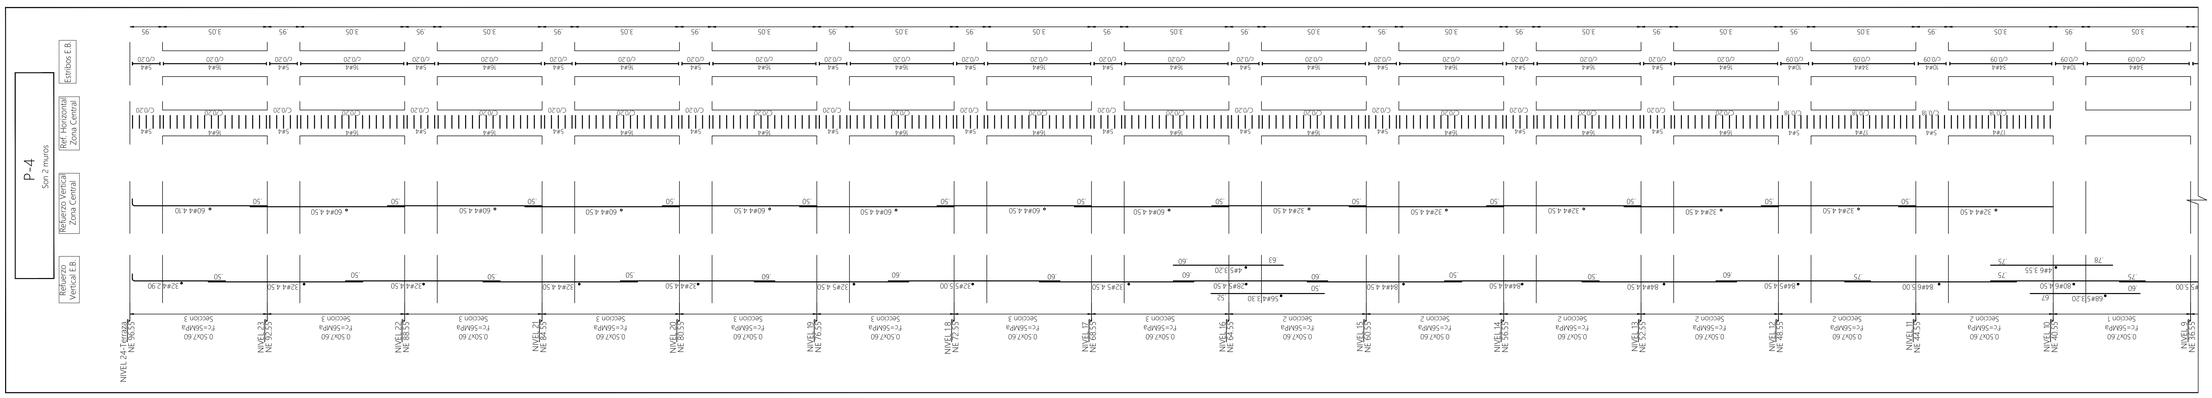

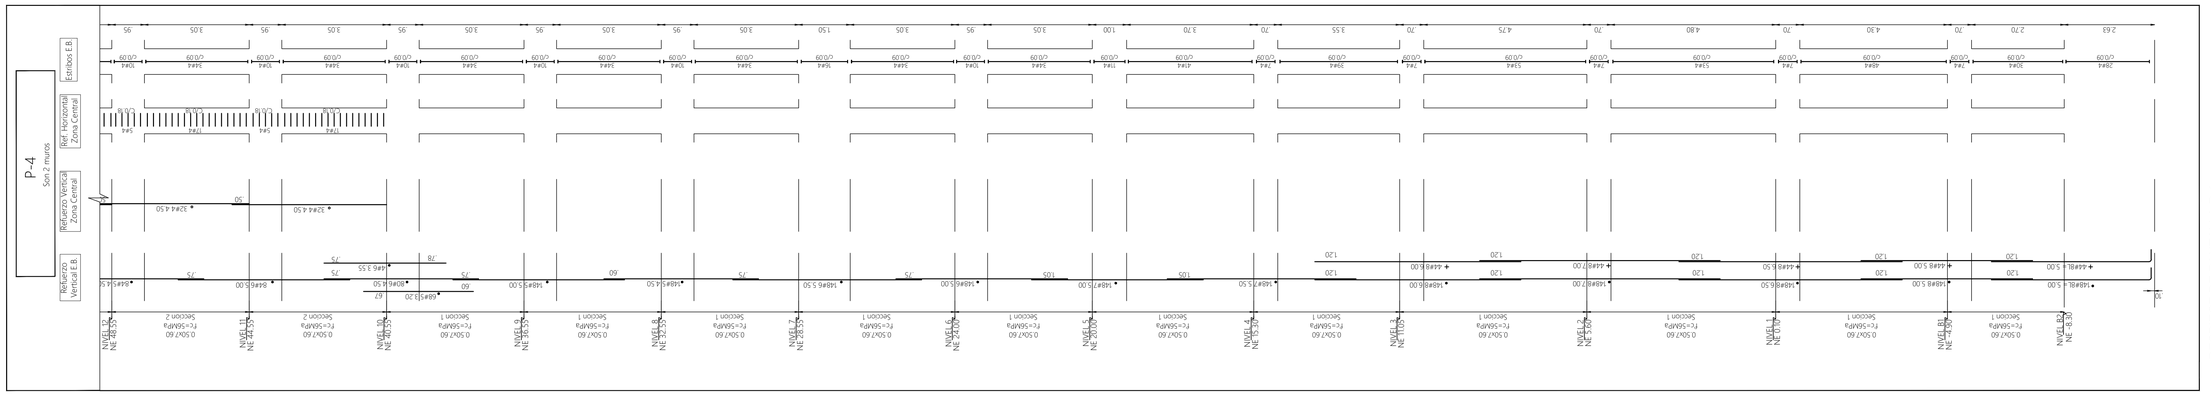

DESPIECE DE PANTALLA P-4
escala 1:75

NOTA: Ver detalle remate refuerzo horizontal zona central muros pantalla plano N°E-0000

CTIB

Campus de Ciencia, Tecnología e Innovación de Bogotá - Región

corferias — Generadores de Oportunidades y Progreso

Cámara de Comercio de Bogotá

BOGOTÁ — Secretaría Distrital de Desarrollo Económico

ARQUITECTO COORDINADOR

EL EQUIPO MAZZANTI + Gensler

DISEÑO ESTRUCTURAL

CNI INGENIEROS

DISEÑADOR: ING. NICOLÁS PARRA GARCÍA, MAT. 25202 62063 CND

INTERVENTORÍA

GUTIÉRREZ DÍAZ S.A.S.
SUPERVISIÓN Y GESTIÓN DE PROYECTOS DE CONSTRUCCIÓN

Director de Interventoría: Ing. Jorge Iván Garcia Mancilla, Mat. 632021 148063 QND

Versión	Emisión	Descripción
AA	15-06-2023	Ingeniería básica
AB	04-08-2023	Anteproyecto
AC	01-11-2023	Anteproyecto V2 50%
AD	15-12-2023	Anteproyecto V2 100%
DD	13-03-2024	Entrega curaduría
EE	10-05-2024	Proyecto Final 100%
EF	31-05-2024	Respuesta Obs 100%
FF	21-06-2024	Entrega Final
01	26-07-2024	ENTREGA FINAL

PROYECTO:

CAMPUS DE CIENCIA TECNOLOGÍA E INNOVACIÓN DE BOGOTA

MAT.: No. SDC-00252470

FASE

ENTREGA FINAL

PROPÓSITO DE EMISIÓN

Curaduría	☐	Coordinación	☐
Revisión	☐	Construcción	■
Entrega Cliente	■		

PROYECTO DETALLADO

APTO PARA CONSTRUCCIÓN (APC)

ZONIFICACIÓN

Nivel 24
Nivel 23
Nivel 22
Nivel 21
Nivel 20
Nivel 19
Nivel 18
Nivel 17
Nivel 16
Nivel 15
Nivel 14
Nivel 13
Nivel 12
Nivel 11
Nivel 10
Nivel 9
Nivel 8
Nivel 7
Nivel 6
Nivel 5
Nivel 4
Nivel 3
Nivel 2
Nivel 1
Nivel B1
Nivel B2

KEY PLAN

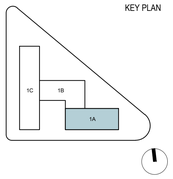

Fecha: 26-07-2024

Escala: As Indicated

DESPIECES DE PANTALLAS

CTIB_CNI_EST_403_DSP_XXX_01