
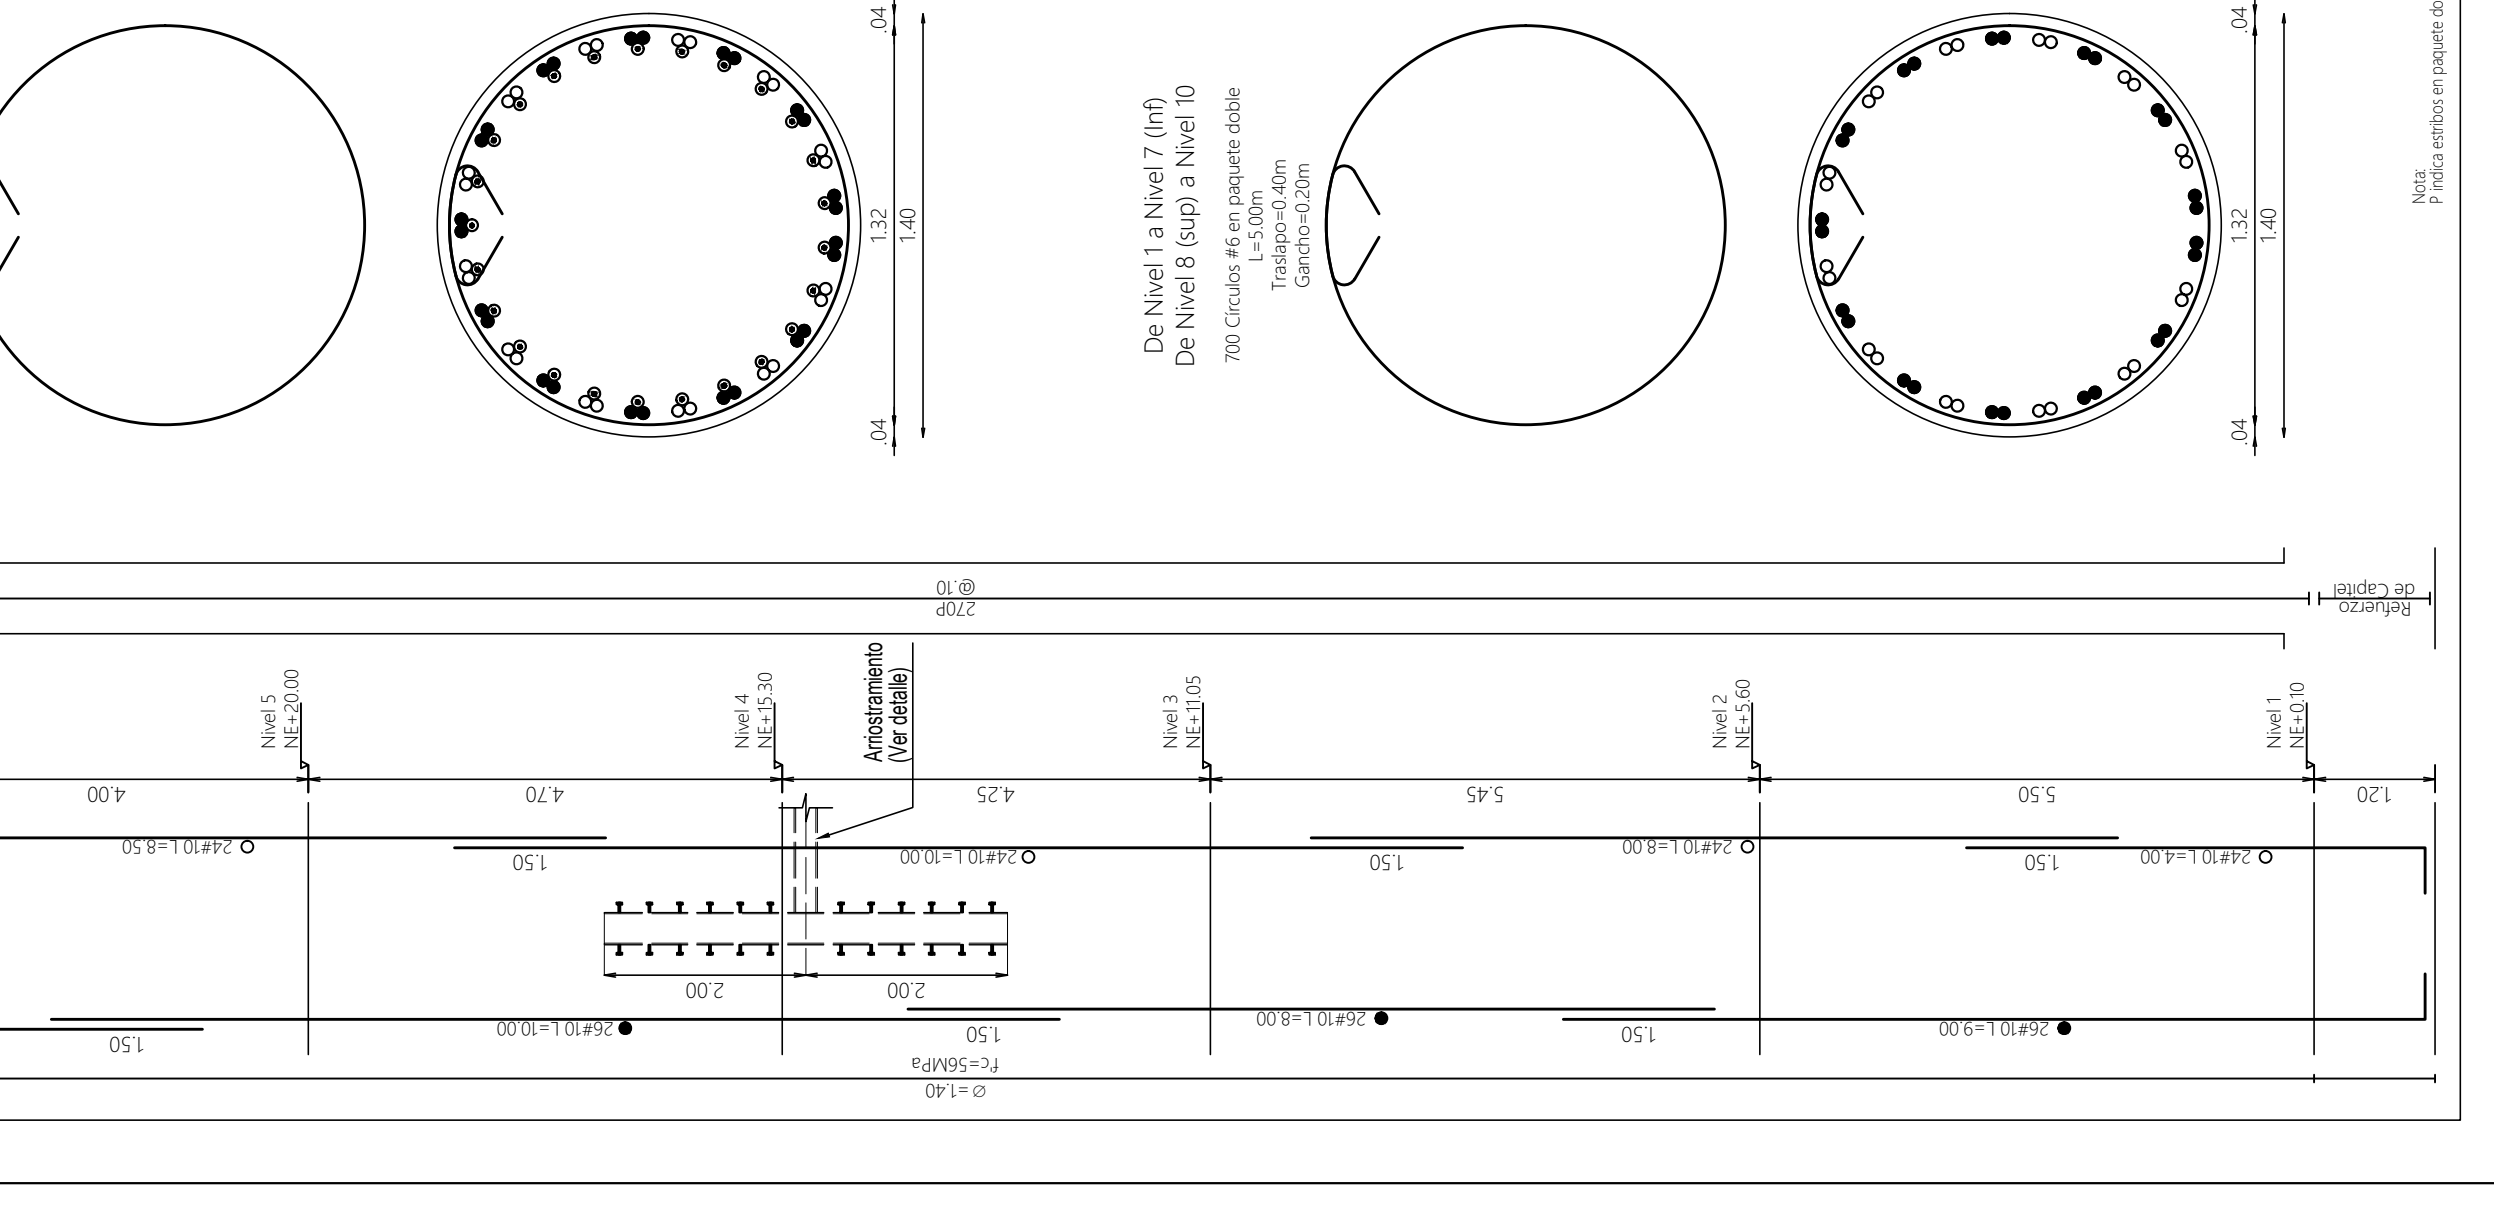
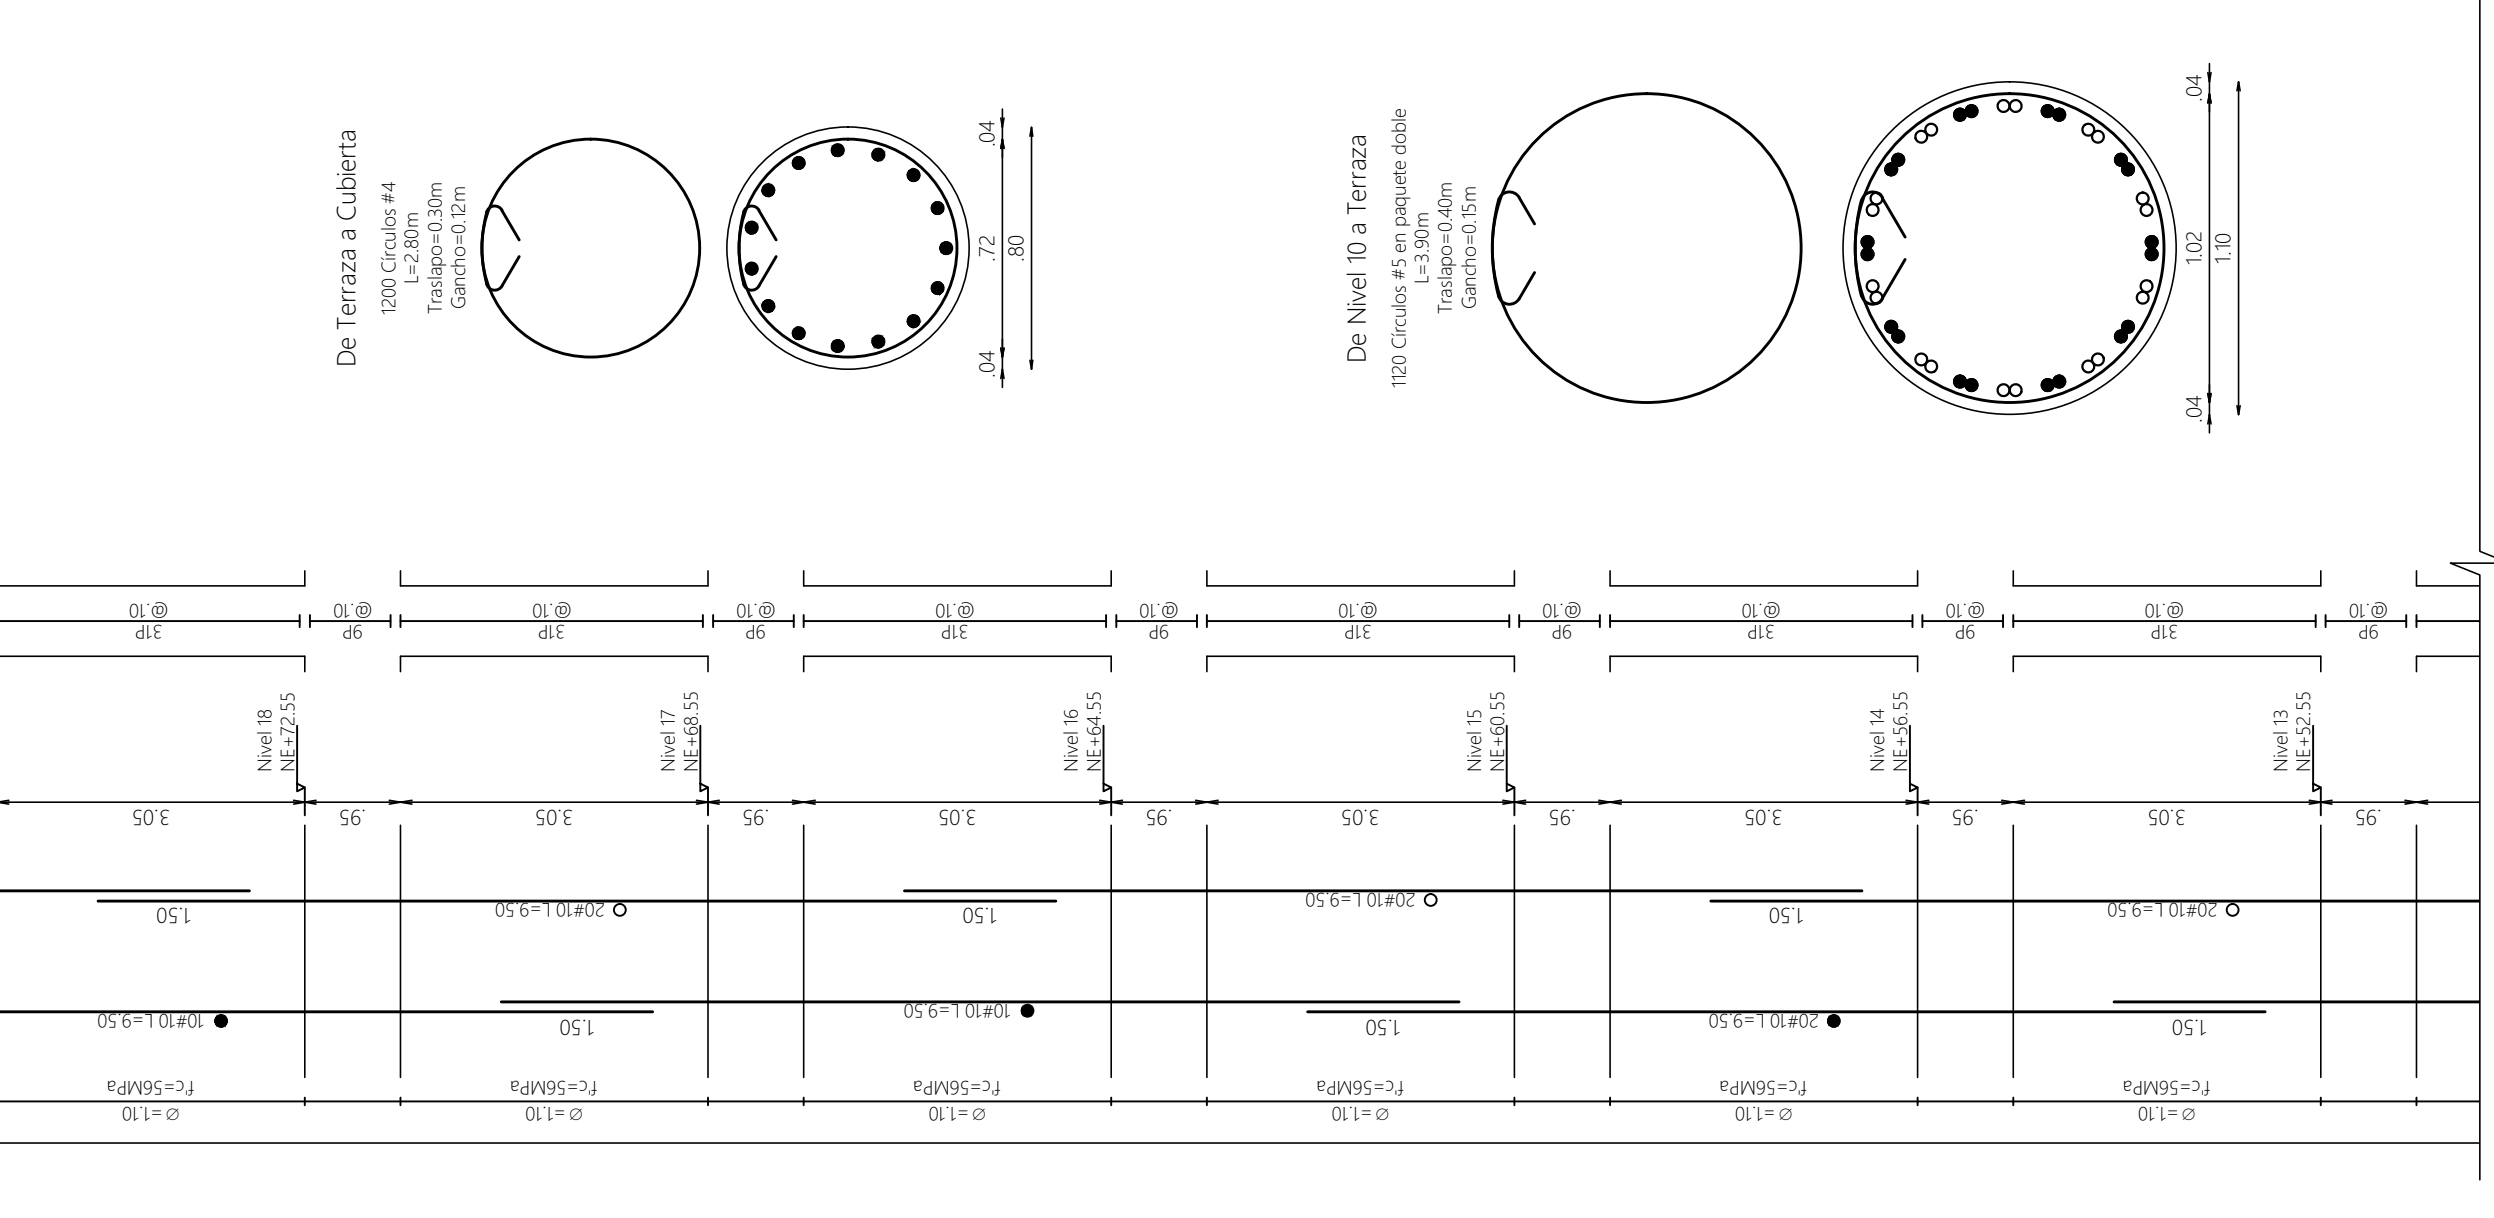
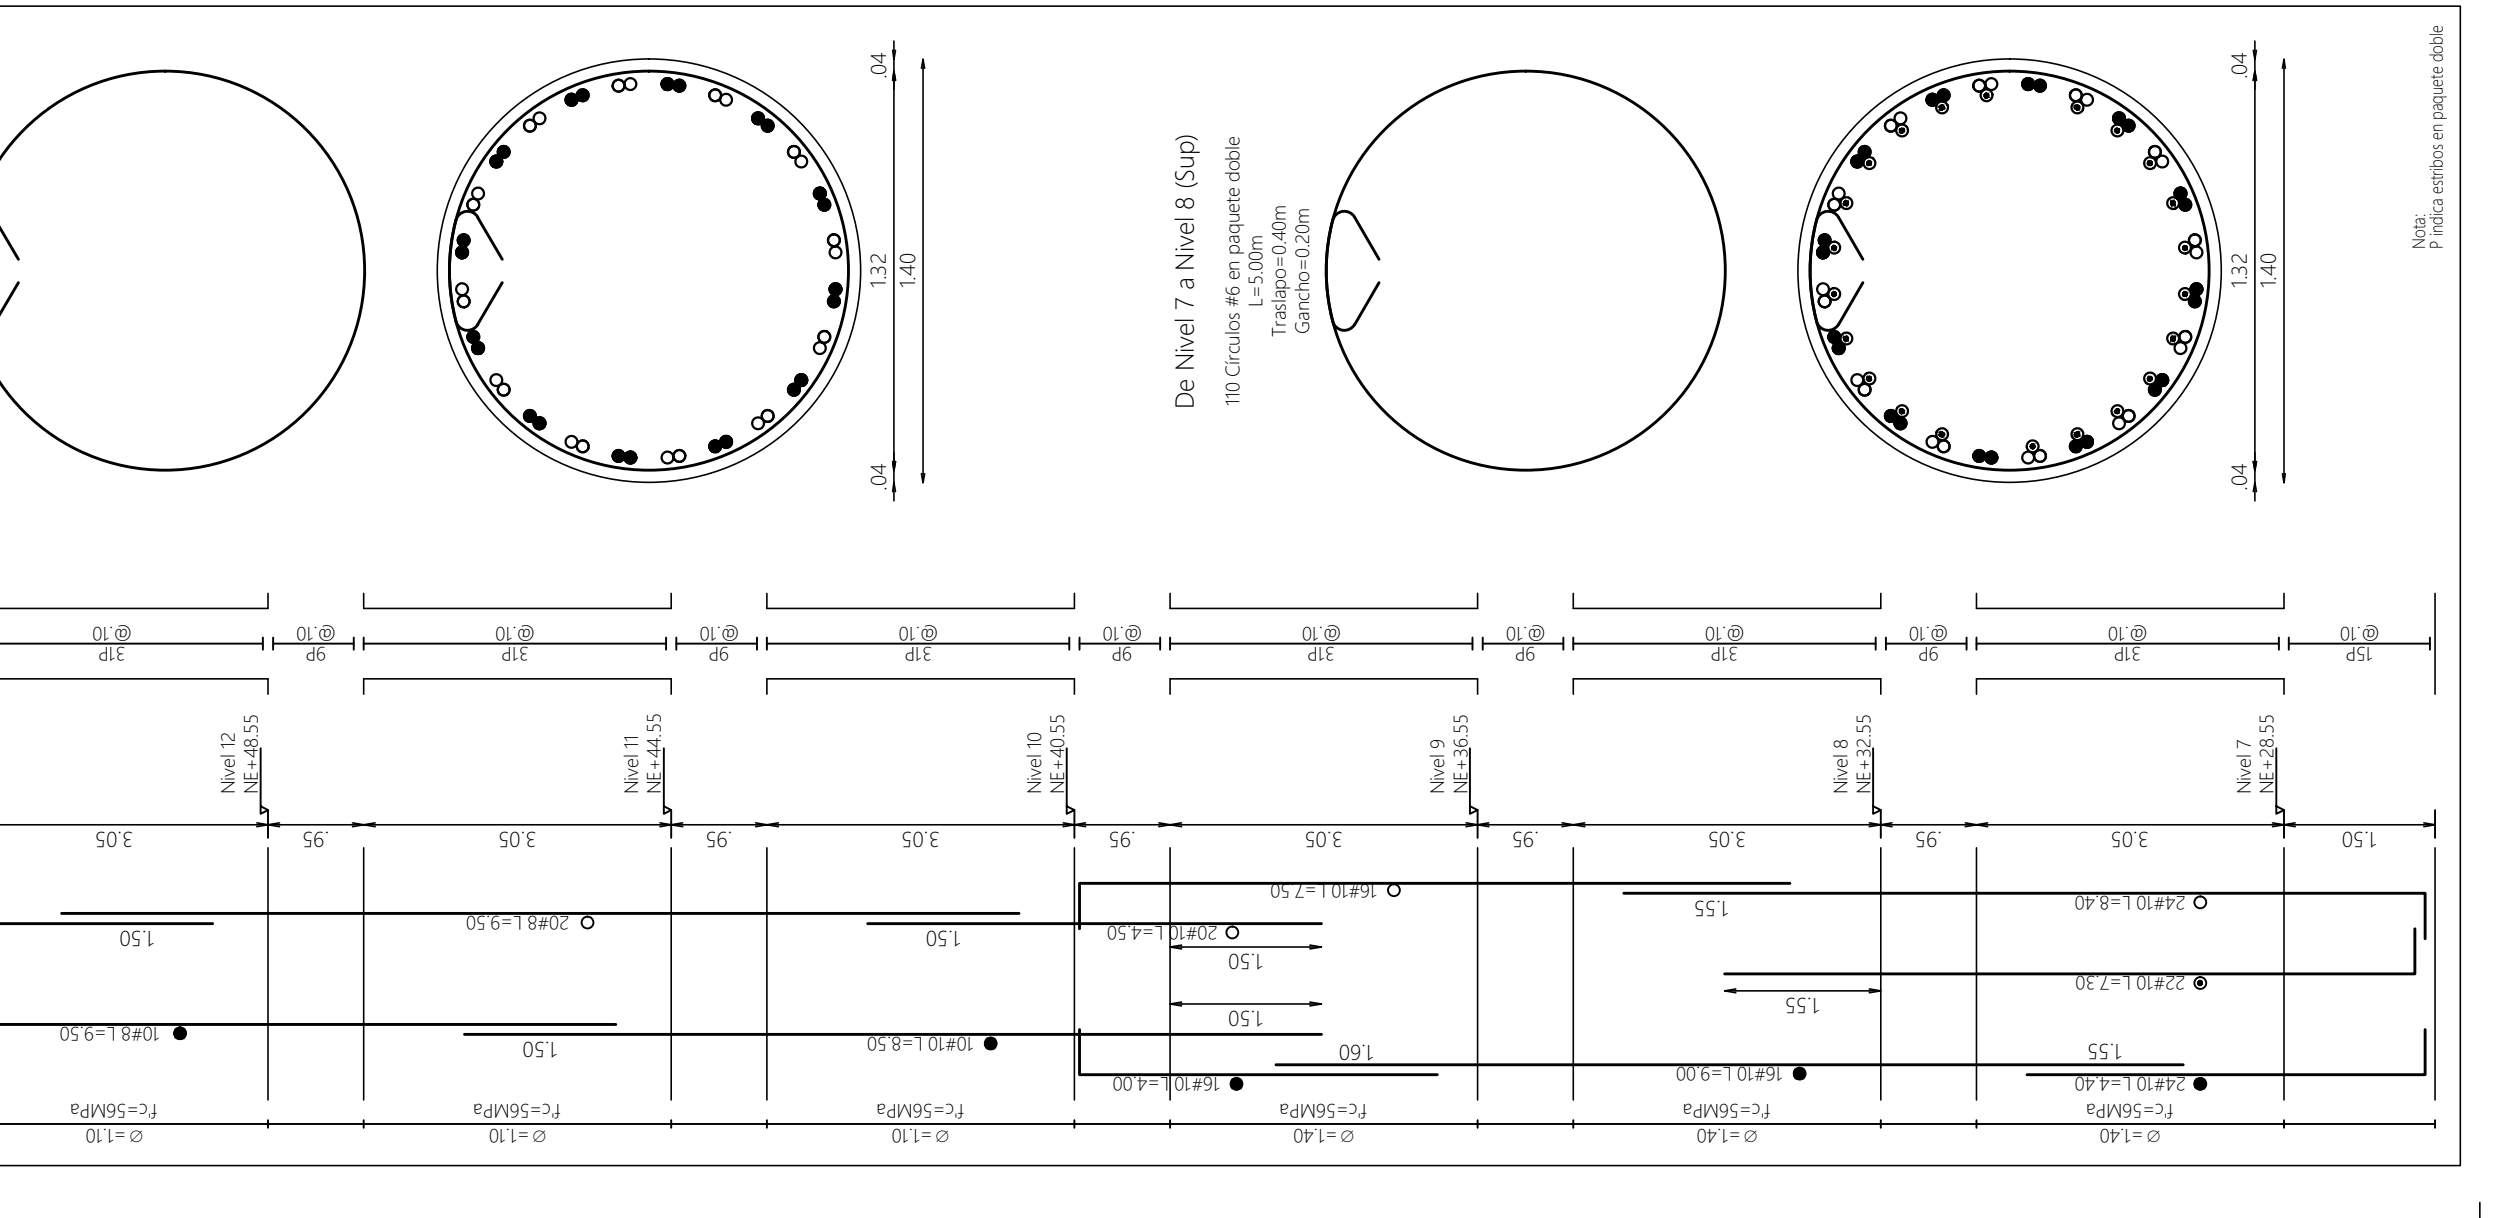
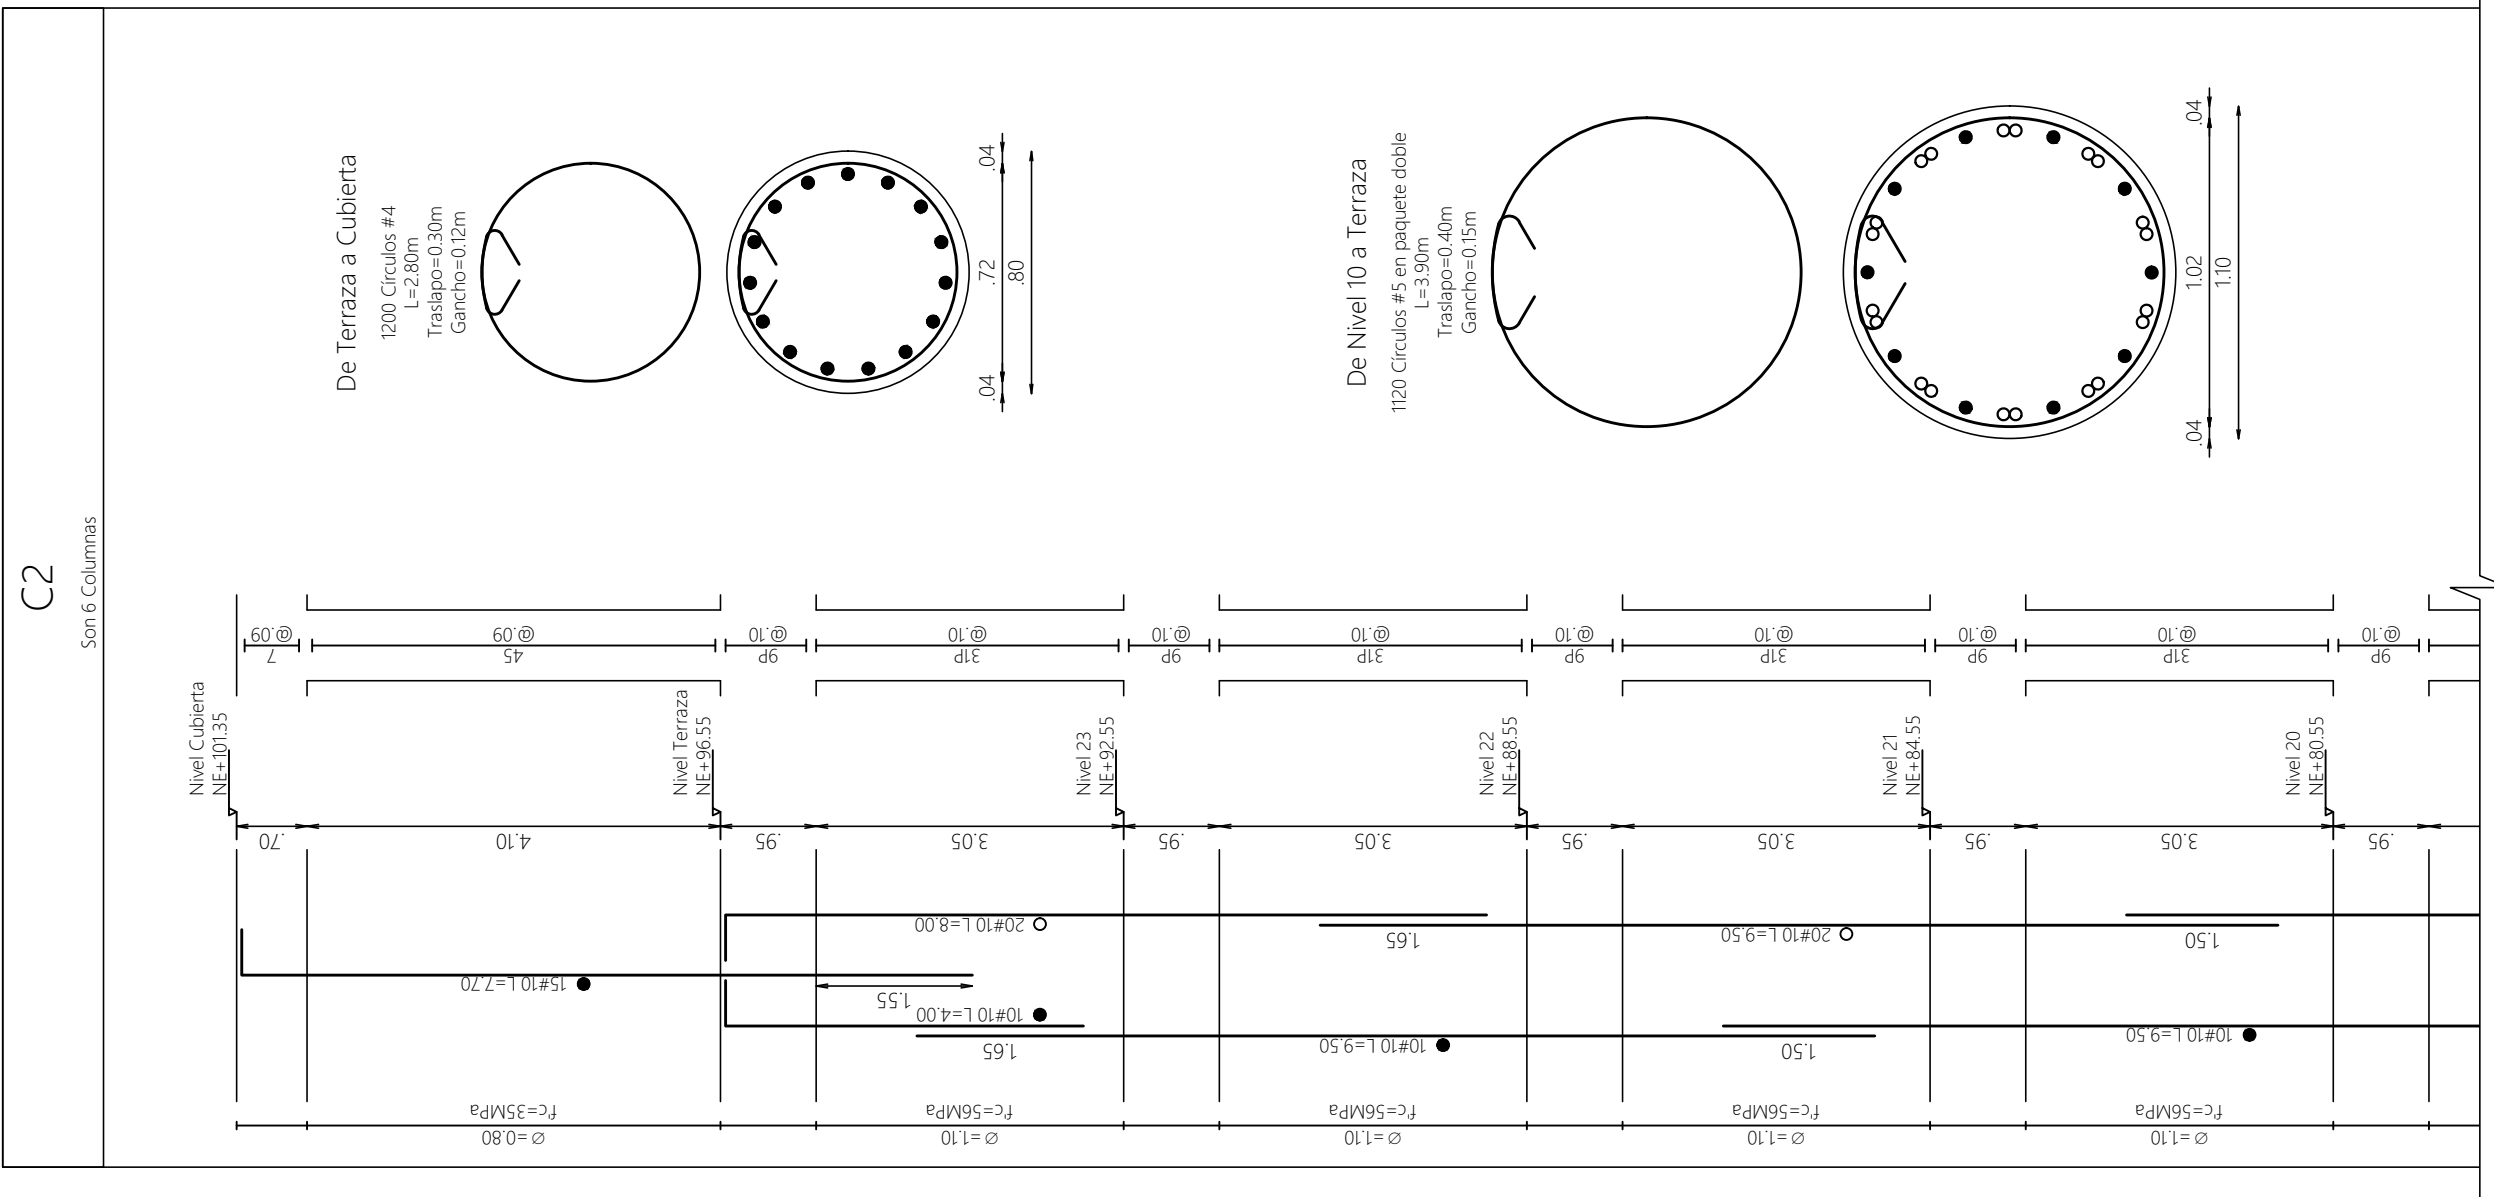
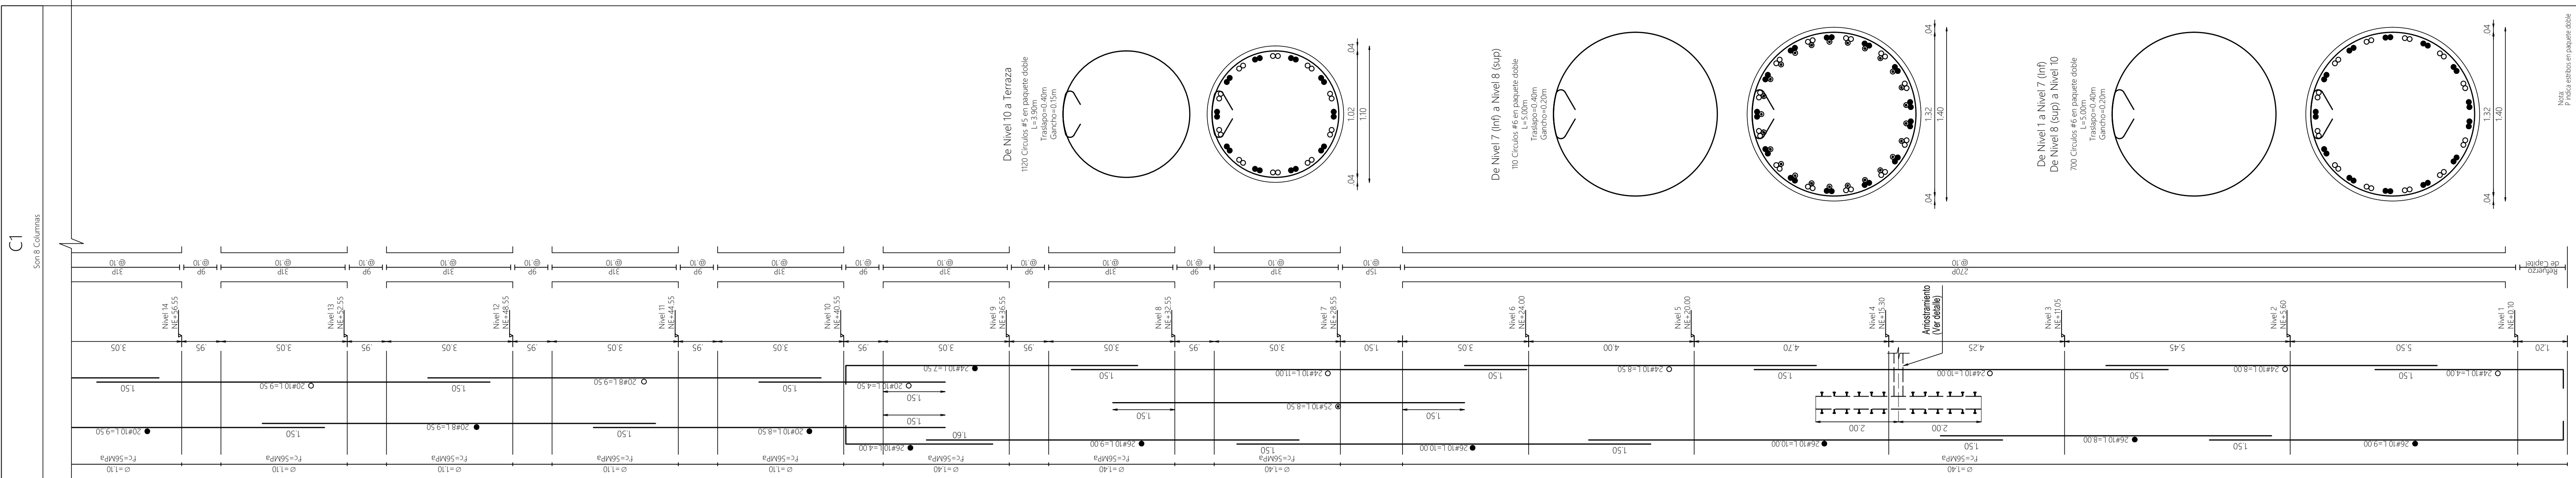
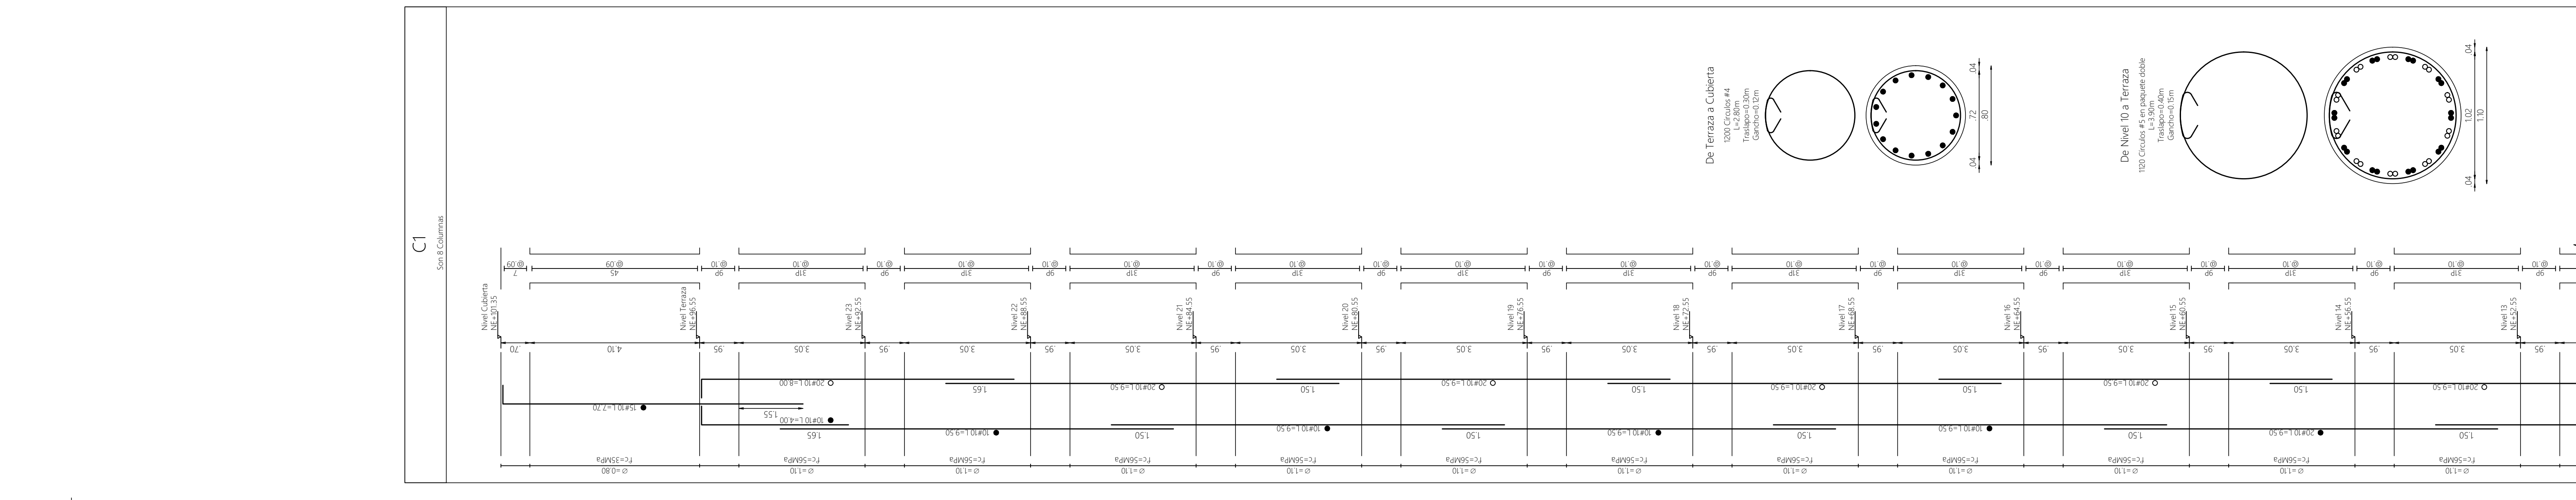


NOTAS IMPORTANTES:

1. Ver detalle de arriostramiento de columnas C1 en Nivel N4 en plano CTIB_CNI_EST_DET_XXX.

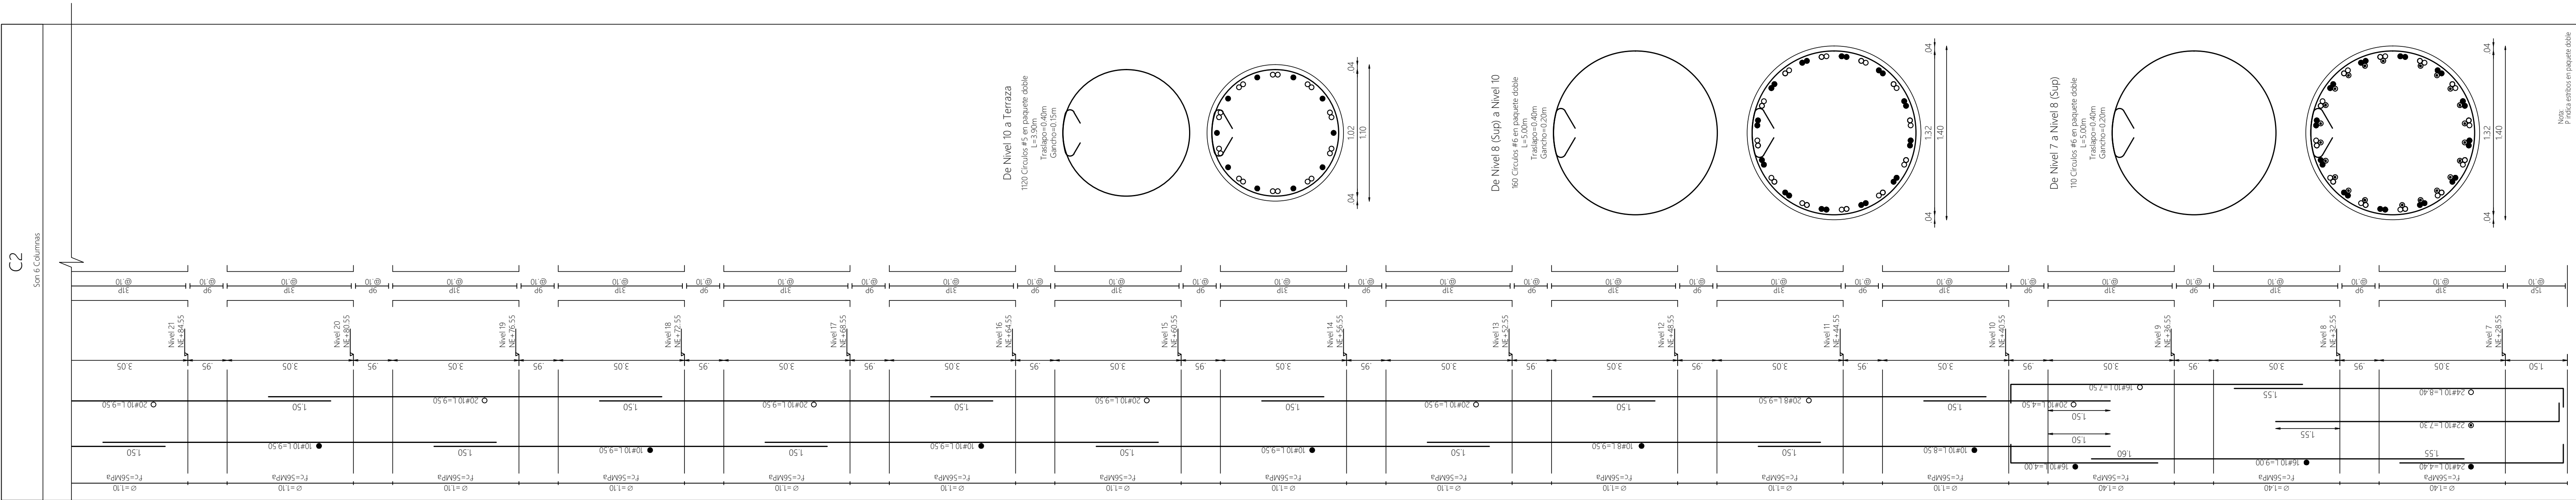

CTIB

Campus de Ciencia, Tecnología e Innovación de Bogotá - Región

corferias

Generadores de Oportunidades y Progreso

Cámara de Comercio de Bogotá

Secretaría Distrital de Desarrollo Económico

BOGOTÁ

Secretaría Distrital de Desarrollo Económico

ARQUITECTO COORDINADOR

ELEQUIPO MAZZANTI + Gensler

DISEÑO ESTRUCTURAL

CNI

DISEÑADOR

ING. NICOLÁS PARRA GARCÍA
MAT. 2202 62063 CND

INTERVENTORIA

GUTIÉRREZ DÍAZ S.A.S.
SUPERVISOR Y LABORATORIO PROYECTOS DE CONSTRUCCIÓN

Director de Interventoría: Ing. Jorge Iván García Mancilla
Mat. 632021 148063 QND

Versión	Emisión	Descripción
AA	15-06-2023	Ingeniería básica
AB	04-08-2023	Anteproyecto
AC	01-11-2023	Anteproyecto V2 50%
AD	15-12-2023	Anteproyecto V2 100%
DD	13-03-2024	Entrega curaduría
EE	10-05-2024	Proyecto Final 100%
EF	31-05-2024	Respuesta Obs 100%
FF	21-06-2024	Entrega Final
01	28-07-2024	ENTREGA FINAL

PROYECTO:

CAMPUS DE CIENCIA TECNOLOGÍA E INNOVACIÓN DE BOGOTÁ

MAT. No. 502-0025470

FASE

ENTREGA FINAL

PROPÓSITO DE EMISIÓN

Curaduría

Revisión

Entrega Cliente

☐

☐

☒

Coordinación

Construcción

☐

☐

ZNIFICACIÓN

Nivel 24

Nivel 23

Nivel 22

Nivel 21

Nivel 20

Nivel 19

Nivel 18

Nivel 17

Nivel 16

Nivel 15

Nivel 14

Nivel 13

Nivel 12

Nivel 11

Nivel 10

Nivel 9

Nivel 8

Nivel 7

Nivel 6

Nivel 5

Nivel 4

Nivel 3

Nivel 2

Nivel 1

Nivel 01

Nivel 02

KEY PLAN

Fecha:

28-07-2024

Escala:

As Indicated

DESPIECES DE COLUMNAS

CTIB_CNI_EST_405_DSP_XXX_01