

PROYECTO:
CAMPUS DE CIENCIA TECNOLOGÍA E
INNOVACIÓN DE BOGOTÁ
MAT - No. 50C-00262470

FASE ENTREGA FINAL

PROPÓSITO DE EMISIÓN

PROPÓSITO DE EMISIÓN

Curaduría	☐	Coordinación	☐
Revisión	☐	Construcción	☒
Entrega Cliente	☒		

ZONIFICACIÓN

PROYECTO
DETALLADO

APTO PARA
CONSTRUCCIÓN
(APC)











KEY PLAN



Escala: As indicated

DESPIECES DE

CTIB CNI EST 408 DSP XXX FF

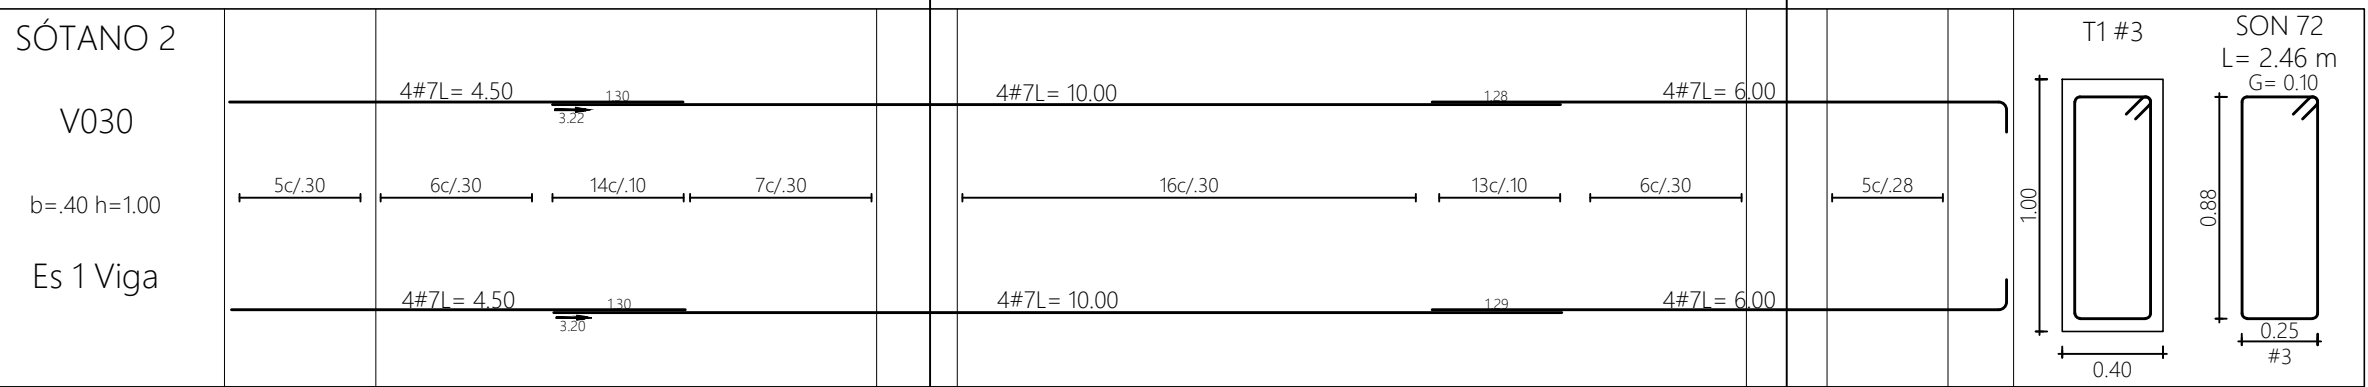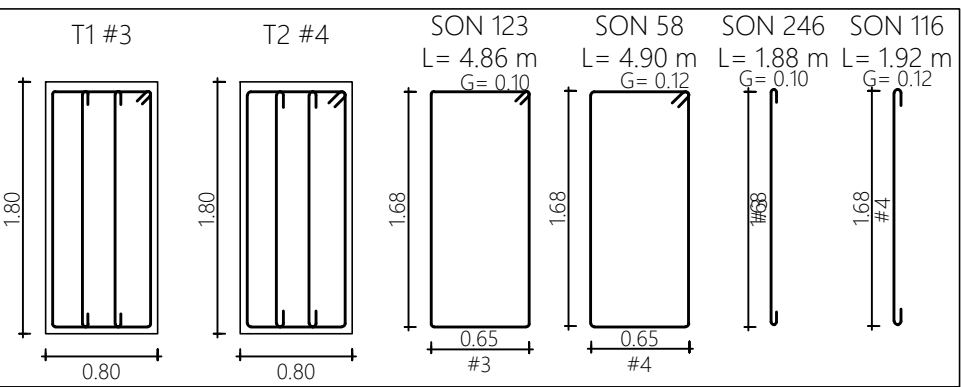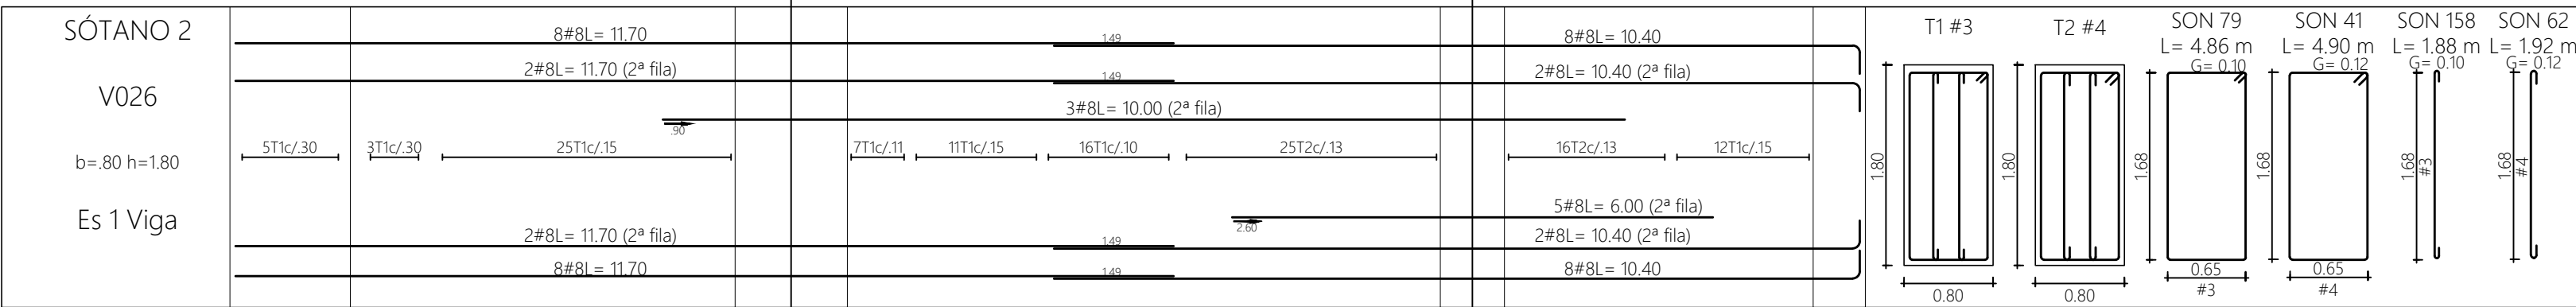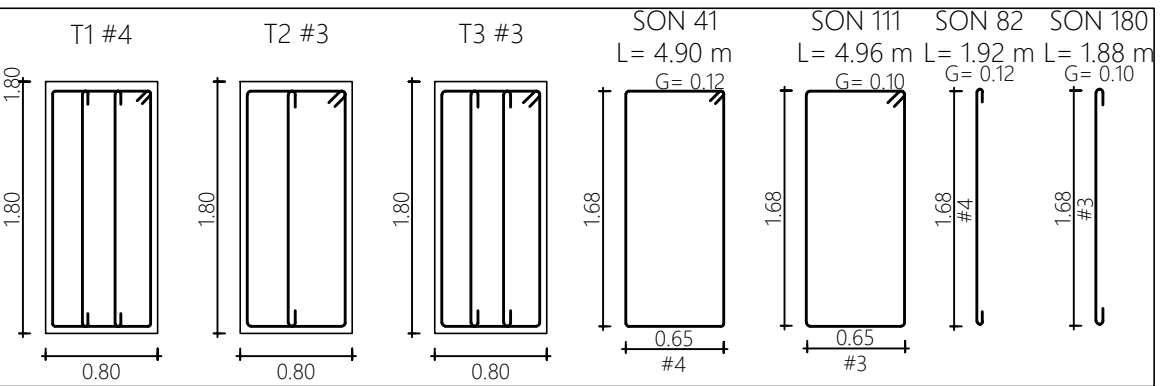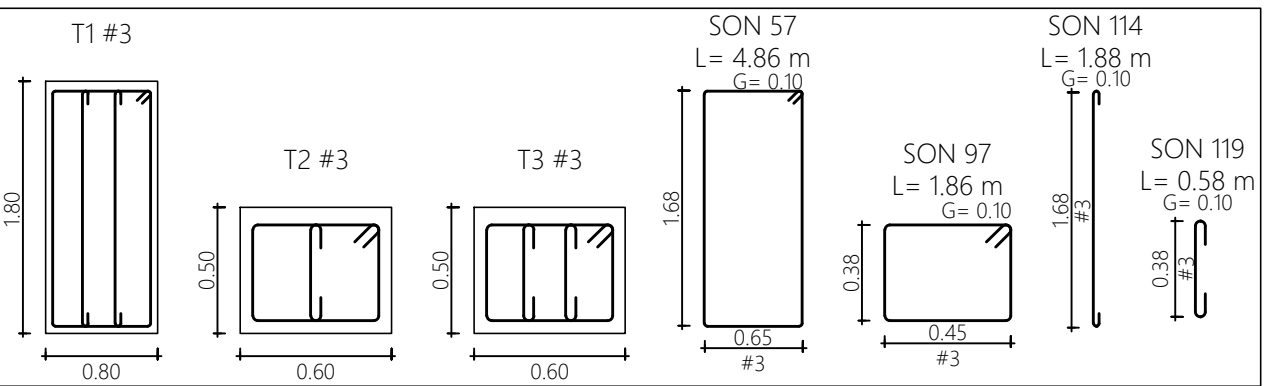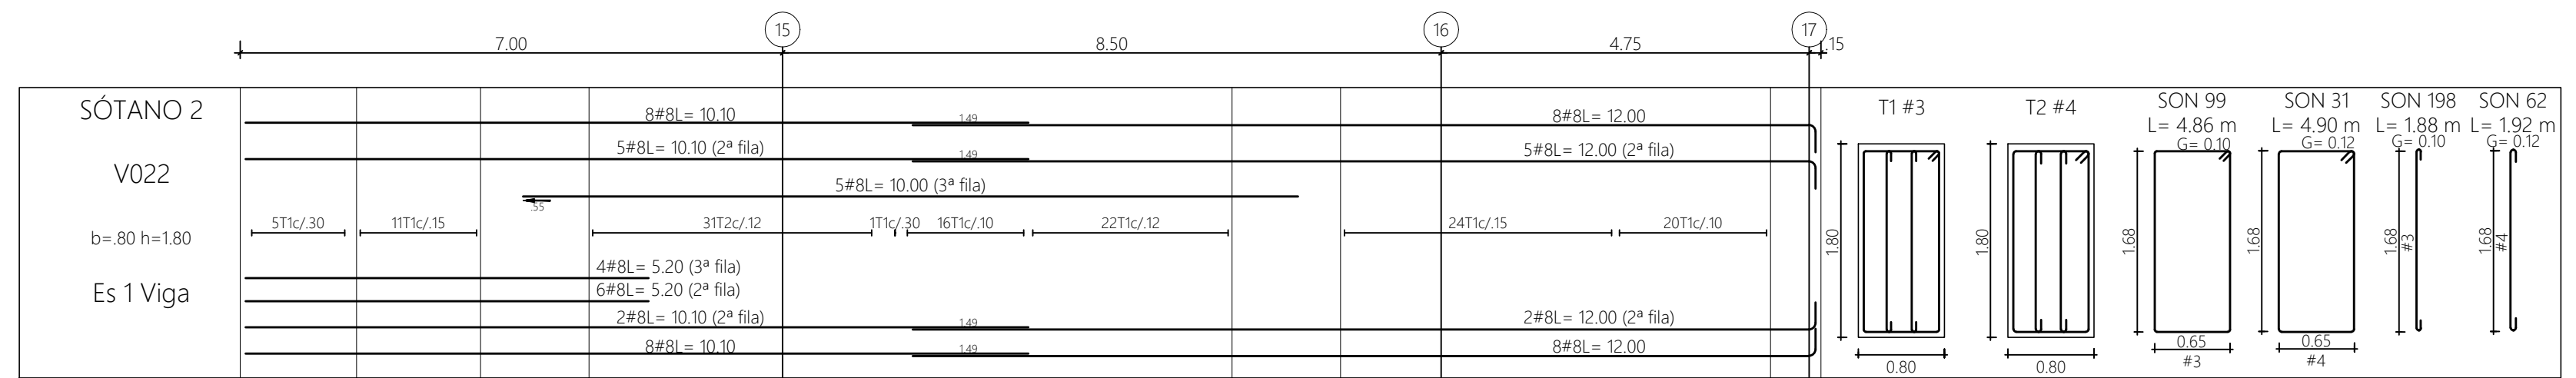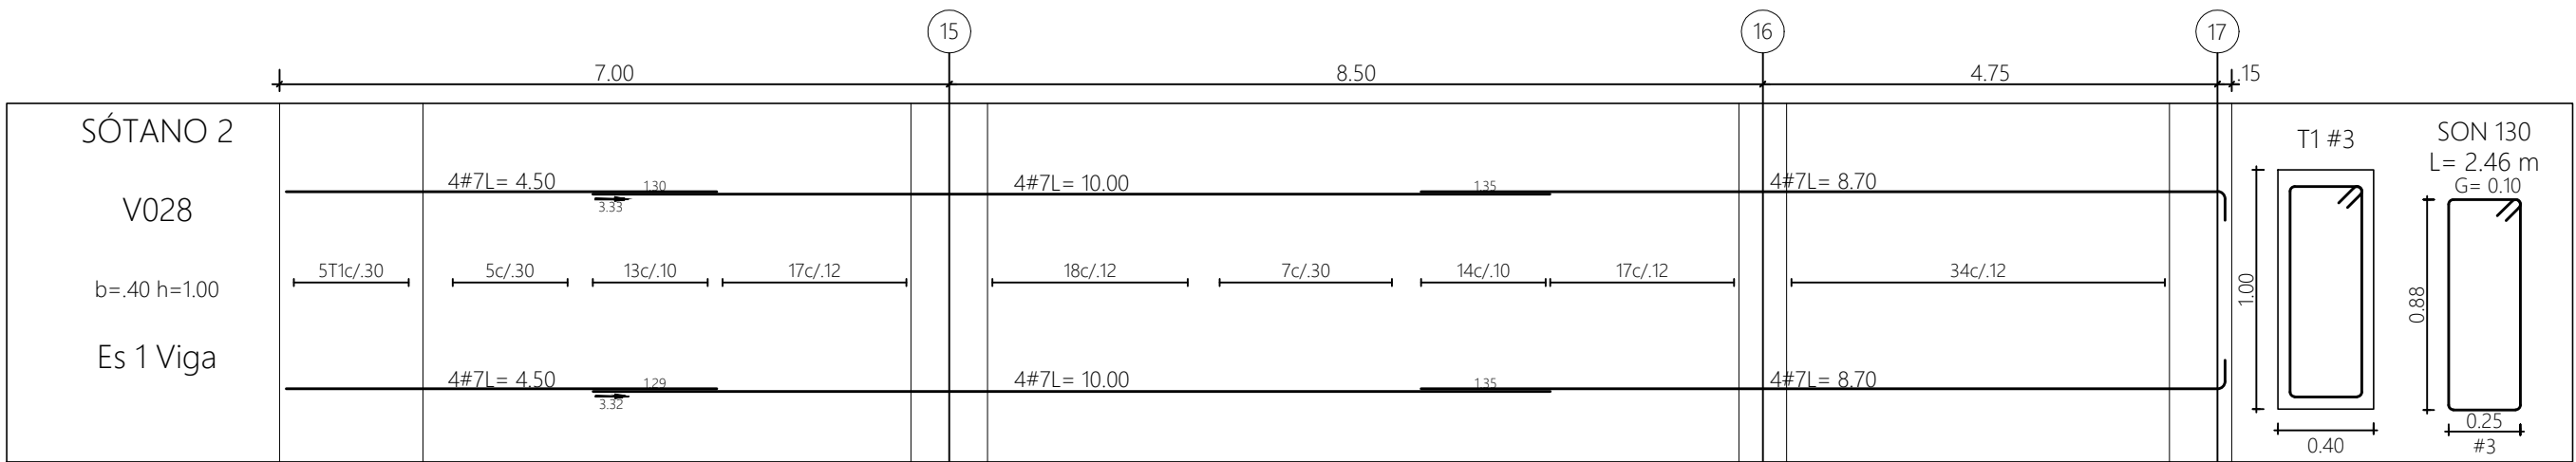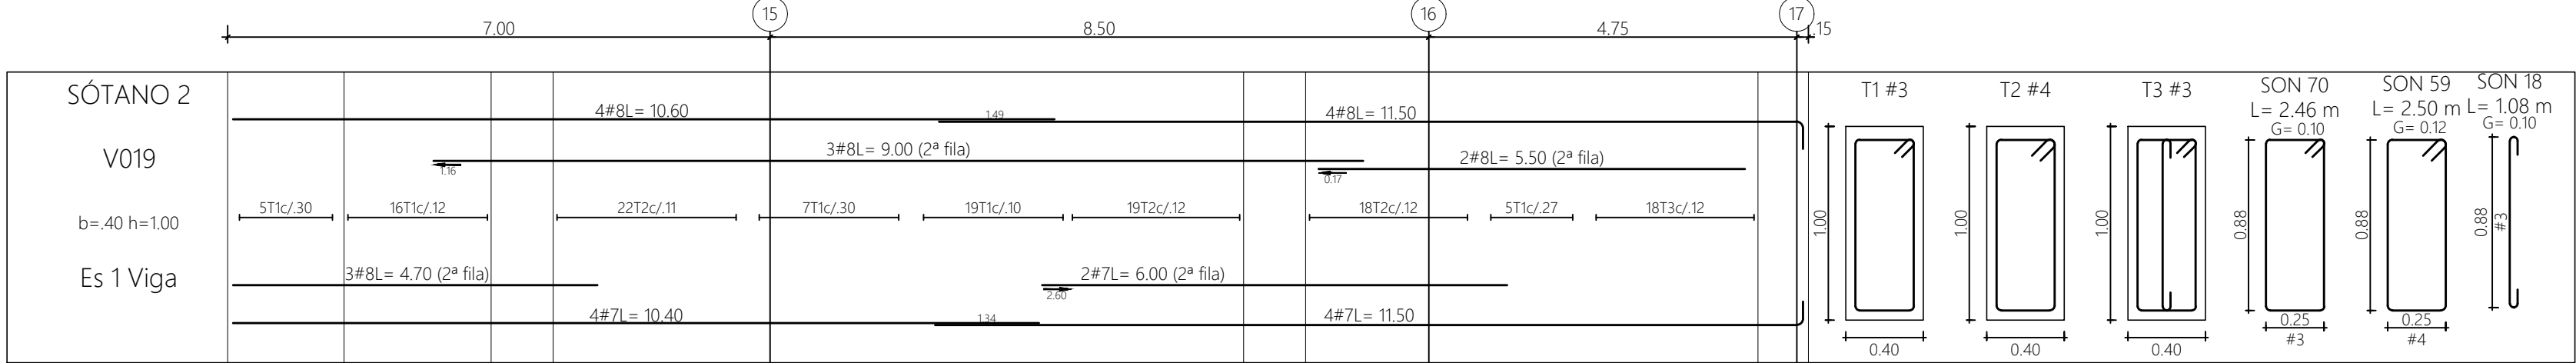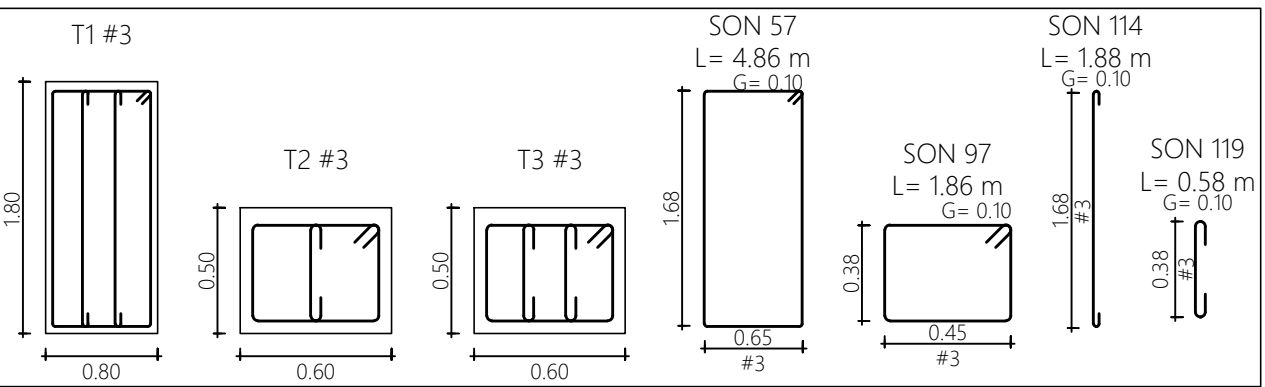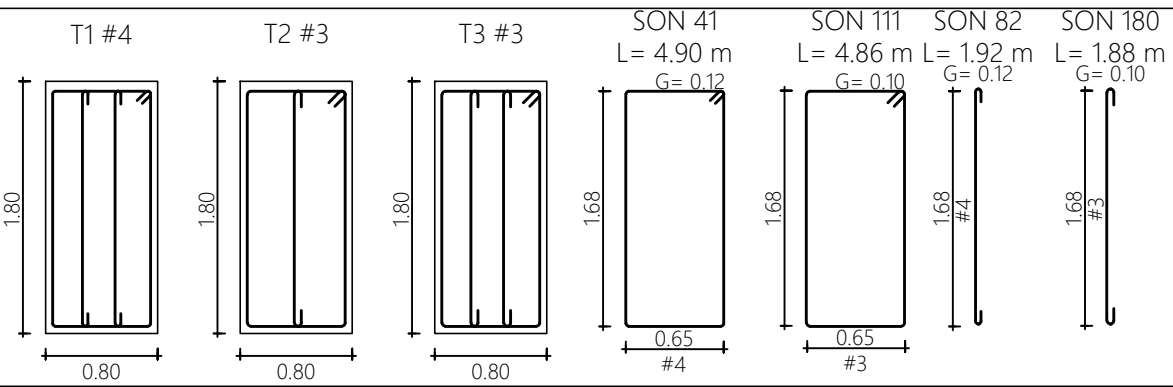

EMPALME MECÁNICO  -INDICA VIGA FUNDIDA SEGUNDA ETAPA

NOTA1: Ver esquema de armado base para vigas y viguetas en plano E000.

NOTA2: En caso de que se requiera, el constructor puede hacer uso de empalmes mecánicos tipo 2

DESPIECE DE VIGAS SOTANO 2
escala 1:75

escala 1:75