


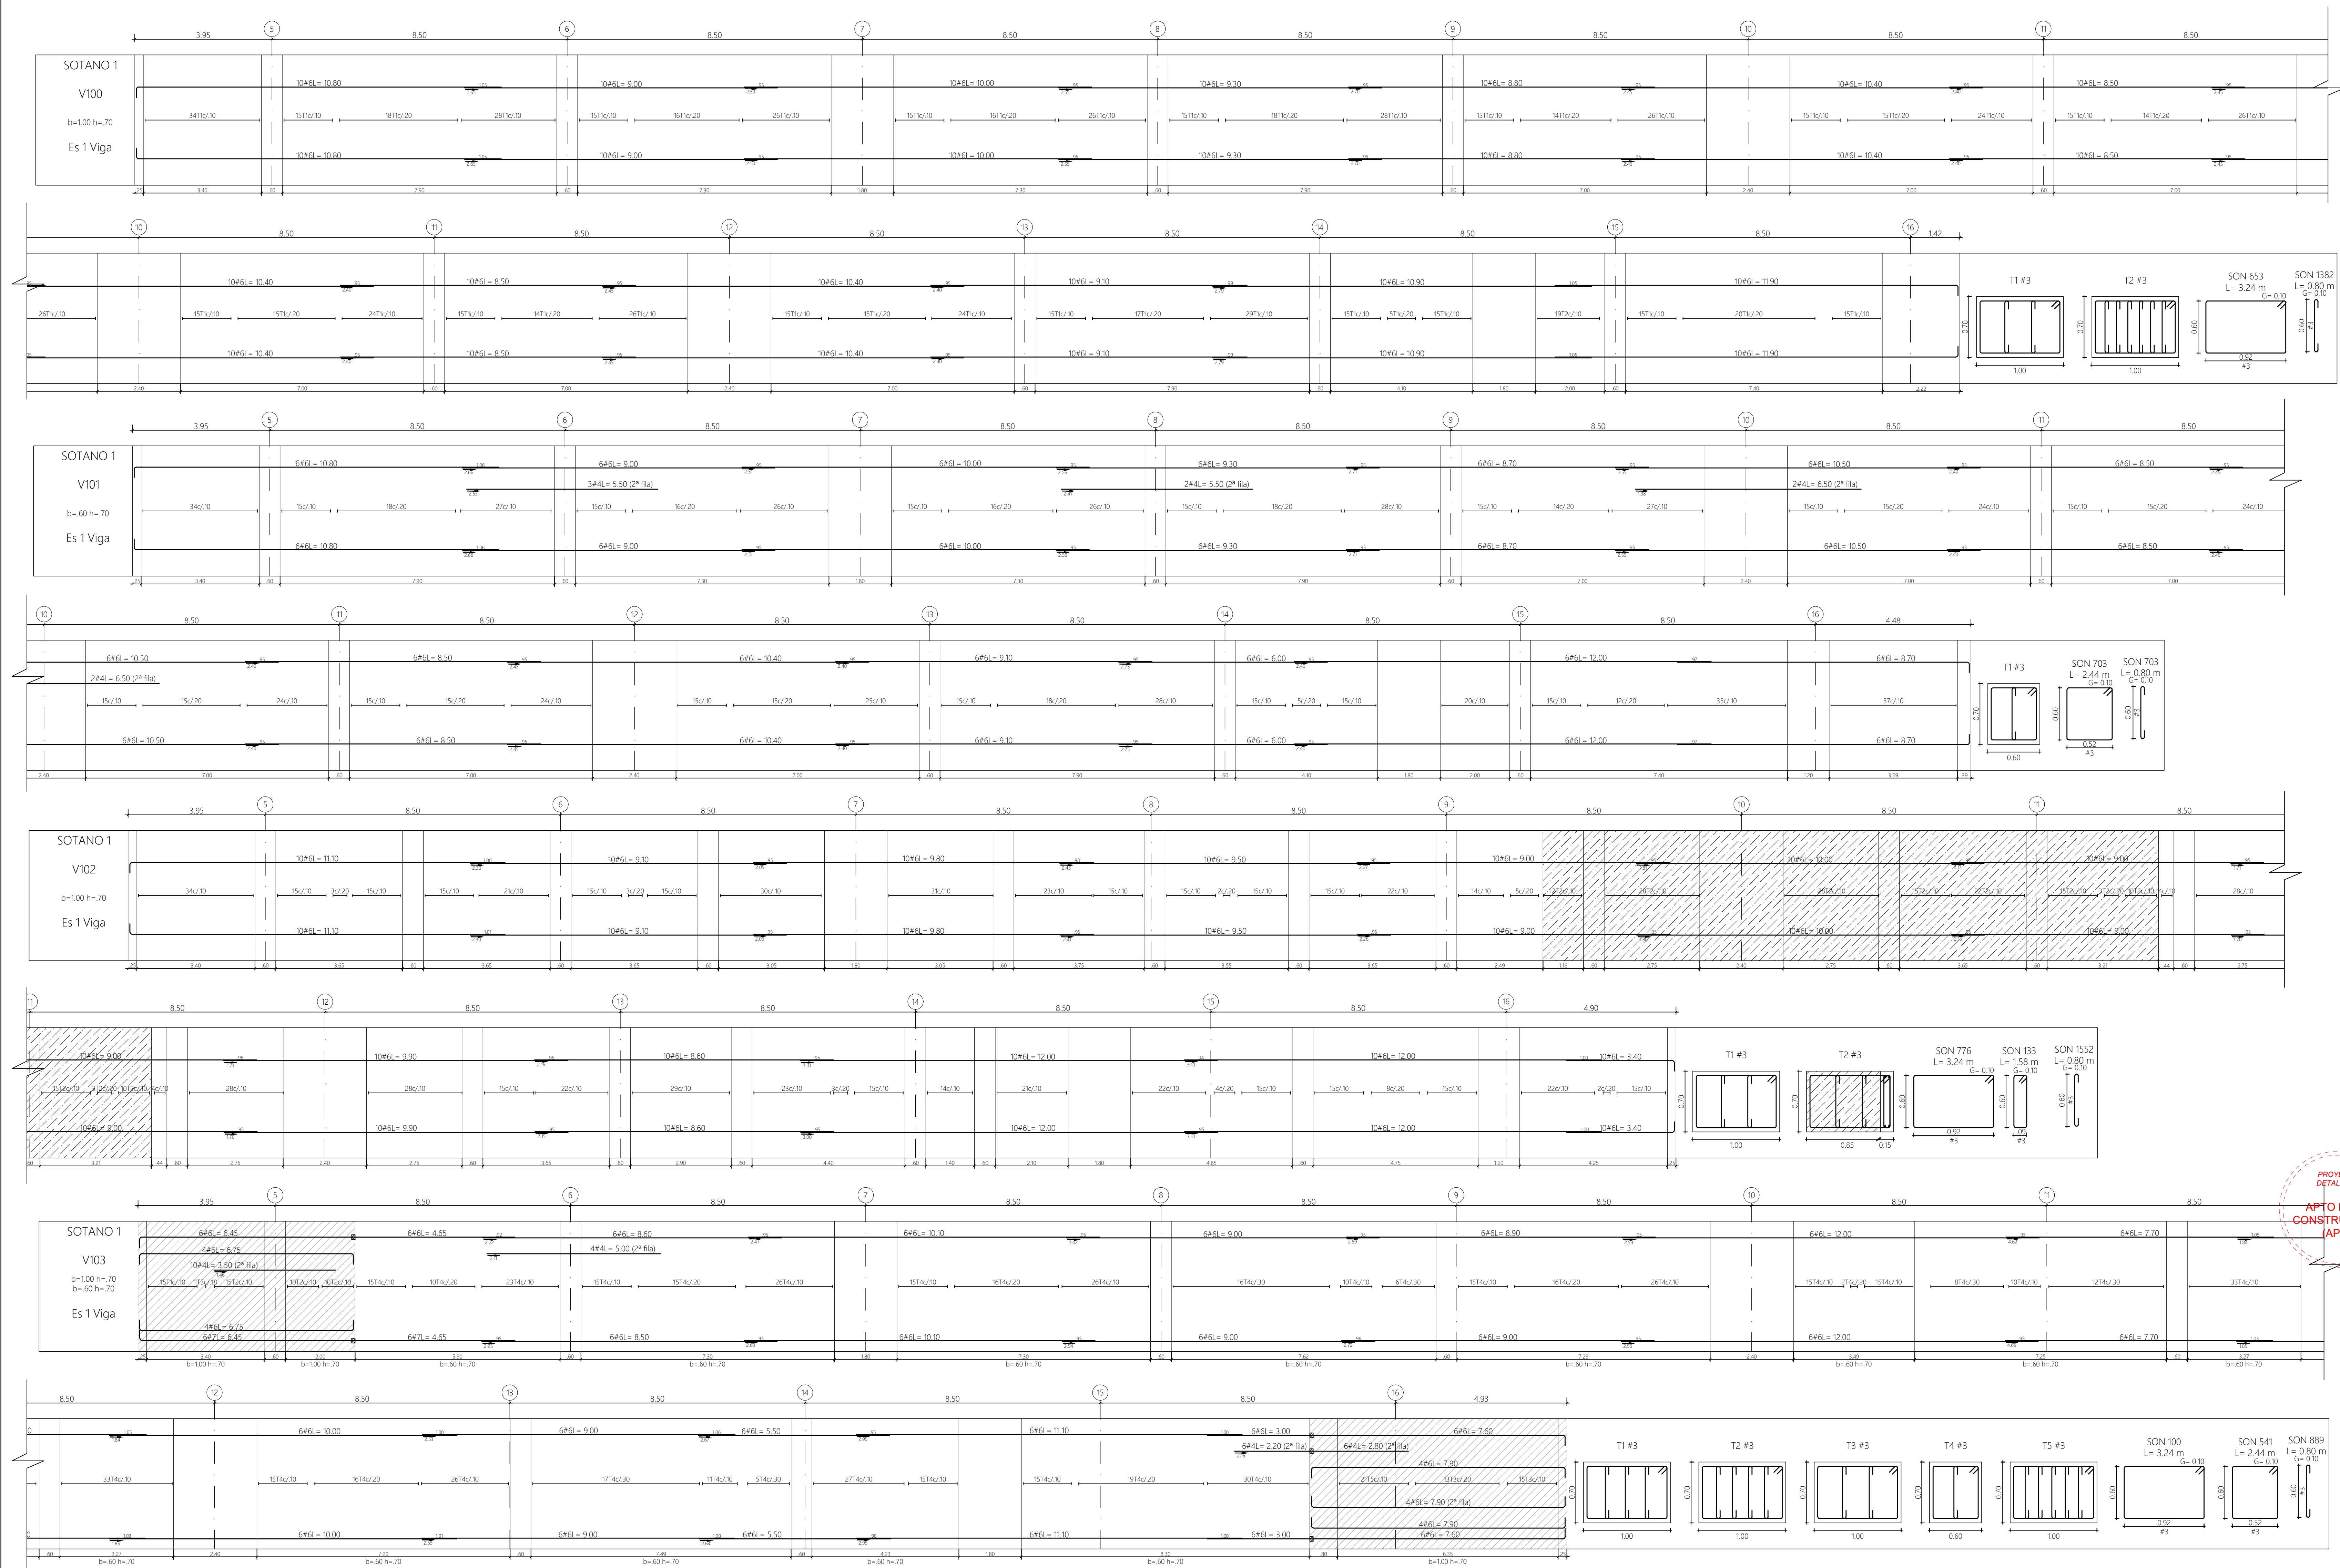

- Indica seccion de viga fundida en Primera Etapa, prever conectores
- Empalme mecánico tipo 2
- Indica zona a demoler

DESPIECE DE VIGAS SÓTANO 1
Escala 1:75
NOTA: Ver esquema de armado base de vigas y viguetas en planos E000

CTIB

Campus de Ciencia, Tecnología e Innovación de Bogotá - Región

corferias

Generadores de Oportunidades y Progreso

Cámara de Comercio de Bogotá

BOGOTÁ

Secretaría Distrital de Desarrollo Económico

ARQUITECTO COORDINADOR

ELEQUIPO MAZZANTI + Gensler

DISEÑO ESTRUCTURAL

CNI

ING. NICOLÁS PARRA GARCÍA

DISEÑADOR

ING. NICOLÁS PARRA GARCÍA
MAT. 22021 148063 QND

INTERVENTORIA

GUTIÉRREZ DÍAZ S.A.S.

SUPERVISOR Y LABORATORIO PROYECTOS DE CONSTRUCCIÓN

Jorge Iván García Mancilla

Director de Interventoría:

Ing. Jorge Iván García Mancilla
Mat. 632021 148063 QND

Versión	Emisión	Descripción
AA	15-06-2023	Ingeniería básica
AB	04-08-2023	Anteproyecto
AC	01-11-2023	Anteproyecto V2 50%
AD	15-12-2023	Anteproyecto V2 100%
DD	13-03-2024	Entrega curaduría
EE	10-05-2024	Proyecto Final 100%
EF	31-05-2024	Respuesta Obs 100%
FF	21-06-2024	Entrega Final
01	28-07-2024	ENTREGA FINAL

PROYECTO:

CAMPUS DE CIENCIA TECNOLOGÍA E INNOVACIÓN DE BOGOTÁ

MAT. No. 500-20252470

FASE

ENTREGA FINAL

PROPÓSITO DE EMISIÓN

Curaduría	☐	Coordinación	☐
Revisión	☐	Construcción	☐
Entrega Cliente	☒		

SONIFICACION

Nivel 24	
Nivel 23	
Nivel 22	
Nivel 21	
Nivel 20	
Nivel 19	
Nivel 18	
Nivel 17	
Nivel 16	
Nivel 15	
Nivel 14	
Nivel 13	
Nivel 12	
Nivel 11	
Nivel 10	
Nivel 9	
Nivel 8	
Nivel 7	
Nivel 6	
Nivel 5	
Nivel 4	
Nivel 3	
Nivel 2	
Nivel 1	
Nivel B1	
Nivel B2	

KEY PLAN

Fecha: 28-07-2024

Escala: As Indicated

DESPIECES DE VIGAS SOTANO 1

CTIB_CNI_EST_410_DSP_XXX_01

PROYECTO DETALLADO

APTO PARA CONSTRUCCION (APC)