
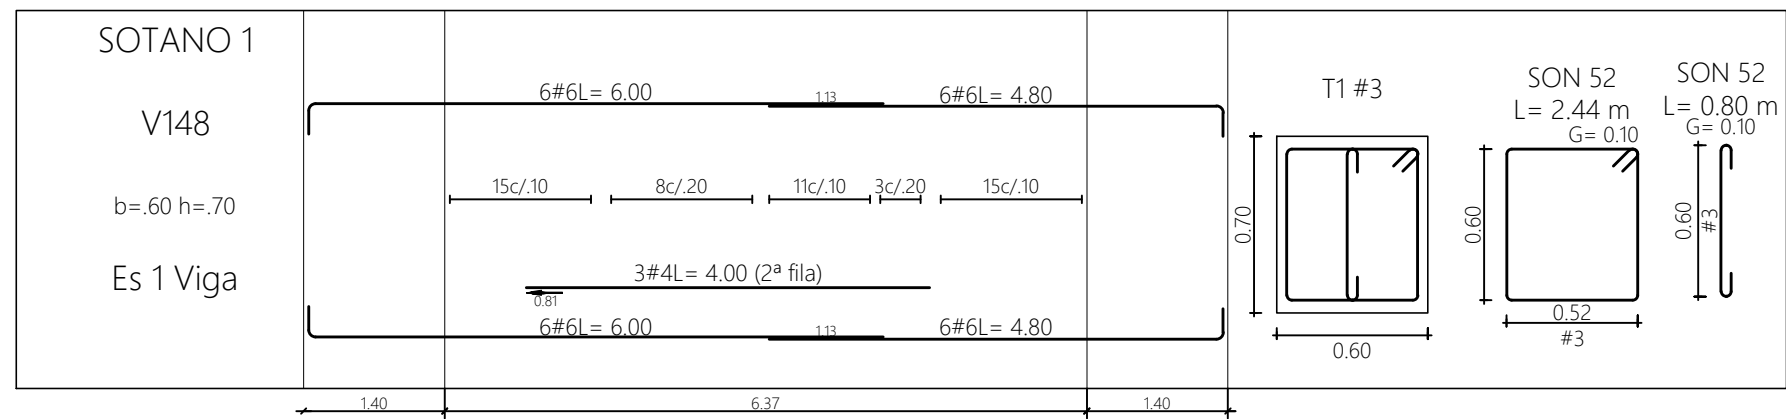
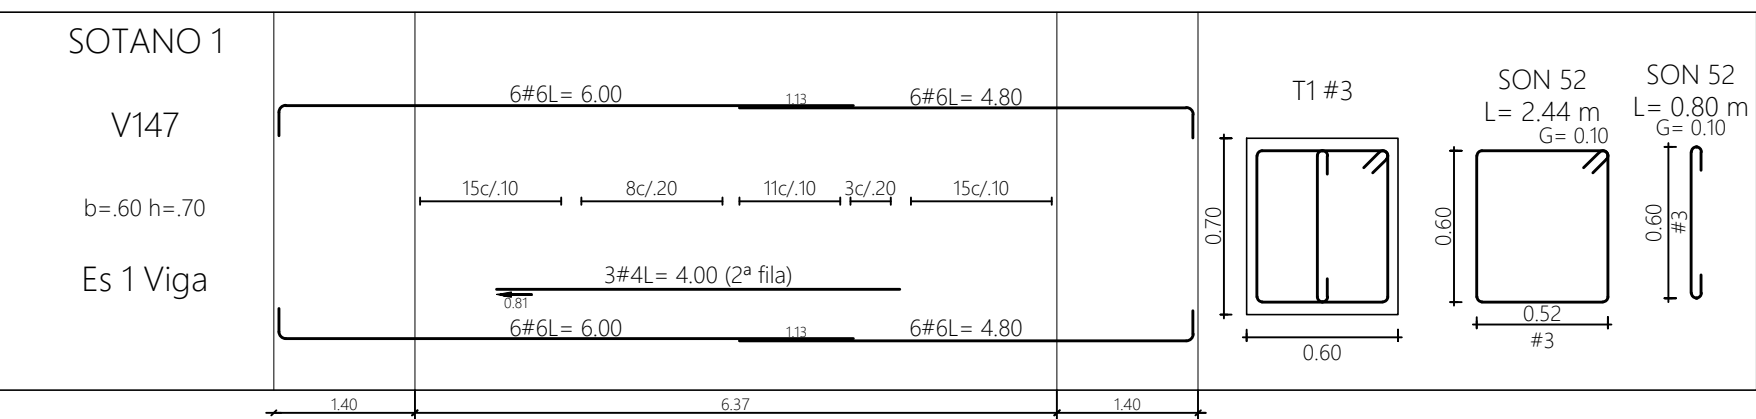
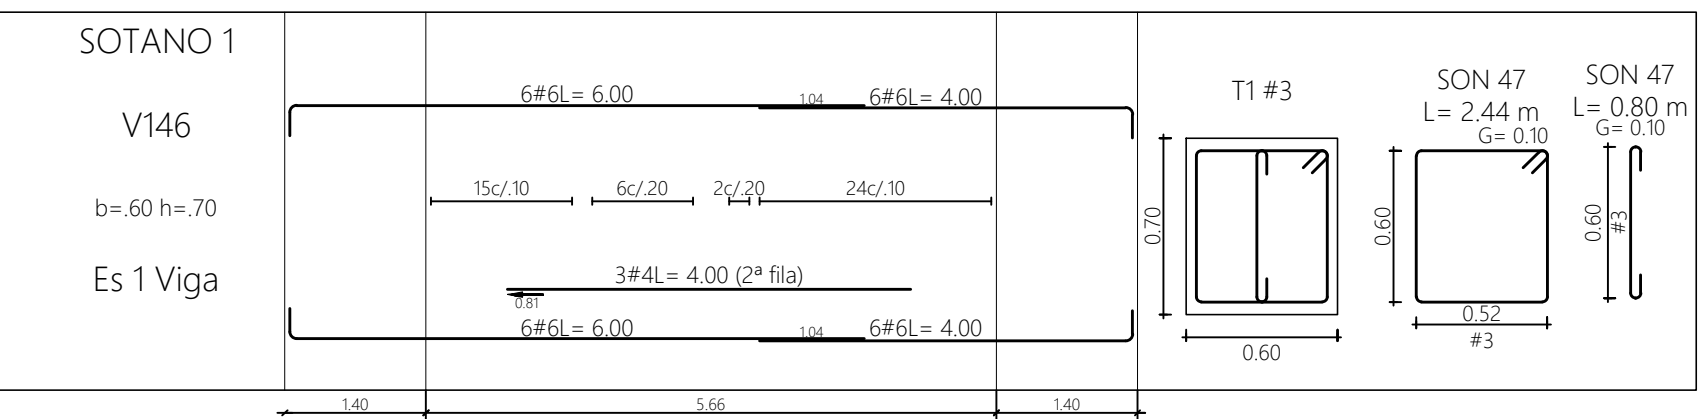
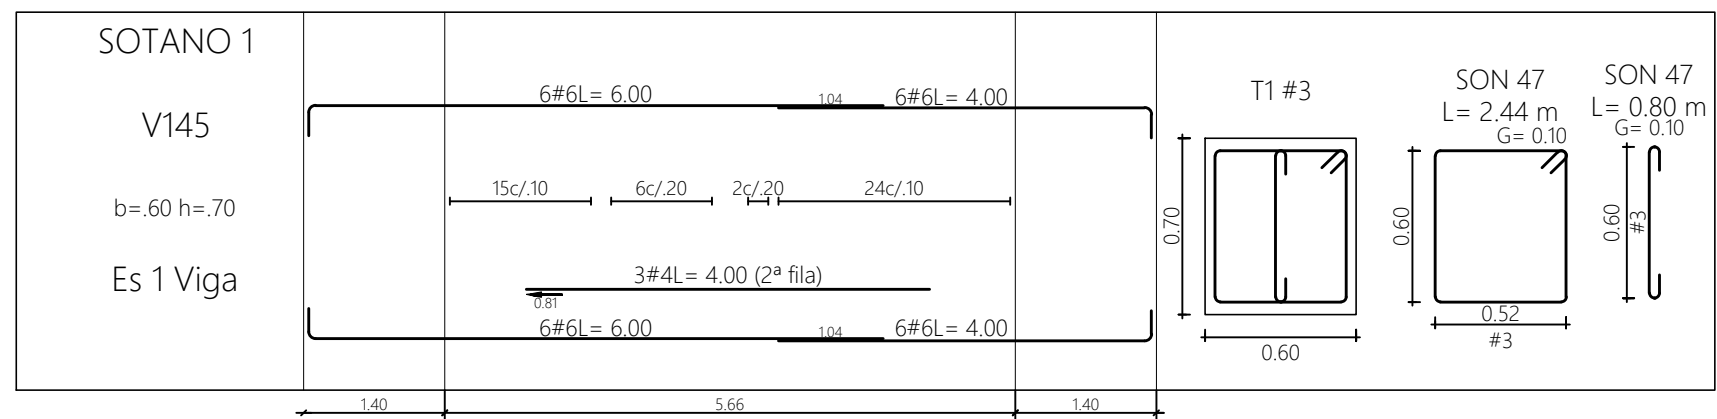
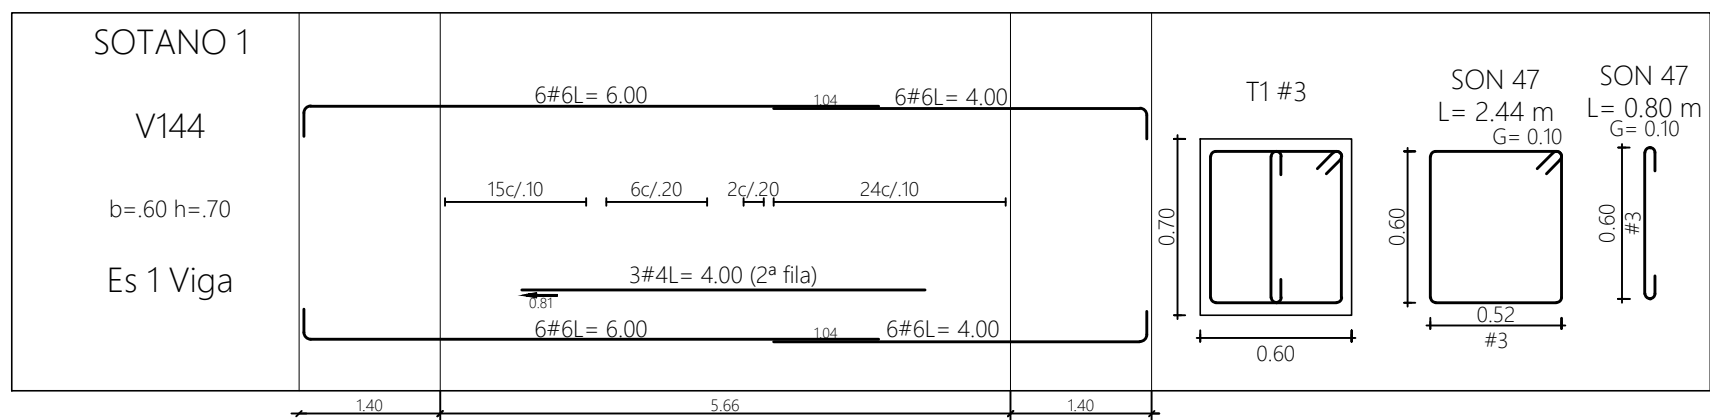
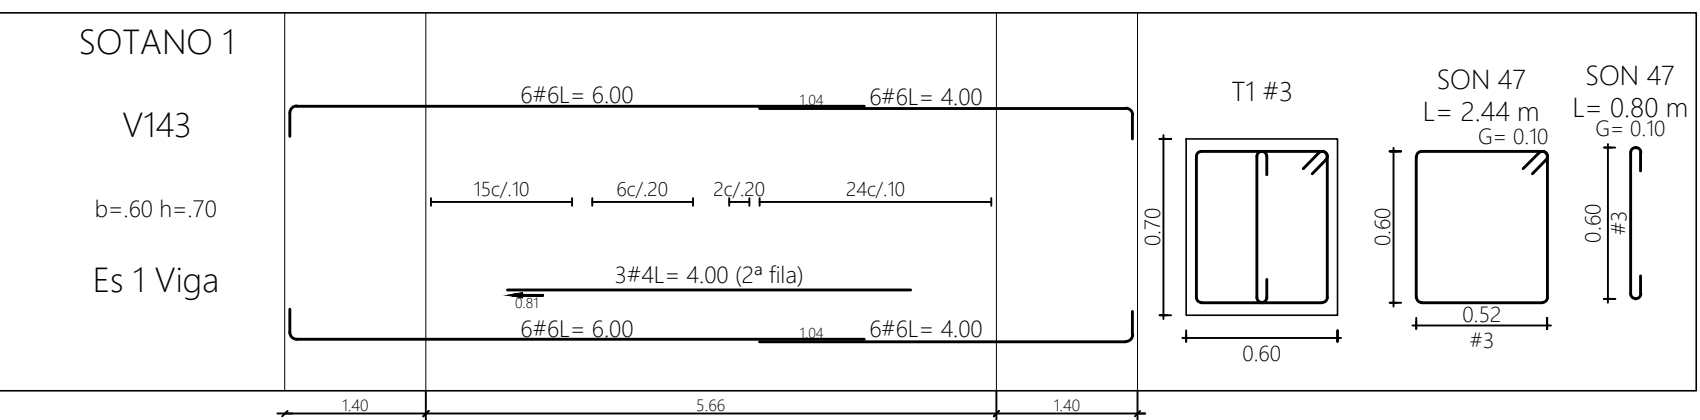
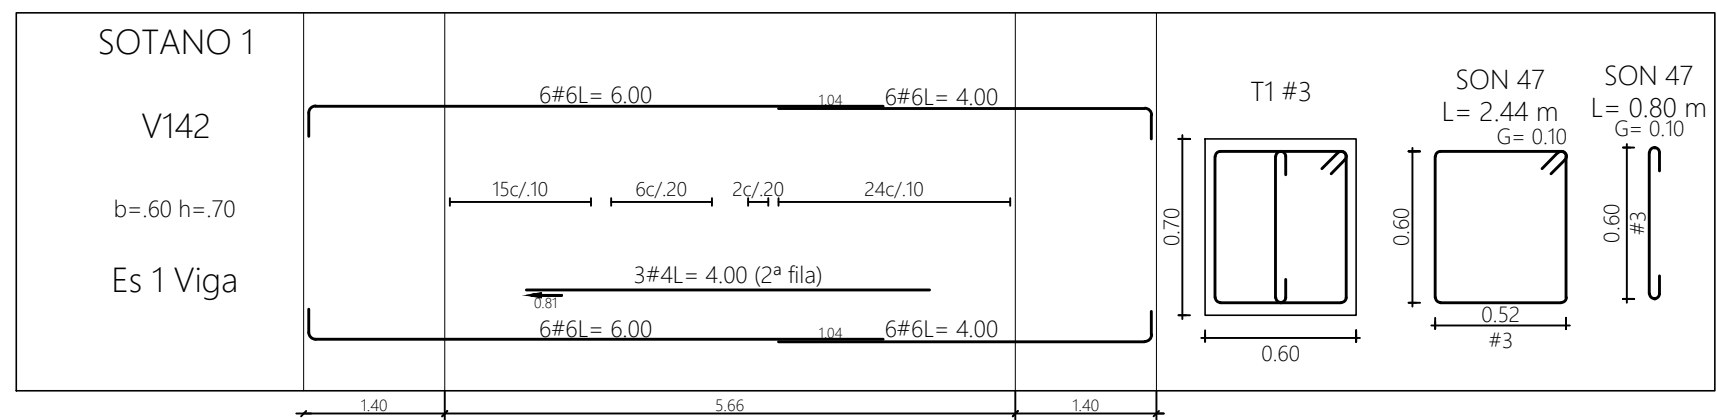
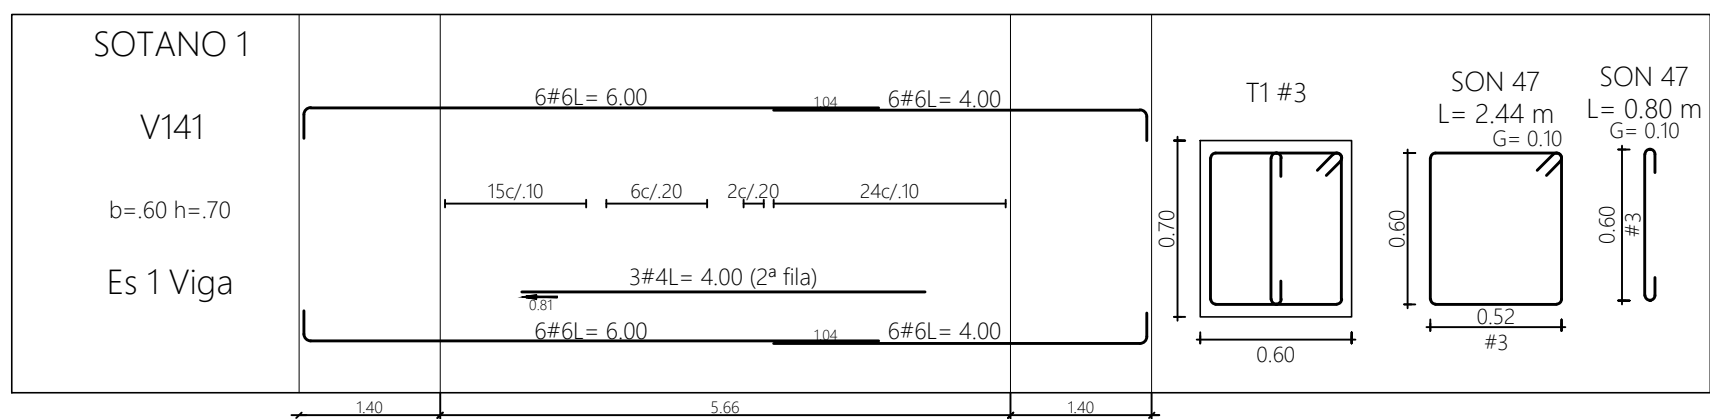
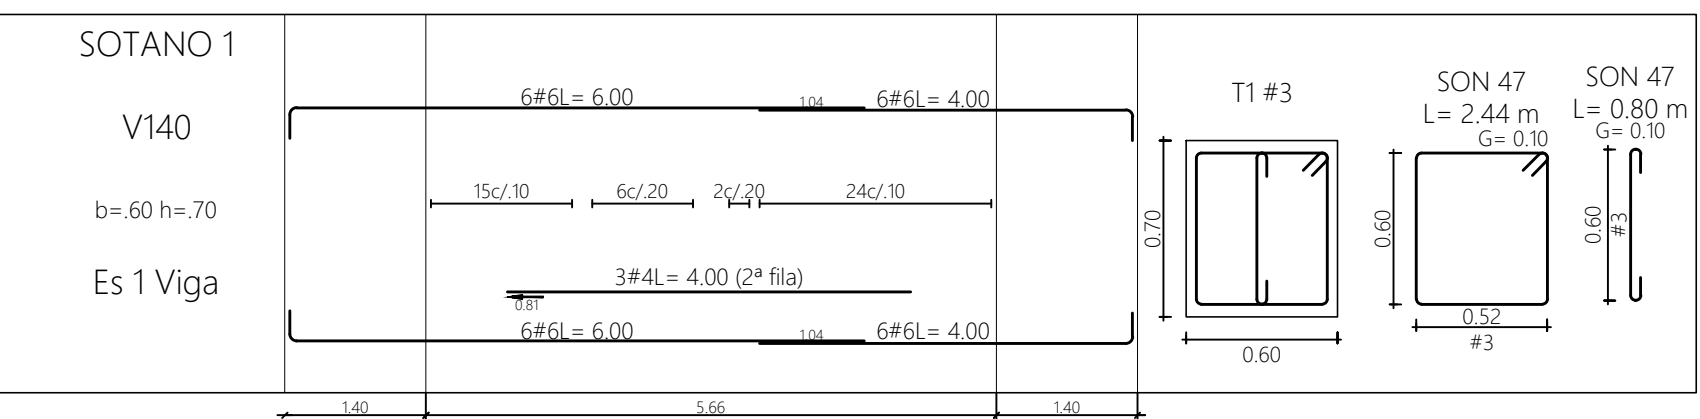
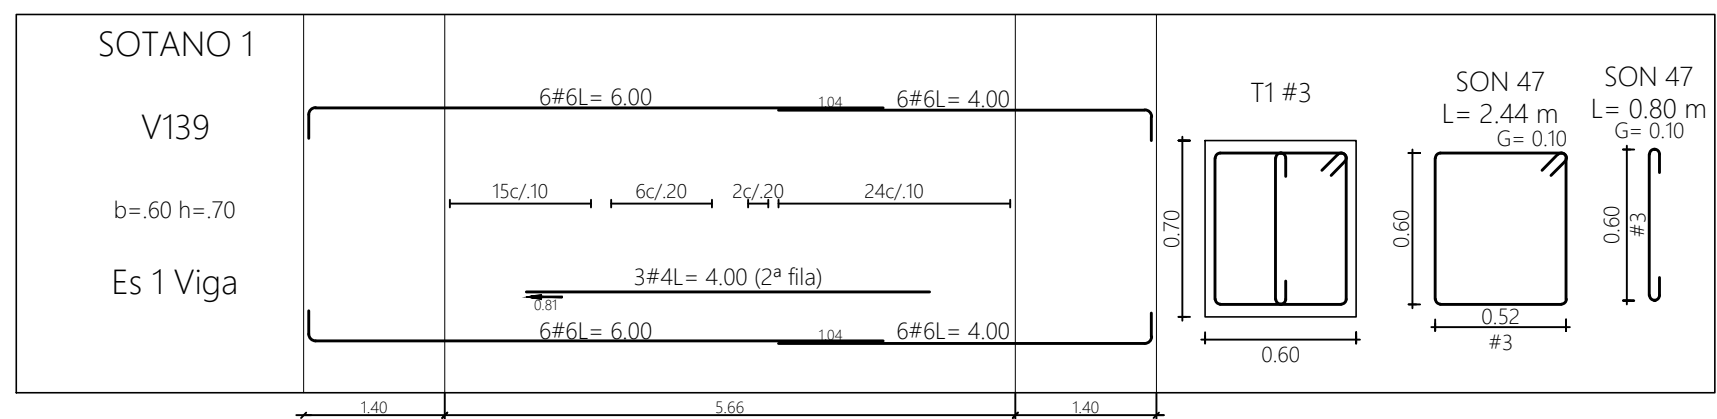
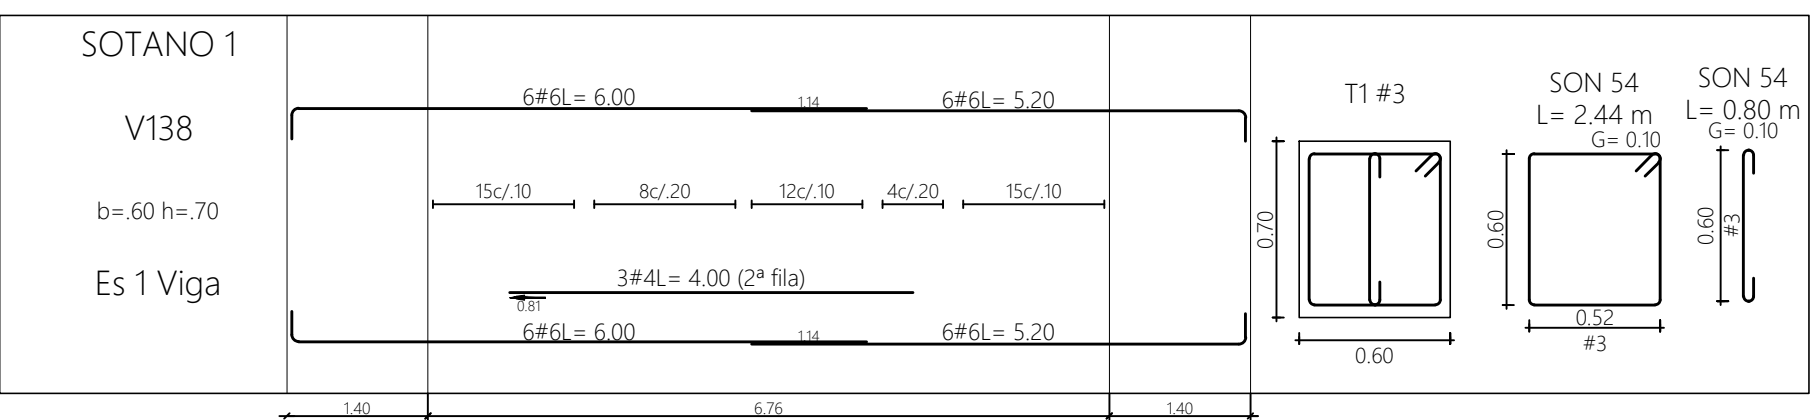
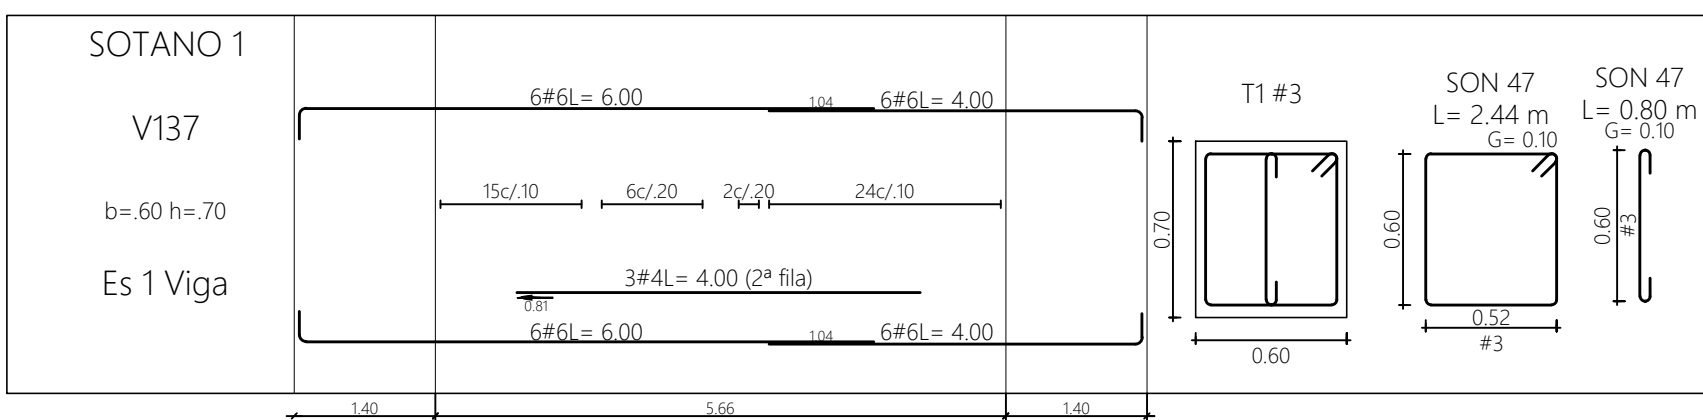


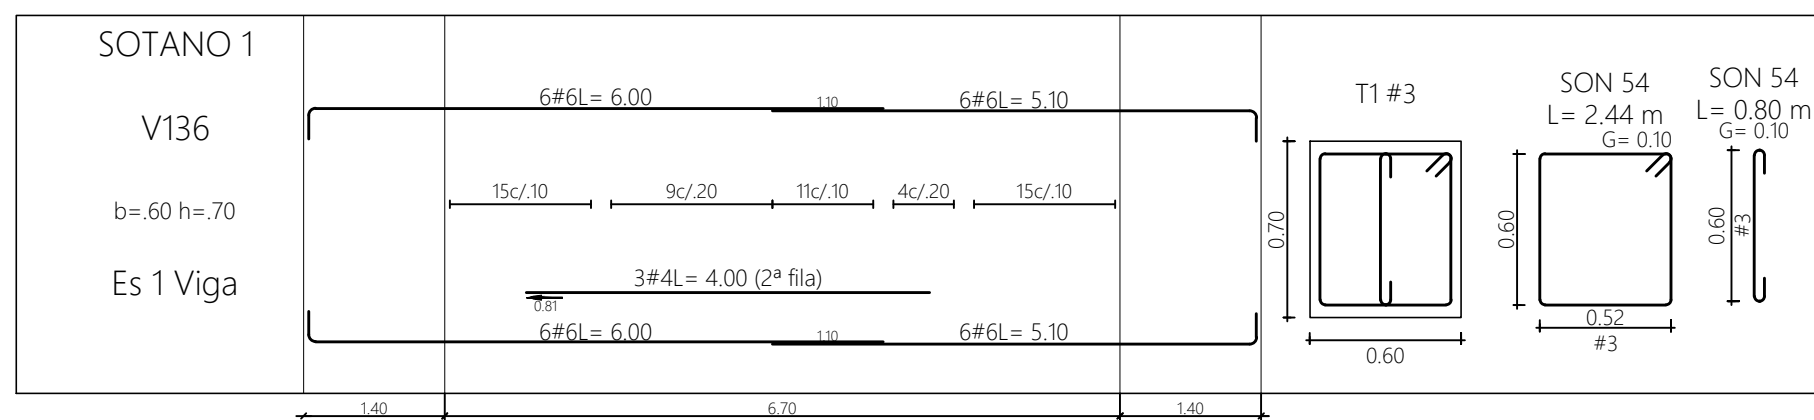

DESPIECE DE VIGAS SÓTANO 1
Escala 1:75

Versión	Emisión	Descripción
AA	15-06-2023	Ingeniería básica
AB	04-06-2023	Anteproyecto
AC	01-11-2023	Anteproyecto V2 50%
AD	15-12-2023	Anteproyecto V2 100%
DD	13-03-2024	Entrega curaduría
EE	10-05-2024	Proyecto Final 100%
EE	31-05-2024	Respuesta Obis 100%
FF	21-06-2024	Entrega Final
01	26-07-2024	ENTREGA FINAL