


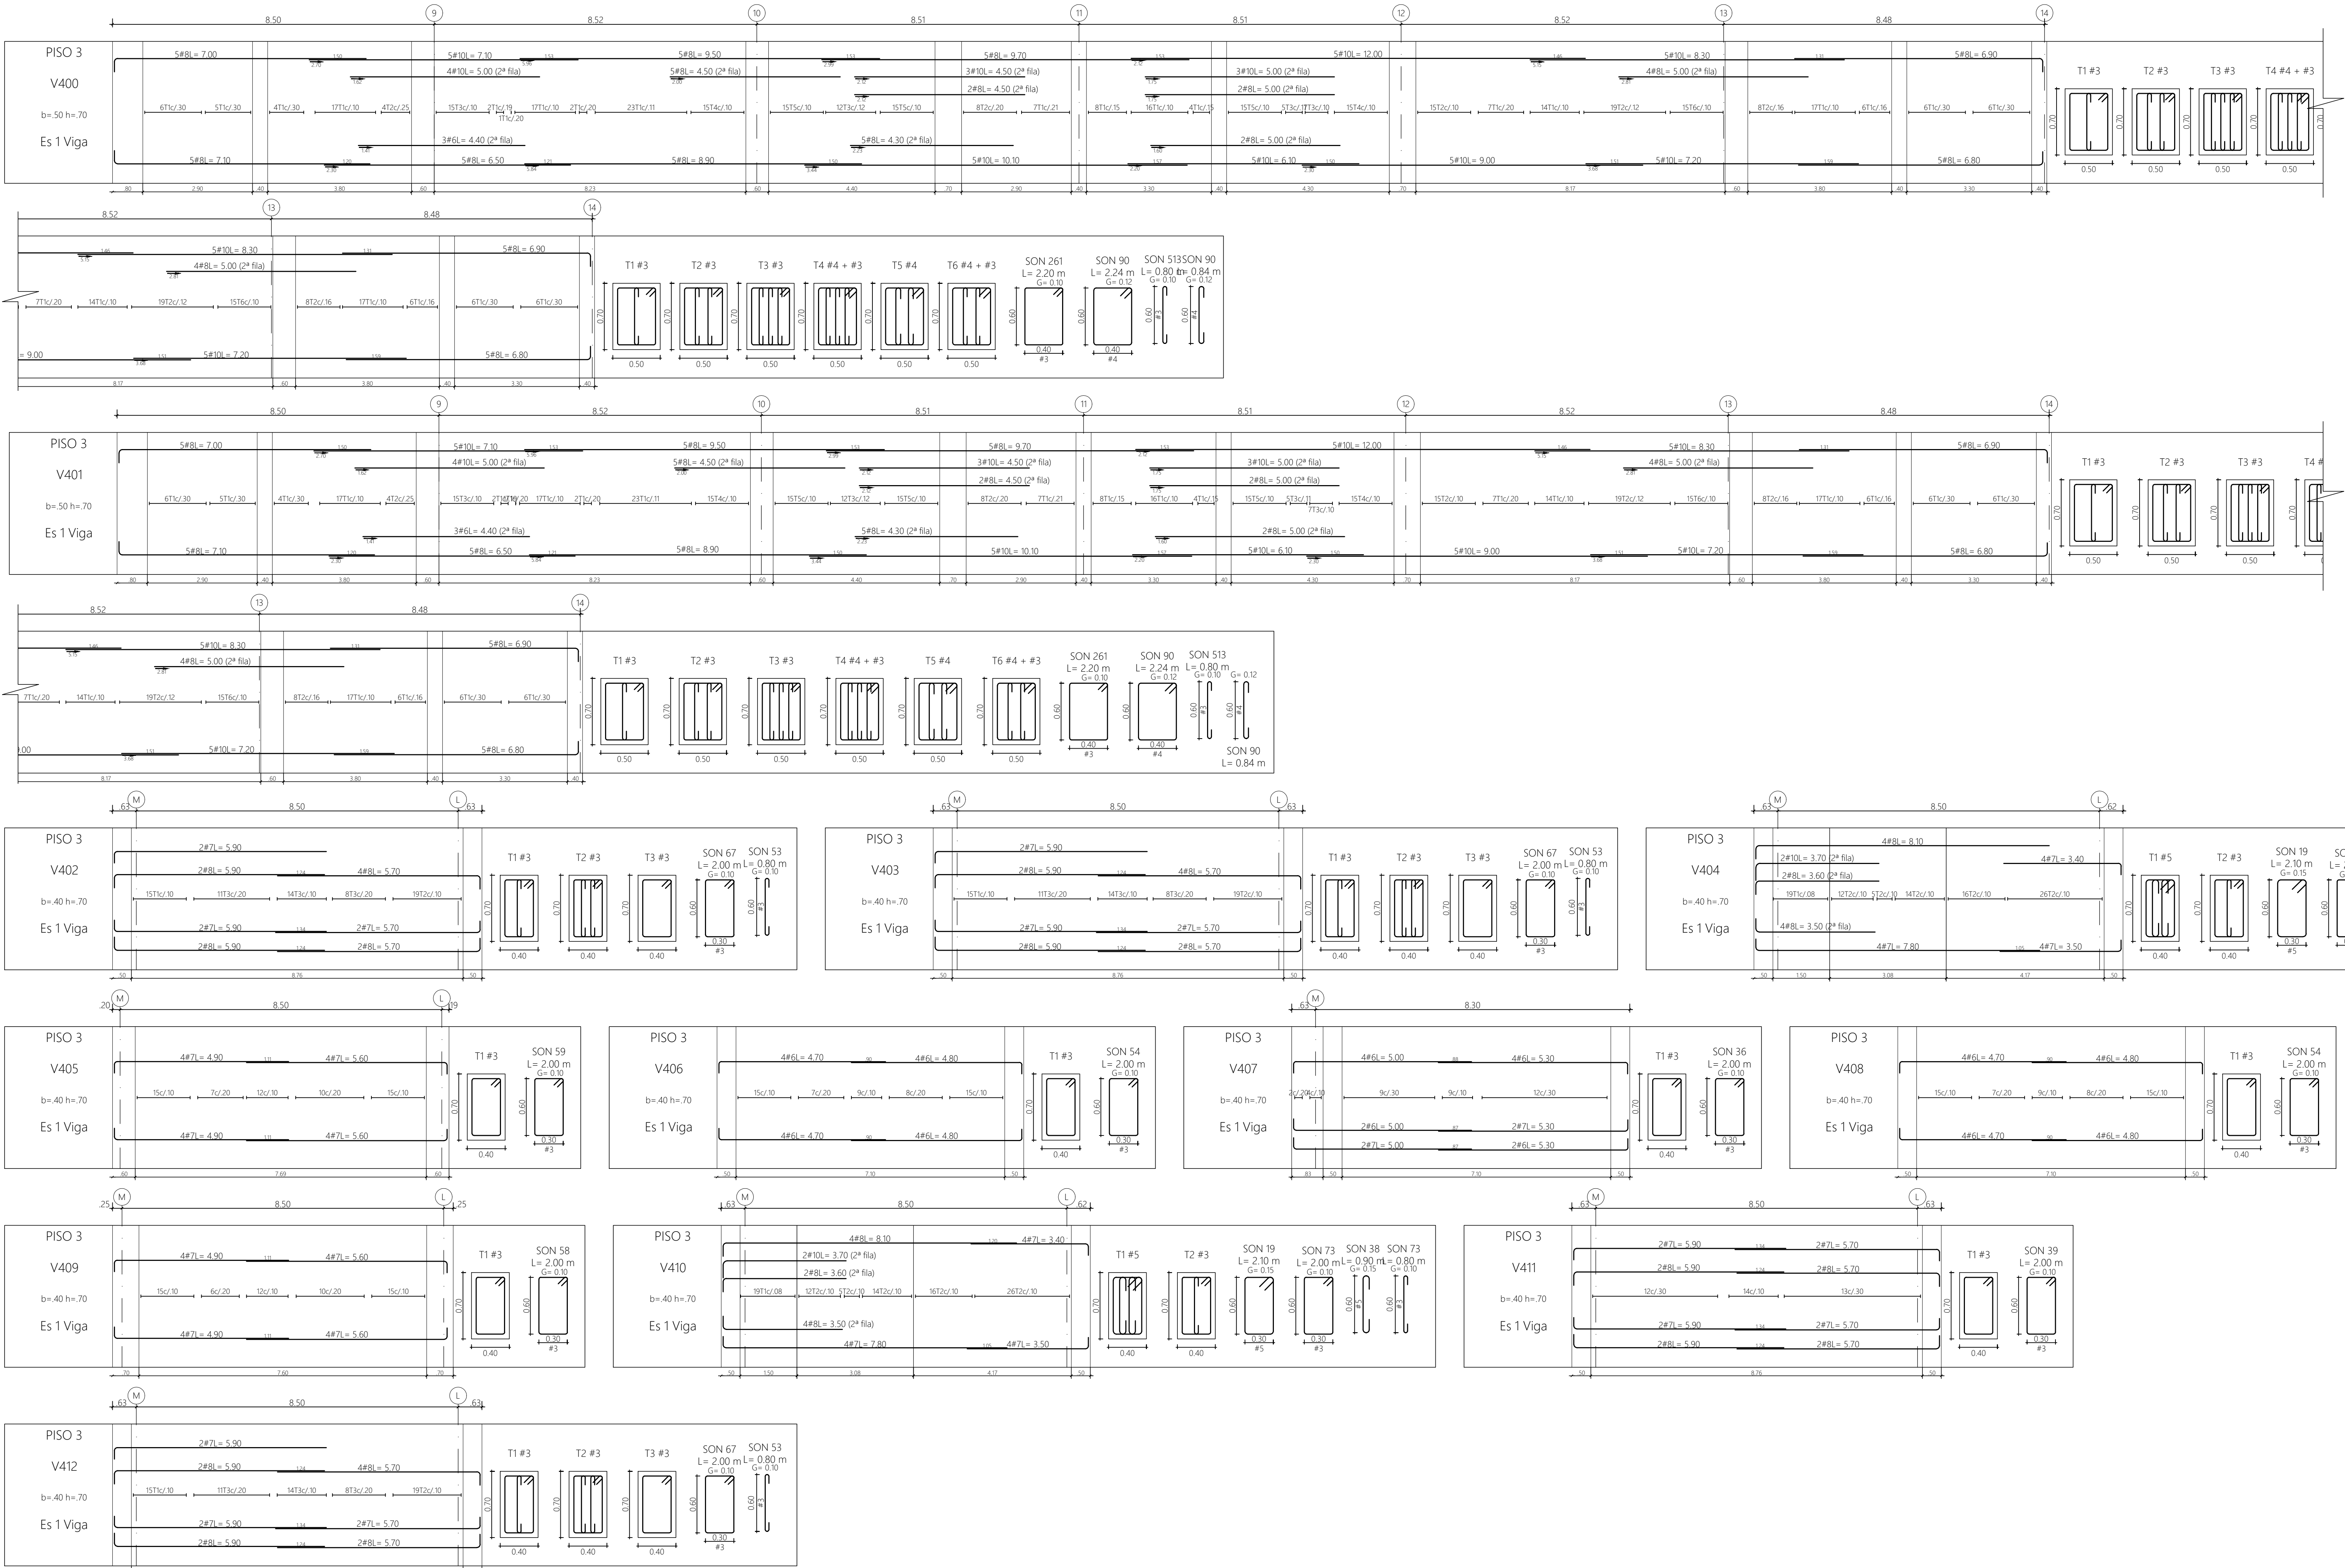

DESPIECES DE VIGAS DE PISO 3
escala 1:75

ARQUITECTO COORDINADOR

ELEQUIPO
MAZZANTI + Gensler

DISÑO ESTRUCTURAL



DISEÑADOR

ING. NICOLÁS PARRA GARCÍA
MAT. 63021-14893 CND

INTERVENTORÍA



Director de Interventoría:

Ing. Jorge Iván García Mancilla
Mat. 63021-14893 CND

Versión

Emisión

Descripción

AA 15-06-2023 Ingeniería básica

AB 04-08-2023 Anteproyecto

AC 01-11-2023 Anteproyecto V2 50%

AD 15-12-2023 Anteproyecto V2 100%

DD 13-03-2024 Entrega curaduría

EE 10-05-2024 Proyecto Final 100%

EF 31-05-2024 Respuesta Obs 100%

FF 21-06-2024 Entrega Final

01 28-07-2024 ENTREGA FINAL

PROYECTO:

CAMPUS DE CIENCIA TECNOLOGÍA E
INNOVACIÓN DE BOGOTÁ

MAT. No. SIC-2023470

FASE

ENTREGA FINAL

PROPOSITO DE EMISIÓN

Curaduría ☐ Coordinación ☐


Revisión ☐ Construcción ☒

Entrega Cliente ☐

ZONIFICACIÓN

Nivel 24
Nivel 23
Nivel 22
Nivel 21
Nivel 20
Nivel 19
Nivel 18
Nivel 17
Nivel 16
Nivel 15
Nivel 14
Nivel 13
Nivel 12
Nivel 11
Nivel 10
Nivel 9
Nivel 8
Nivel 7
Nivel 6
Nivel 5
Nivel 4
Nivel 3
Nivel 2
Nivel 1
Nivel B1
Nivel B2

KEY PLAN

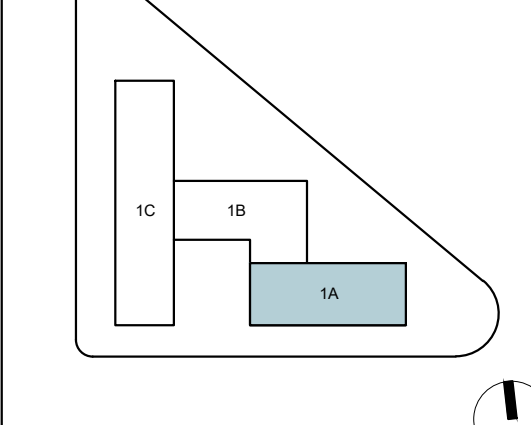

Fecha:

26-07-2024

Escala:

As indicated

DESPIECES DE
VIGAS DE PISO 3

CTIB_CNI_Ext_423_DSP_XXX_01