


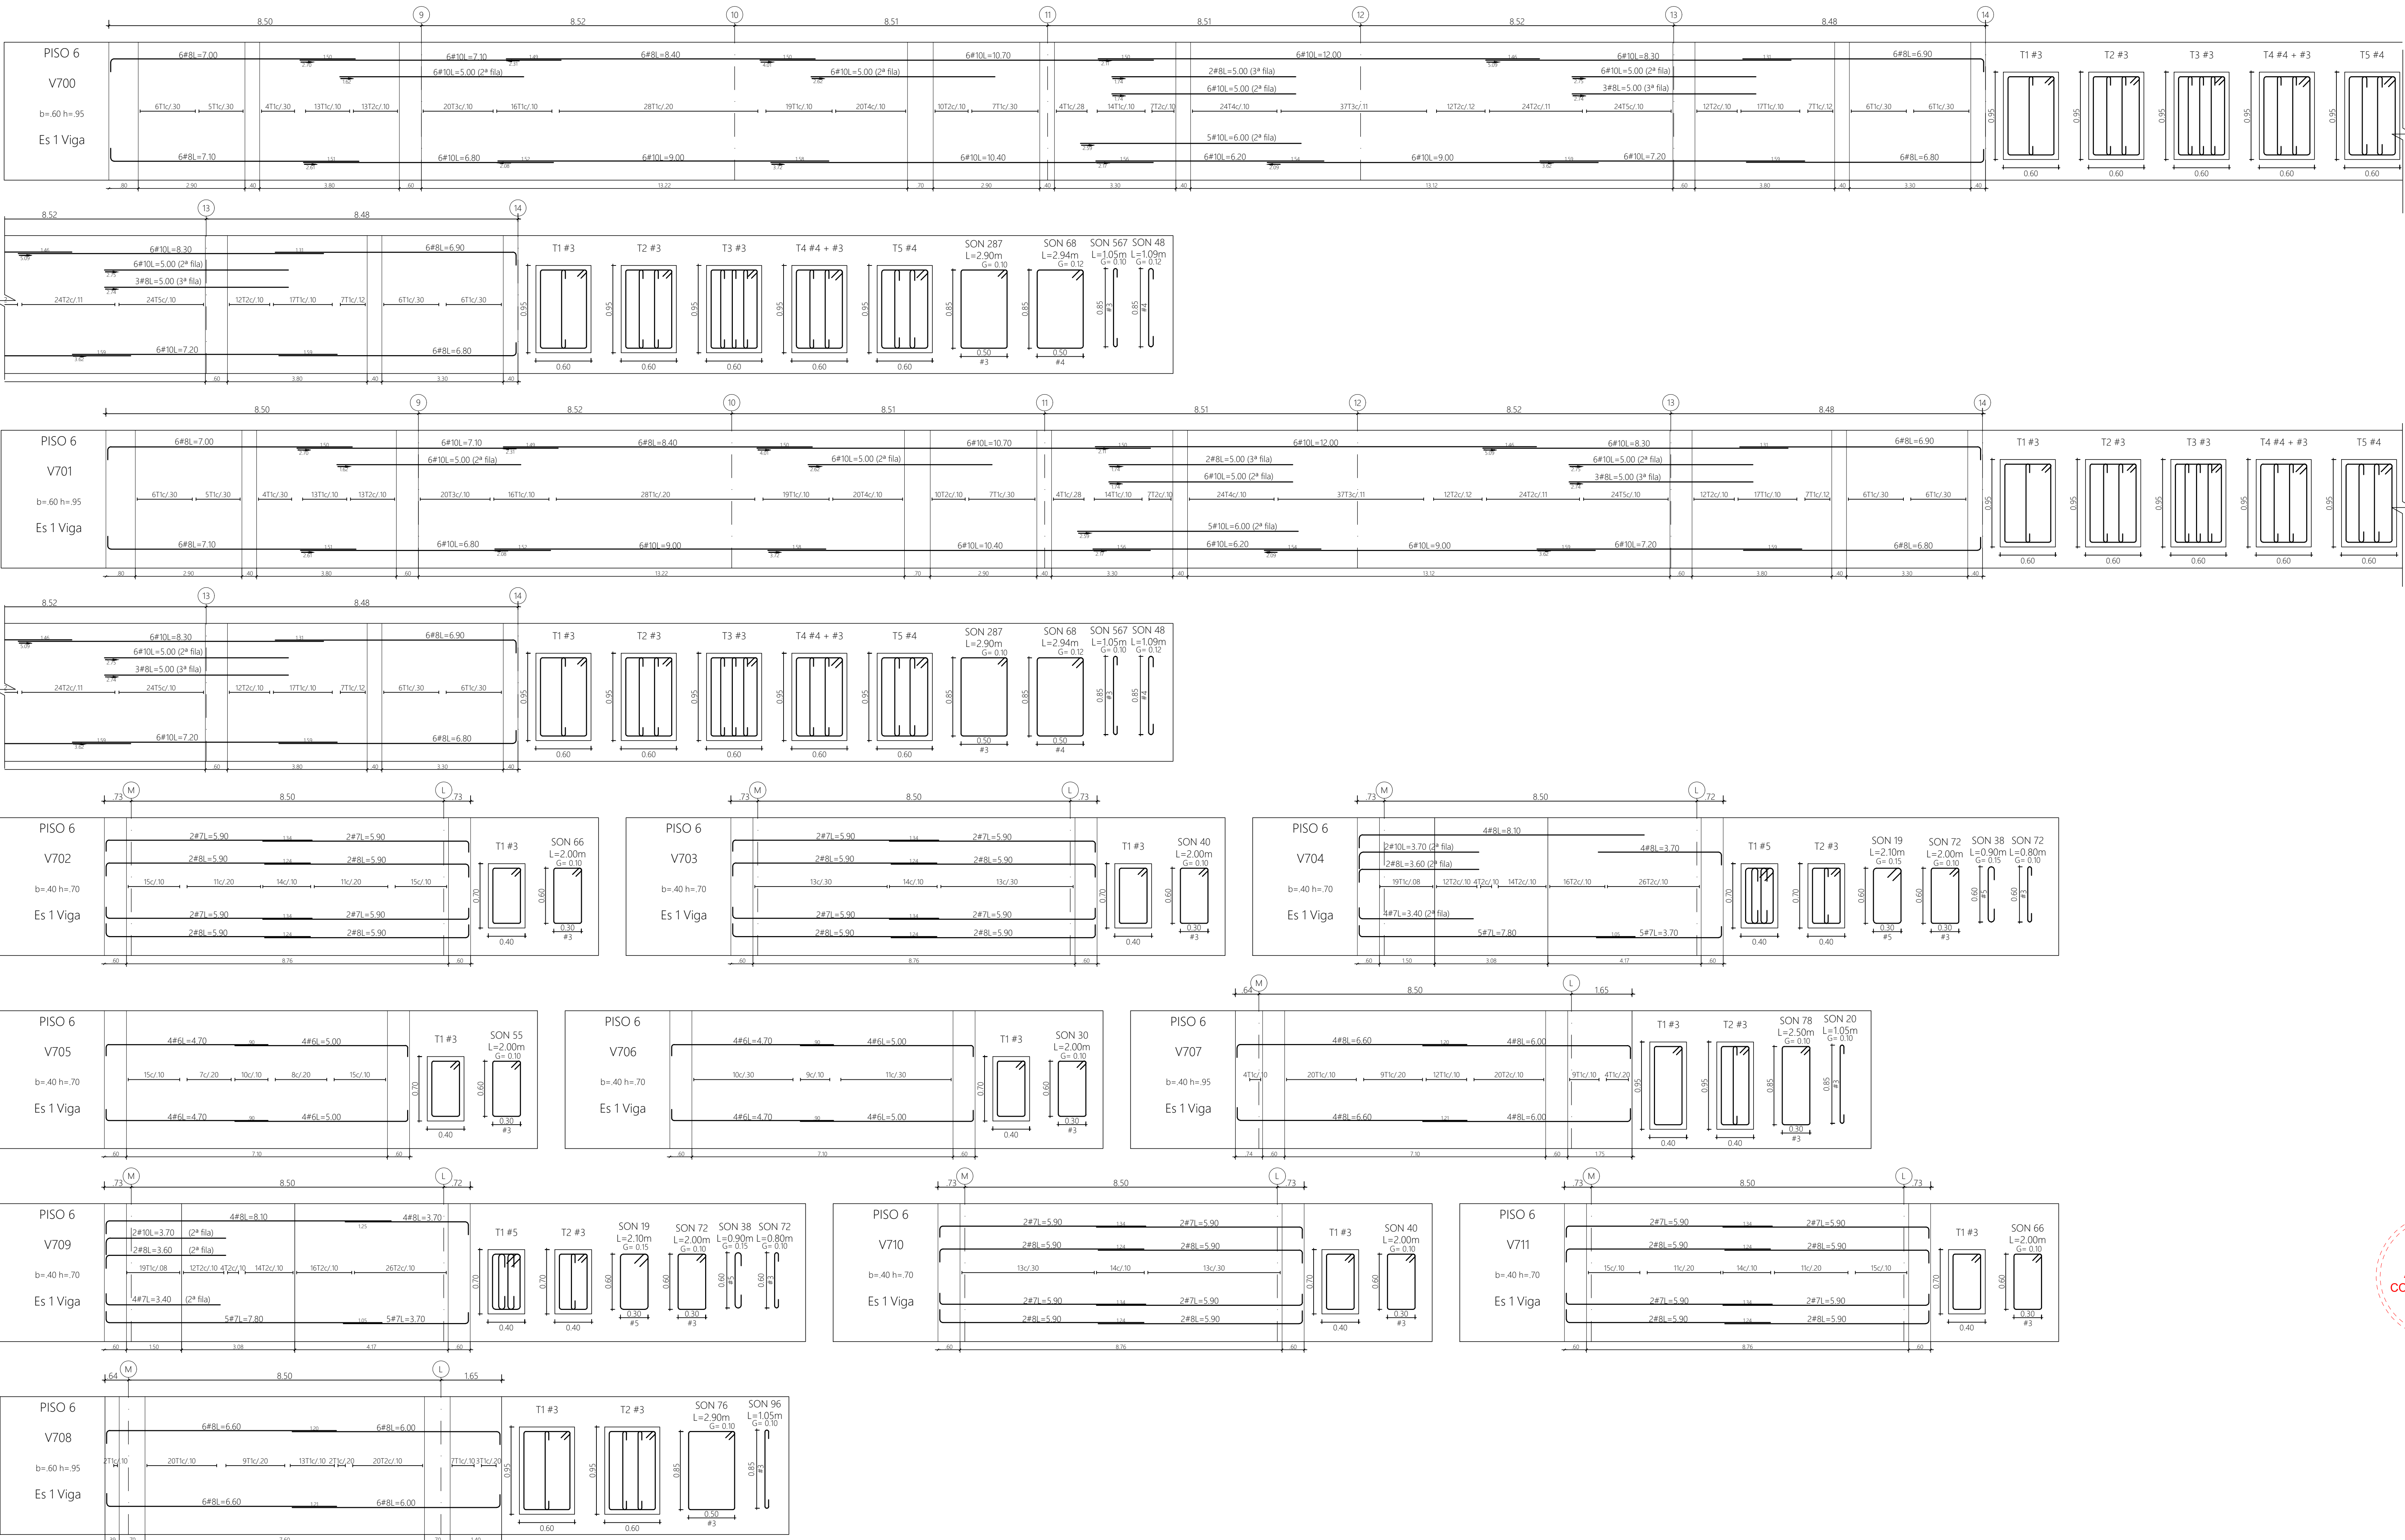

DESPIECES DE VIGAS DE PISO 6
escala 1:75

CTIB

Campus de Ciencia, Tecnología e Innovación de Bogotá - Región

corferias

Generadores de Oportunidades y Progreso

Cámara de Comercio de Bogotá

BOGOTÁ

Secretaría Distrital de Desarrollo Económico

ARQUITECTO COORDINADOR

ELEQUIPO MAZZANTI + Gensler

DISÑO ESTRUCTURAL

CNI

CONSTRUCCIÓN

ING. NICOLÁS PARRA GARCÍA

MAT. 232021 62063 CND

INTERVENTORIA

GUTIERREZ DÍAZ S.A.S.

SUPERVISIÓN Y LABORATORIO PROYECTOS DE CONSTRUCCIÓN

Director de Interventoría:

Ing. Jorge Iván García Mancilla

MAT. 632021 148063 QND

Versión	Emisión	Descripción
AA	15-06-2023	Ingeniería básica
AB	04-08-2023	Anteproyecto
AC	01-11-2023	Anteproyecto V2 50%
AD	15-12-2023	Anteproyecto V2 100%
DD	13-03-2024	Entrega curaduría
EE	10-05-2024	Proyecto Final 100%
FF	31-05-2024	Respuesta Obs 100%
FF	21-06-2024	Entrega Final
01	28-07-2024	ENTREGA FINAL

PROYECTO:

CAMPUS DE CIENCIA TECNOLOGÍA E INNOVACIÓN DE BOGOTÁ

MAT. No. 500-00252470

FASE

ENTREGA FINAL

PROPÓSITO DE EMISIÓN

Curaduría

Revisión

Entrega Cliente

☐

☐

☒

Coordinación

Construcción

☐

☒

ZONIFICACIÓN

Nivel 24
Nivel 23
Nivel 22
Nivel 21
Nivel 20
Nivel 19
Nivel 18
Nivel 17
Nivel 16
Nivel 15
Nivel 14
Nivel 13
Nivel 12
Nivel 11
Nivel 10
Nivel 9
Nivel 8
Nivel 7
Nivel 6
Nivel 5
Nivel 4
Nivel 3
Nivel 2
Nivel 1
Nivel 01
Nivel 02

KEY PLAN

1C

1B

1A

Fecha:

26-07-2024

Escala:

As Indicated

DESPIECES DE VIGAS DE PISO 6

CTIB_CNI_EST_426_DSP_XXX_01

PROYECTO DETALLADO
APTO PARA CONSTRUCCIÓN (APC)