


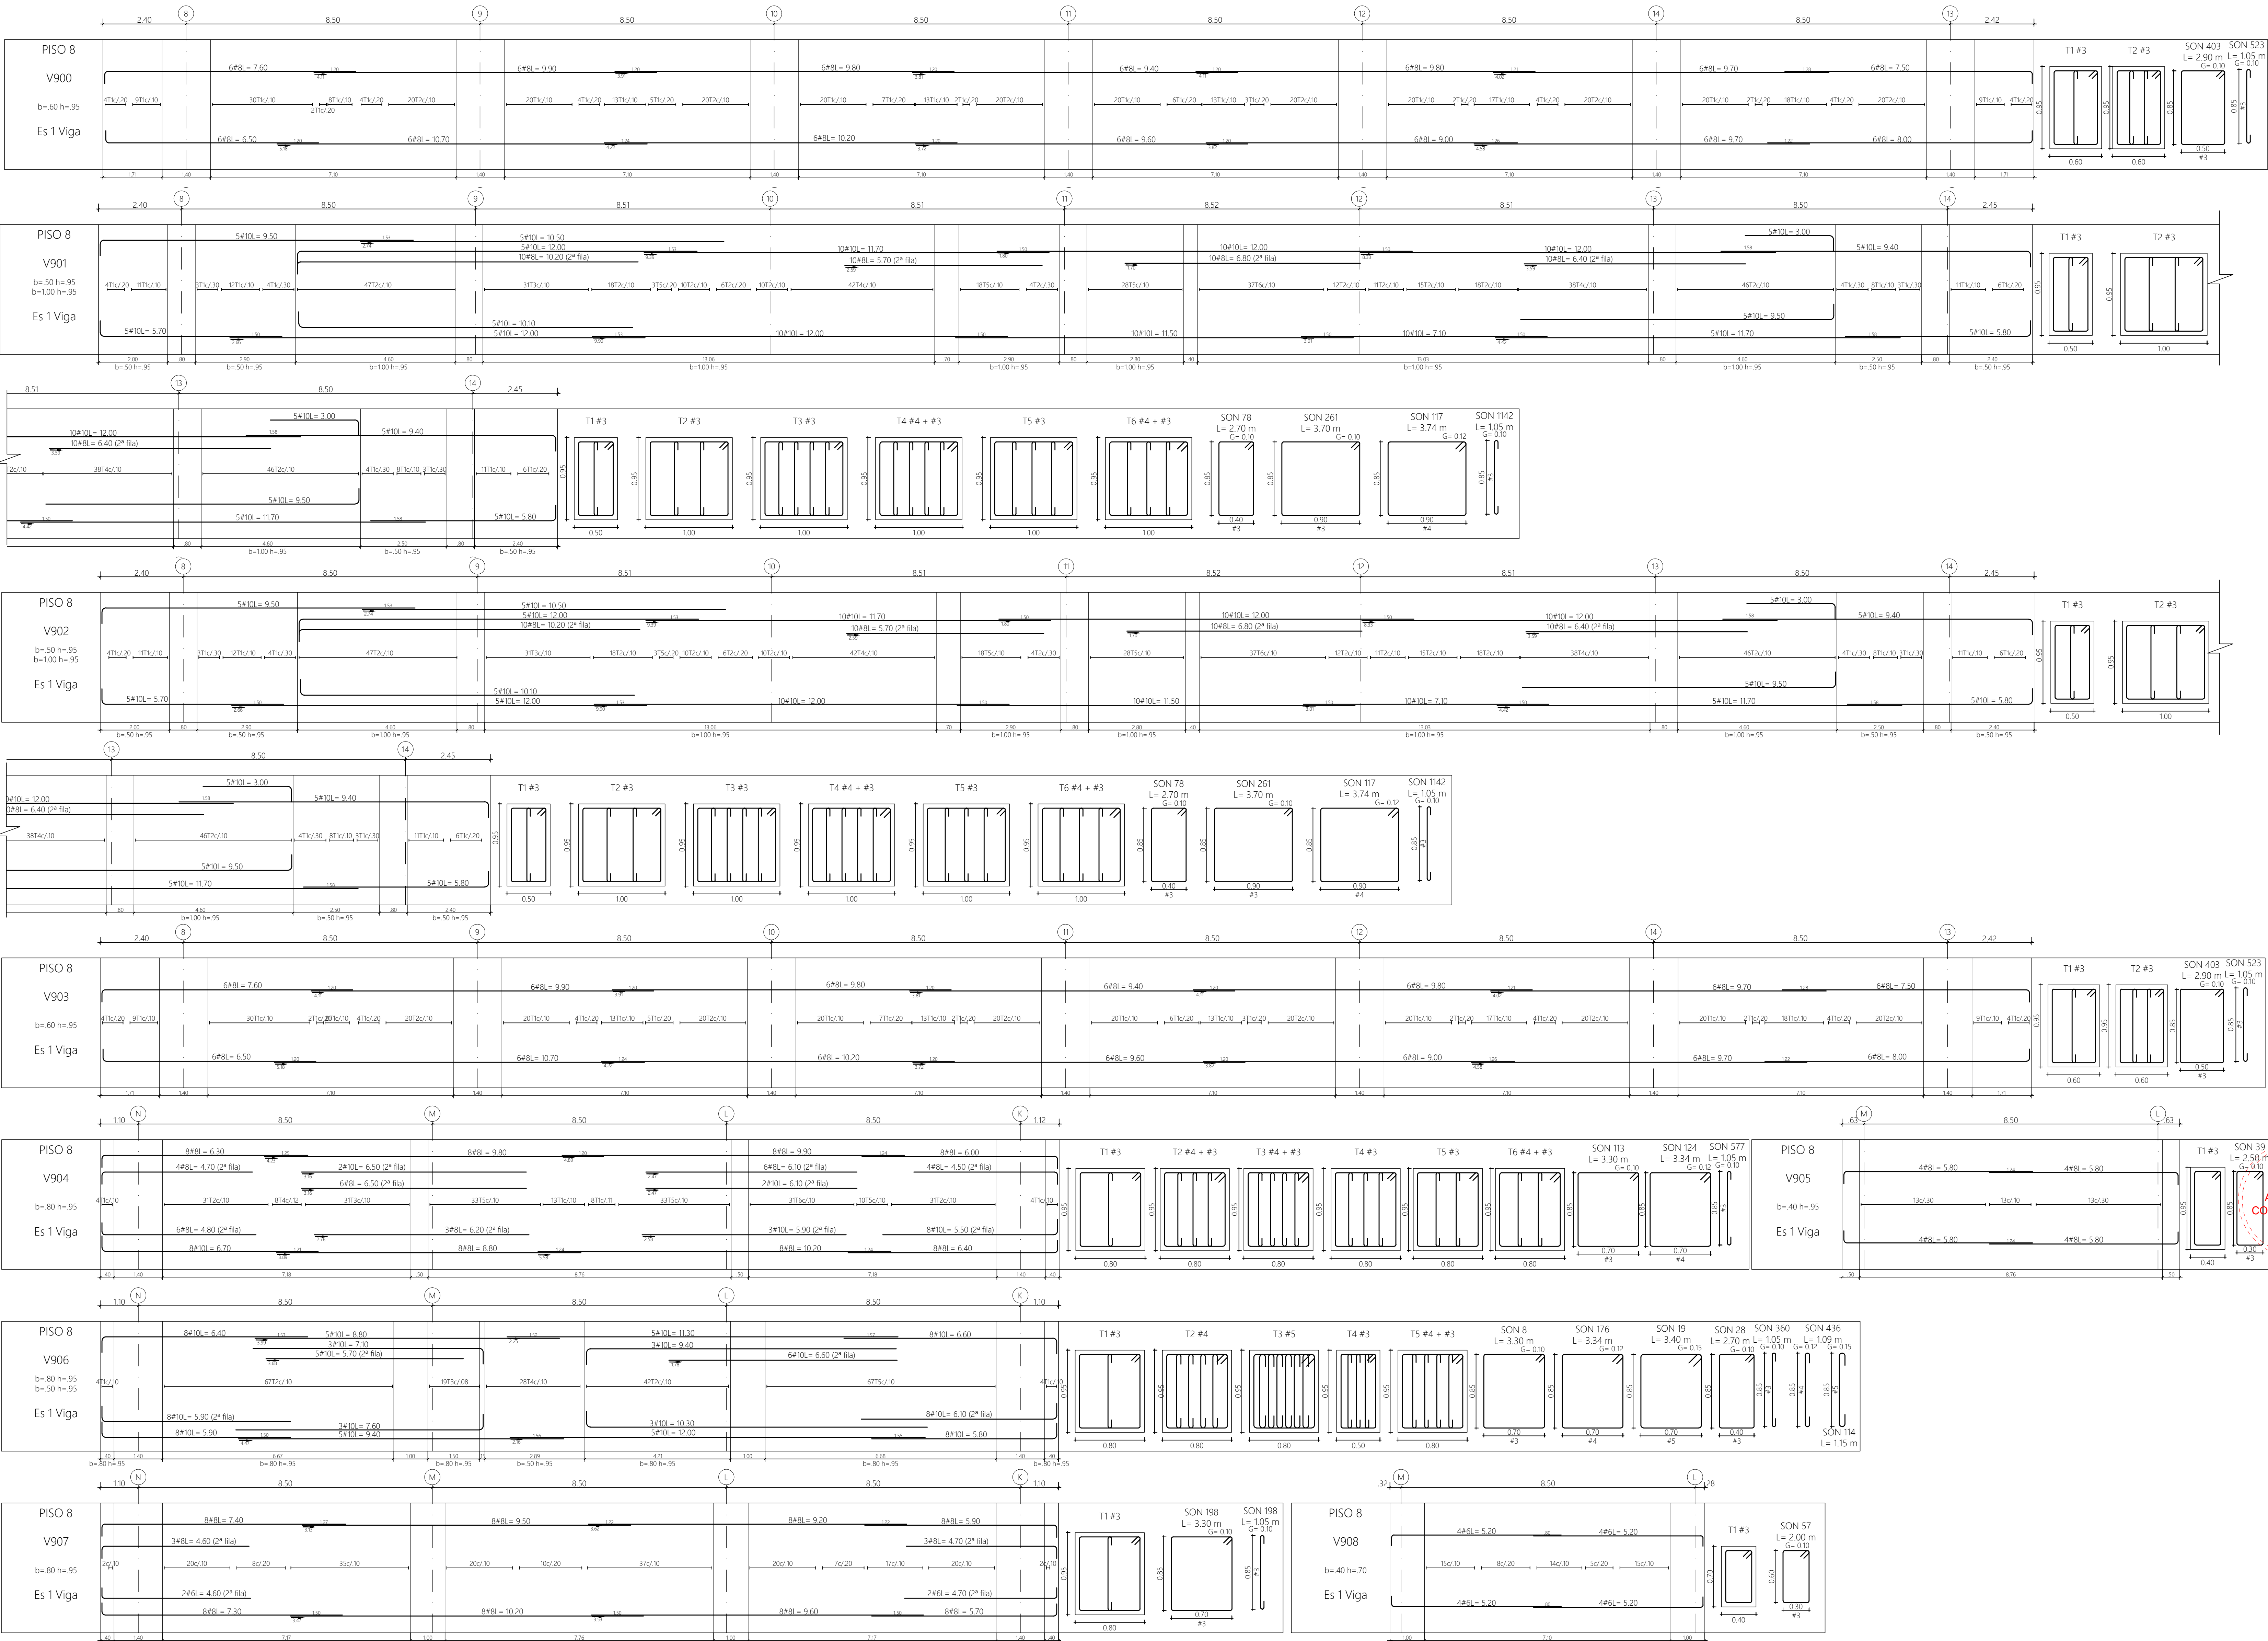

DESPIECES DE VIGAS DE PISO 8  
escala 1:75

**CTIB**  
Campus de Ciencia, Tecnología e Innovación de Bogotá - Región

**corferias**  
Generadores de Oportunidades y Progreso

**Cámara de Comercio de Bogotá**  
Secretaría Distrital de Economía Urbana

**BOGOTÁ**  
Secretaría Distrital de Economía Urbana

ARQUITECTO COORDINADOR

**EL EQUIPO MAZZANTI + Gensler**

DISÑO ESTRUCTURAL

**CNI**  
CONSTRUCCIÓN NACIONAL INTEGRAL

DISEÑADOR

ING. NICOLÁS PARRA GARCÍA  
MAT. 23202 62063 CND

INTERVENTORIA

**GUTIÉRREZ DÍAZ S.A.S.**  
SUPERVISIÓN Y LABORATORIO PROYECTOS DE CONSTRUCCIÓN

Director de Interventoría:

Ing. Jorge Iván García Mancilla  
Mat. 632021 148063 QND

| Versión | Emisión    | Descripción          |
|---------|------------|----------------------|
| AA      | 15-06-2023 | Ingeniería básica    |
| AB      | 04-08-2023 | Anteproyecto         |
| AC      | 01-11-2023 | Anteproyecto V2 50%  |
| AD      | 15-12-2023 | Anteproyecto V2 100% |
| DD      | 13-03-2024 | Entrega curaduría    |
| EE      | 10-05-2024 | Proyecto Final 100%  |
| EF      | 31-05-2024 | Respuesta Obs 100%   |
| FF      | 21-06-2024 | Entrega Final        |
| 01      | 28-07-2024 | ENTREGA FINAL        |

PROYECTO:

**CAMPUS DE CIENCIA TECNOLOGÍA E INNOVACIÓN DE BOGOTÁ**  
MAT. No. 500-00252470

FASE

**ENTREGA FINAL**

PROPÓSITO DE EMISIÓN

|                 |                                     |              |                          |
|-----------------|-------------------------------------|--------------|--------------------------|
| Curaduría       | <input type="checkbox"/>            | Coordinación | <input type="checkbox"/> |
| Revisión        | <input type="checkbox"/>            | Construcción | <input type="checkbox"/> |
| Entrega Cliente | <input checked="" type="checkbox"/> |              |                          |

SONIFICACION

|          |  |
|----------|--|
| Nivel 24 |  |
| Nivel 23 |  |
| Nivel 22 |  |
| Nivel 21 |  |
| Nivel 20 |  |
| Nivel 19 |  |
| Nivel 18 |  |
| Nivel 17 |  |
| Nivel 16 |  |
| Nivel 15 |  |
| Nivel 14 |  |
| Nivel 13 |  |
| Nivel 12 |  |
| Nivel 11 |  |
| Nivel 10 |  |
| Nivel 9  |  |
| Nivel 8  |  |
| Nivel 7  |  |
| Nivel 6  |  |
| Nivel 5  |  |
| Nivel 4  |  |
| Nivel 3  |  |
| Nivel 2  |  |
| Nivel 1  |  |
| Nivel 01 |  |
| Nivel 02 |  |

KEY PLAN

Fecha:

28-07-2024

Escala:

As Indicated

DESPIECES DE VIGAS DE PISO 8  
CTIB\_CNI\_EST\_429\_DSP\_XXX\_01

PROYECTO DETALLADO  
APTO PARA CONSTRUCCIÓN (APC)