


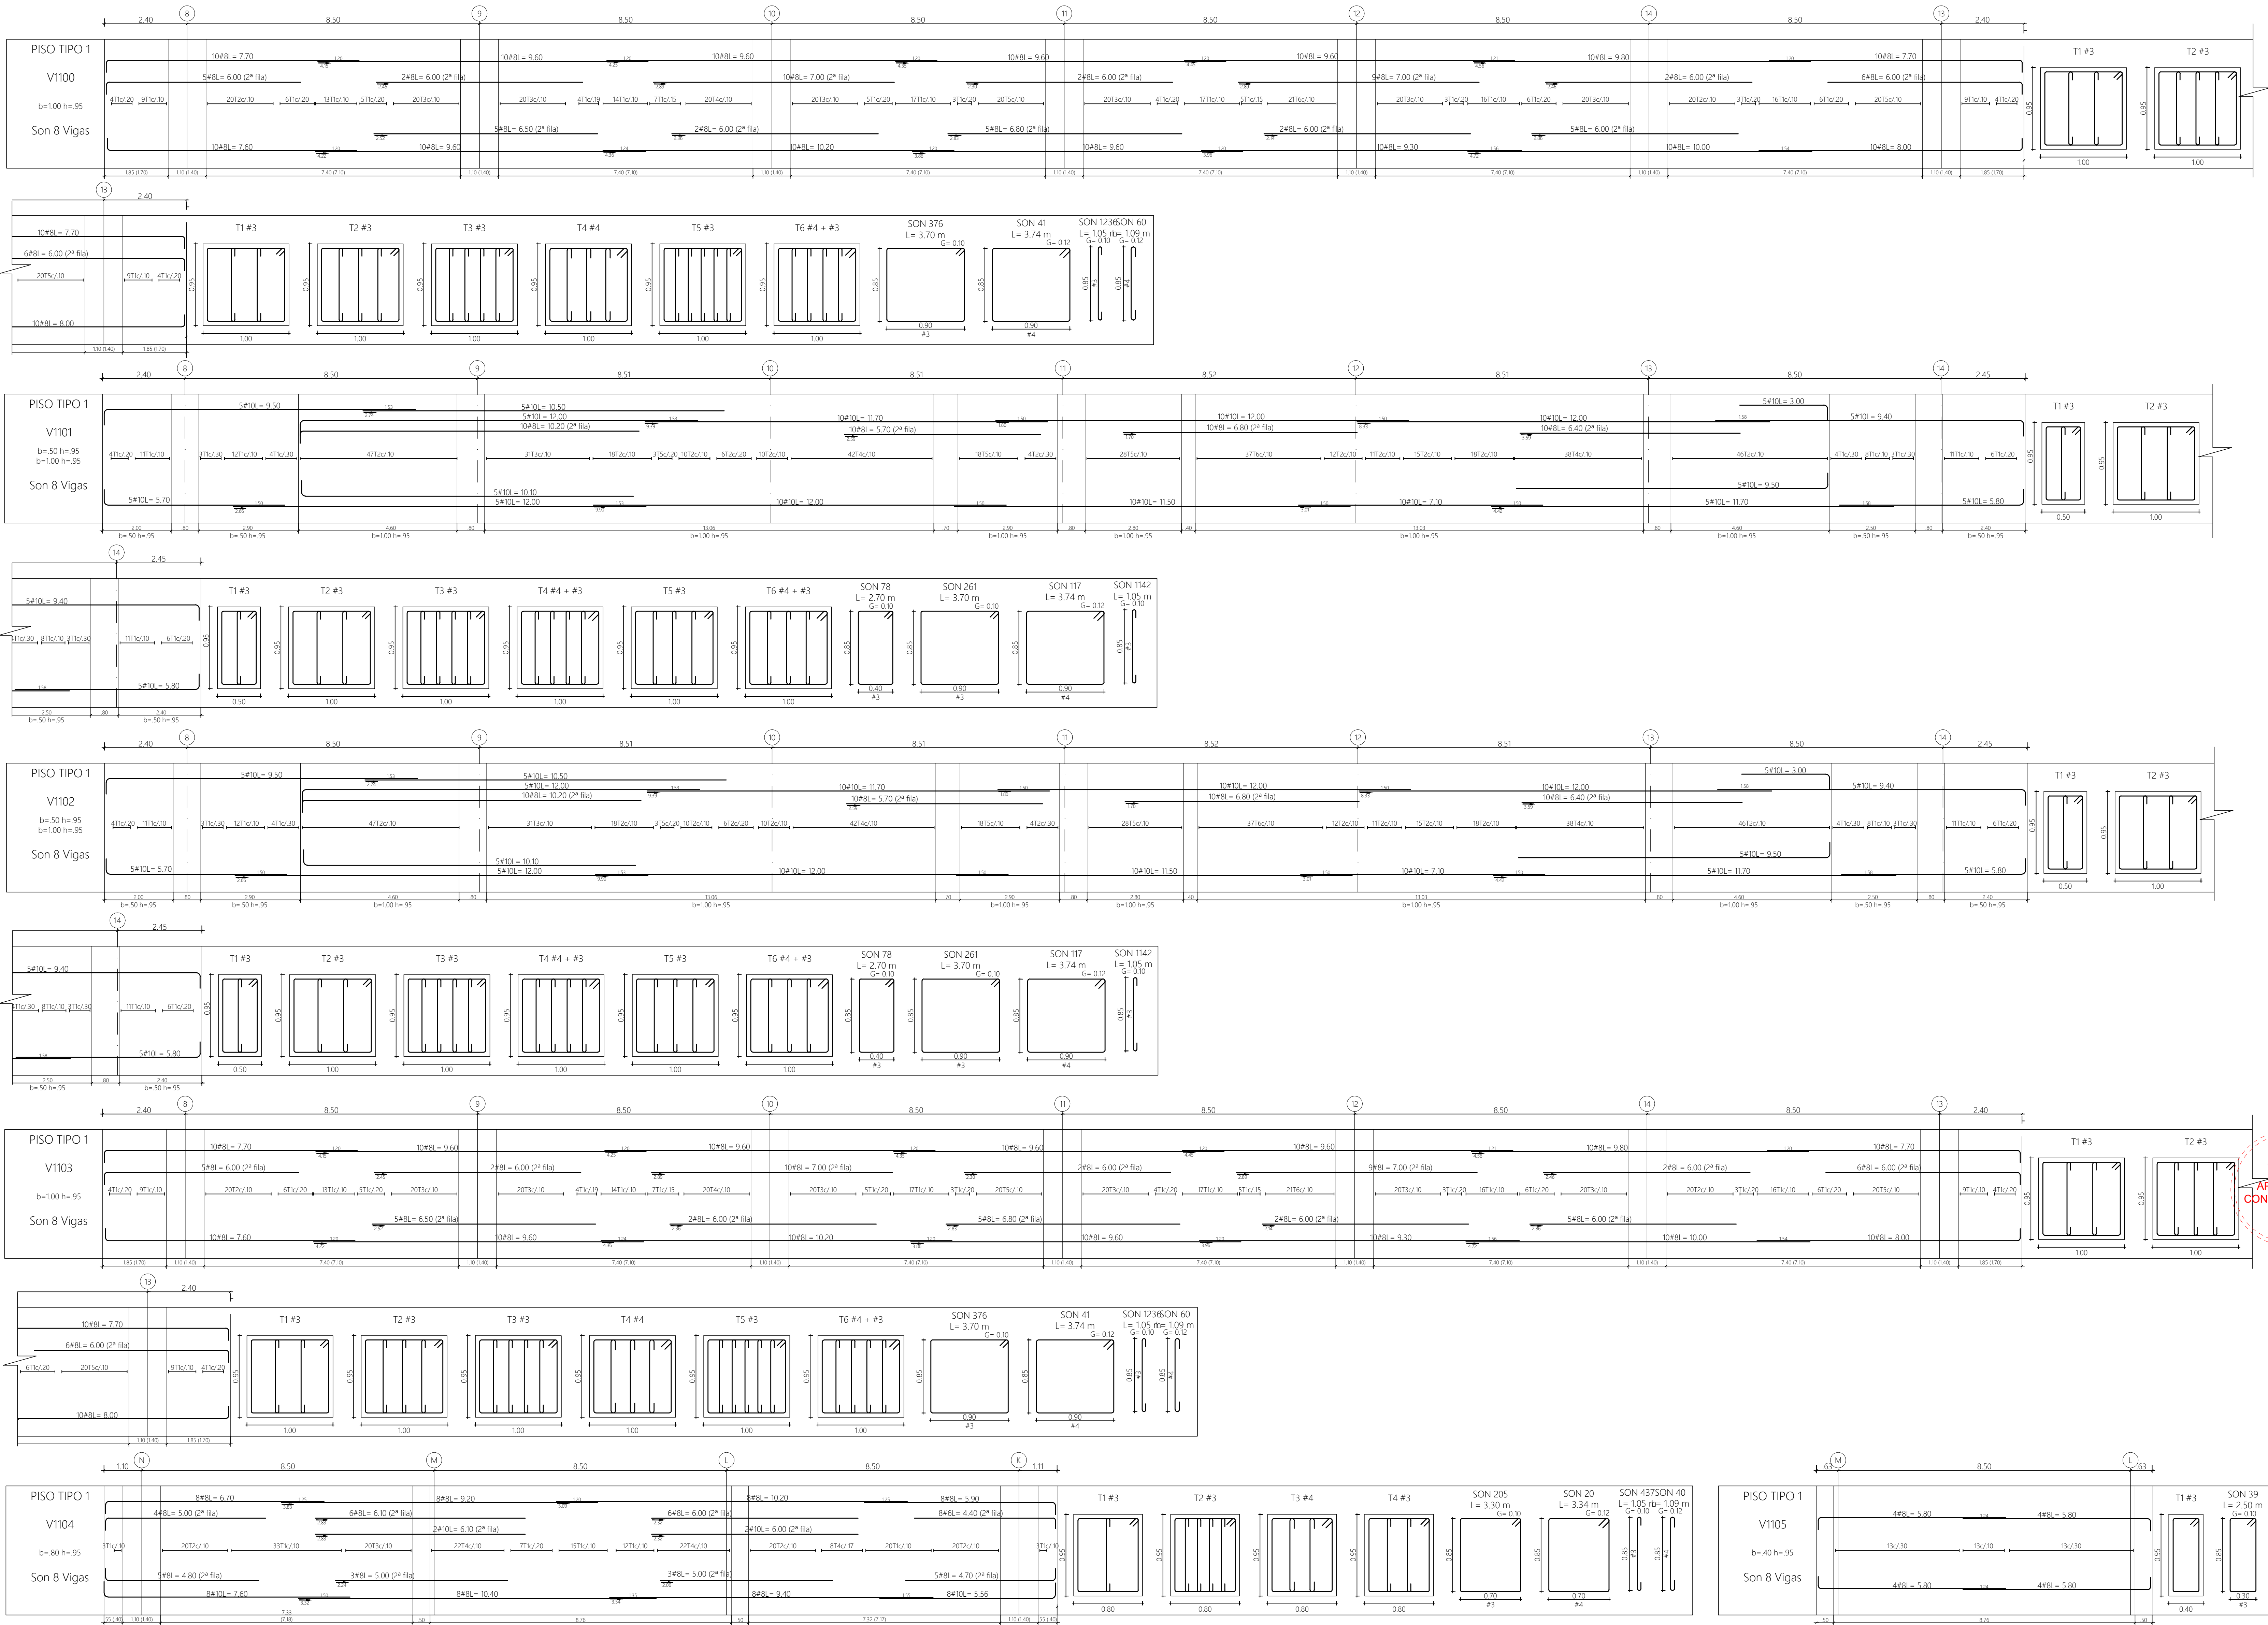

DESPIECES DE VIGAS DE PISO TIPO 1 (NIVEL 10 A 17)
escala 1:75

NOTAS IMPORTANTES:
1. Los valores entre parentesis aplican para el nivel 10.
2. El primer estribo debe quedar a 5cm de la cara de la columna o el muro.

CTIB
Campus de Ciencia, Tecnología e Innovación de Bogotá - Región

corferias
Generadores de Oportunidades y Progreso

Cámara de Comercio de Bogotá
Secretaría Distrital de Desarrollo Económico

BOGOTÁ
Secretaría Distrital de Desarrollo Económico

ARQUITECTO COORDINADOR

ELEQUIPO MAZZANTI + Gensler

DISEÑO ESTRUCTURAL

CNI

DISEÑADOR: ING. NICOLÁS PARRA GARCÍA
MAT. 23202 62063 CND

INTERVENTORIA

GUTIERREZ DÍAZ S.A.S.
SUPERVISIÓN Y LABORATORIO PROYECTOS DE CONSTRUCCIÓN

Director de Interventoría: Ing. Jorge Iván García Mancilla
Mat. 632021 148063 QND

Versión	Emisión	Descripción
AA	15-06-2023	Ingeniería básica
AB	04-08-2023	Anteproyecto
AC	01-11-2023	Anteproyecto V2 50%
AD	15-12-2023	Anteproyecto V2 100%
DD	13-03-2024	Entrega curaduría
DE	10-05-2024	Proyecto Final 100%
EF	31-05-2024	Respuesta Obs 100%
FF	21-06-2024	Entrega Final
01	26-07-2024	ENTREGA FINAL

PROYECTO:
CAMPUS DE CIENCIA TECNOLOGÍA E INNOVACIÓN DE BOGOTÁ
MAT. No. 502-0025470

FASE
ENTREGA FINAL

PROPÓSITO DE EMISIÓN

Curaduría	☐	Coordinación	☐
Revisión	☐	Construcción	☐
Entrega Cliente	☒		

ZONIFICACIÓN

Nivel 24	
Nivel 23	
Nivel 22	
Nivel 21	
Nivel 20	
Nivel 19	
Nivel 18	
Nivel 17	
Nivel 16	
Nivel 15	
Nivel 14	
Nivel 13	
Nivel 12	
Nivel 11	
Nivel 10	
Nivel 9	
Nivel 8	
Nivel 7	
Nivel 6	
Nivel 5	
Nivel 4	
Nivel 3	
Nivel 2	
Nivel 1	
Nivel 0	
Nivel B1	
Nivel B2	

KEY PLAN

Fecha: 26-07-2024

Escala: As Indicated

DESPIECES DE VIGAS PISO TIPO 1 (NIVEL 10 A 17)

CTIB_CNI_EST_433_DSP_XXX_01

PROYECTO DETALLADO
APTO PARA CONSTRUCCIÓN (APC)