


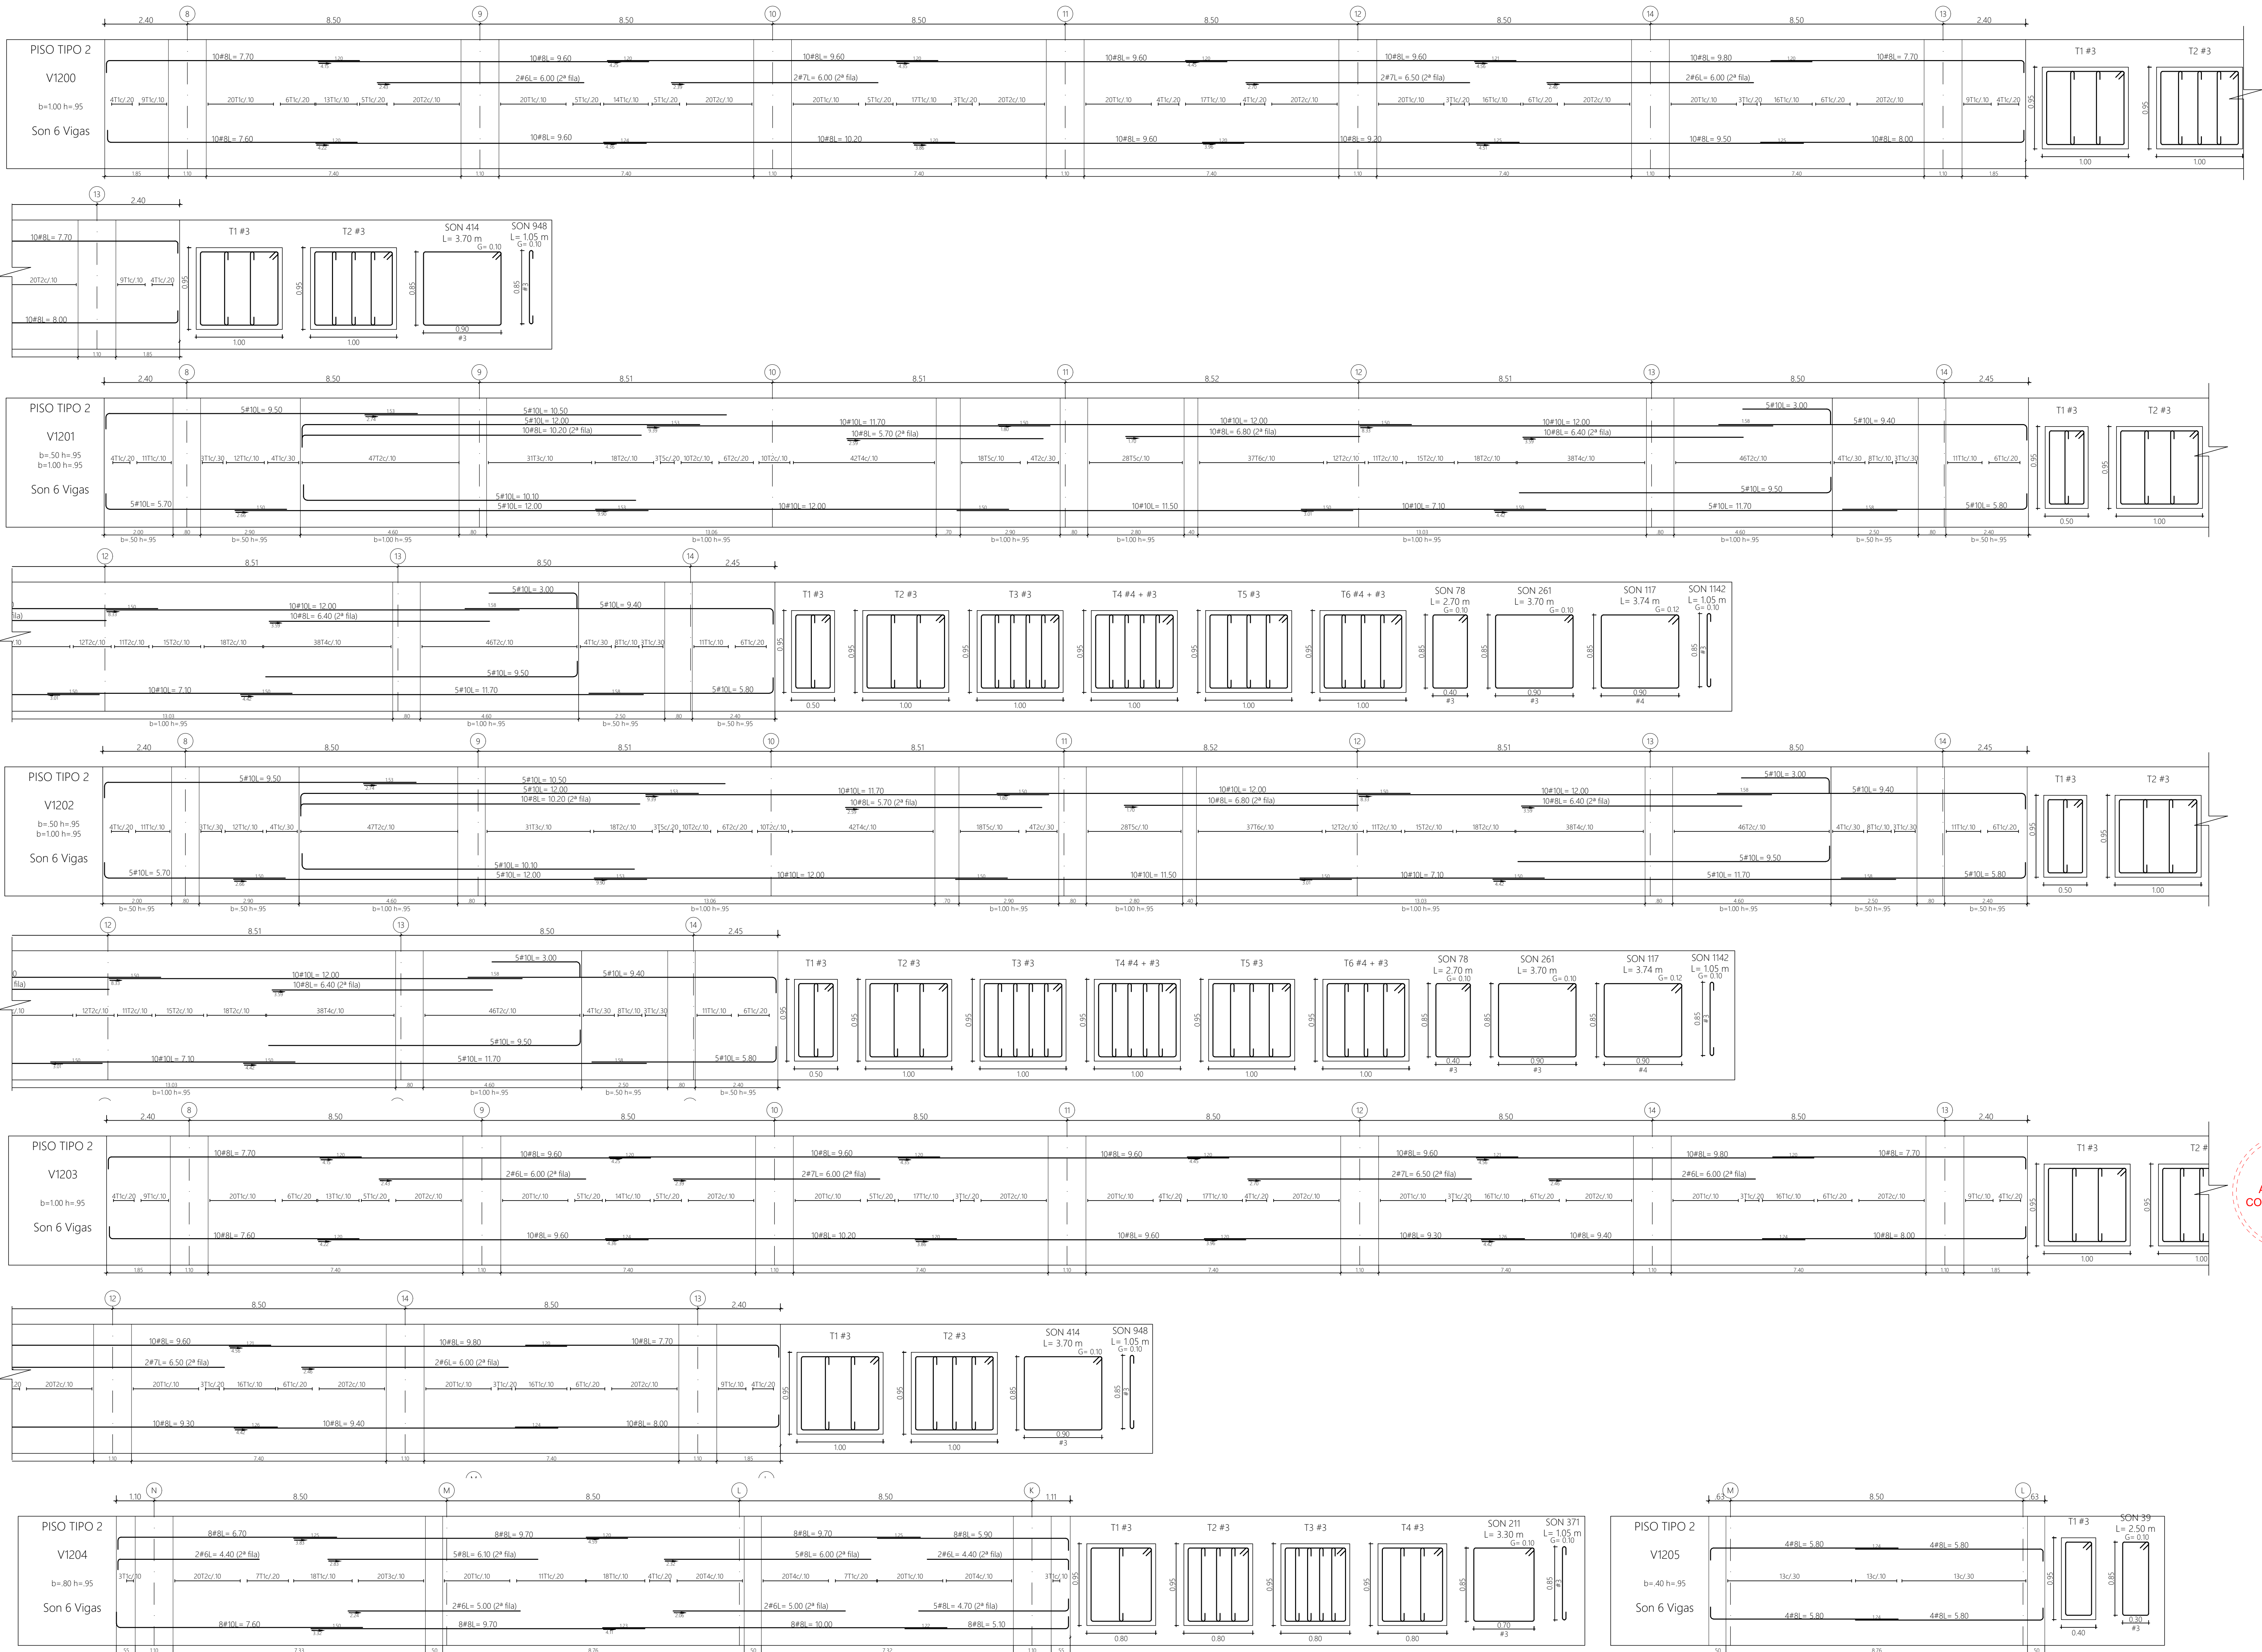

DESPIECES DE VIGAS DE PISO TIPO 2 (NIVEL 18 A 23)
escala 1:75

Versión	Emisión	Descripción
AA	15-06-2023	Ingeniería básica
AB	04-08-2023	Anteproyecto
AC	01-11-2023	Anteproyecto V2 50%
AD	15-12-2023	Anteproyecto V2 100%
DD	13-03-2024	Entrega curaduría
EE	10-05-2024	Proyecto Final 100%
EF	31-05-2024	Respuesta Obs 100%
FF	21-06-2024	Entrega Final
01	26-07-2024	ENTREGA FINAL


PROYECTO:
CAMPUS DE CIENCIA TECNOLOGÍA E
INNOVACIÓN DE BOGOTÁ
MAT. No. 502-00252470

FASE
ENTREGA FINAL

PROPÓSITO DE EMISIÓN
Curaduría ☐ Coordinación ☐
Revisión ☐ Construcción ☐
Entrega Cliente ☒

ZONIFICACIÓN

Nivel 24	
Nivel 23	
Nivel 22	
Nivel 21	
Nivel 20	
Nivel 19	
Nivel 18	
Nivel 17	
Nivel 16	
Nivel 15	
Nivel 14	
Nivel 13	
Nivel 12	
Nivel 11	
Nivel 10	
Nivel 9	
Nivel 8	
Nivel 7	
Nivel 6	
Nivel 5	
Nivel 4	
Nivel 3	
Nivel 2	
Nivel 1	
Nivel B1	
Nivel B2	

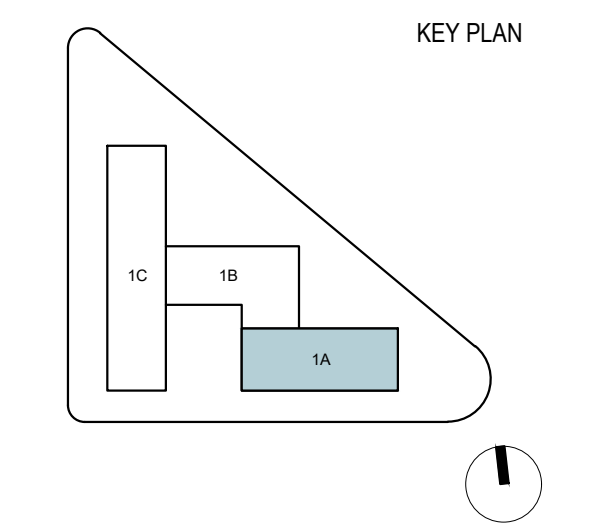

Fecha: 26-07-2024

Escala: As Indicated

DESPIECES DE VIGAS DE PISO TIPO 2
(NIVEL 18 A 23)

CTIB_CNI_Ext_435_DSP_XXX_01