


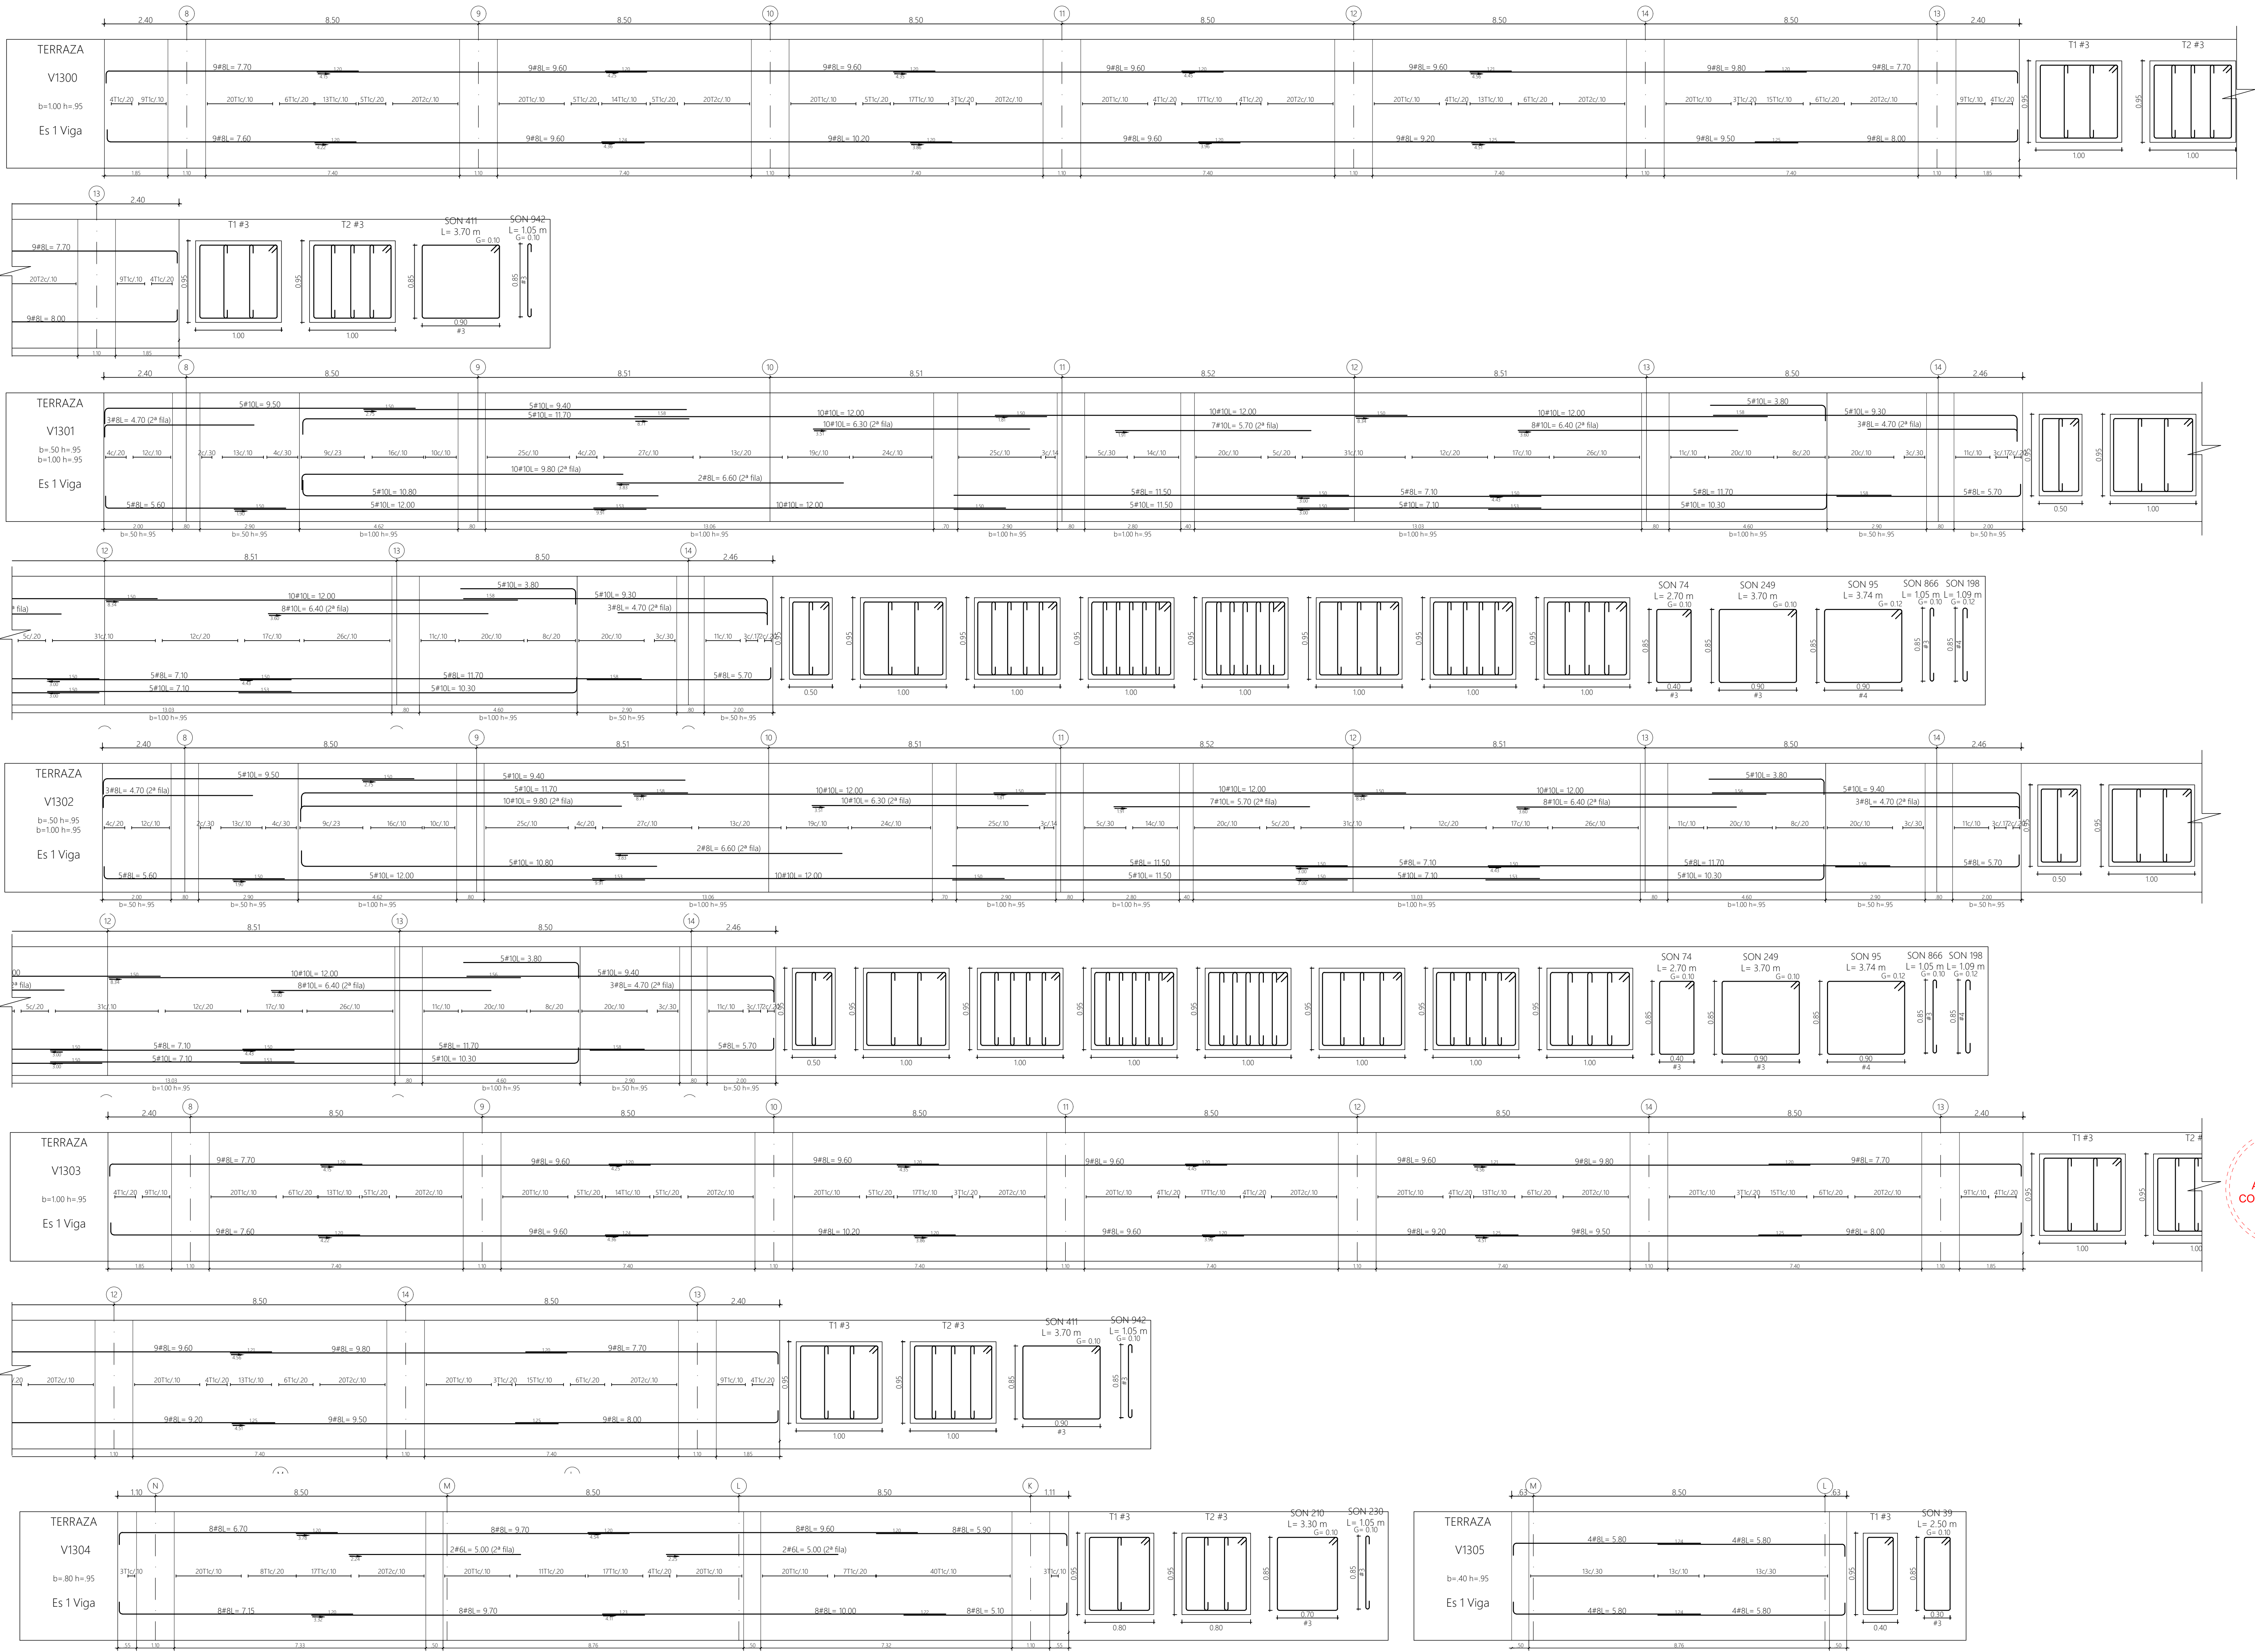

DESPICIES DE VIGAS DE TERRAZA
escala 1:75

CTIB
Campus de Ciencia, Tecnología e
Innovación de Bogotá - Región

Generadores de
Oportunidades y Progreso

Cámara
de Comercio
de Bogotá

BOGOTÁ
Secretaría Distrital de
Desarrollo Económico

ARQUITECTO COORDINADOR

ELEQUIPO MAZZANTI + Gensler

DISEÑO ESTRUCTURAL

CNI

DISEÑADOR

ING. NICOLÁS PARRA GARCÍA
MAT. 232021 62063 CND

INTERVENTORIA

GUTIERREZ DÍAZ S.A.S.
SUPERVISOR Y LABORATORIO PROYECTOS DE CONSTRUCCIÓN

Director de Interventoría:

Ing. Jorge Iván García Mancilla
Mat. 632021 148063 QND

Versión	Emisión	Descripción
AA	15-06-2023	Ingeniería básica
AB	04-08-2023	Anteproyecto
AC	01-11-2023	Anteproyecto V2 50%
AD	15-12-2023	Anteproyecto V2 100%
DD	13-03-2024	Entrega curaduría
EE	10-05-2024	Proyecto Final 100%
EF	31-05-2024	Respuesta Obs 100%
FF	21-06-2024	Entrega Final
01	28-07-2024	ENTREGA FINAL

PROYECTO:

CAMPUS DE CIENCIA TECNOLOGÍA E
INNOVACIÓN DE BOGOTÁ

MAT. No. 502-0025470

FASE

ENTREGA FINAL

PROPÓSITO DE EMISIÓN

Curaduría ☐ Coordinación ☐
Revisión ☐ Construcción ☐
Entrega Cliente ☒

ZONIFICACION

Nivel	Descripción
Nivel 24	
Nivel 23	
Nivel 22	
Nivel 21	
Nivel 20	
Nivel 19	
Nivel 18	
Nivel 17	
Nivel 16	
Nivel 15	
Nivel 14	
Nivel 13	
Nivel 12	
Nivel 11	
Nivel 10	
Nivel 9	
Nivel 8	
Nivel 7	
Nivel 6	
Nivel 5	
Nivel 4	
Nivel 3	
Nivel 2	
Nivel 1	
Nivel 01	
Nivel 02	

KEY PLAN

Fecha:

28-07-2024

Escala:

As Indicated

DESPICIES DE
VIGAS DE TERRAZA

CTIB_CNI_EST_437_DSP_XXX_01