




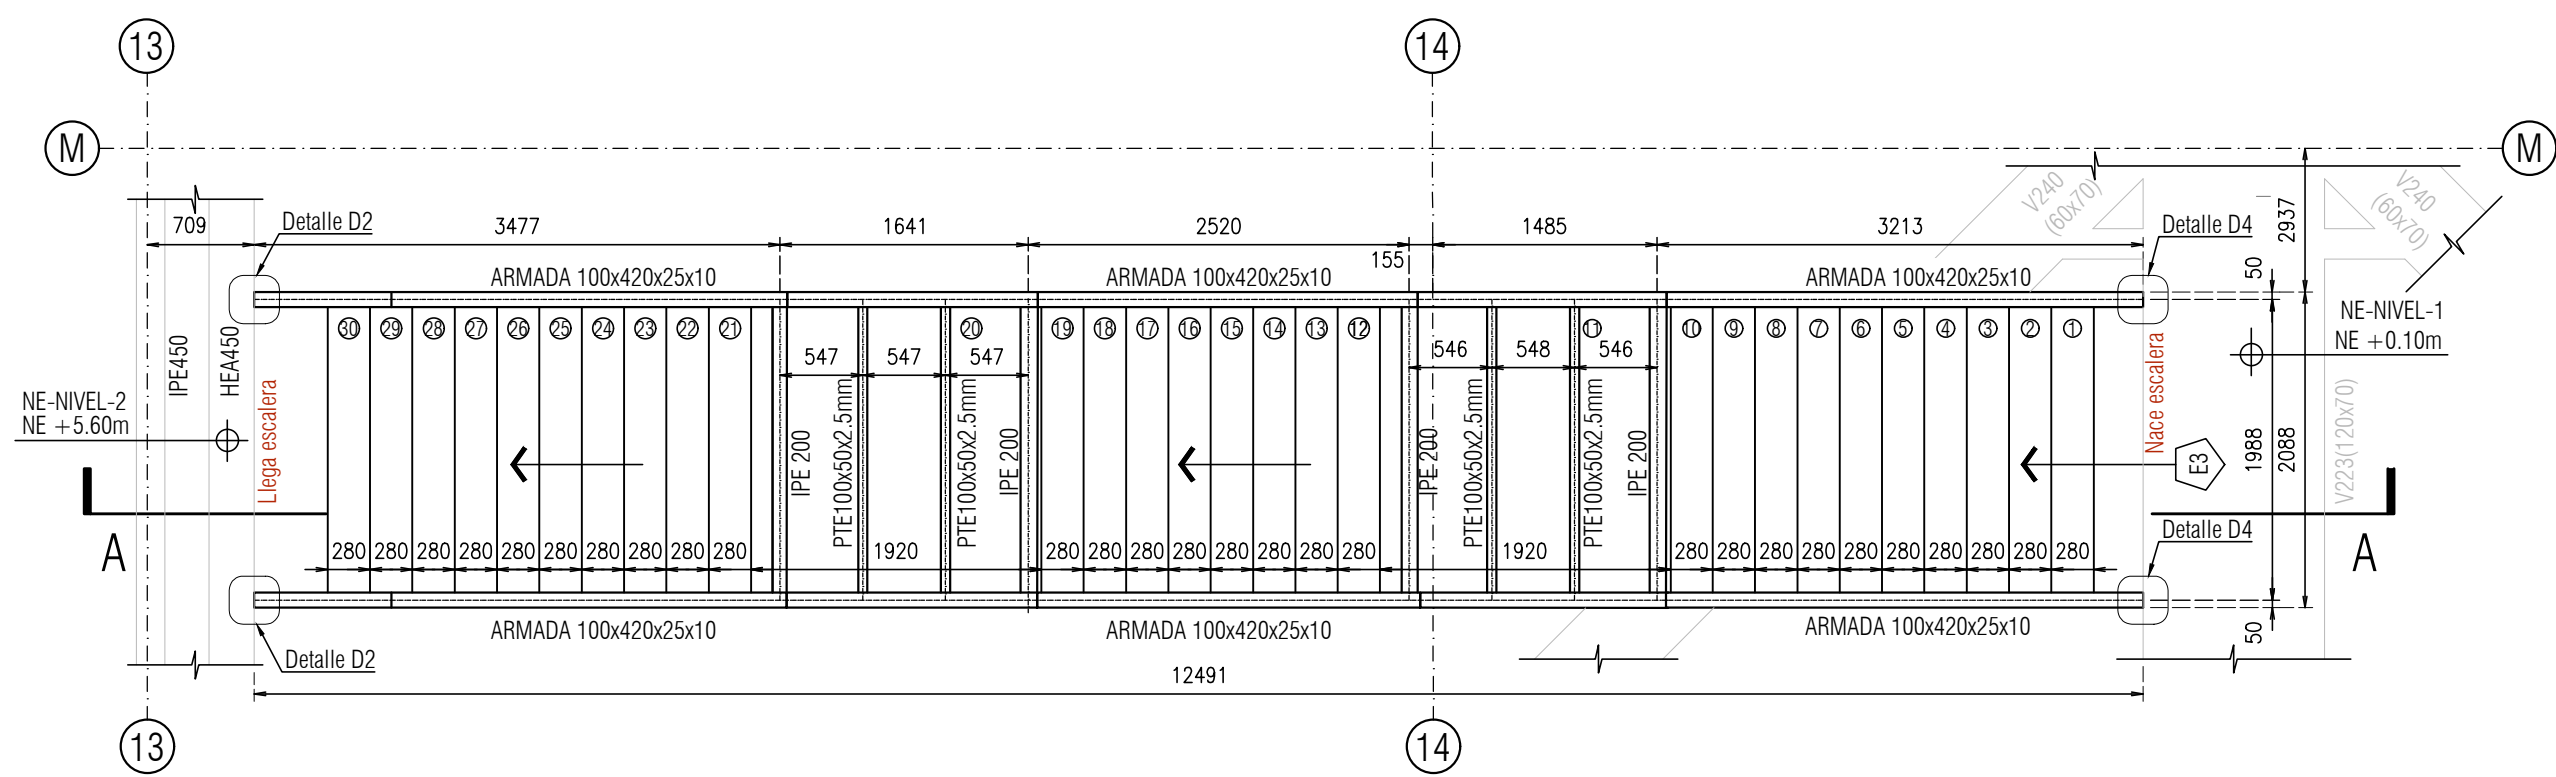


PLANTA ESCALERA E3
escala 1:50

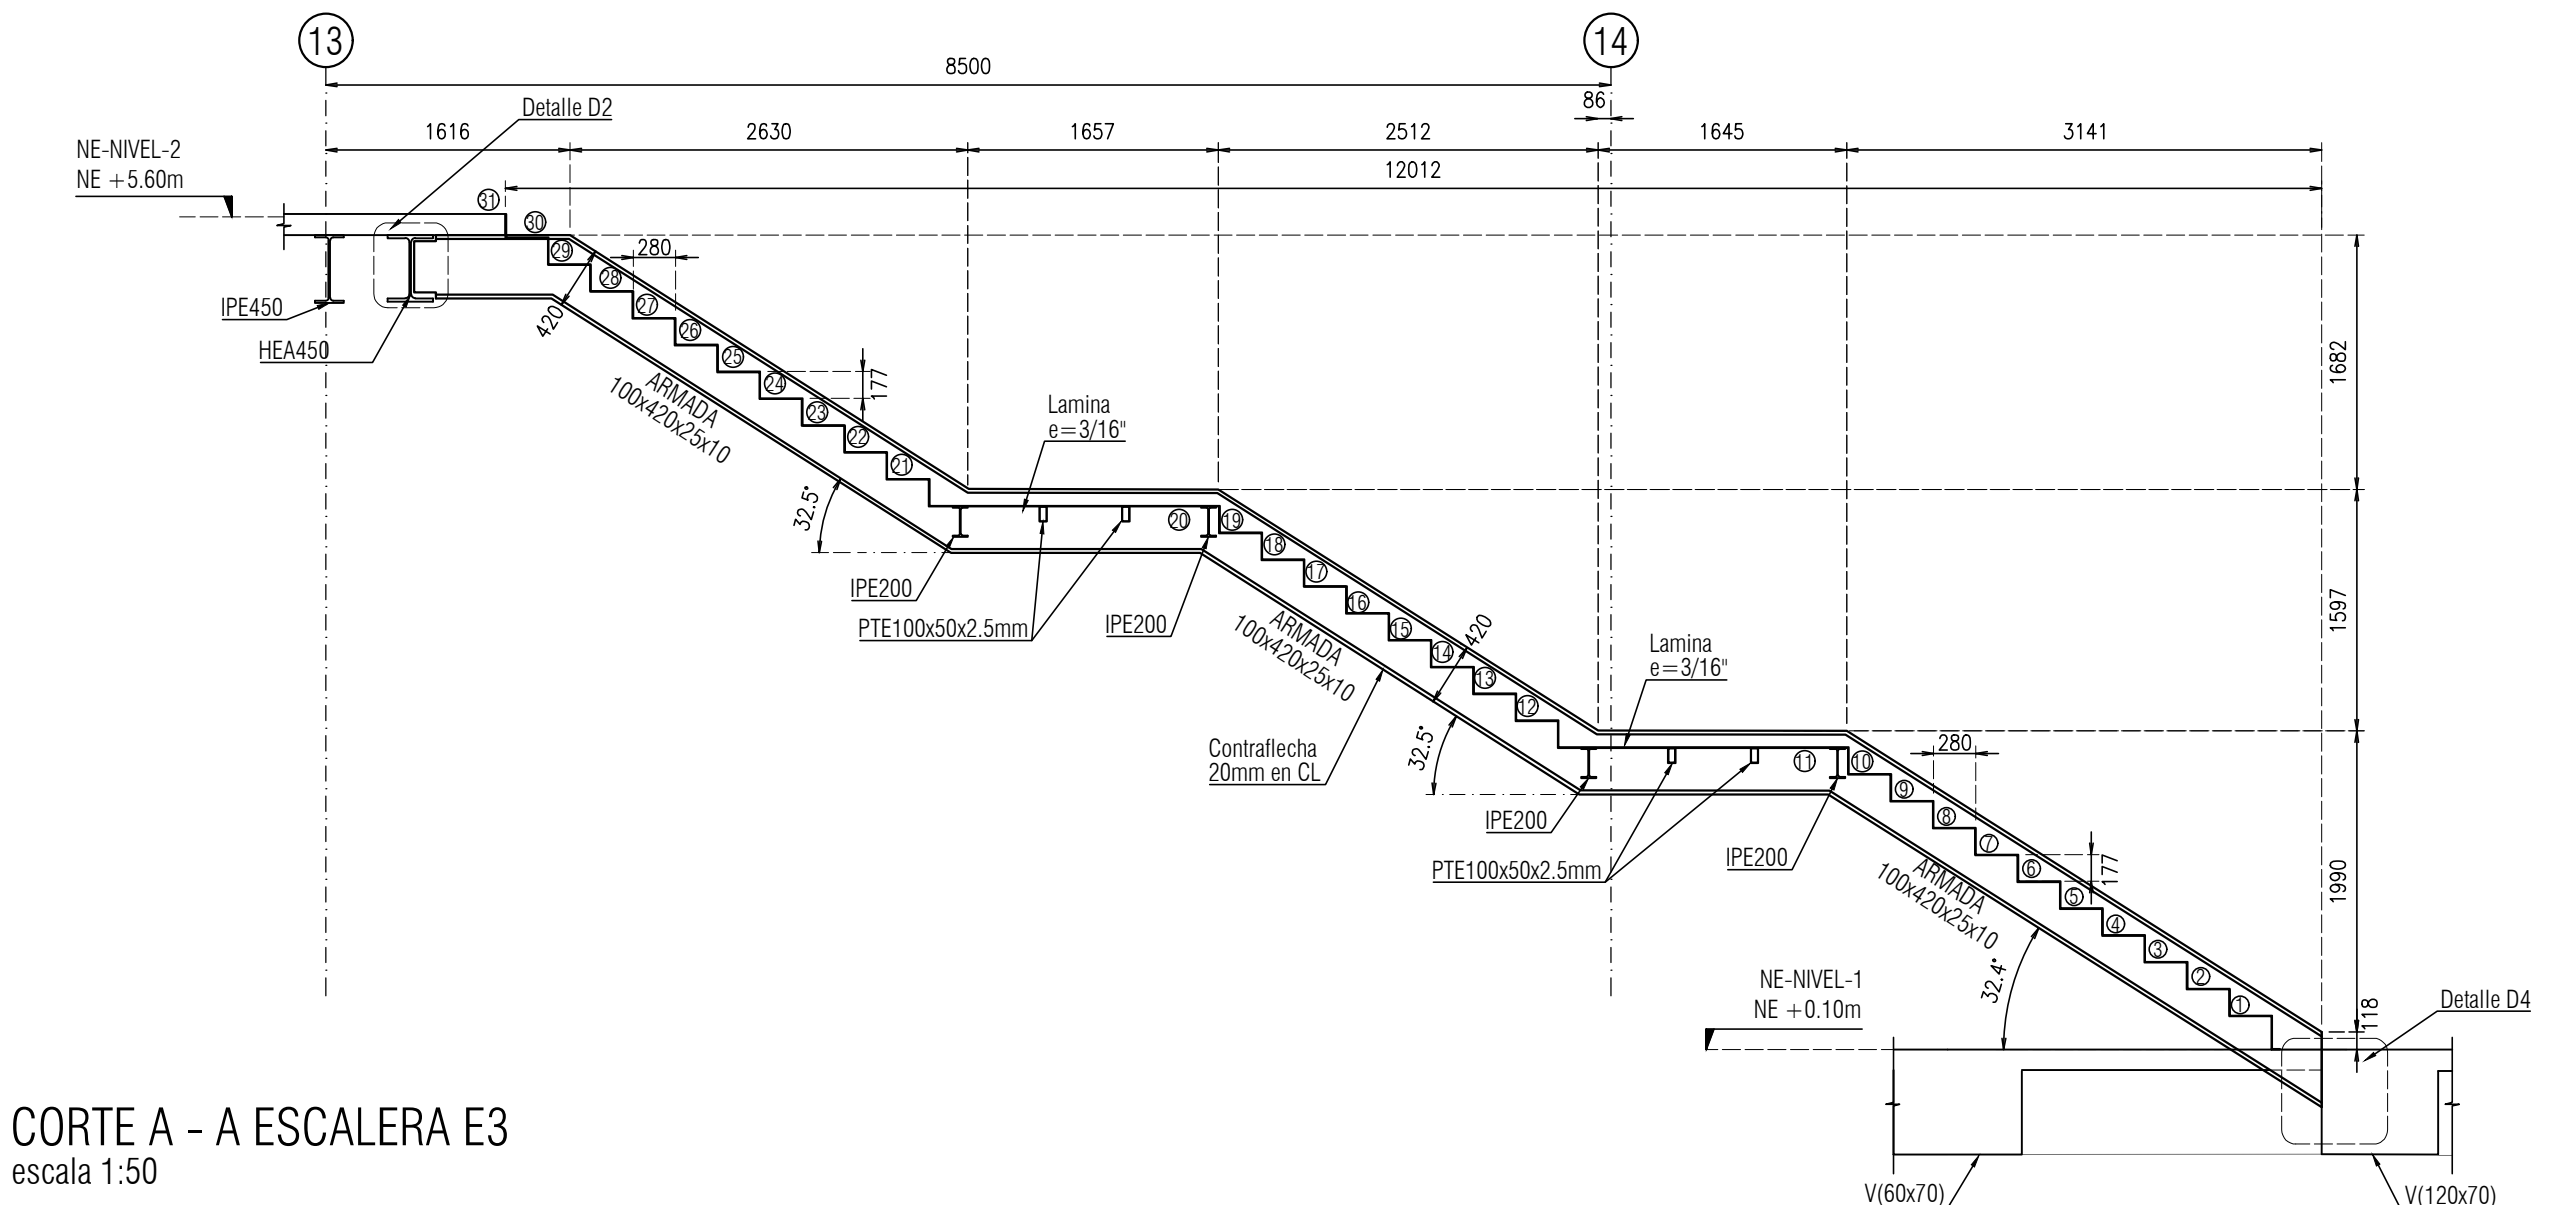


CORTE A - A ESCALERA E3
escala 1:50

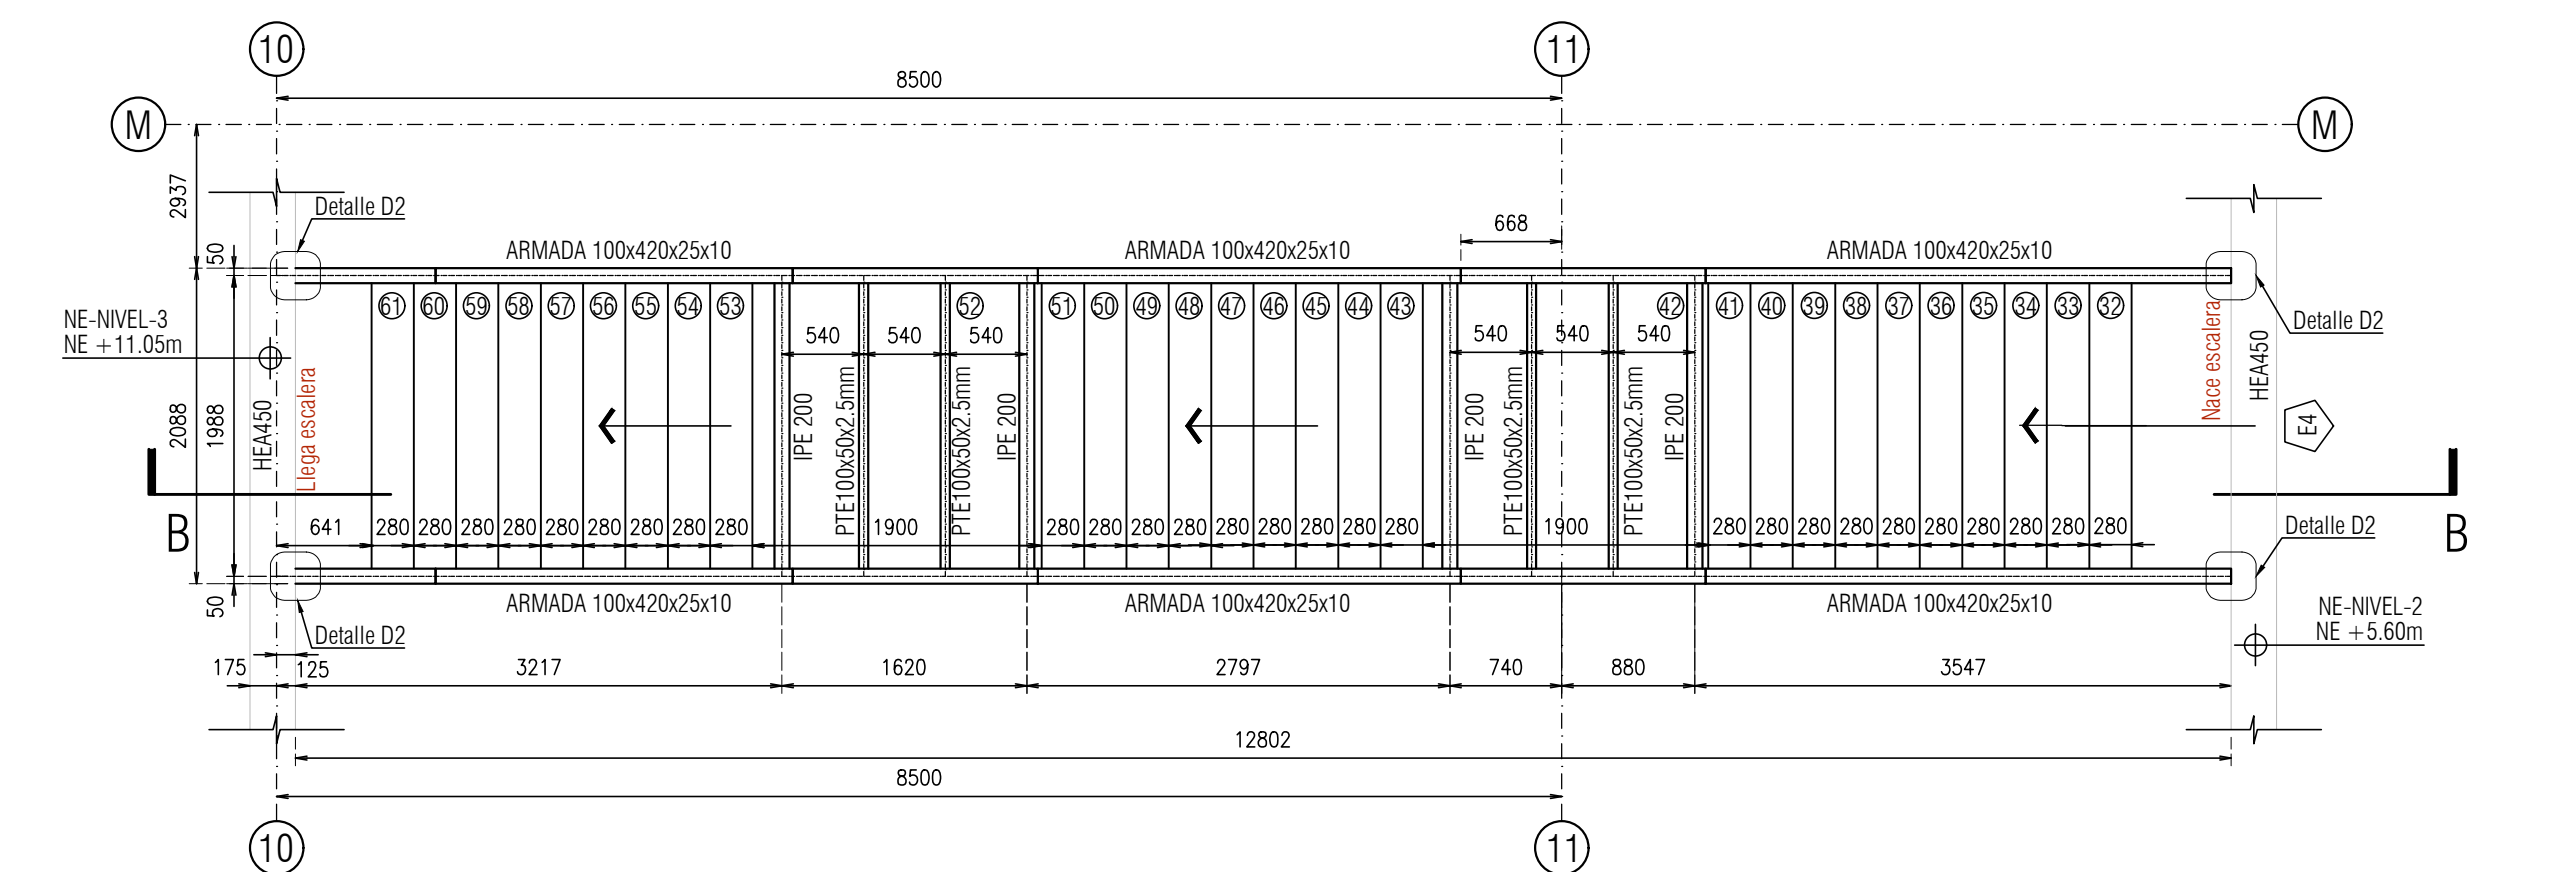

PLANTA ESCALERA E4
escala 1:50

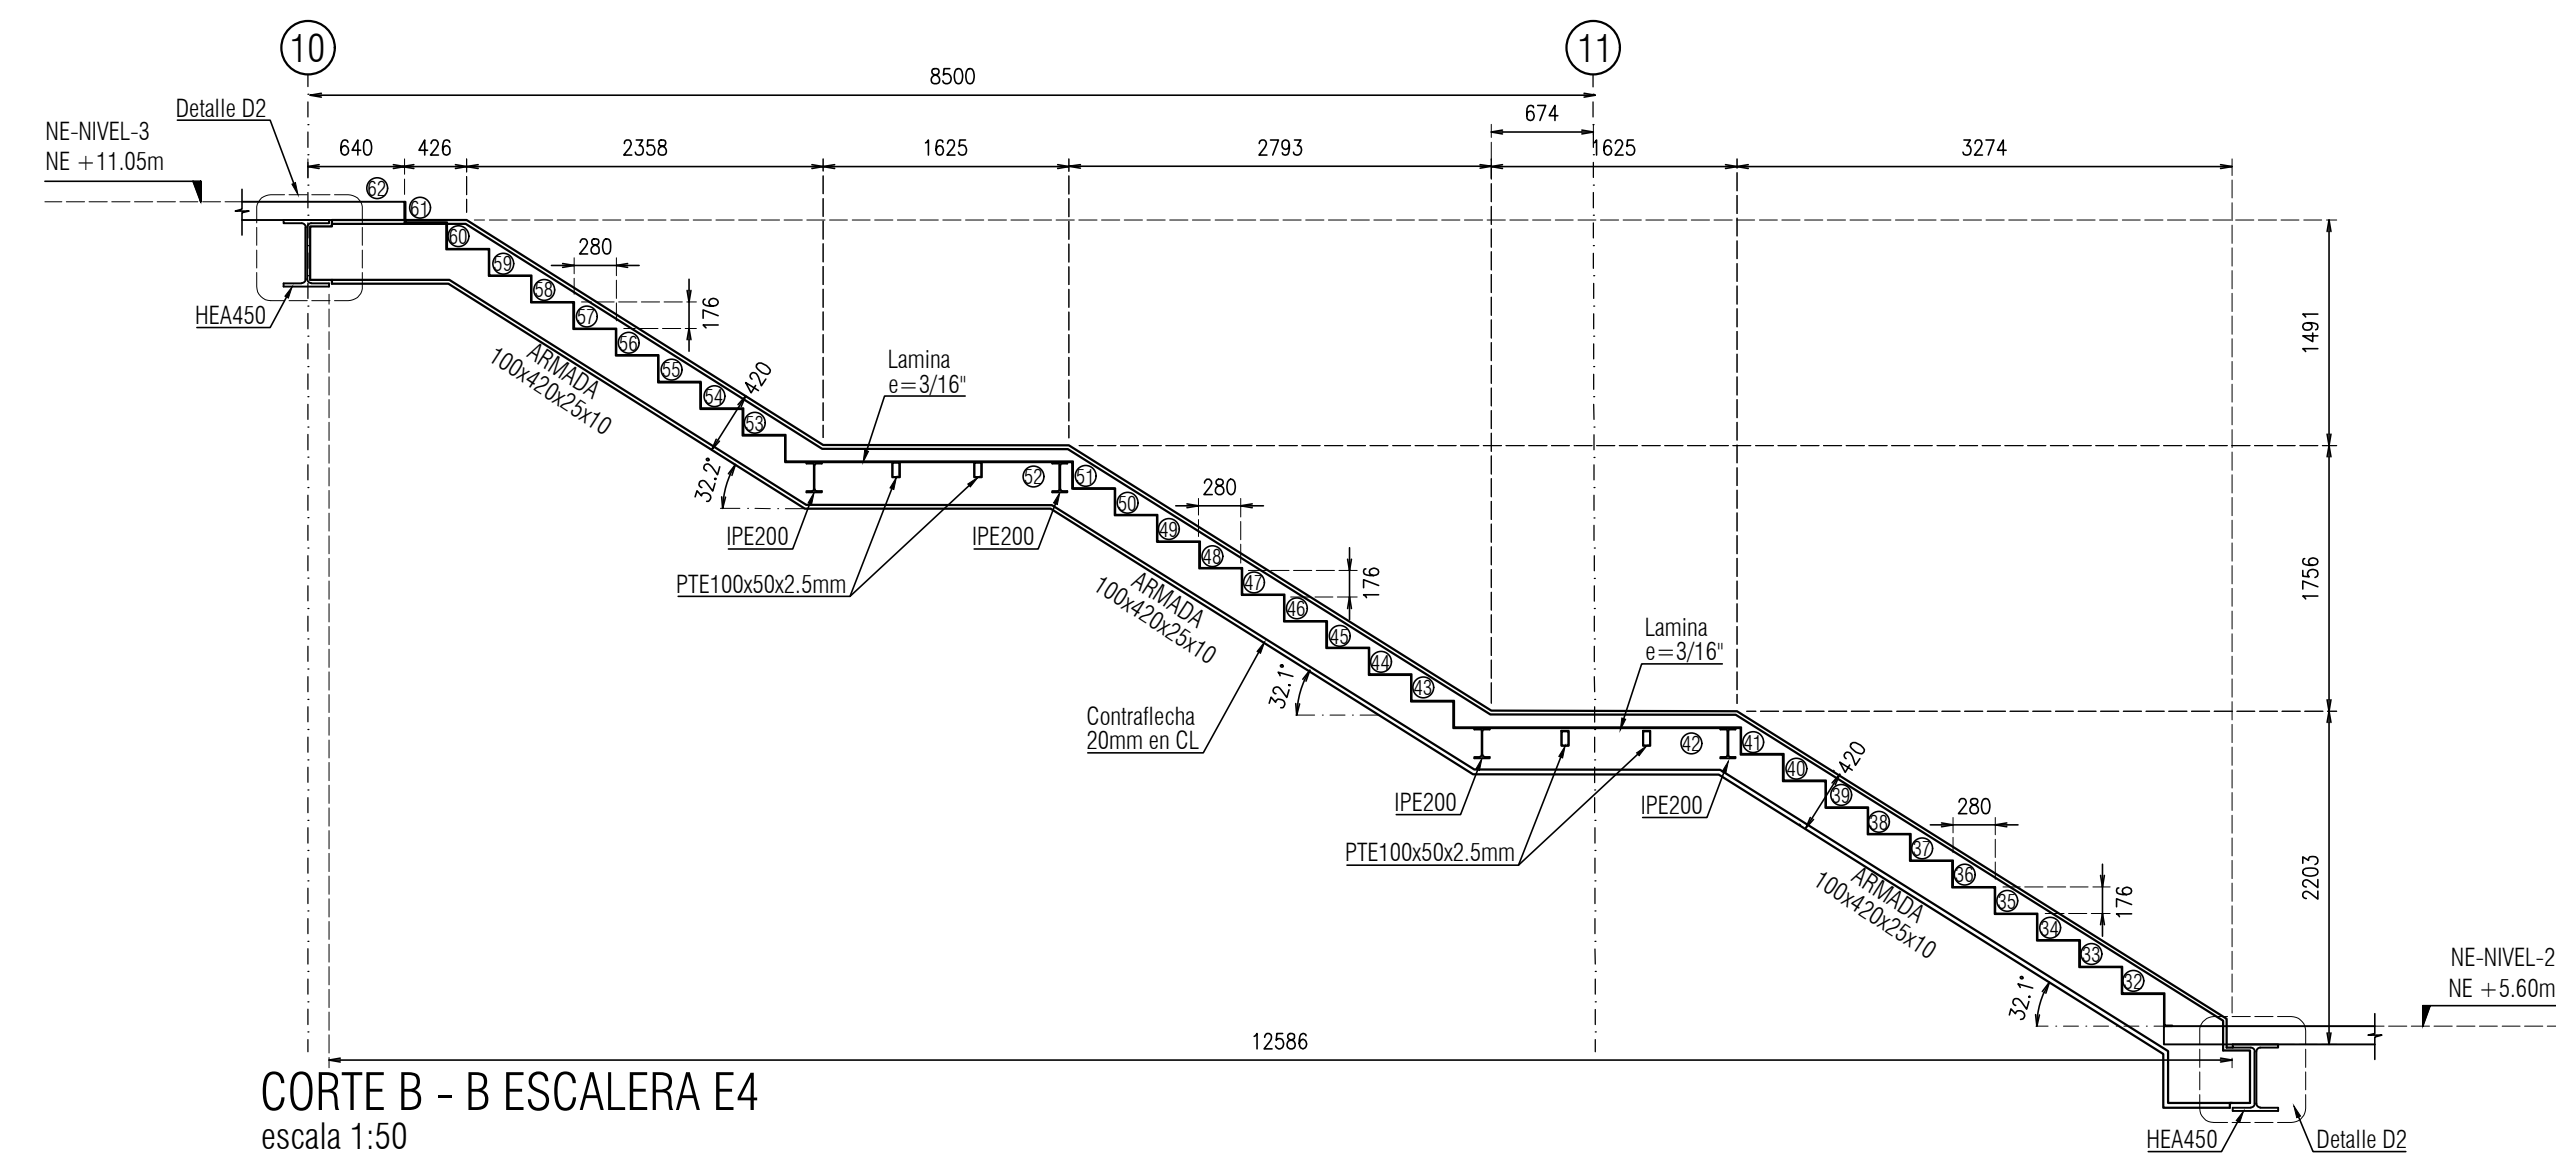


CORTE B - B ESCALERA E4
escala 1:50

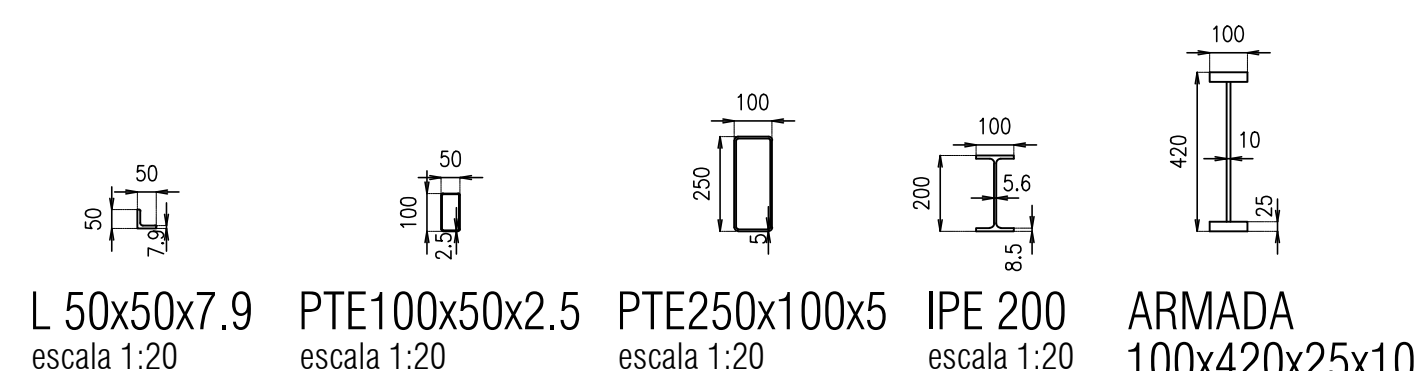


NOTAS IMPORTANTES:


- Los presentes planos son de diseño. El fabricante de la estructura metálica debe elaborar los respectivos planos de taller, los cuales deben ser revisados y aprobados por la interventoría y la supervisión técnica de la obra.
- Las escaleras E3, E4 y E5 requieren contralacha de 20mm en el centro de luz.
- Ver detalle de subestructura de escaleras E3, E4 y E5 en plano CTIB_CNI_EST_702_ENE_XXX.
- Escala E6 requiere contralacha de 10mm en la punta del voladizo.

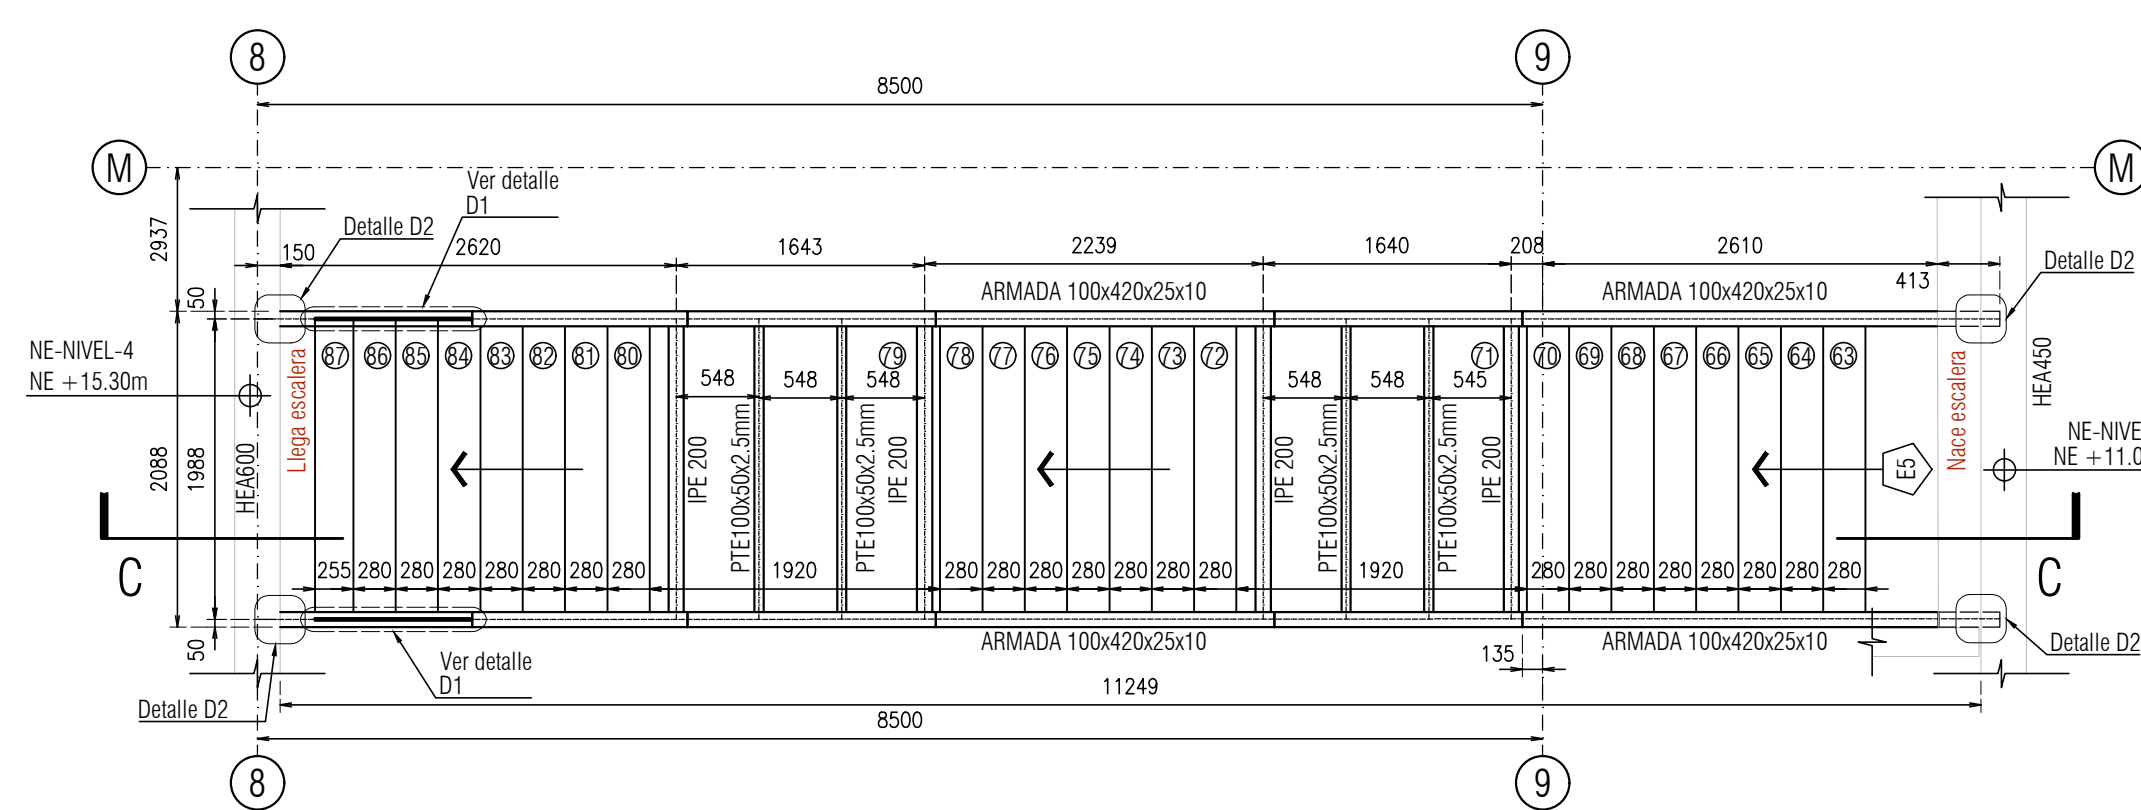


PLANTA ESCALERA E5
escala 1:50

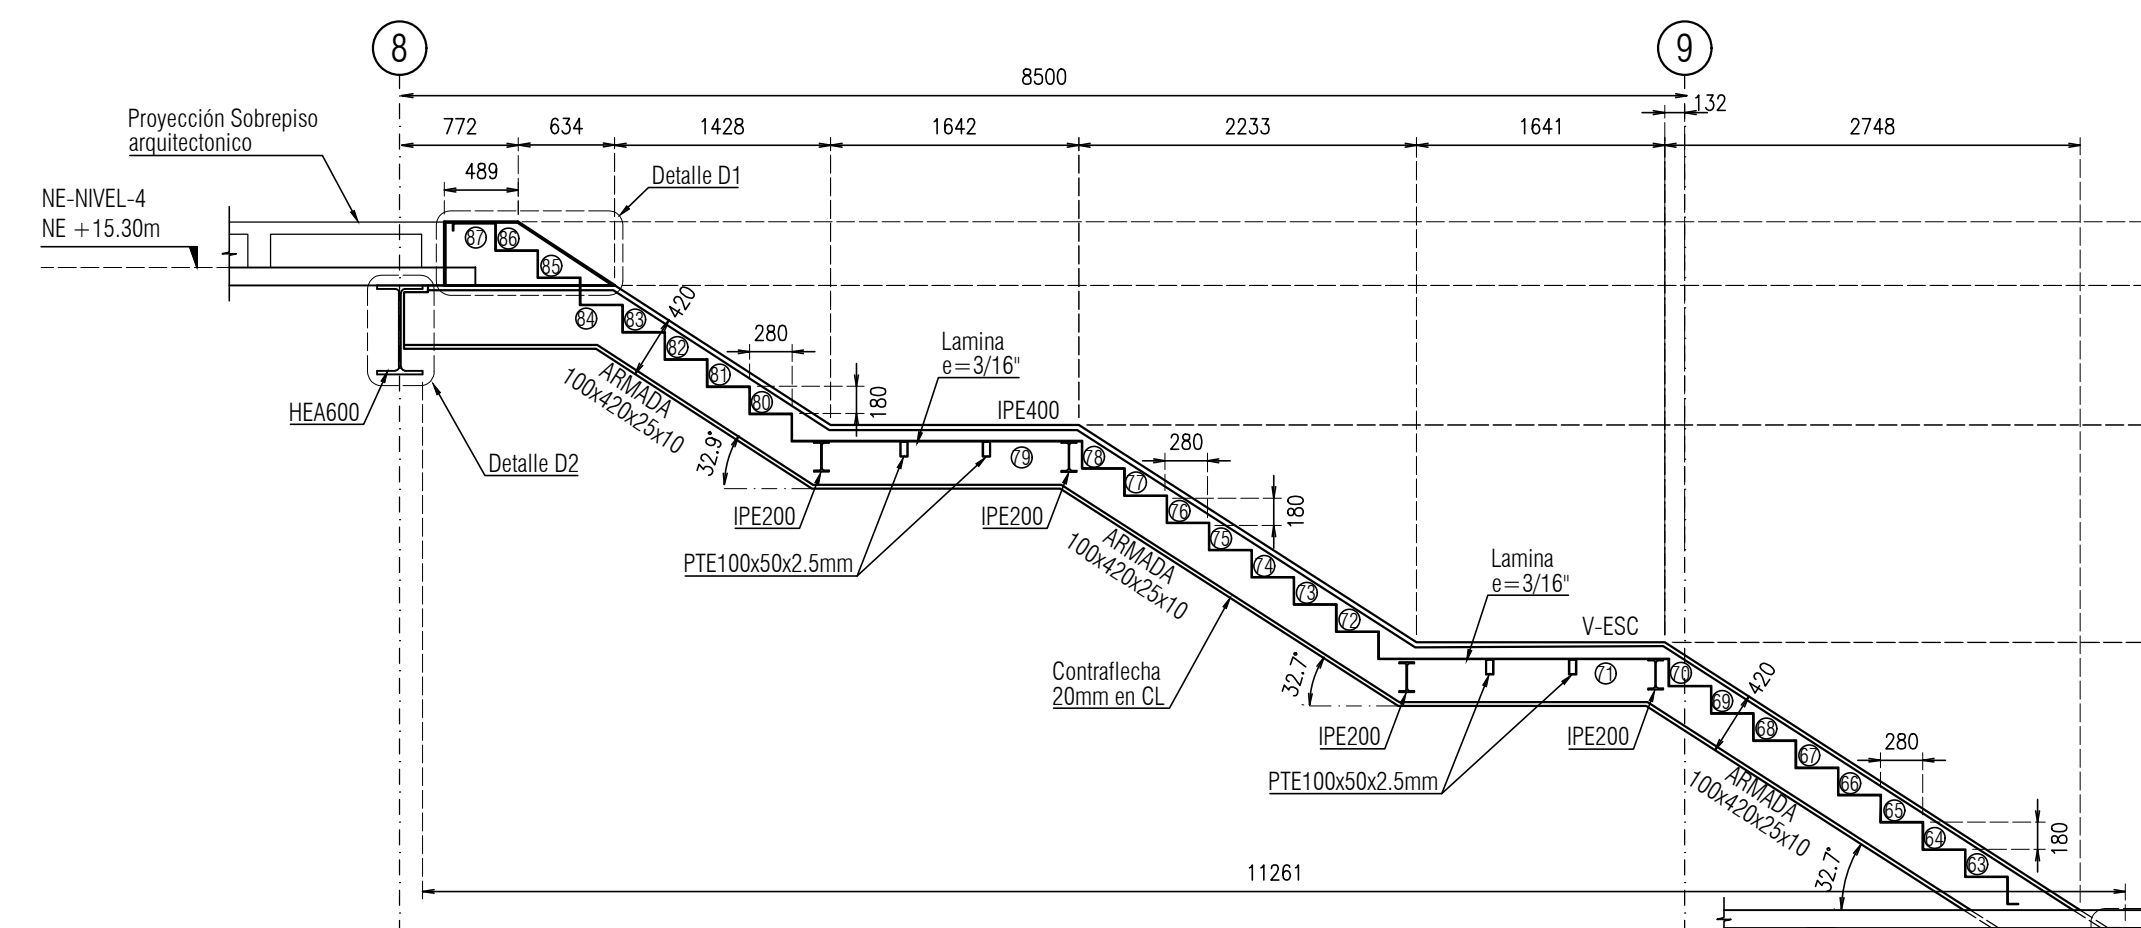


CORTE C - C ESCALERA E5
escala 1:50

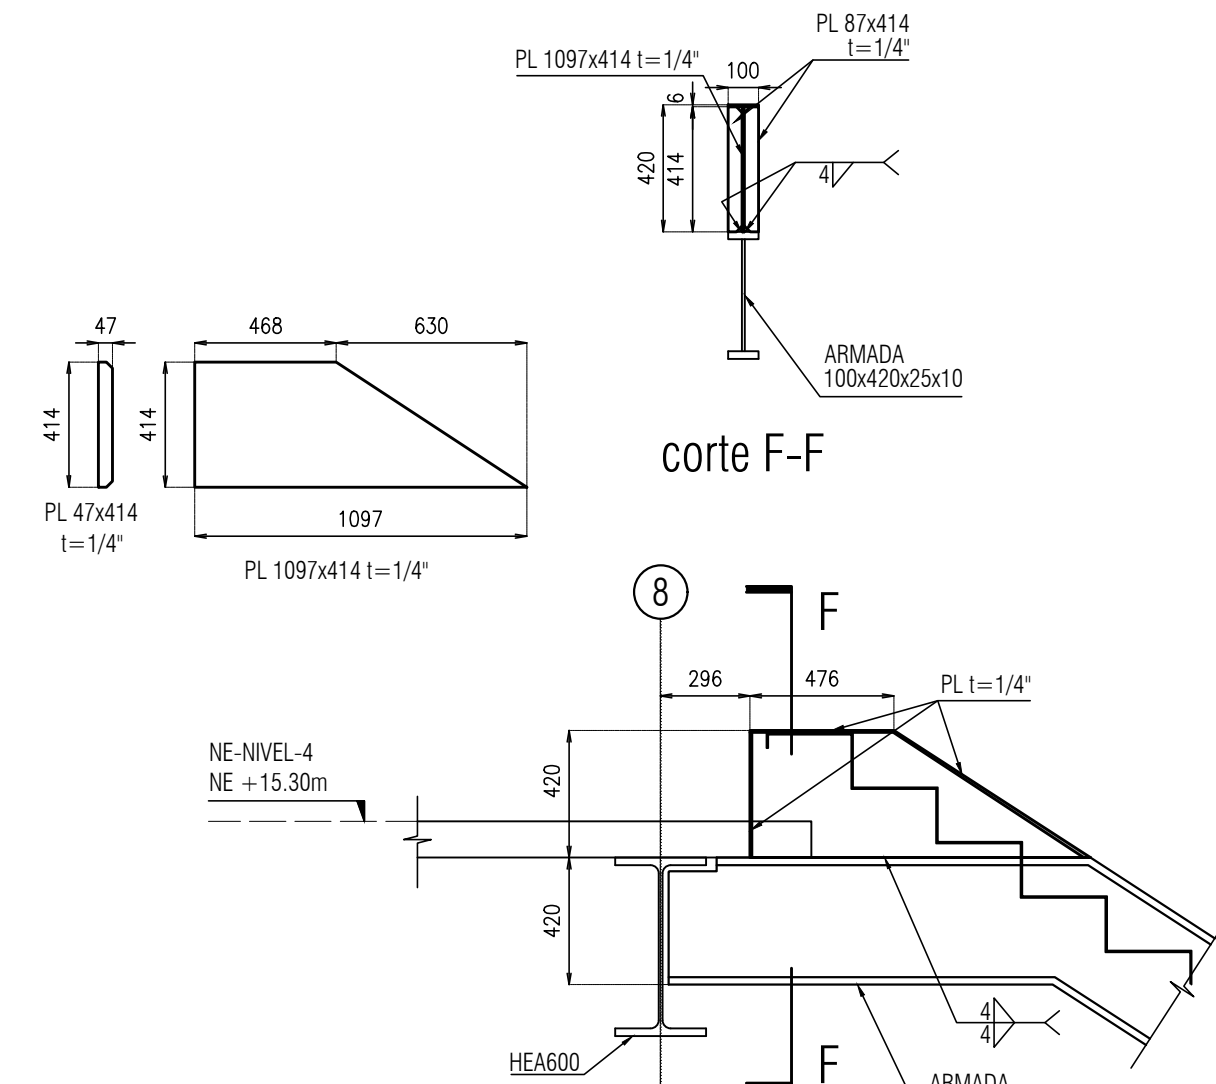


DETALLE D1
escala 1:25

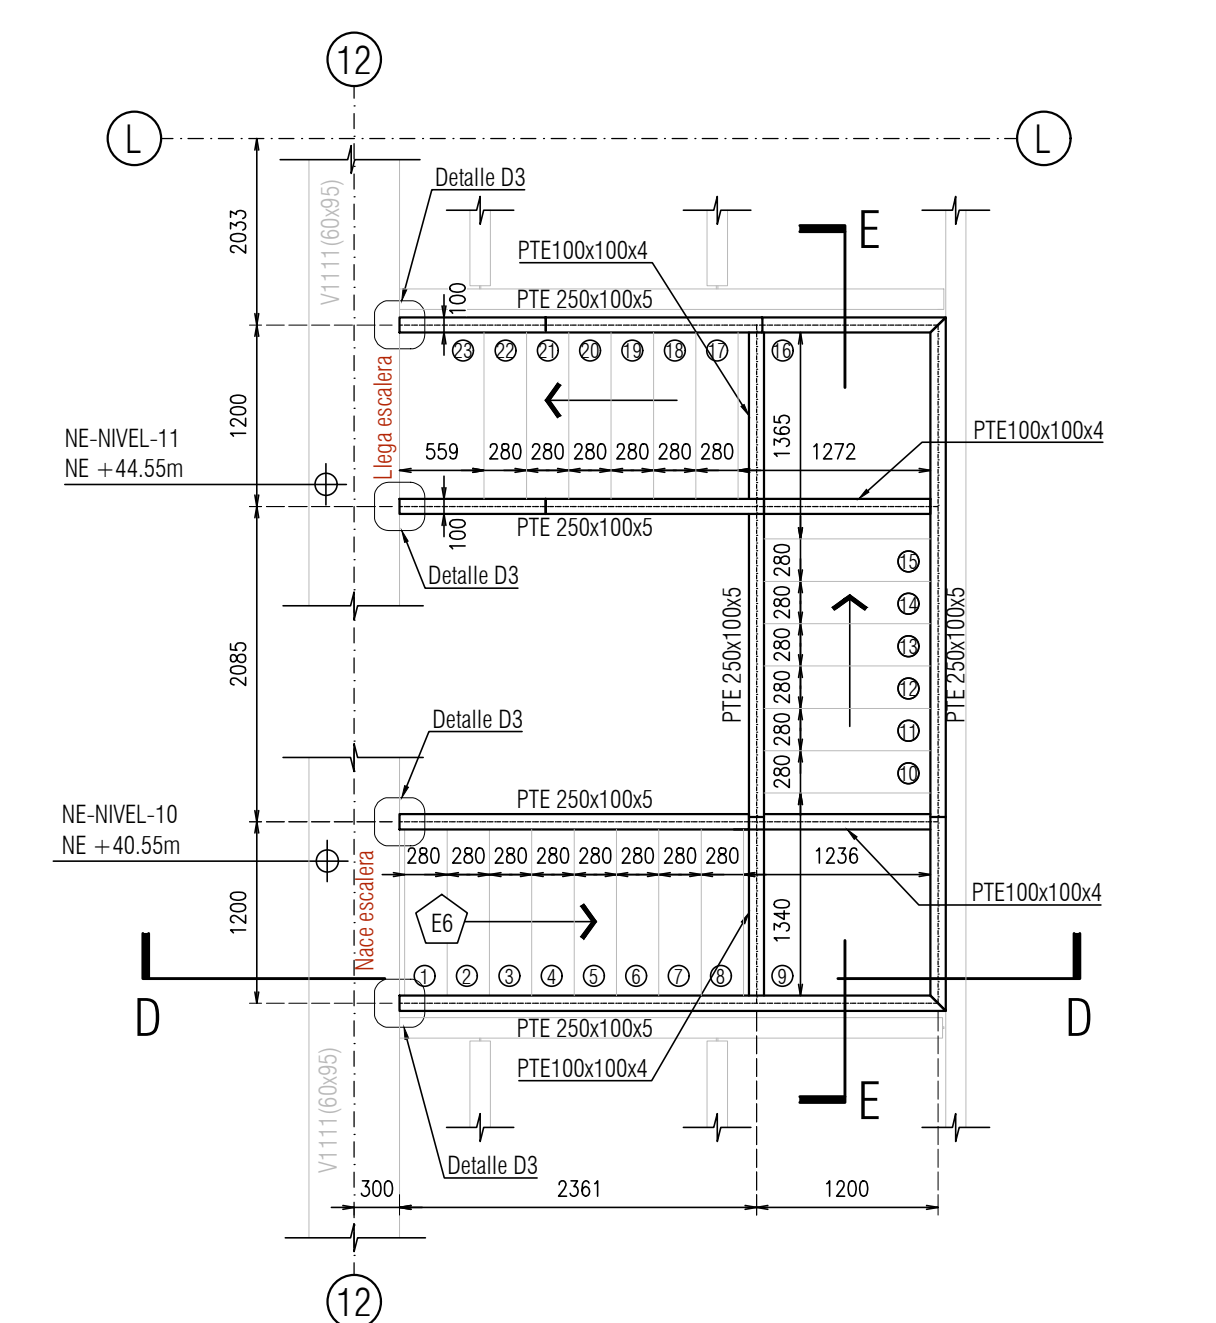


PLANTA ESCALERA E6
escala 1:50

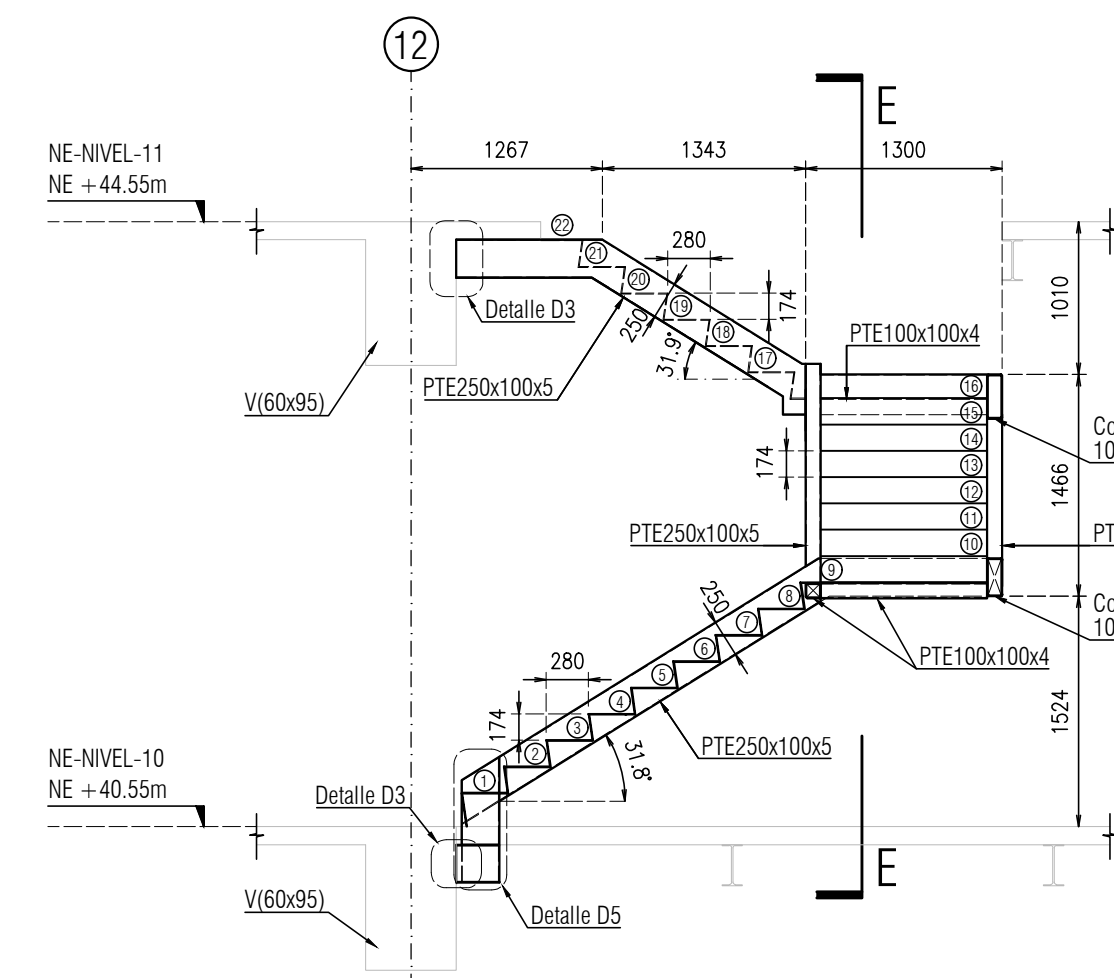


CORTE D - D ESCALERA E6
escala 1:50

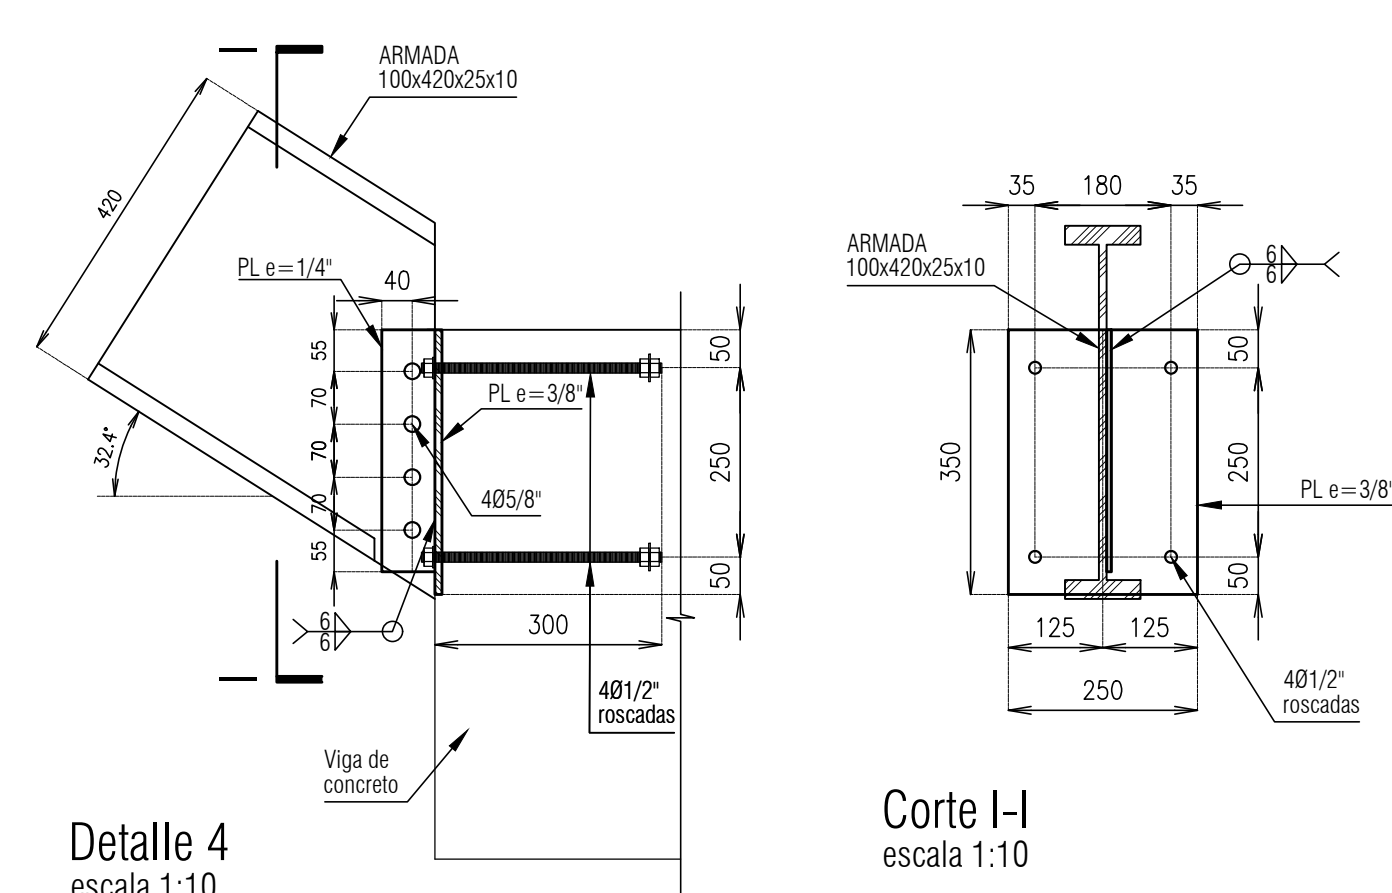

Detalle 4
escala 1:10

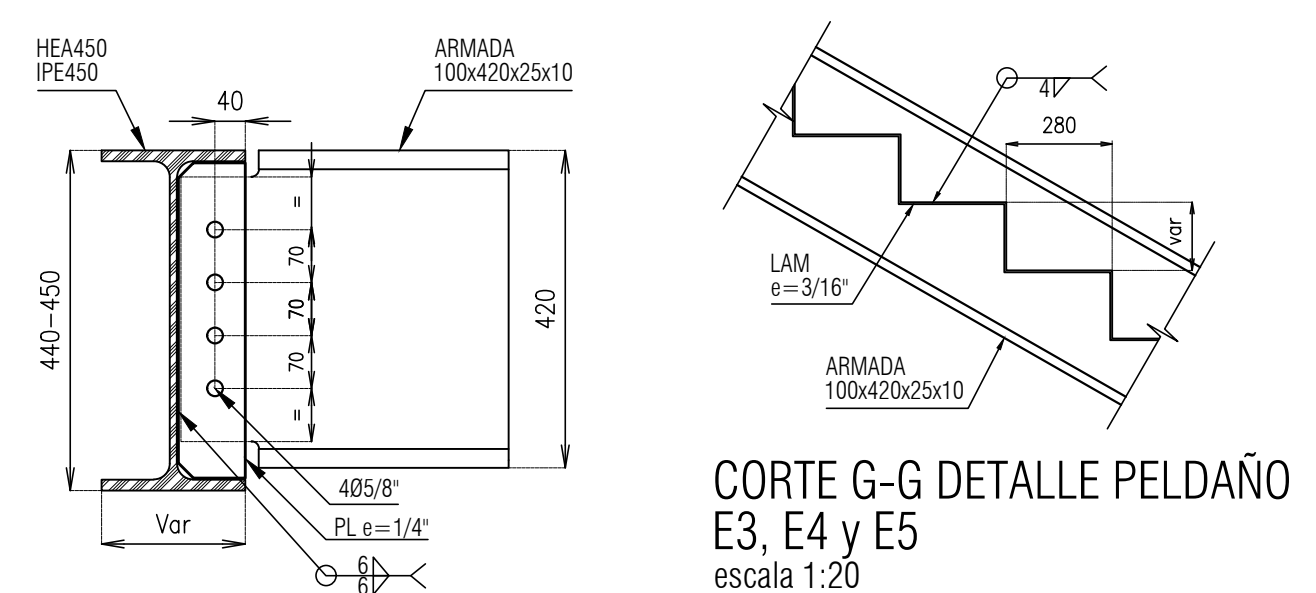


CORTE G-G DETALLE PELDAÑO
E3, E4 y E5
escala 1:20

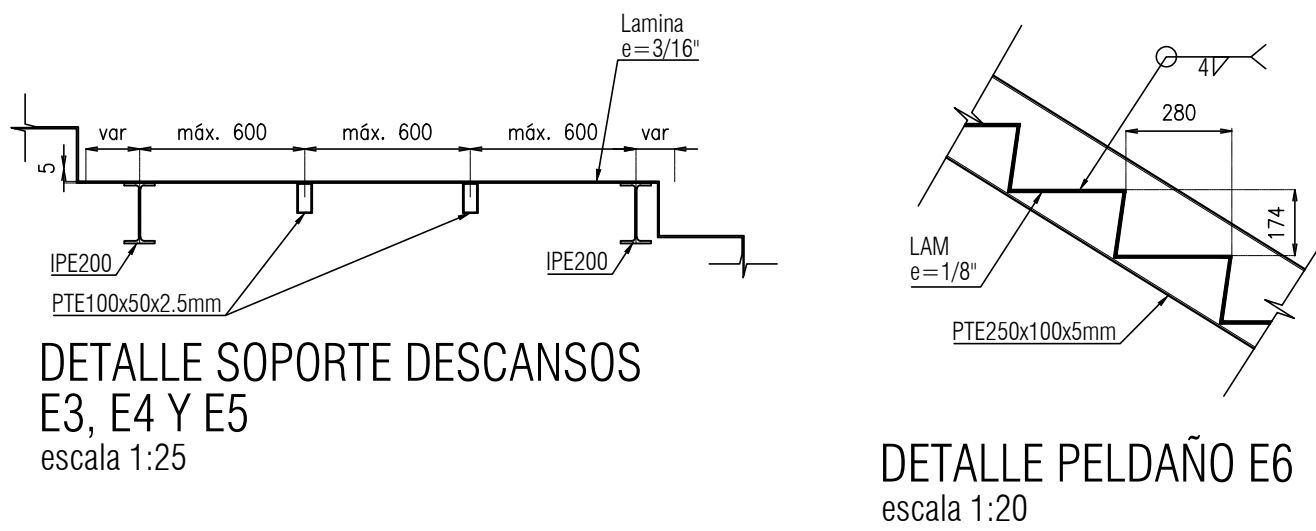


DETALLE SOPORTE DESCANSOS
E3, E4 y E5
escala 1:25

DETALLE PELDAÑO E6
escala 1:20


DETALLE SOPORTE DE PELDAÑOS
E3, E4 y E5
escala 1:25

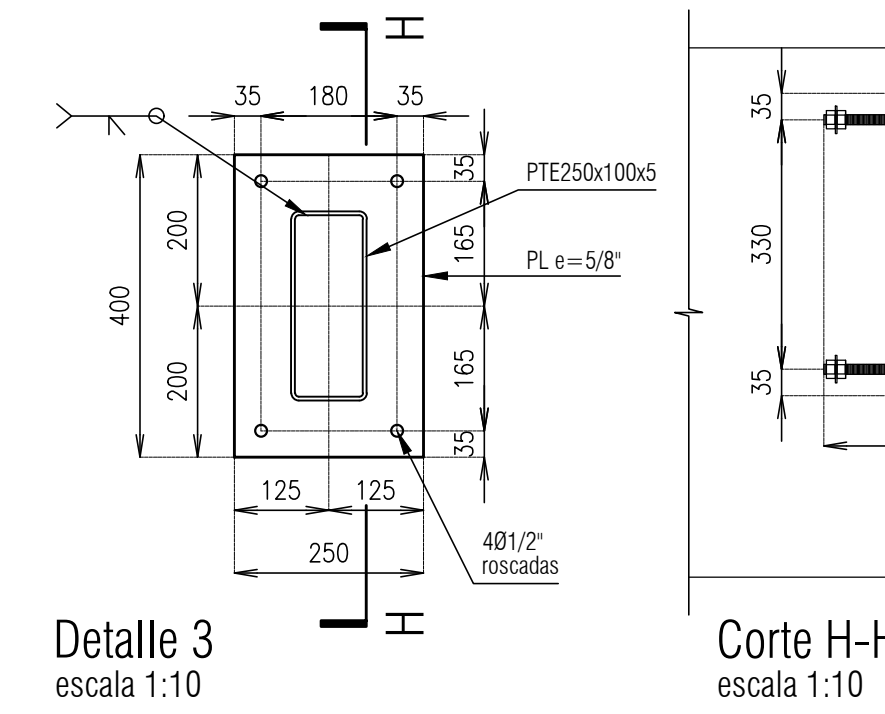


Detalle 3
escala 1:10

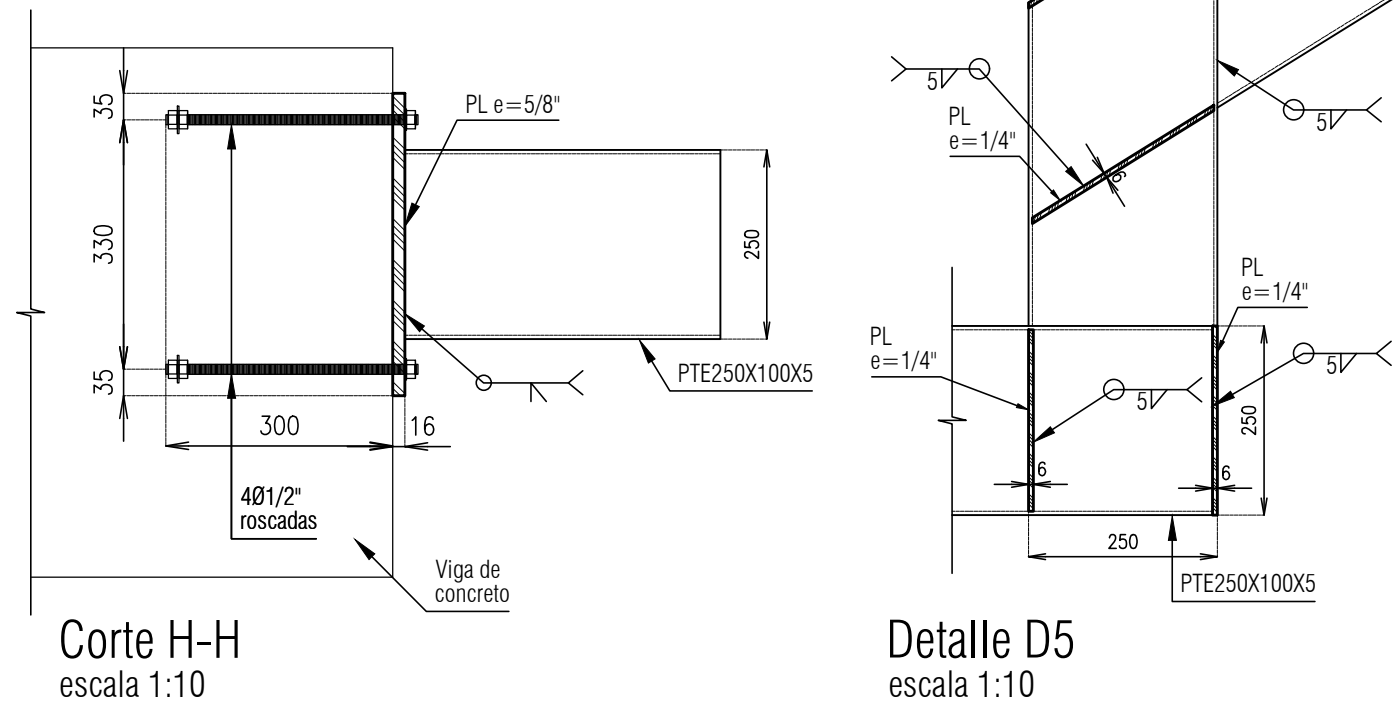

Corte H-H
escala 1:10

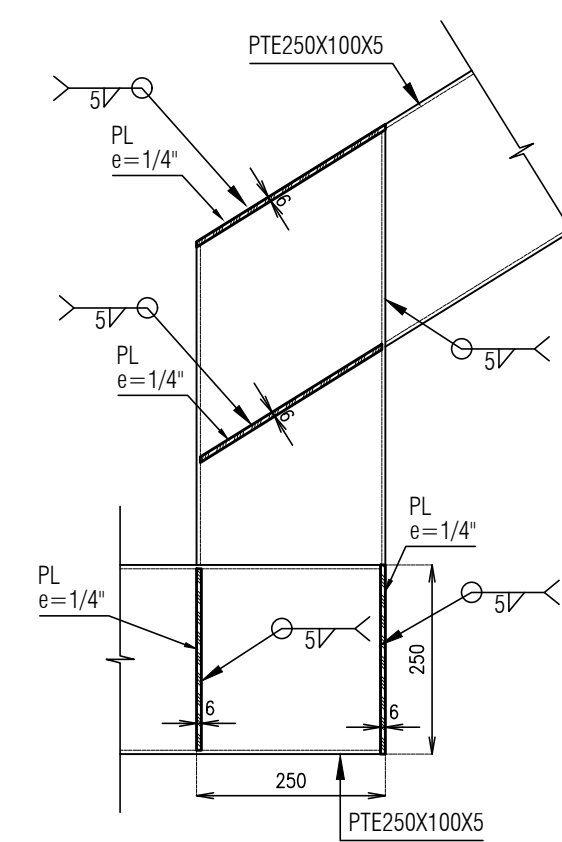

Detalle D5
escala 1:10

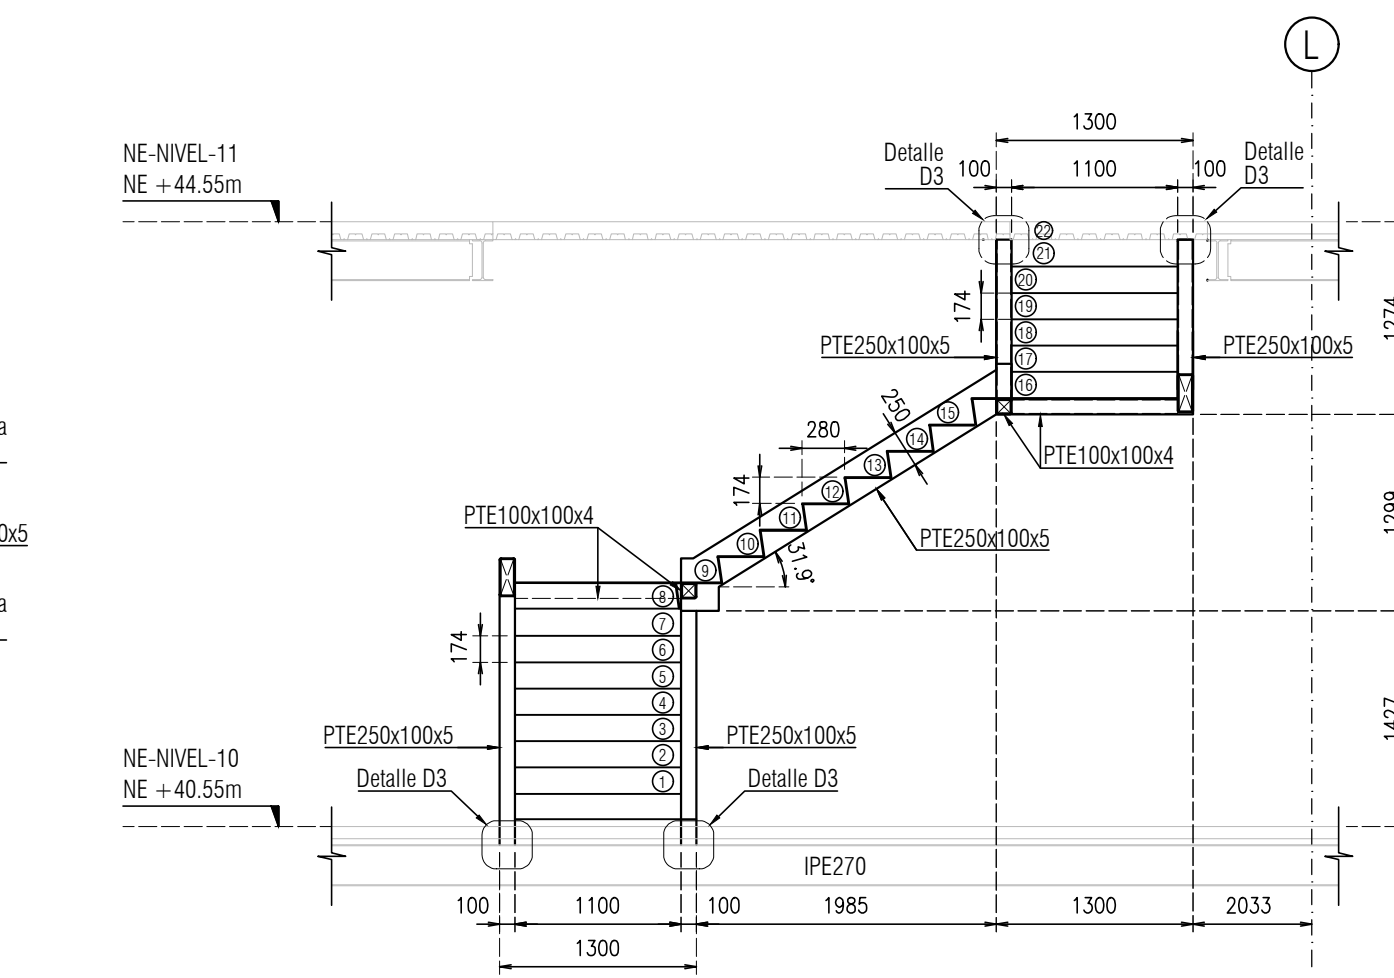

CORTE E - E ESCALERA E6
escala 1:50

ARQUITECTO COORDINADOR

EL EQUIPO MAZZANTI + Gensler

DISÑO ESTRUCTURAL



Ing. Nicolás Parra García

DISEÑADOR ING. NICOLÁS PARRA GARCÍA
MAT. 23021 148063 CND

INTERVENTORIA



Director de Interventoría: Ing. Jorge Iván García Mancilla
Mat. 632021 148063 CND

Versión	Emisión	Descripción
AA	15-06-2023	Ingeniería básica
AB	04-08-2023	Anteproyecto
AC	01-11-2023	Anteproyecto V2 50%
AD	15-12-2023	Anteproyecto V2 100%
DD	13-03-2024	Entrega curaduría
EE	10-05-2024	Proyecto Final 100%
EF	31-05-2024	Respuesta Obs 100%
FF	21-06-2024	Entrega Final
01	28-07-2024	ENTREGA FINAL


PROYECTO:
CAMPUS DE CIENCIA TECNOLOGÍA E
INNOVACIÓN DE BOGOTÁ
MAT. No. 502-00252410

FASE
ENTREGA FINAL

PROPÓSITO DE EMISIÓN
Curaduría ☐ Coordinación ☐
Revisión ☐ Construcción ☐
Entrega Cliente ☒

ZONIFICACION
Nivel 24
Nivel 23
Nivel 22
Nivel 21
Nivel 20
Nivel 19
Nivel 18
Nivel 17
Nivel 16
Nivel 15
Nivel 14
Nivel 13
Nivel 12
Nivel 11
Nivel 10
Nivel 9
Nivel 8
Nivel 7
Nivel 6
Nivel 5
Nivel 4
Nivel 3
Nivel 2
Nivel 1
Nivel 0

PROYECTO
DETALLADO
APTO PARA
CONSTRUCCIÓN
(APC)

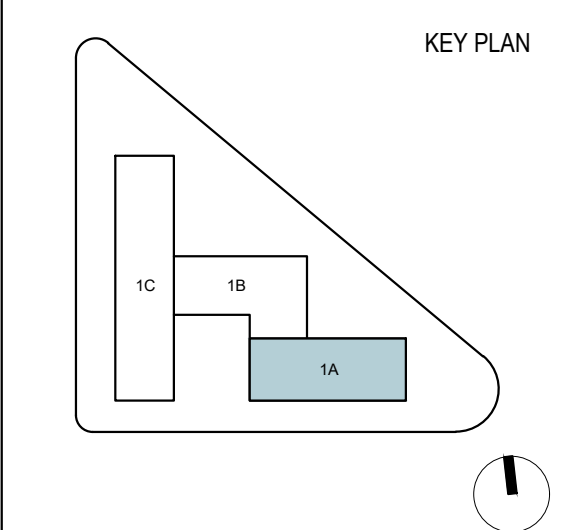

Fecha: 28-07-2024

Escala: As Indicated

DETALLES DE
ESCALERAS
CTIB_CNI_EST_508_DET_XXX_01