




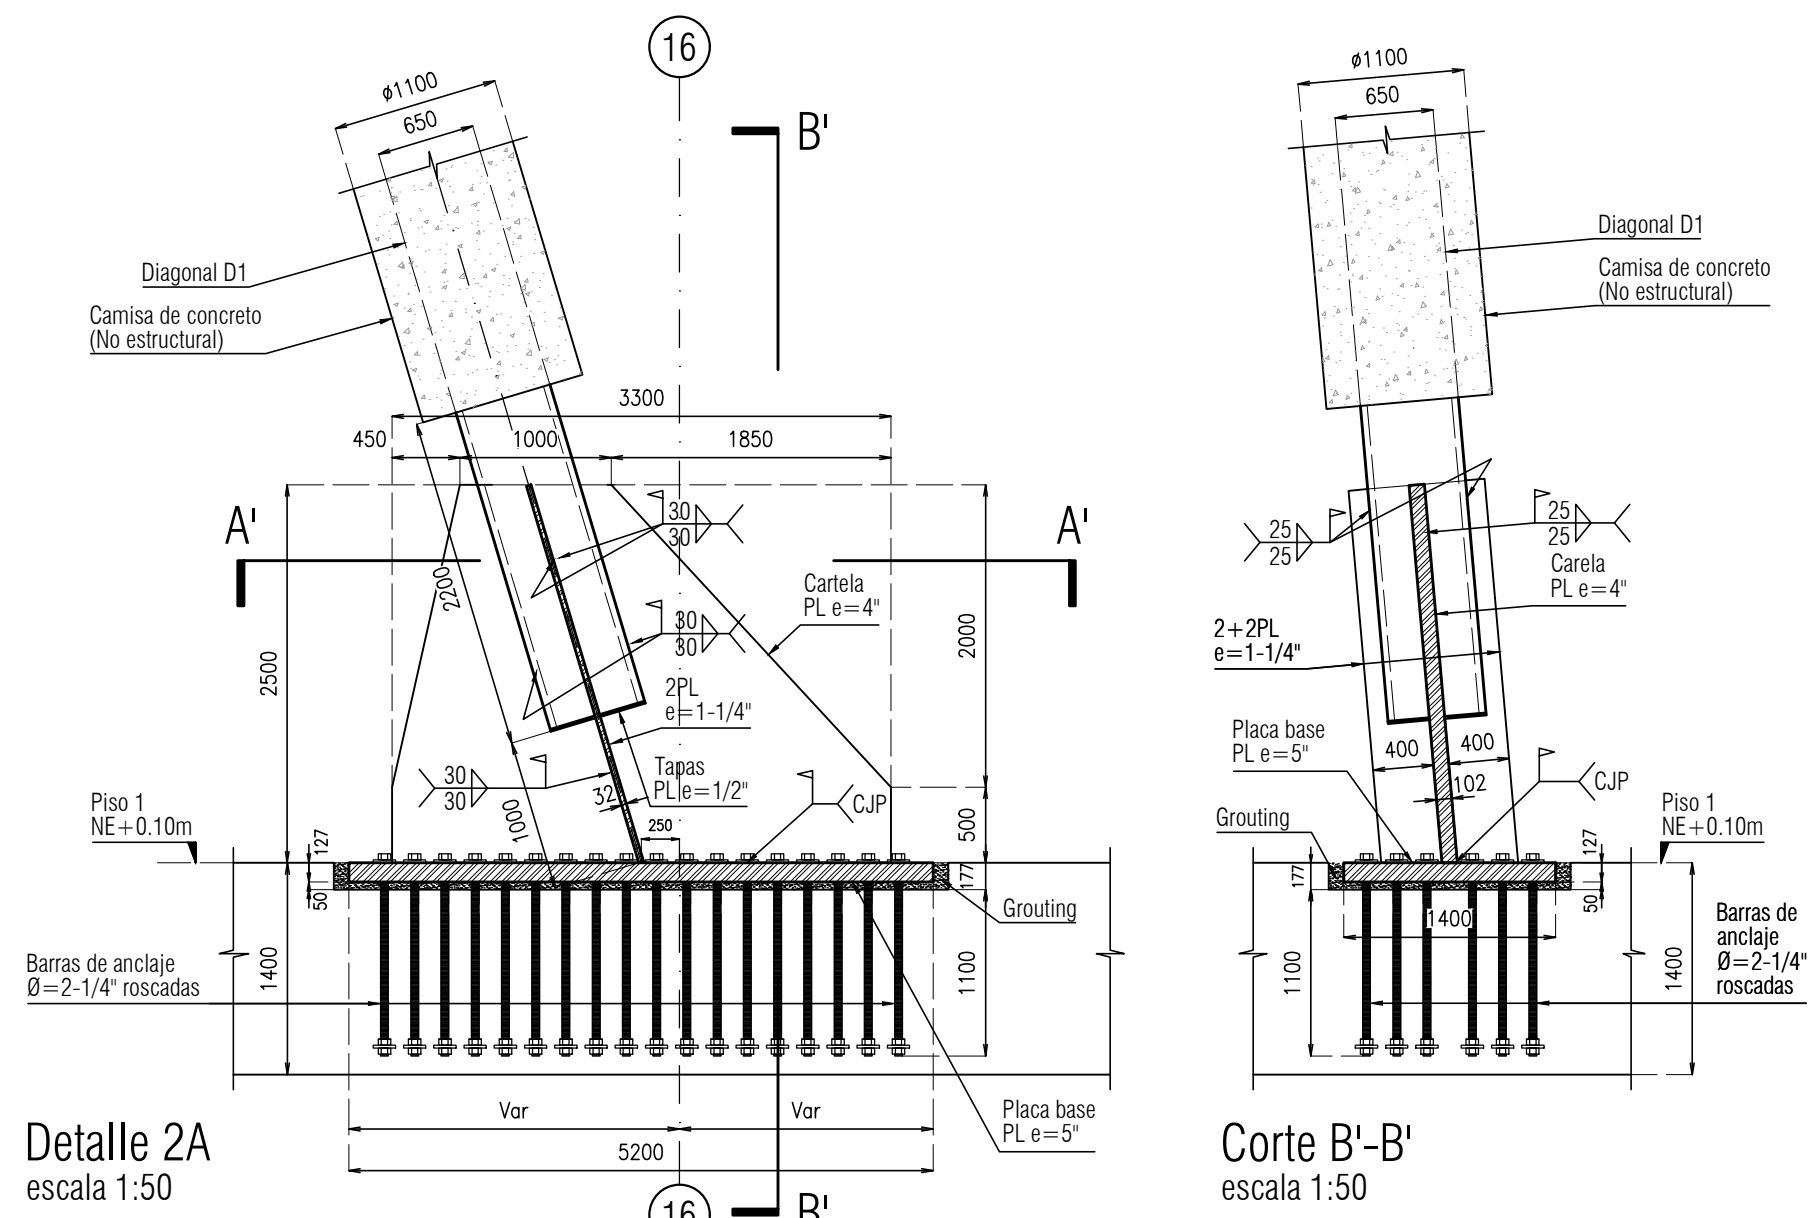


Detalle 2A
escala 1:50

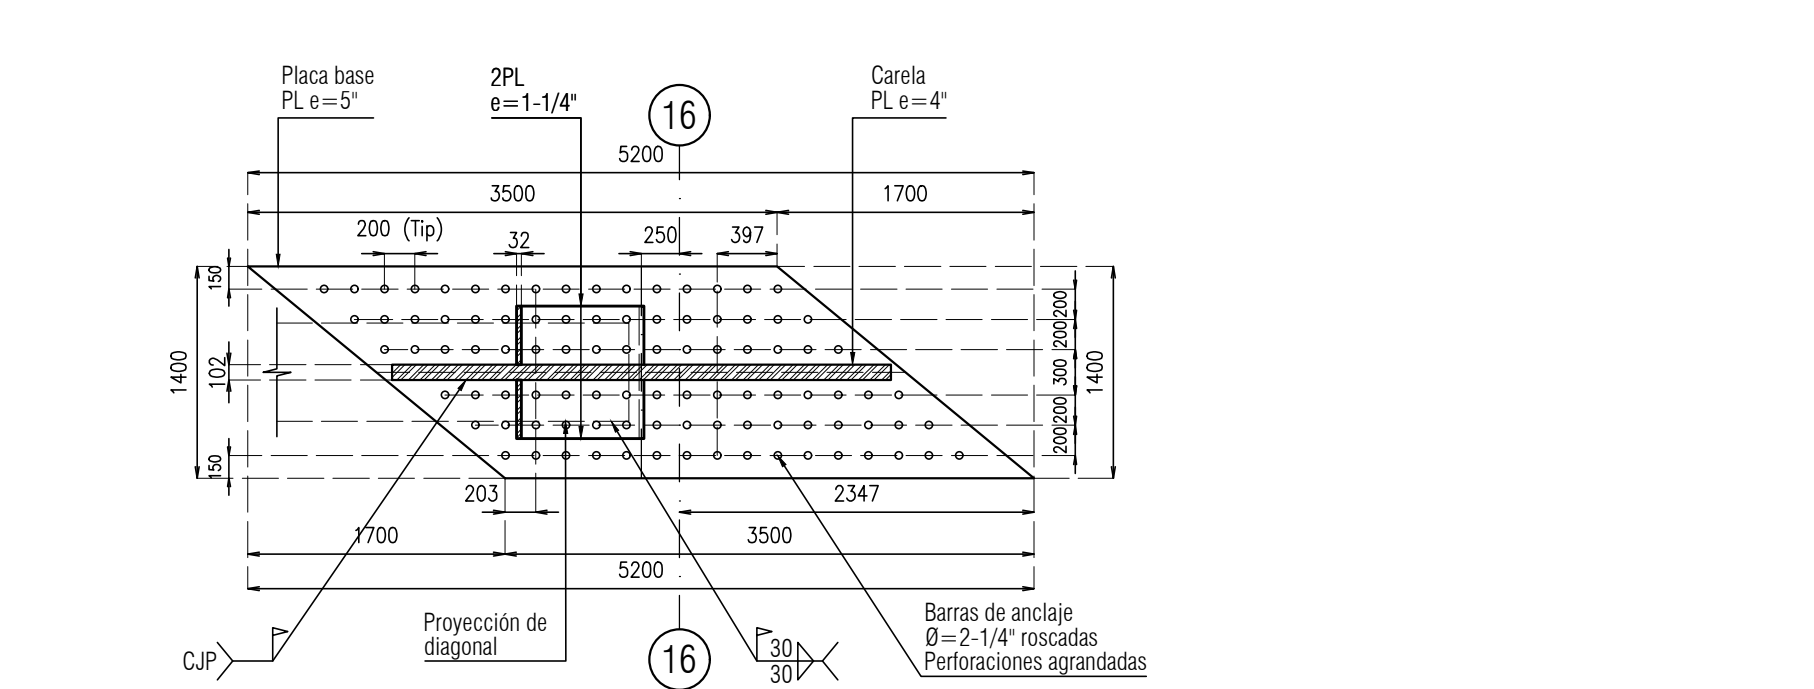

Detalle 2B
escala 1:50

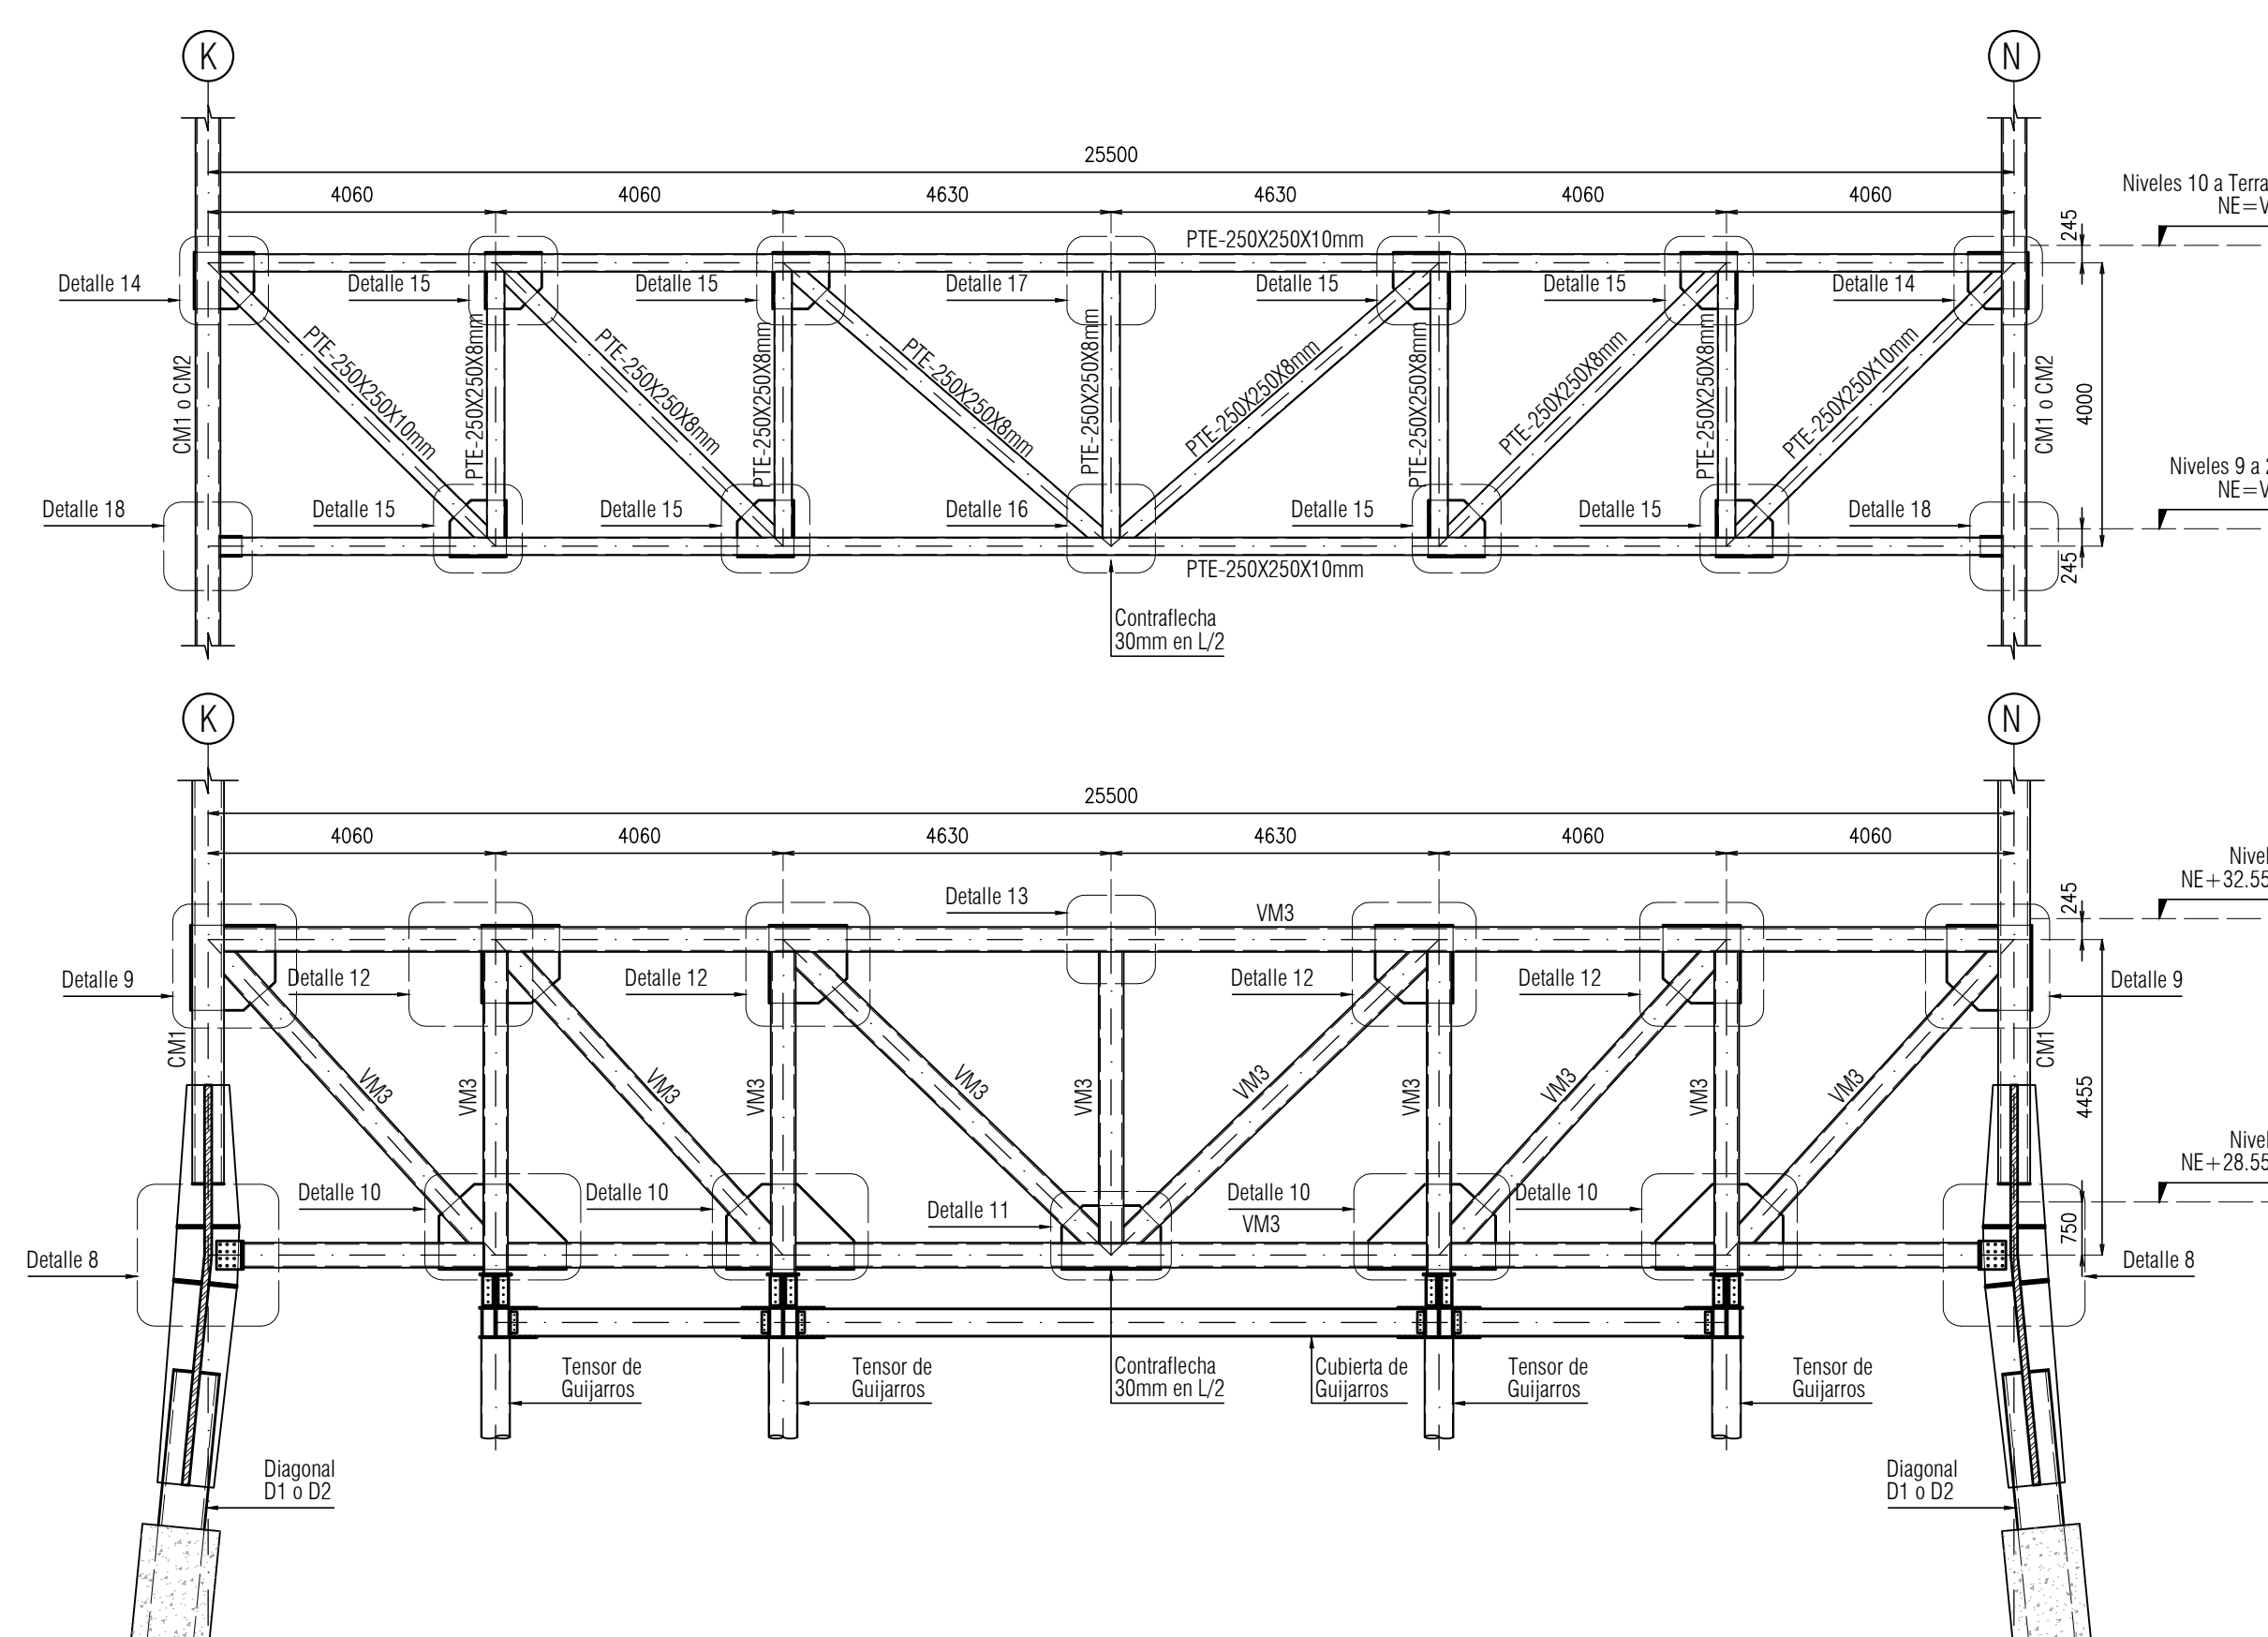

ALZADO CERCHAS DE FACHADA EJES 7 Y 15
escala 1:100

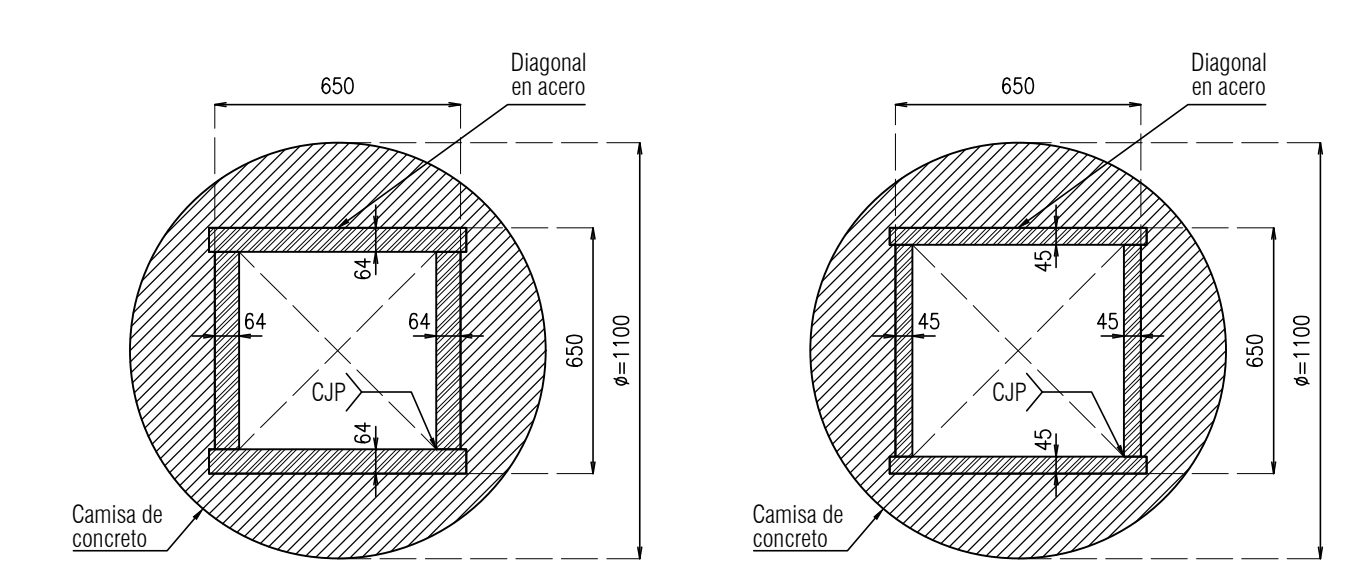

SECCION DIAGONAL D1
escala 1:20

SECCION DIAGONAL D2
escala 1:20

SECCION DIAGONAL D3
escala 1:20

SECCION DIAGONAL D4
escala 1:20

SECCION COLUMNA CM1
escala 1:20

SECCION COLUMNA CM2
escala 1:20


SECCION VIGA VM1
escala 1:20

SECCION VIGA VM2
escala 1:20

SECCION VIGA VM3
escala 1:20

PTE-250X250X8
escala 1:20


PTE-250X250X10
escala 1:20

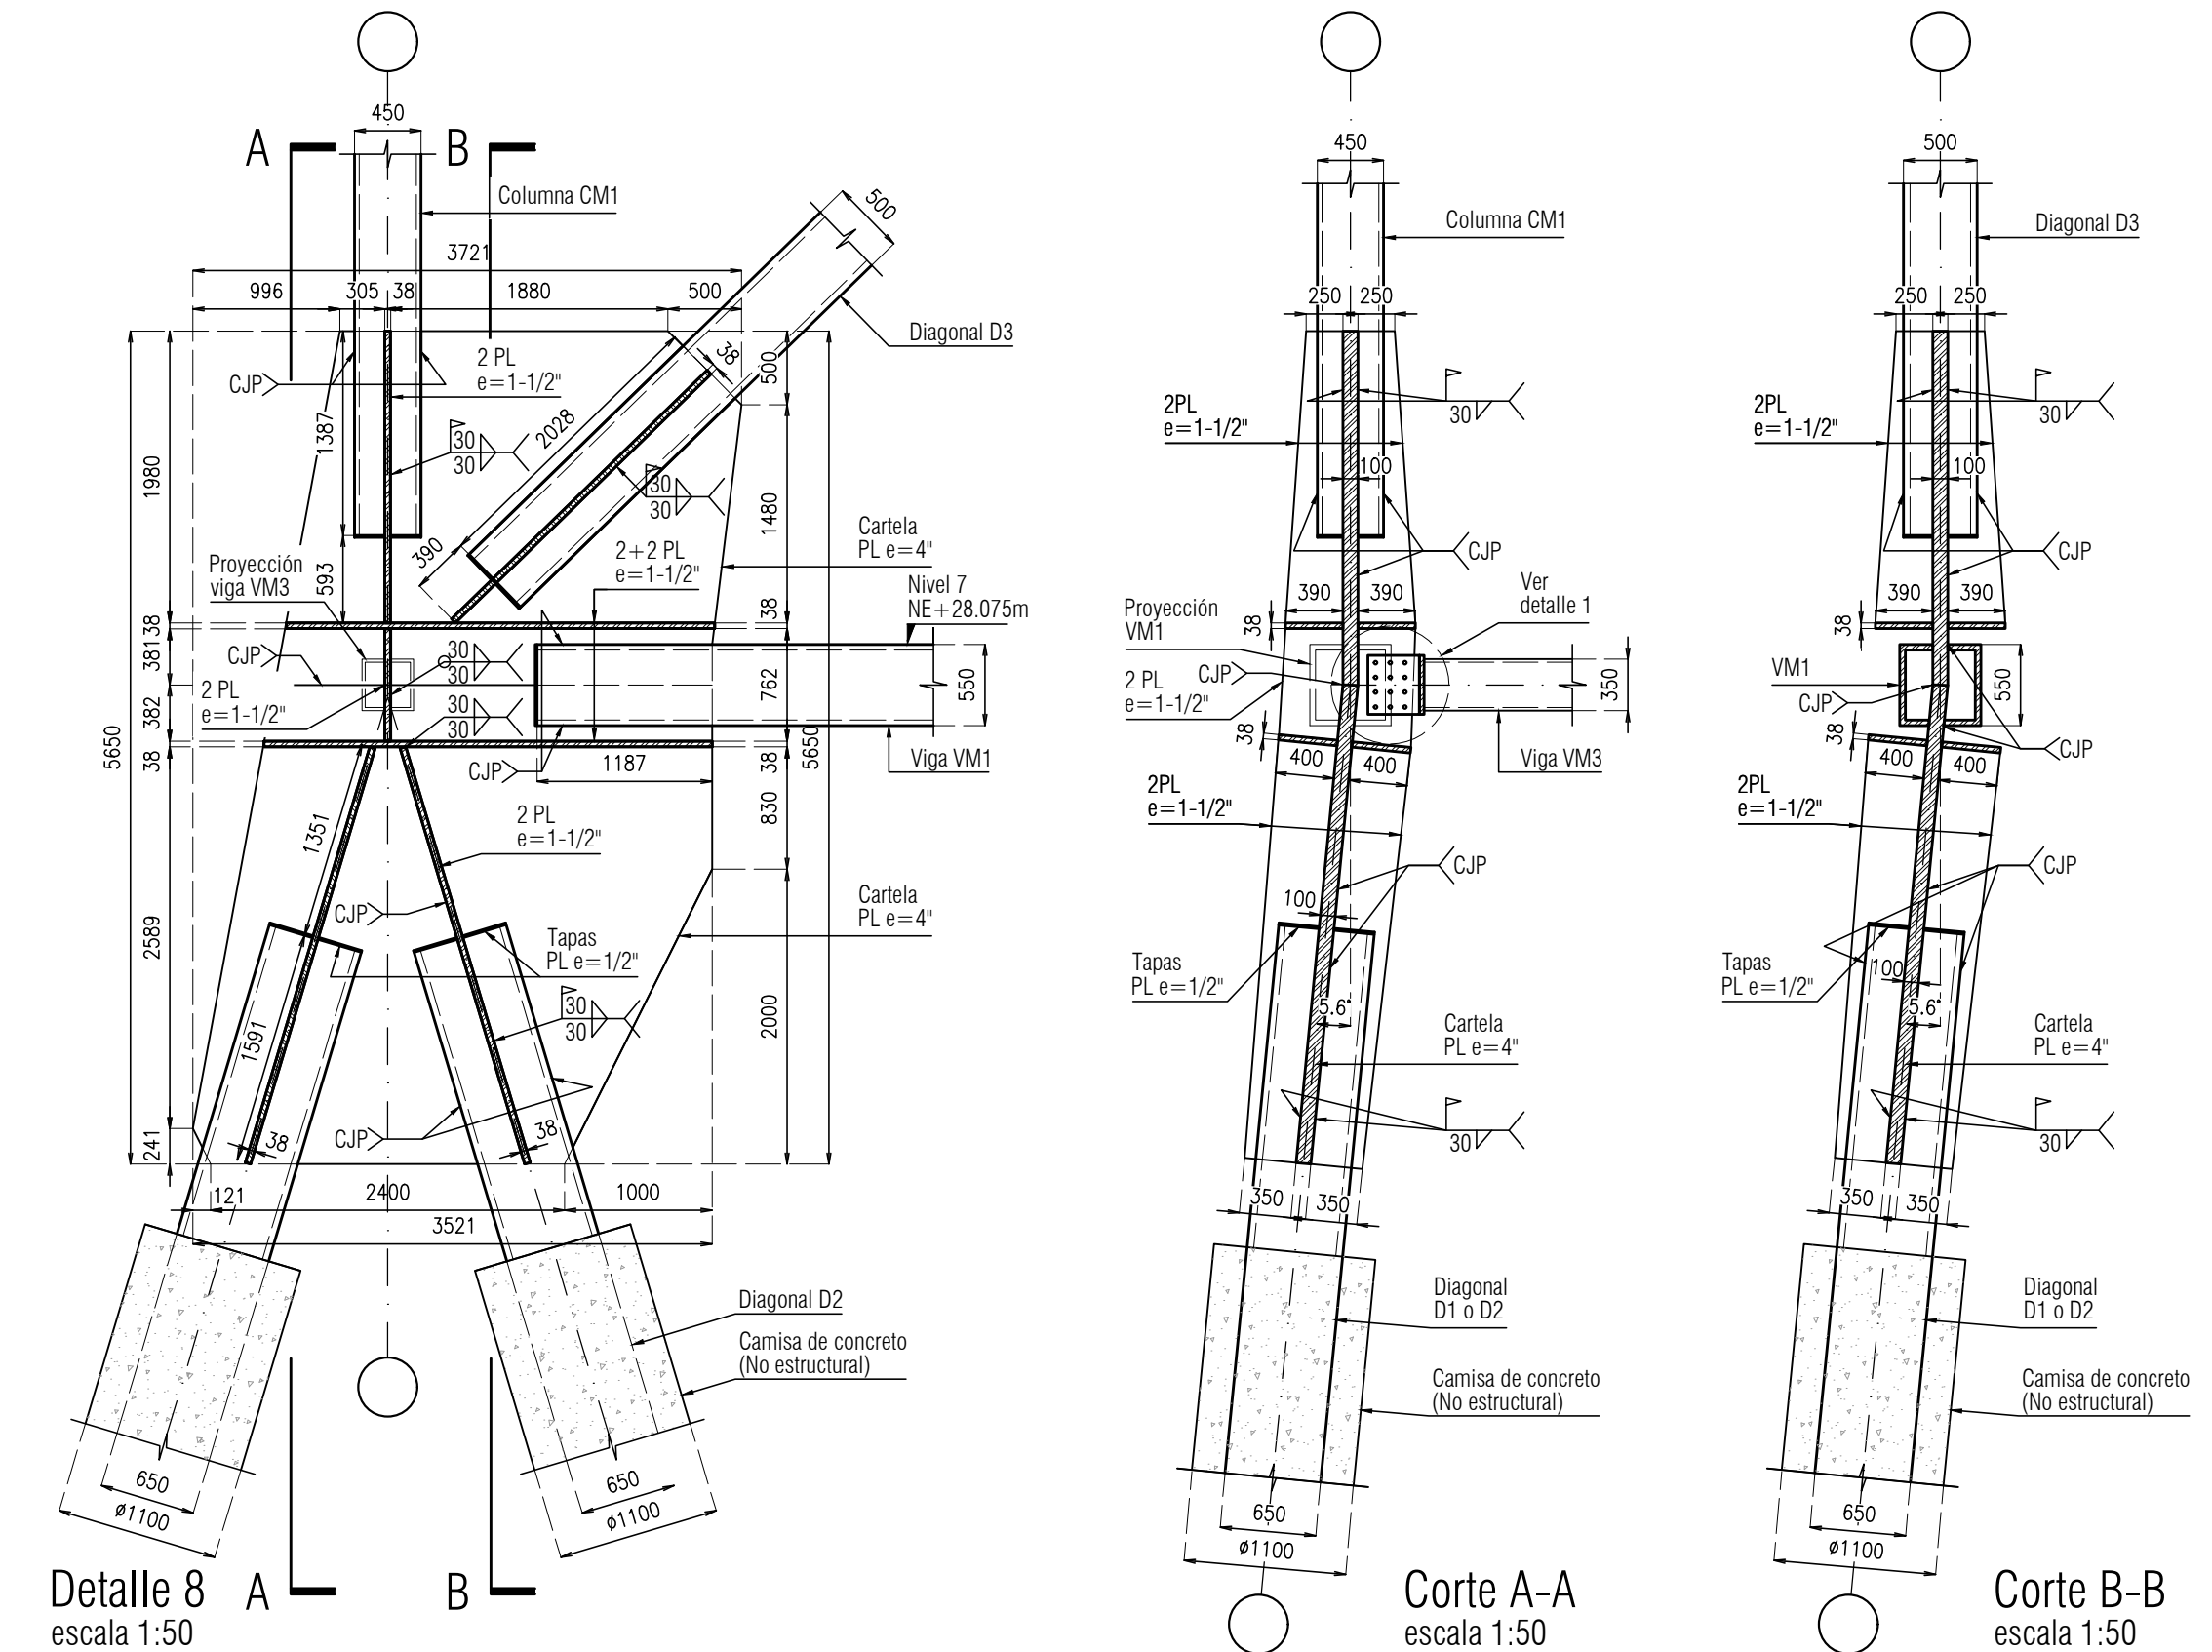

Detalle 8
escala 1:50


Corte A-A
escala 1:50

Corte B-B
escala 1:50

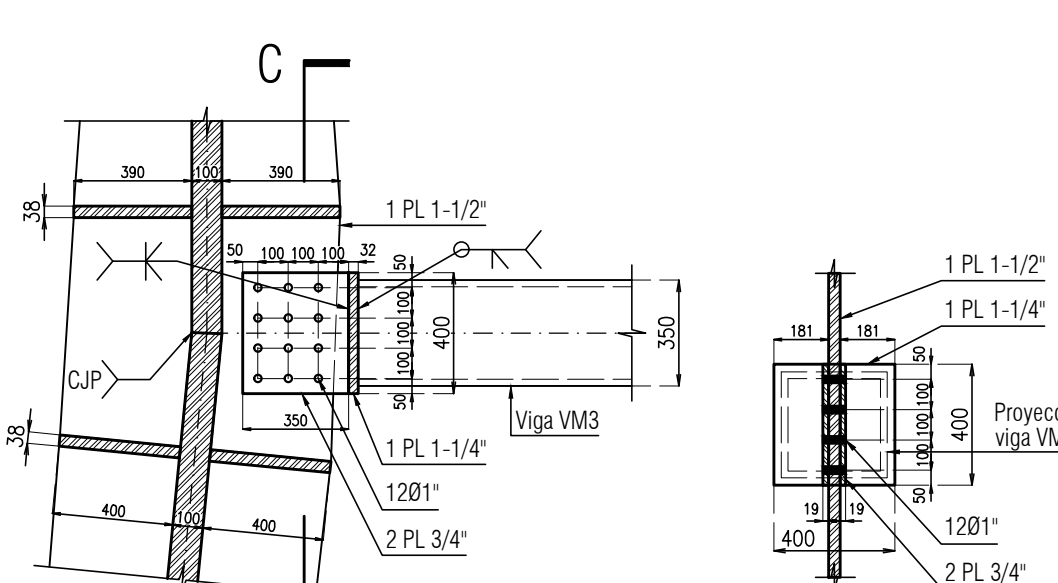


Detalle 1
escala 1:25


Corte C-C
escala 1:25

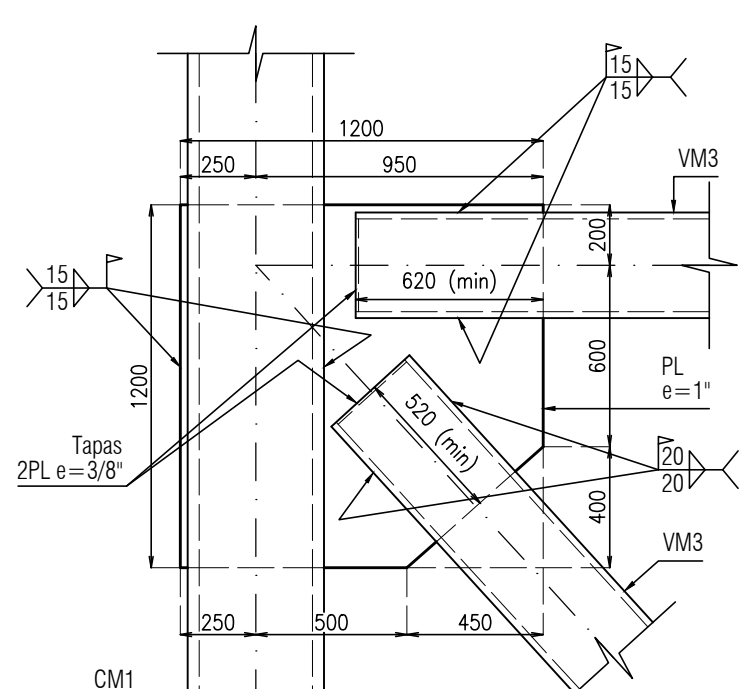


Detalle 9
escala 1:25

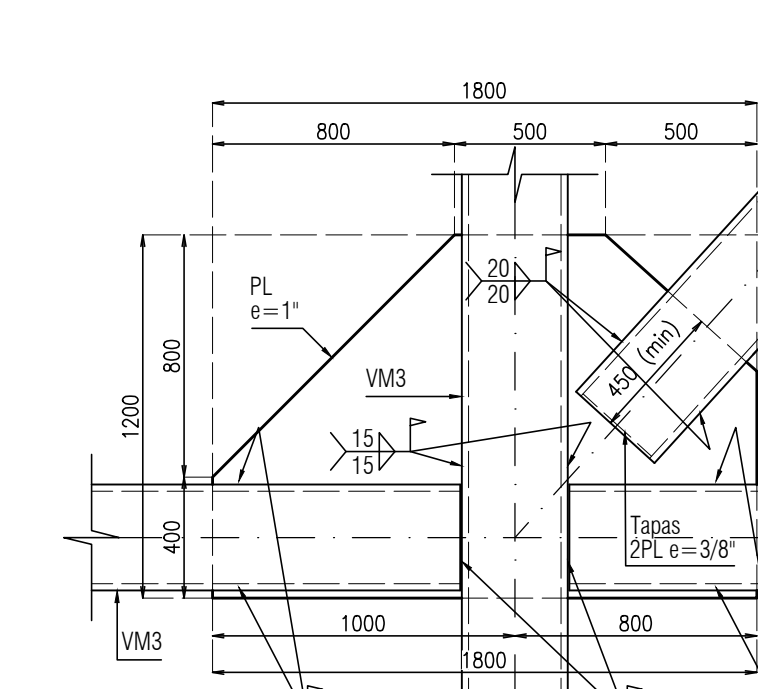


Detalle 10
escala 1:25

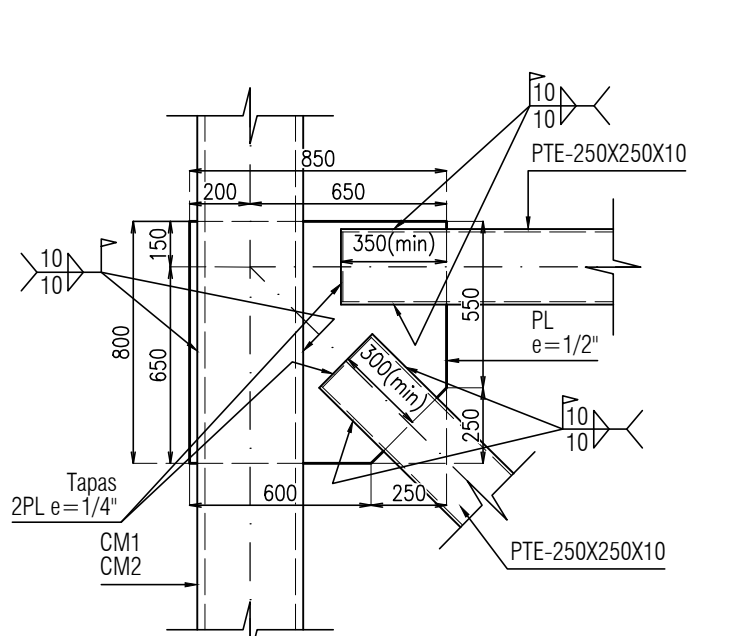

Detalle 14
escala 1:25

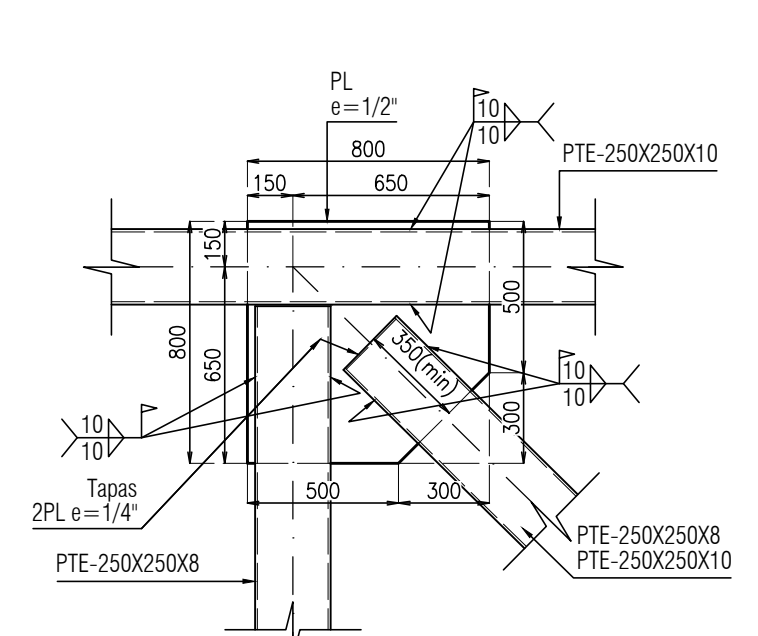


Detalle 15
escala 1:25

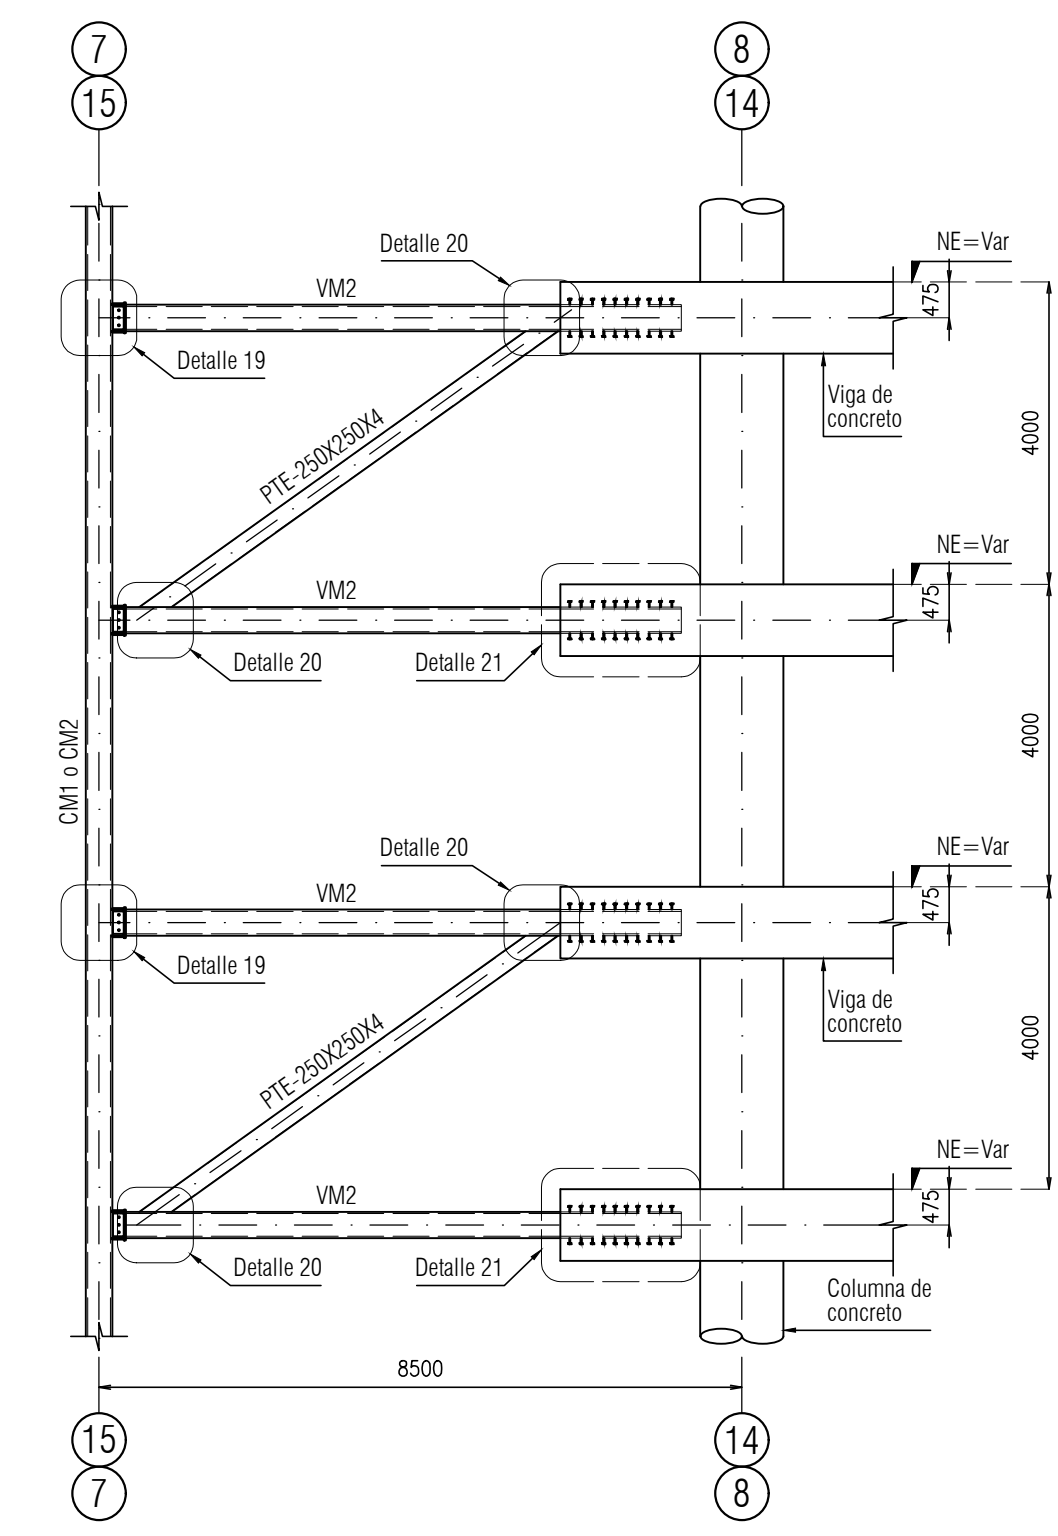

ALZADO FACHADA EJES K Y N
escala 1:100


Detalle 16
escala 1:25

Detalle 17
escala 1:25

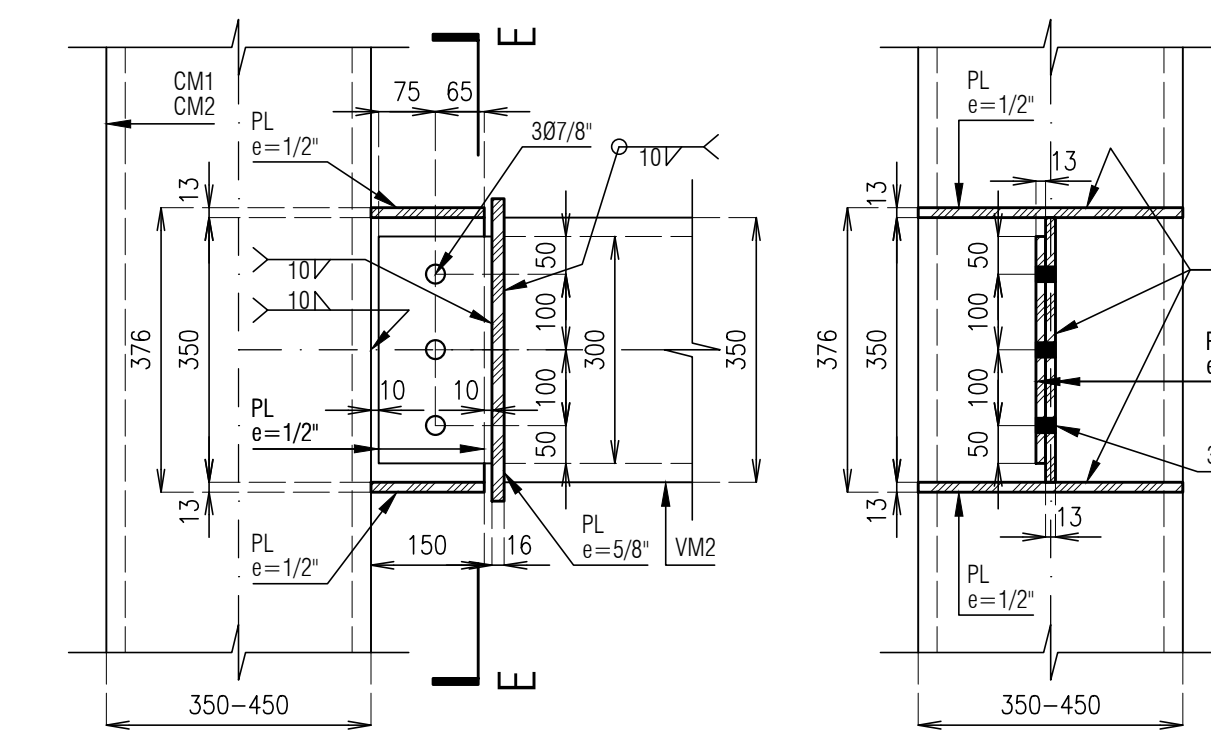


Detalle 19
escala 1:10

Corte E-E
escala 1:10

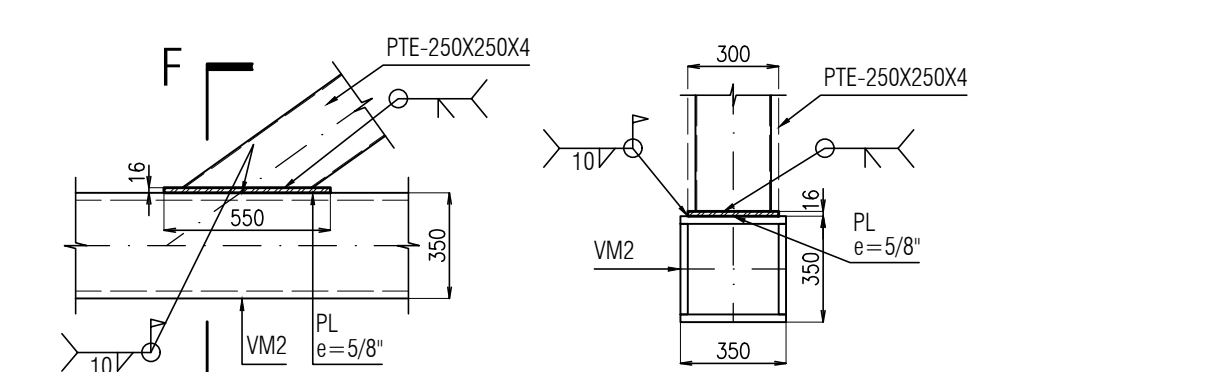


Detalle 20
escala 1:25

Corte F-F
escala 1:25

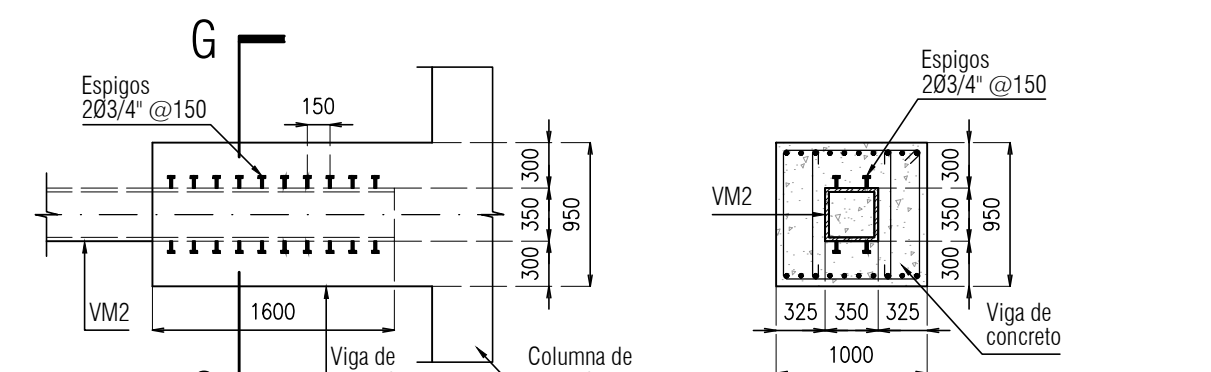


Detalle 21
escala 1:50

Corte G-G
escala 1:50

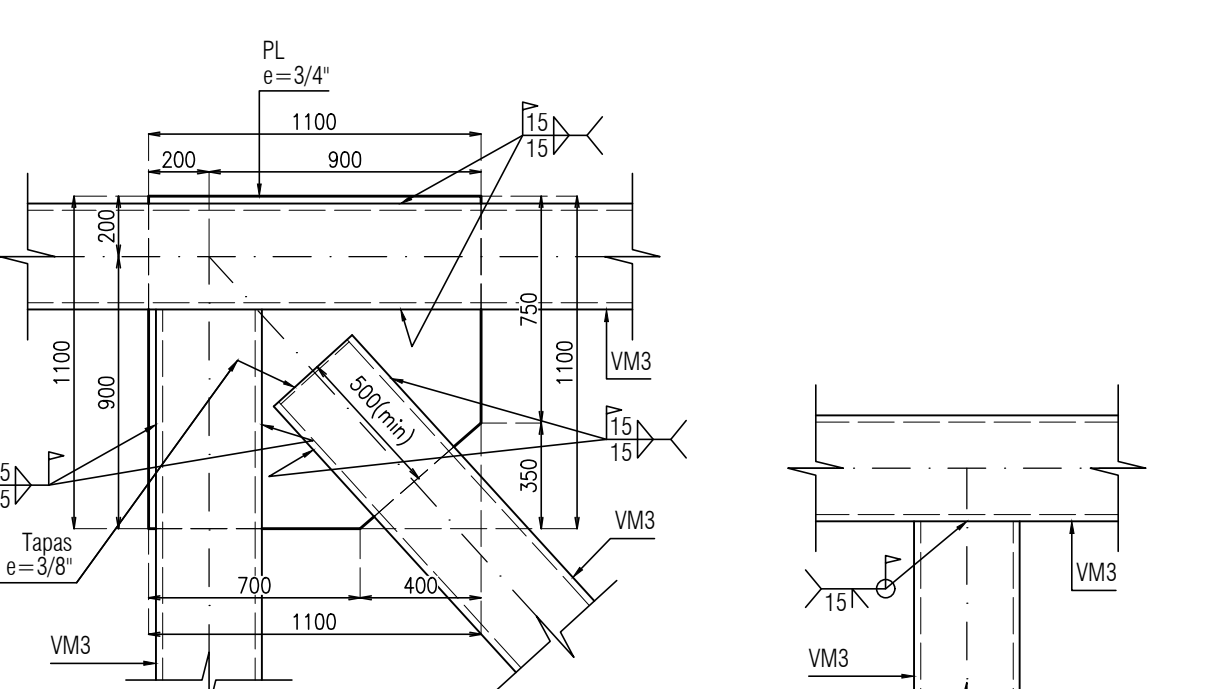

Detalle 12
escala 1:25

Detalle 13
escala 1:25

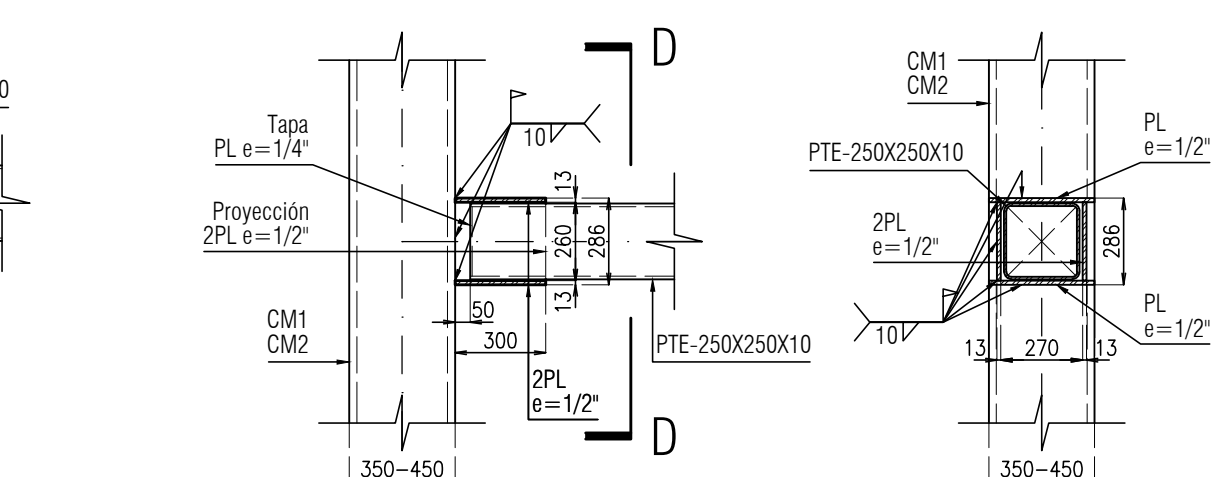

Detalle 18
escala 1:25

Corte D-D
escala 1:25

NOTAS IMPORTANTES:

- Ver especificaciones de materiales en plano CTIB_CNI_EST_000_GEN_XXX
- Los presentes planos son de diseño. El fabricante de la estructura metálica debe elaborar los respectivos planos de taller, los cuales deben ser revisados y aprobados por la interventoría y la supervisión técnica de la obra.
- En los detalles se indican cantidad y diámetro de pernos de conexión.

CTIB

Campus de Ciencia, Tecnología e Innovación de Bogotá - Región

corferias

Generadores de Oportunidades y Progreso

Cámara de Comercio de Bogotá

BOGOTÁ

ARQUITECTO COORDINADOR

EL EQUIPO MAZZANTI + Gensler

DISEÑO ESTRUCTURAL

CNI

DISEÑADOR

ING. NICOLÁS PARRA GARCÍA

INTERVENTORIA

GUTIERREZ DÍAZ S.A.S.

Director de Interventoría:

Ing. Jorge Iván García Mancilla

Versión	Emisión	Descripción
AA	15-06-2023	Ingeniería básica
AB	04-08-2023	Anteproyecto
AC	01-11-2023	Anteproyecto V2 50%
AD	15-12-2023	Anteproyecto V2 100%
DD	13-03-2024	Entrega curaduría
EE	10-05-2024	Proyecto Final 100%
EF	31-05-2024	Respuesta Obs 100%
FF	21-06-2024	Entrega Final
01	28-07-2024	ENTREGA FINAL

PROYECTO:

CAMPUS DE CIENCIA TECNOLOGÍA E INNOVACIÓN DE BOGOTÁ

FASE

ENTREGA FINAL

PROPÓSITO DE EMISIÓN

Curaduría

Revisión

Entrega Cliente

COORDINACIÓN

CONSTRUCCIÓN

CONSTRUCCIÓN DETALLADA

APTO PARA CONSTRUCCIÓN (APC)

KEY PLAN

1C

1B

1A

FECHA:

28-07-2024

ESCALA:

As Indicated

DETALLES DE CONEXIONES

CTIB_CNI_EST_513_DET_XXX_01