



Corte 1-1
escala 1:50

Nota: El refuerzo debe quedar intercalado con las barras de anclaje mostradas en el plano E512.

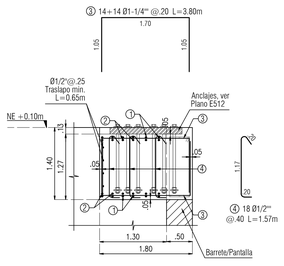


Corte 2-2
escala 1:50

Nota: El refuerzo debe quedar intercalado con las barras de anclaje mostradas en el plano E512.

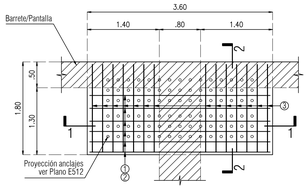

Refuerzo inferior
escala 1:50


Nota: El refuerzo debe quedar intercalado con las barras de anclaje mostradas en el plano E512.

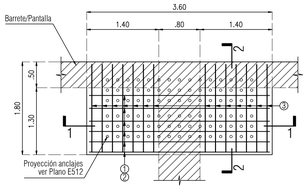


Refuerzo superior
escala 1:50

Nota: El refuerzo debe quedar intercalado con las barras de anclaje mostradas en el plano E512.

CAPITEL CA1

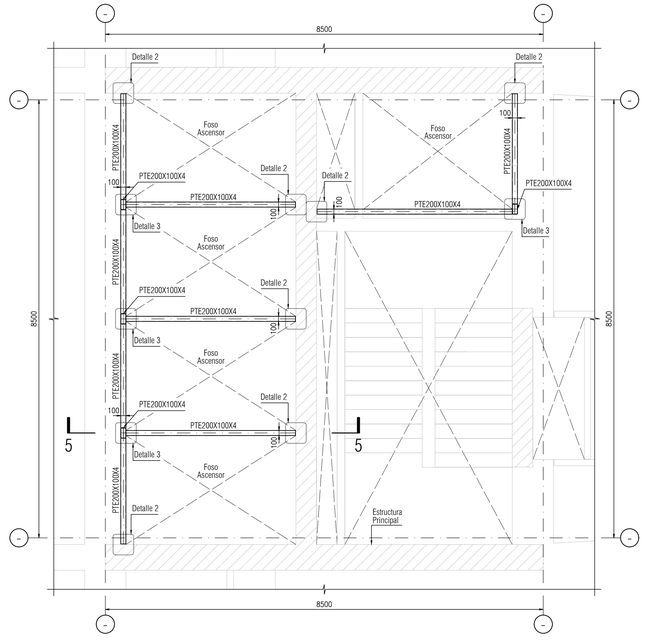


Planta Típica Subestructura de Ascensores
escala 1:50

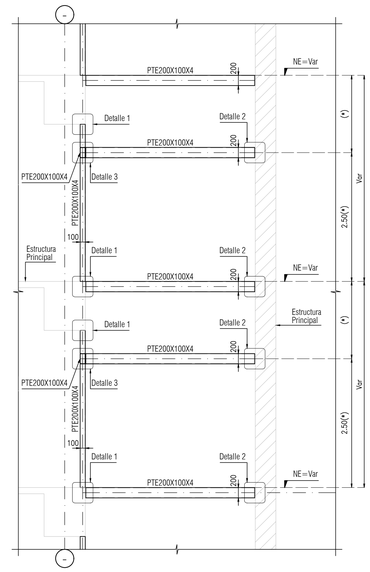

(*) Distancia entre vigas máxima recomendada por proveedor. Verificar dimensiones y niveles con planos de ascensores

Corte 5-5
escala 1:50

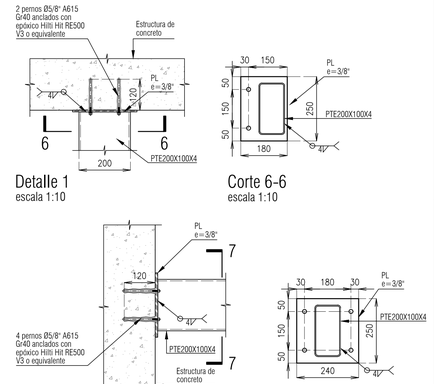


Detalle 1
escala 1:10


Corte 6-6
escala 1:10

Detalle 2
escala 1:10


Corte 7-7
escala 1:10

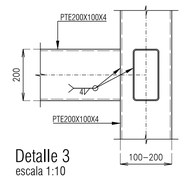


Detalle 3
escala 1:10

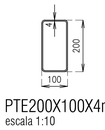


PTE200X100X4mm
escala 1:10

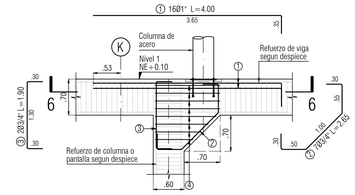

Detalle Mensulas Nivel 1 ejes 6 y 7
escala 1:50

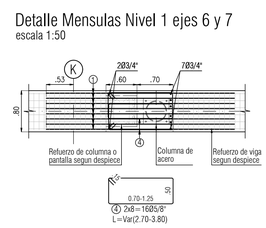


Corte 6-6
escala 1:50

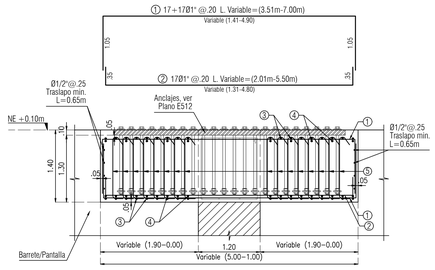


Corte 3-3
escala 1:50

Nota: El refuerzo debe quedar intercalado con las barras de anclaje mostradas en el plano E512.

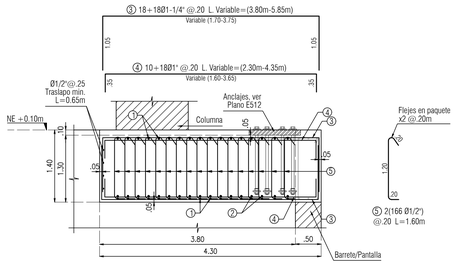


Corte 4-4
escala 1:50

Nota: El refuerzo debe quedar intercalado con las barras de anclaje mostradas en el plano E512.

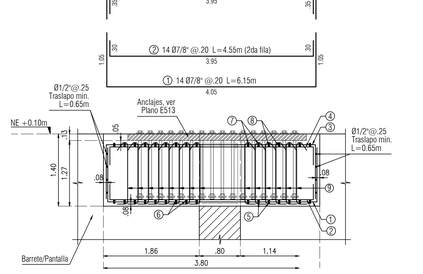


Corte 5-5
escala 1:50

Nota: El refuerzo debe quedar intercalado con las barras de anclaje mostradas en el plano E513.

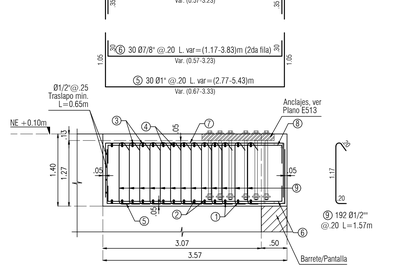


Corte 6-6
escala 1:50

Nota: El refuerzo debe quedar intercalado con las barras de anclaje mostradas en el plano E513.

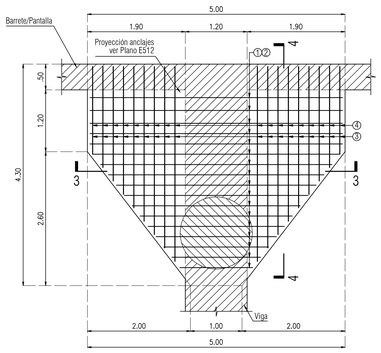

Refuerzo inferior
escala 1:50


Nota: El refuerzo debe quedar intercalado con las barras de anclaje mostradas en el plano E512.

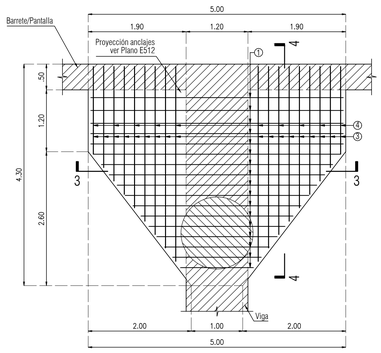

Refuerzo superior
escala 1:50


Nota: El refuerzo debe quedar intercalado con las barras de anclaje mostradas en el plano E512.

CAPITEL CA2

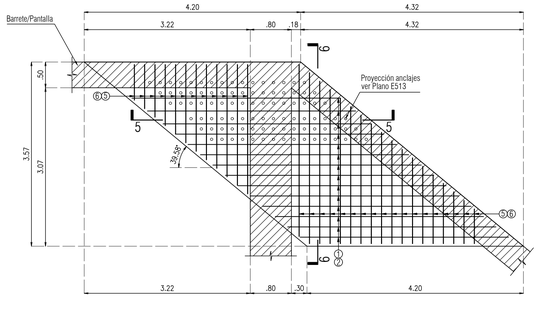

Refuerzo inferior
escala 1:50

Nota: El refuerzo debe quedar intercalado con las barras de anclaje mostradas en el plano E513.

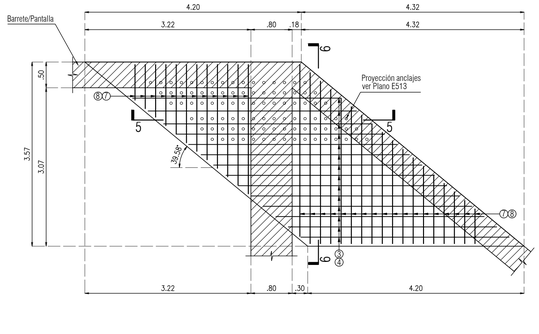

Refuerzo superior
escala 1:50

Nota: El refuerzo debe quedar intercalado con las barras de anclaje mostradas en el plano E513.

CAPITEL CA3

NOTAS GENERALES ASCENSORES:

1. Los presentes planos son de diseño. El fabricante de la estructura metálica debe elaborar los respectivos planos de taller, los cuales deben ser revisados y aprobados por la interventoría y la supervisión técnica de la obra.

2. Los elementos estructurales contenidos en este plano fueron diseñados para las reacciones estipuladas en los planos de diseño del proveedor de ascensores.

3. Todos los niveles y dimensiones deben ser verificados en obra por el constructor, de acuerdo con los requisitos del equipo de ascensores.

4. Los anclajes y apoyos de las guias y demás elementos mecánicos son responsabilidad del proveedor del equipo.

5. Procesos de soldadura calificada según AWS.

6. Limpieza de superficie SSPC 3.

7. Imprimante alquidico de fosfato de zinc, 3.0mils de espesor (película seca).

8. Las conexiones pernadas no requieren pretensionamiento. Son de apriete justo (snug tight).

9. La interventoria definirá la cantidad de ensayos de calidad de soldadura de acuerdo con los requisitos del titulo F de la NSR-10.

CTIB
Campus de Ciencia, Tecnología e Innovación de Bogotá - Región

corferias
Generadores de Oportunidades y Progreso

Cámara de Comercio de Bogotá

BOGOTÁ
Secretaría Distrital de Desarrollo Económico

ARQUITECTO COORDINADOR

EL EQUIPO MAZZANTI + Gensler

DISEÑO ESTRUCTURAL

CNI INGENIEROS

DISEÑADOR: ING. NICOLÁS PARRA GARCÍA
MAT. 25202 62063 CND

INTERVENTORÍA

GUTIÉRREZ DÍAZ S.A.S.
SUPERVISIÓN Y GESTIÓN DE PROYECTOS DE CONSTRUCCIÓN

Director de Interventoria: Ing. Jorge Iván Garcia Mancilla
Mat. 632021 148063 QND

Versión	Emisión	Descripción
AA	15-06-2023	Ingeniería básica
AB	04-08-2023	Anteproyecto
AC	01-11-2023	Anteproyecto V2 50%
AD	15-12-2023	Anteproyecto V2 100%
DD	13-03-2024	Entrega curaduría
EE	10-05-2024	Proyecto Final 100%
EF	31-05-2024	Respuesta Obs 100%
FF	21-06-2024	Entrega Final
01	26-07-2024	ENTREGA FINAL

PROYECTO:
CAMPUS DE CIENCIA TECNOLOGÍA E INNOVACIÓN DE BOGOTA
MAT.: No. 50C-00252470

FASE
ENTREGA FINAL

PROPÓSITO DE EMISIÓN


Curaduría	☐	Coordinación	☐
Revisión	☐	Construcción	☑
Entrega Cliente	☑		

ZONIFICACIÓN

Nivel 24
Nivel 23
Nivel 22
Nivel 21
Nivel 20
Nivel 19
Nivel 18
Nivel 17
Nivel 16
Nivel 15
Nivel 14
Nivel 13
Nivel 12
Nivel 11
Nivel 10
Nivel 9
Nivel 8
Nivel 7
Nivel 6
Nivel 5
Nivel 4
Nivel 3
Nivel 2
Nivel 1
Nivel S1
Nivel S2

PROYECTO DETALLADO
APTO PARA CONSTRUCCIÓN (APC)

KEY PLAN

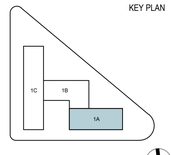

Fecha: 26-07-2024

Escala: As Indicated

DETALLES DE CAPITELES Y SUBESTRUCTURAS DE ASCENSORES

CTIB_CNI_EST_515_DET_XXX_01