
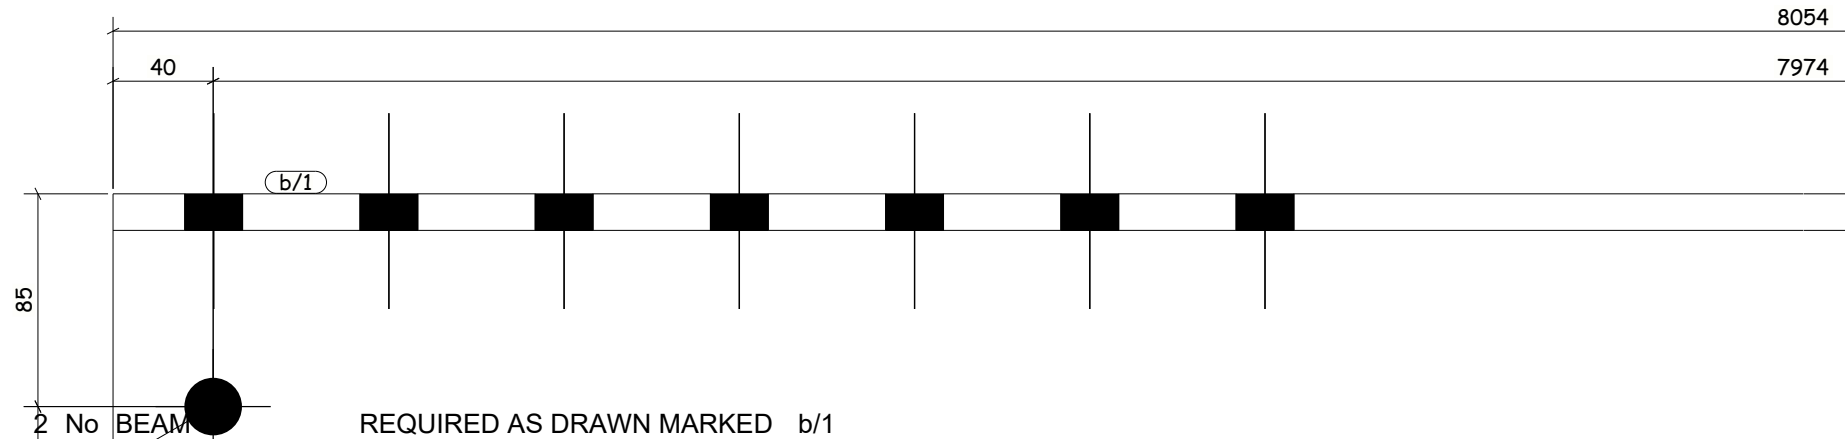


SHAFT DRAWING

ALLOCATION TO ASSEMBLIES	
Assembly Mark	TOTAL
B/1159	1
B/1170	1
Total	2

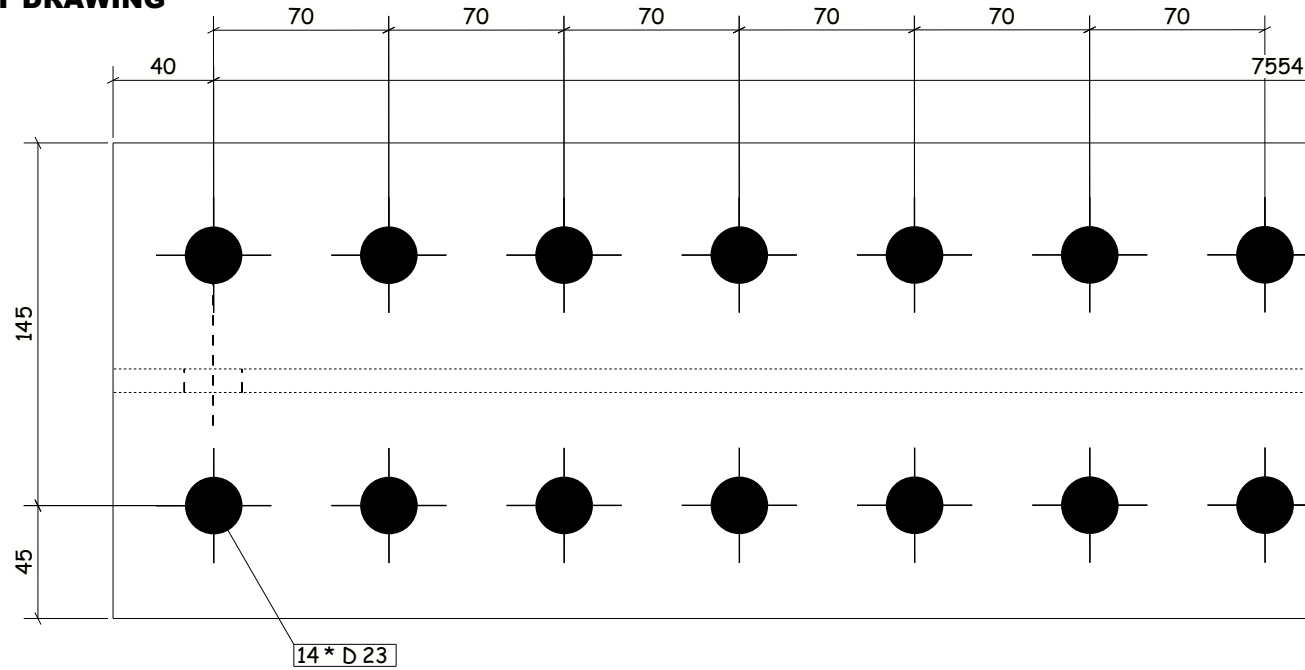

2 No BEAM REQUIRED AS DRAWN MARKED b/1

LOT	0	QTY	2
PHASE	1	QTY	2

Fabricación: HcB Ingeniería

Project: CTIB 2026

General Notes:
ALL HOLES 22 Dia UNO

FINISH: 0
Steel Grade: S235JR

Drawn:

Checked:

Scale: N.T.S.

HcB CTIB

Job No. / Dwg No. / Rev

1 / b/1 /

5 * D 23