
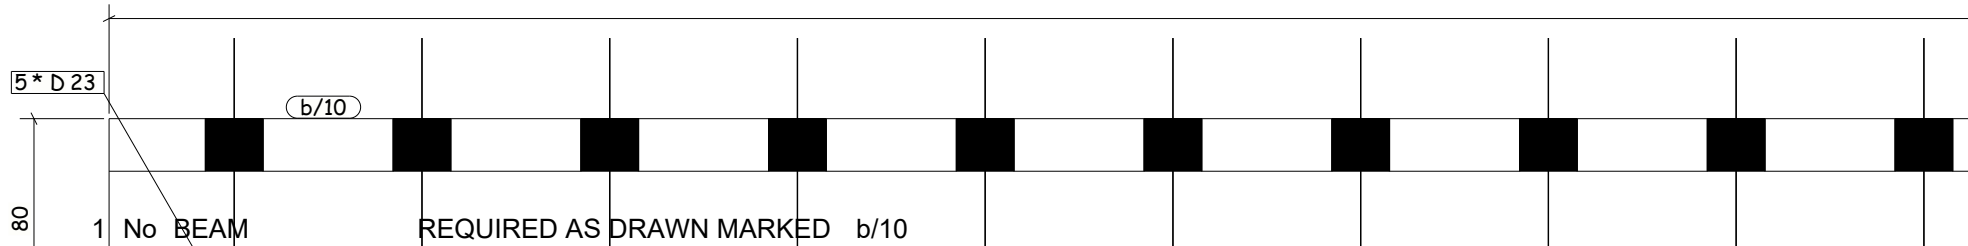


SHAFT DRAWING

ALLOCATION TO ASSEMBLIES	
Assy	75 y Mark
B/117	1
Total	1

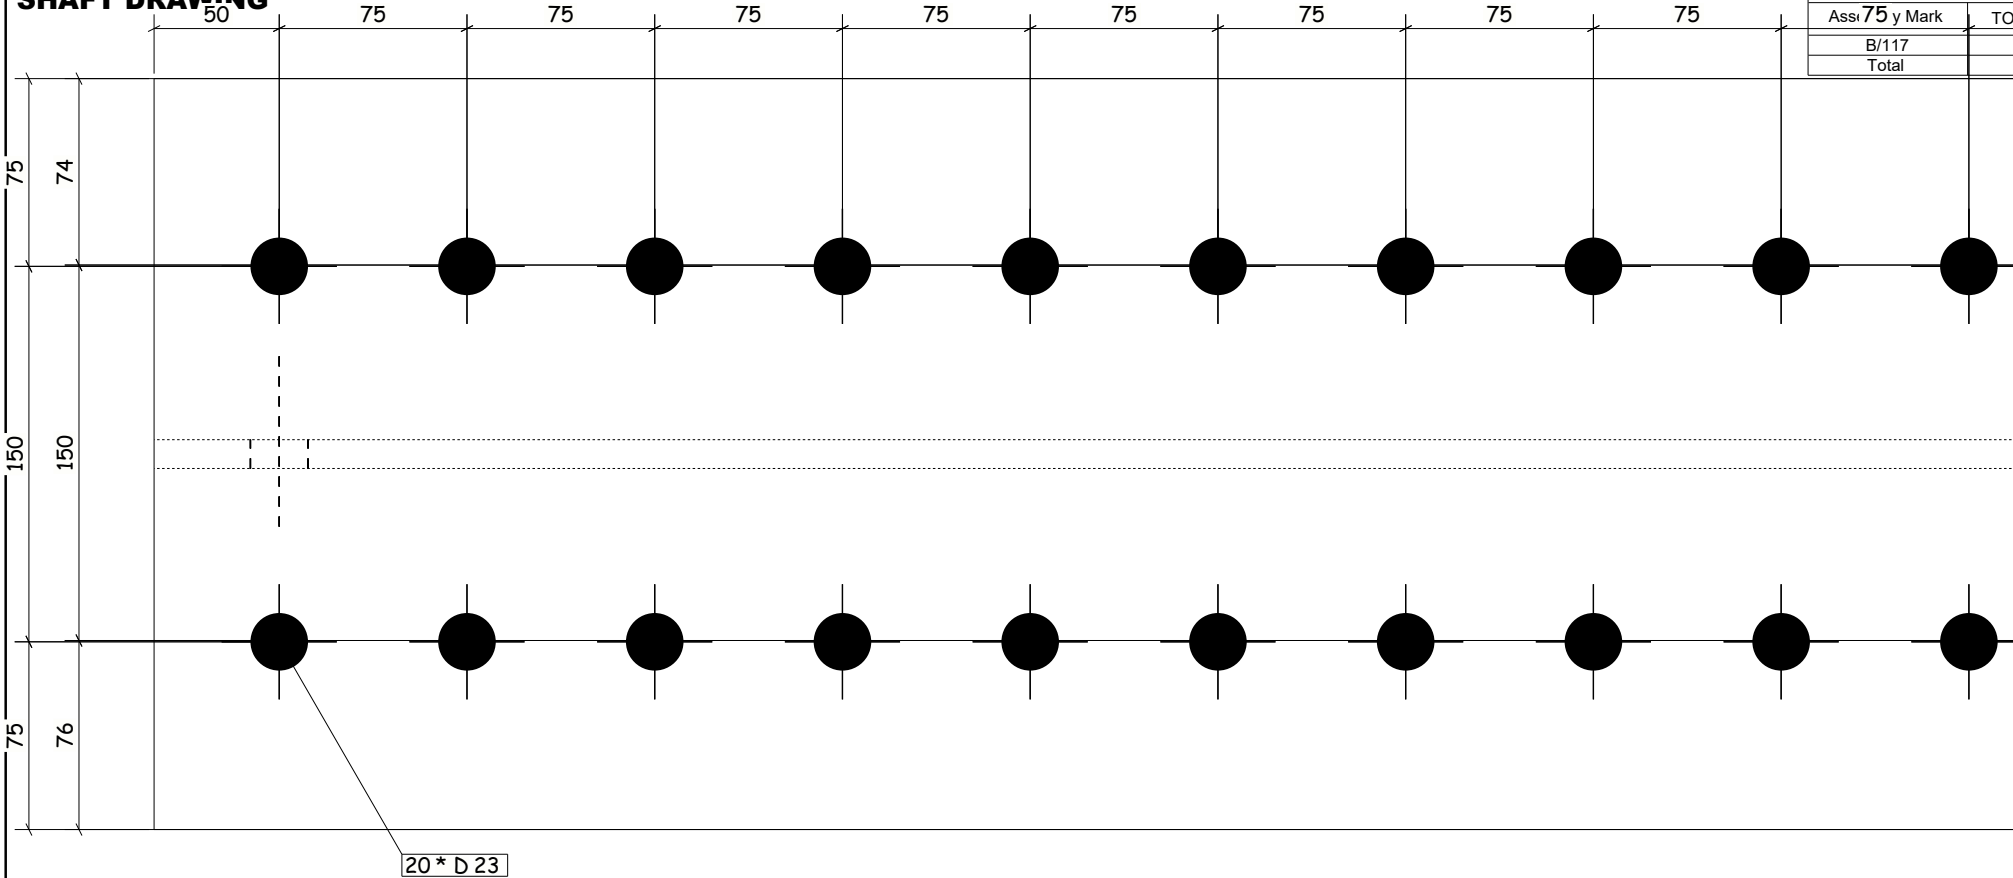

LOT	0	QTY	1
PHASE	1	QTY	1

Fabricación: HcB Ingeniería

Project: CTIB 2026

General Notes:

ALL HOLES 22 Dia UNO

FINISH: 0

Steel Grade: S235JR

Drawn:

Checked:

Scale: N.T.S.

HcB CTIB

Job No. / Dwg No. / Rev

1 / b/10 /

Rev	By	Date	Details				
b/10		HEA450	S235JR	1	9268.1	18.64	1249.7
Mark		Profile	Grade	QTY	Length	Area	Weight