


SHAFT DRAWING

ALLOCATION TO ASSEMBLIES	
Assembly Mark	TOTAL
B/226	8
Total	8

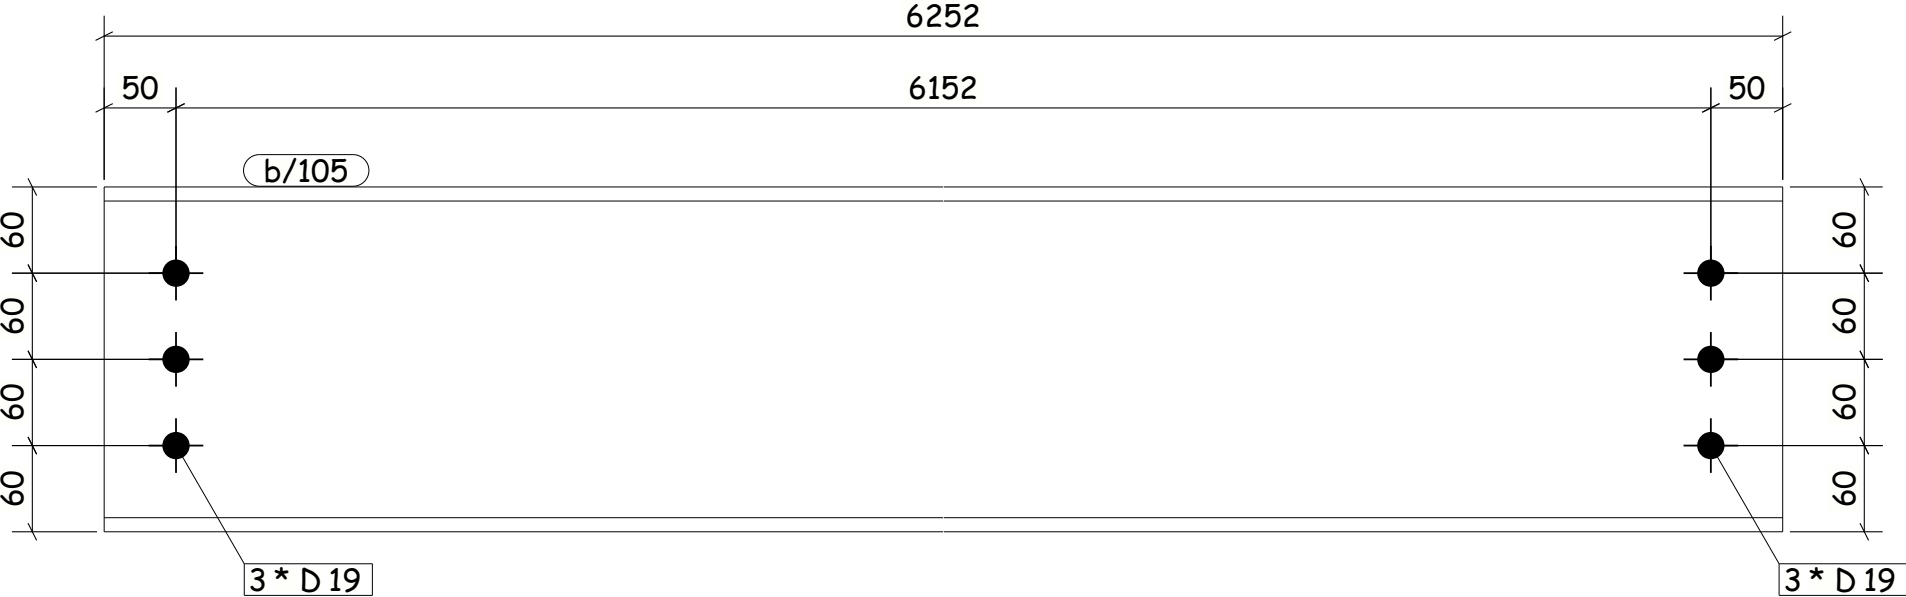

8 No BEAM

REQUIRED AS DRAWN MARKED b/105

LOT	0	QTY	8
PHASE	1	QTY	8

Rev	By	Date	Details				
b/105		IPE240	S235JR	8	6251.8	5.76	182.5
Mark		Profile	Grade	QTY	Length	Area	Weight

Fabricación: HcB Ingeniería

Project: CTIB 2026

General Notes:

ALL HOLES 22 Dia UNO

FINISH: 0

Steel Grade: S235JR

Drawn:

Checked:

Scale: N.T.S.



Job No. / Dwg No. / Rev

1 / b/105 /

A4