
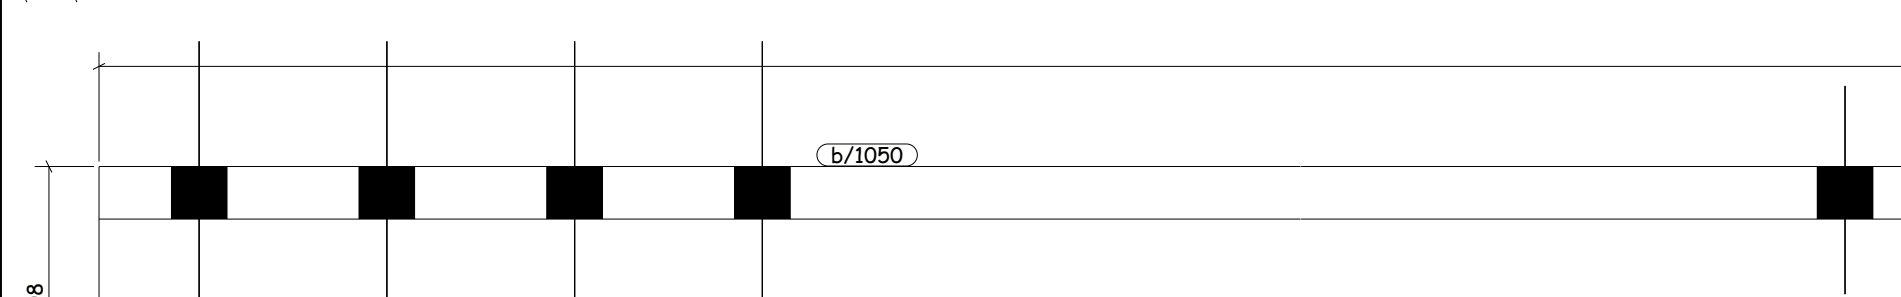


SHAFT DRAWING

ALLOCATION TO ASSEMBLIES

Assembly Mark	TOTAL
B/1151	1
Total	1

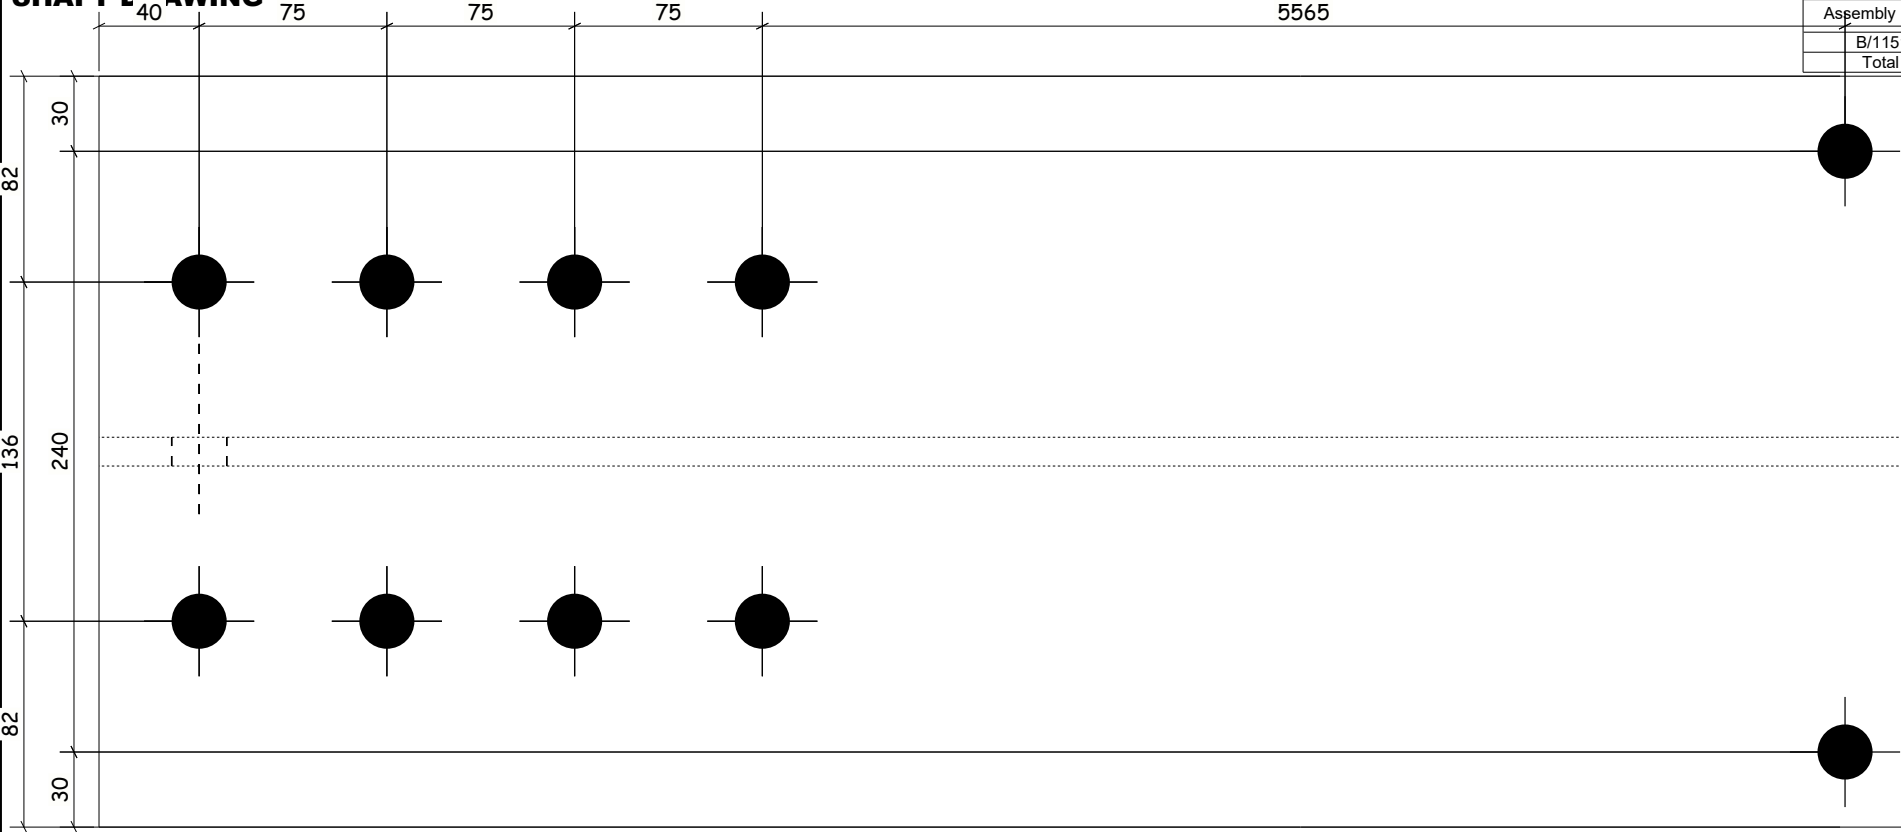

1 No BEAM

REQUIRED AS DRAWN MARKED b/***

LOT	0	QTY	1
PHASE	1	QTY	1

Rev	By	Date	Details				
b/1050		HEA450	S235JR	1	12000.0	24.13	1618.1
Mark		Profile	Grade	QTY	Length	Area	Weight

Fabricación: HcB Ingeniería

Project: CTIB 2026

General Notes:

ALL HOLES 22 Dia UNO

FINISH: 0

Steel Grade: S235JR

Drawn:

Checked:

Scale: N.T.S.

HcB CTIB

Job No. / Dwg No. / Rev

1 / b/*** /