
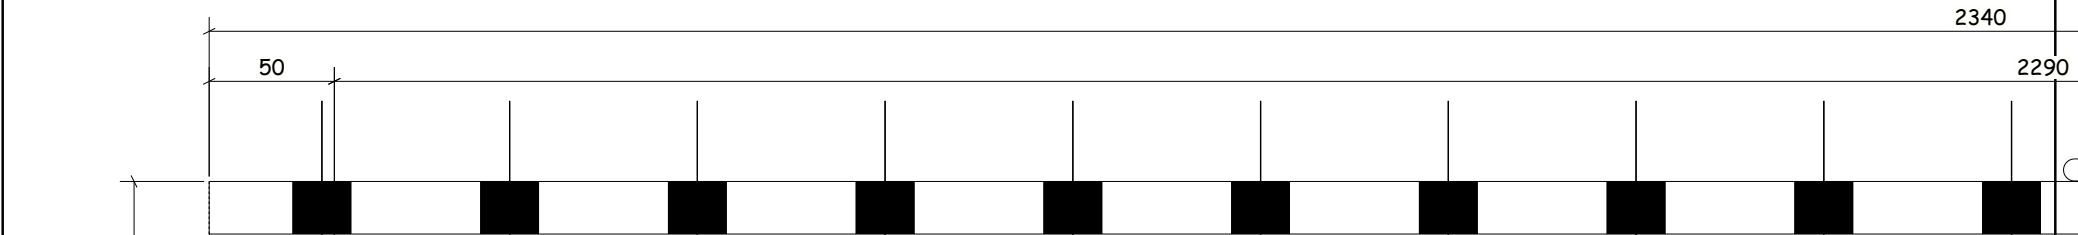


SHAFT DRAWING

ALLOCATION TO ASSEMBLIES	
Assembly 75 <	TOTAL
B/104	1
Total	1

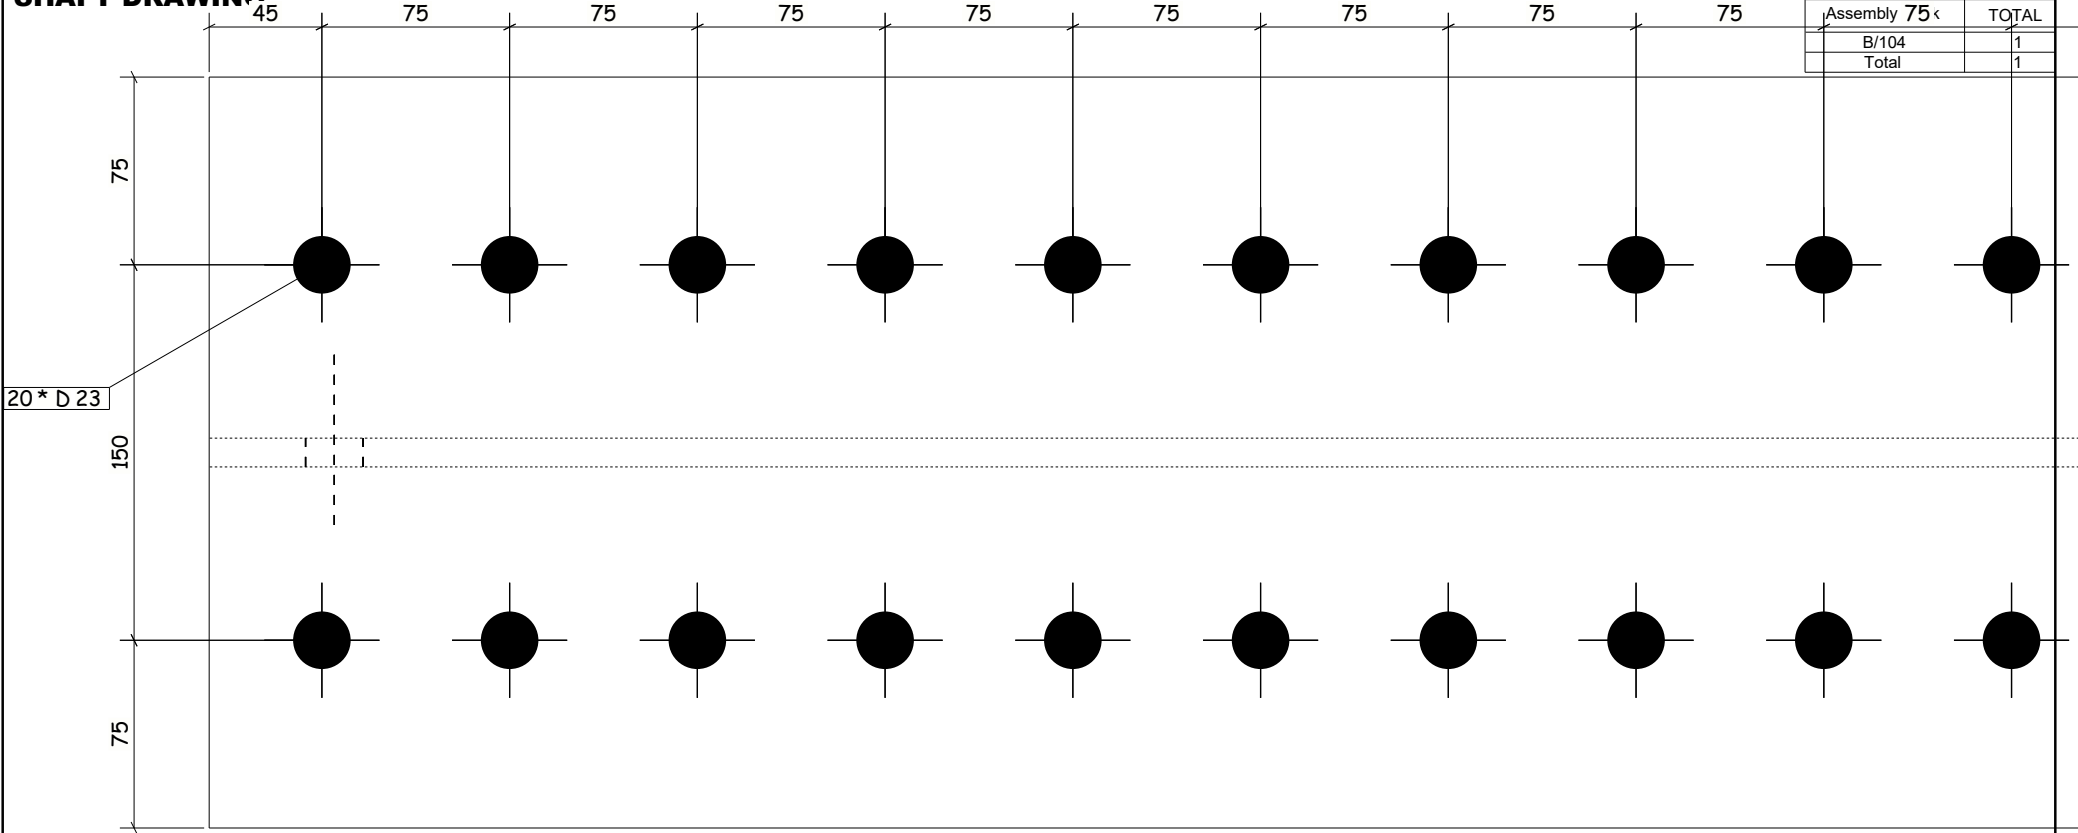

88		1 No BEAM		REQUIRED AS DRAWN MARKED				b/***	
----	--	-----------	--	--------------------------	--	--	--	-------	--	--	

Fabricación: HcB Ingeniería

Project: CTIB 2026

General Notes:

ALL HOLES 22 Dia UNO

FINISH: 0

Steel Grade: S235JR

Drawn:

Checked:

Scale: N.T.S.

HcB CTIB

Job No. / Dwg No. / Rev

1 / b/*** /