
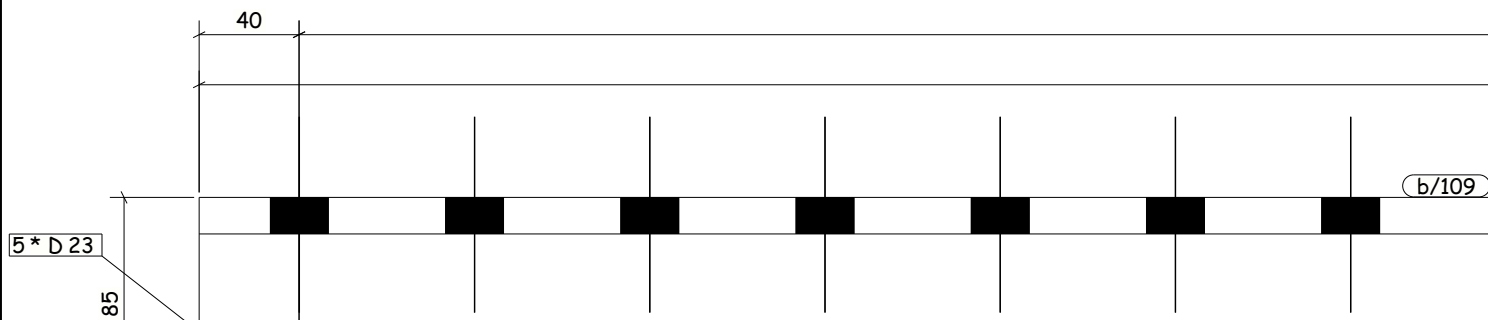


SHAFT DRAWING

ALLOCATION TO ASSEMBLIES	
Assembly Mark	TOTAL
B/6	1
B/42	1
B/84	1
Total	3

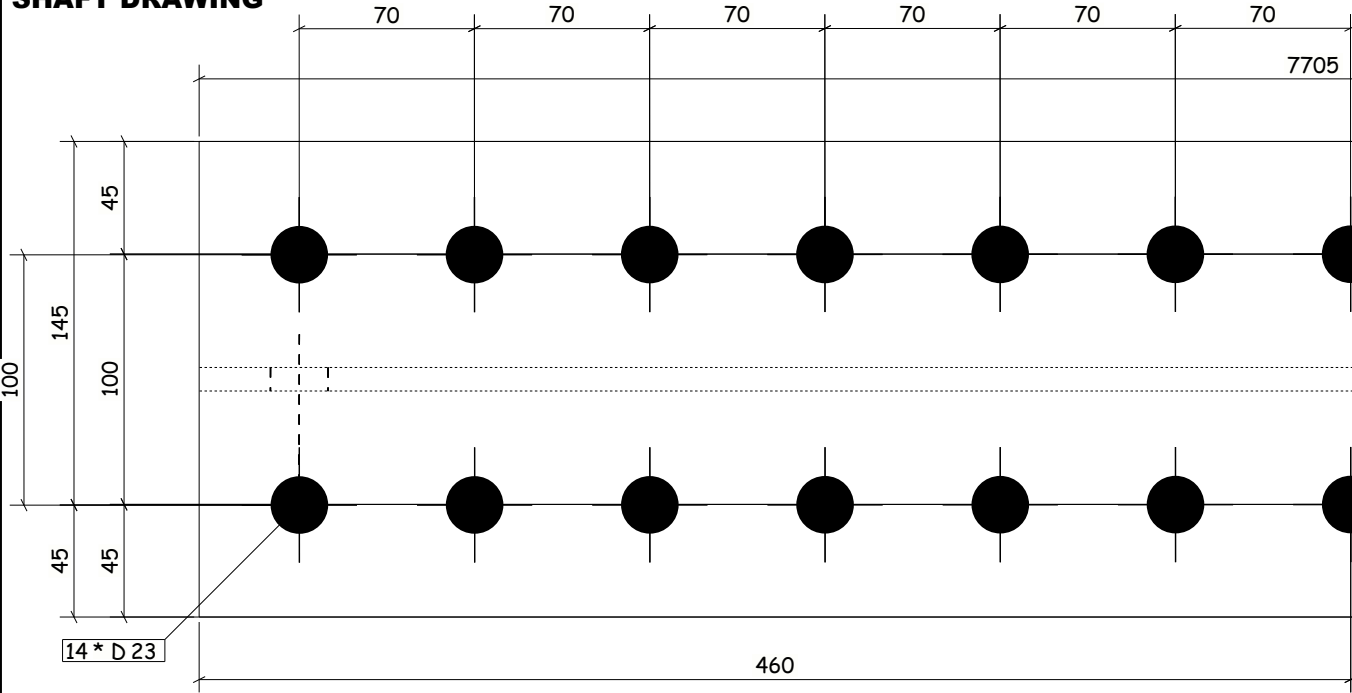

3 No BEAM REQUIRED AS DRAWN MARKED b/109

LOT	0	QTY	3
PHASE	1	QTY	3

Fabricación: HcB Ingeniería	
Project: CTIB 2026	
General Notes: ALL HOLES 22 Dia UNO FINISH: 0 Steel Grade: S235JR	Drawn:
	Checked:
	Scale: N.T.S.



Job No. /	Dwg No. /	Rev
1	/ b/109	/

Rev	By	Date	Details				
b/109		IPE450	S235JR	3	8165.0	13.10	609.1
Mark		Profile	Grade	QTY	Length	Area	Weight