
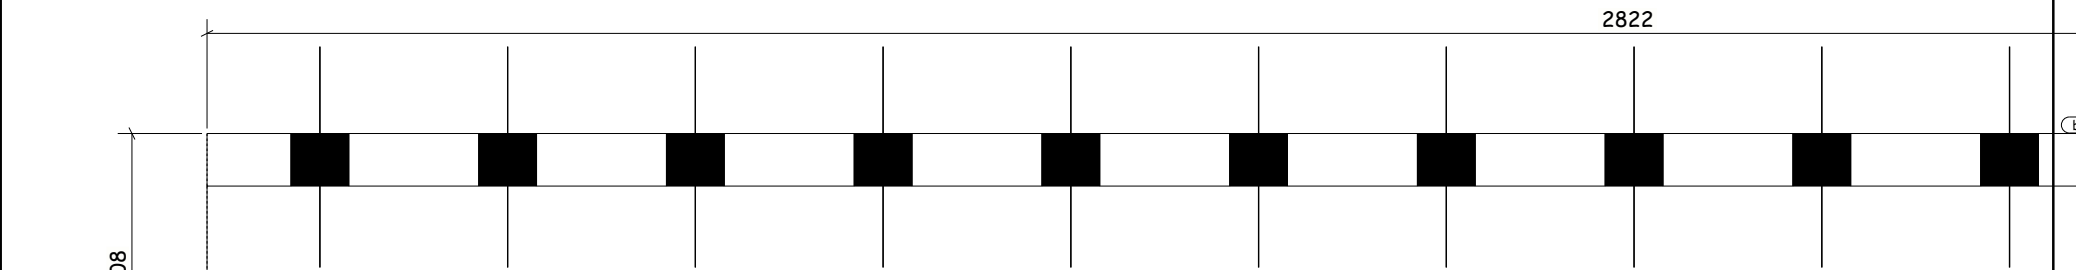


SHAFT DRAWING

ALLOCATION TO ASSEMBLIES	
Assembly 75 <	TOTAL
A/119	1
A/120	1
Total	2

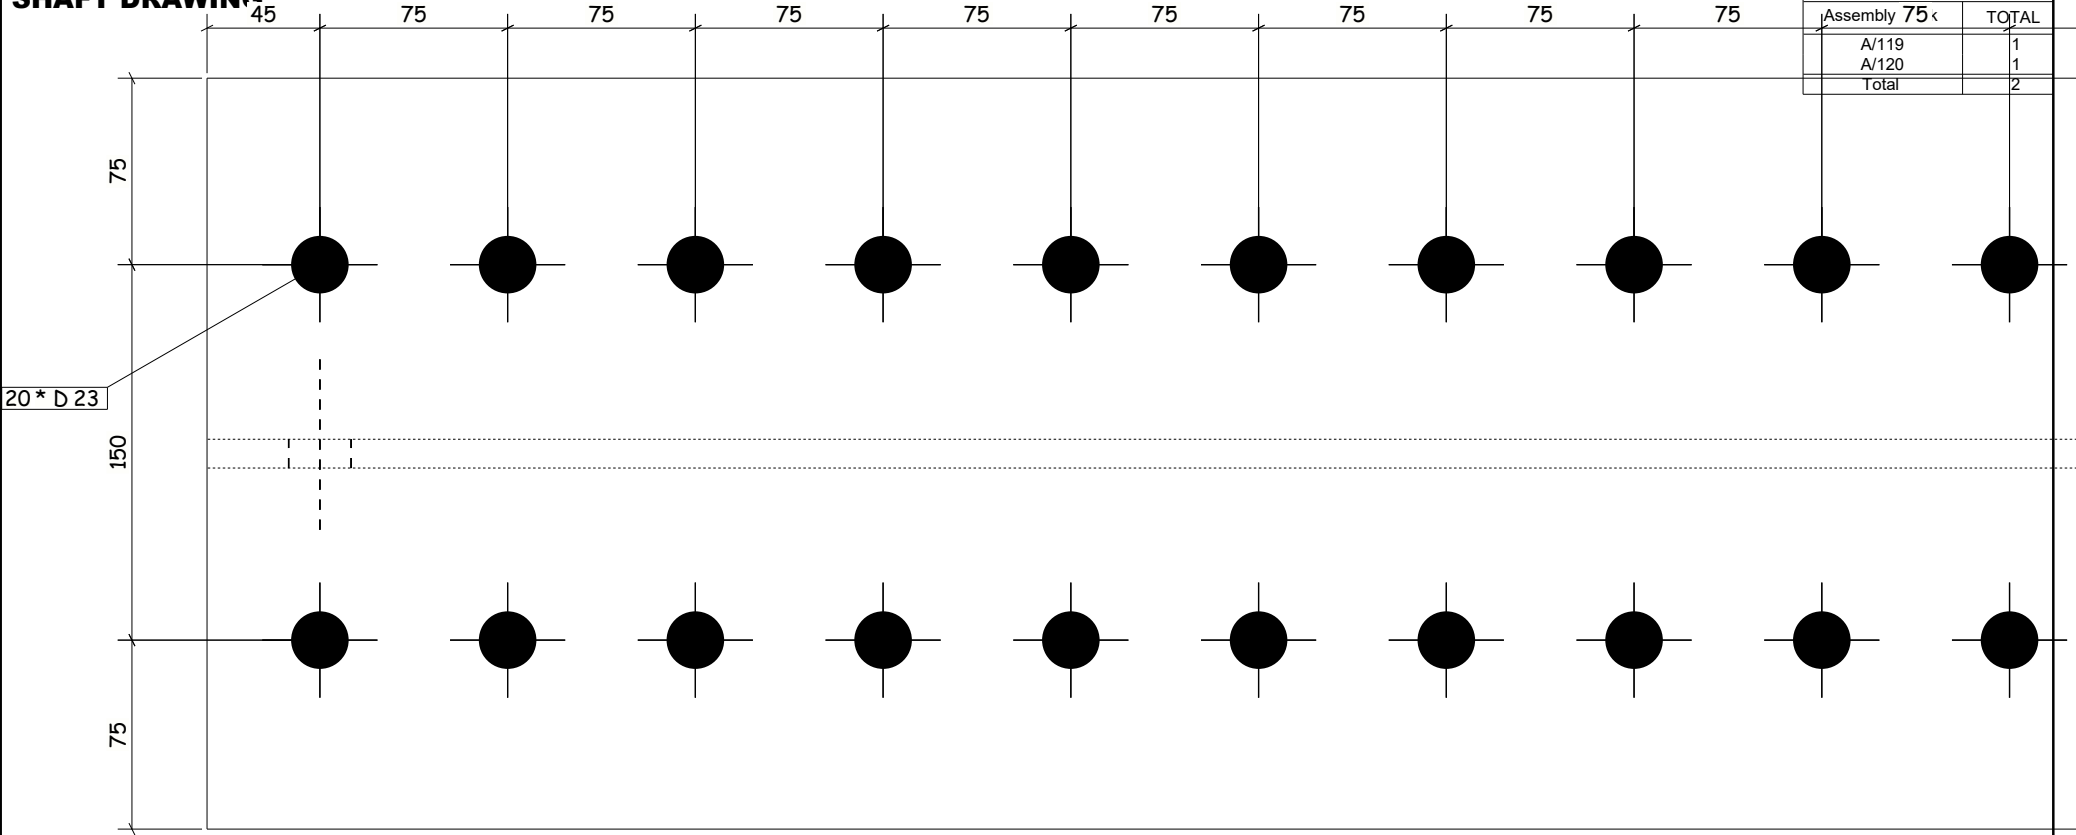

2 No BEAM REQUIRED AS DRAWN MARKED b/11

LOT	0	QTY	2
PHASE	1	QTY	2

Fabricación: HcB Ingeniería	
Project: CTIB 2026	
General Notes: ALL HOLES 22 Dia UNO FINISH: 0 Steel Grade: S235JR	Drawn:
	Checked:
	Scale: N.T.S.

HcB CTIB		
Job No. / Dwg No. / Rev		
1	/ b/11	/

75								
	Rev	By	Date	Details				
	b/11		HEA450	S235JR	2	2821.6	5.67	380.5
4 * D.25	Mark		Profile	Grade	QTY	Length	Area	Weight

Tekla structures