

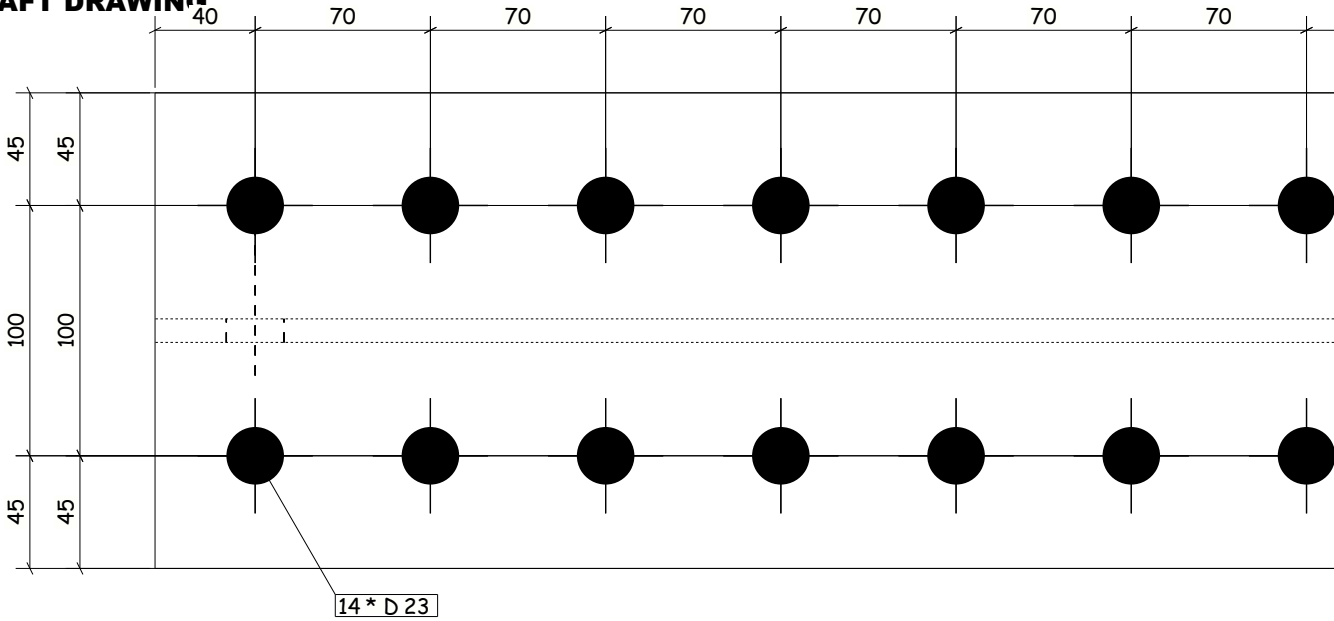


SHAFT DRAWING

ALLOCATION TO ASSEMBLIES	
Asserr 6327 k	TOTAL
B/5	1
Total	1

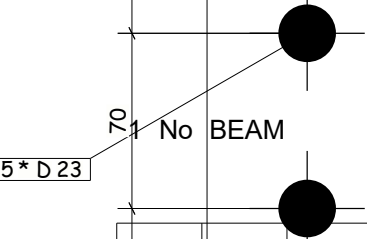

7391
7351

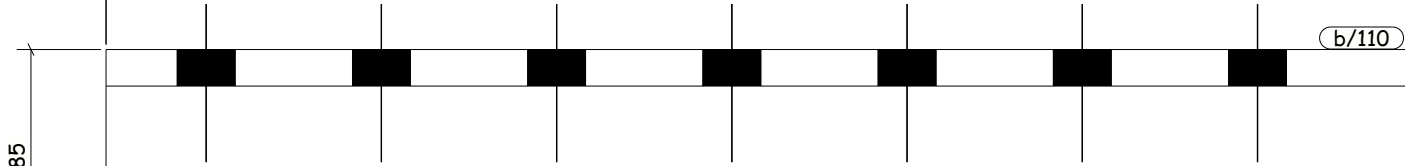

REQUIRED AS DRAWN MARKED b/110

LOT	0	QTY	1
PHASE	1	QTY	1

Fabricación: HcB Ingeniería	
Project: CTIB 2026	
General Notes: ALL HOLES 22 Dia UNO FINISH: 0 Steel Grade: S235JR	Drawn:
	Checked:
	Scale: N.T.S.

HcB CTIB		
Job No. /	Dwg No. /	Rev
1	/ b/110	/

Rev	By	Date	Details				
b/110		IPE450	S235JR	1	7390.8	11.86	544.7
Mark		Profile	Grade	QTY	Length	Area	Weight

Tekla structures