
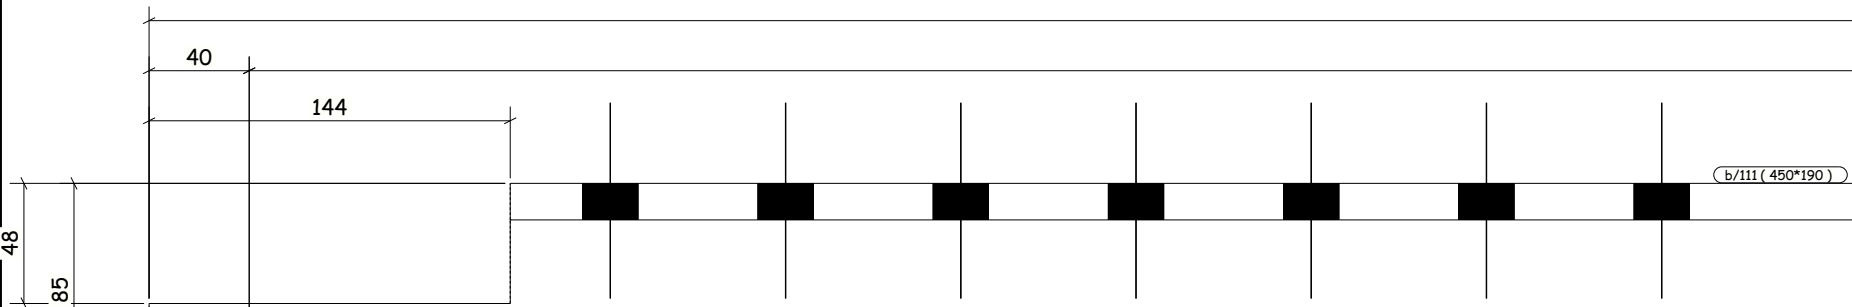


SHAFT DRAWING

8624

ALLOCATION TO ASSEMBLIES	
Assembly Mark	TOTAL
B/1287	1
Total	1

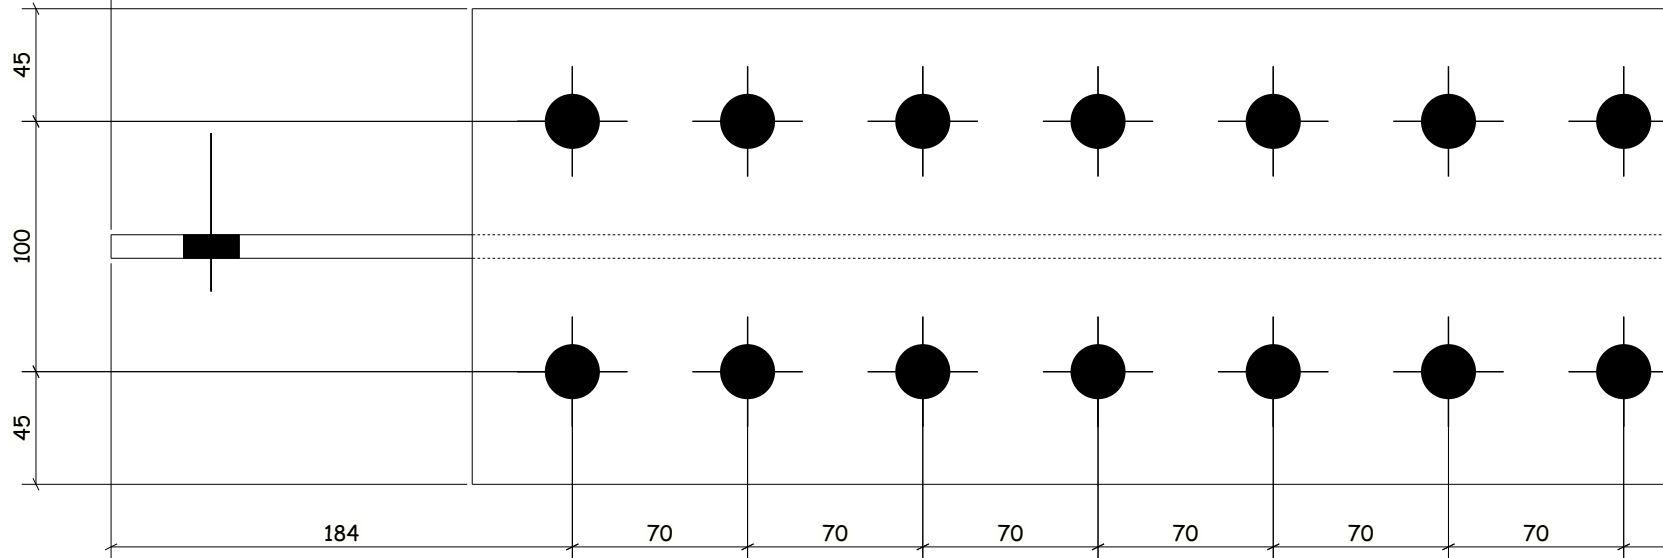

1 No BEAM

REQUIRED AS DRAWN MARKED b/111

LOT	0	QTY	1
PHASE	1	QTY	1

Rev	By	Date	Details					
	b/111	IPE450	S235JR	1	9228.5	14.81	674.3	
	Mark	Profile	Grade	QTY	Length	Area	Weight	

Fabricación: HcB Ingeniería		
Project: CTIB 2026		
General Notes: ALL HOLES 22 Dia UNO FINISH: 0 Steel Grade: S235JR	Drawn:	Job No. / Dwg No. / Rev 1 / b/111 /
	Checked:	
	Scale: N.T.S.	